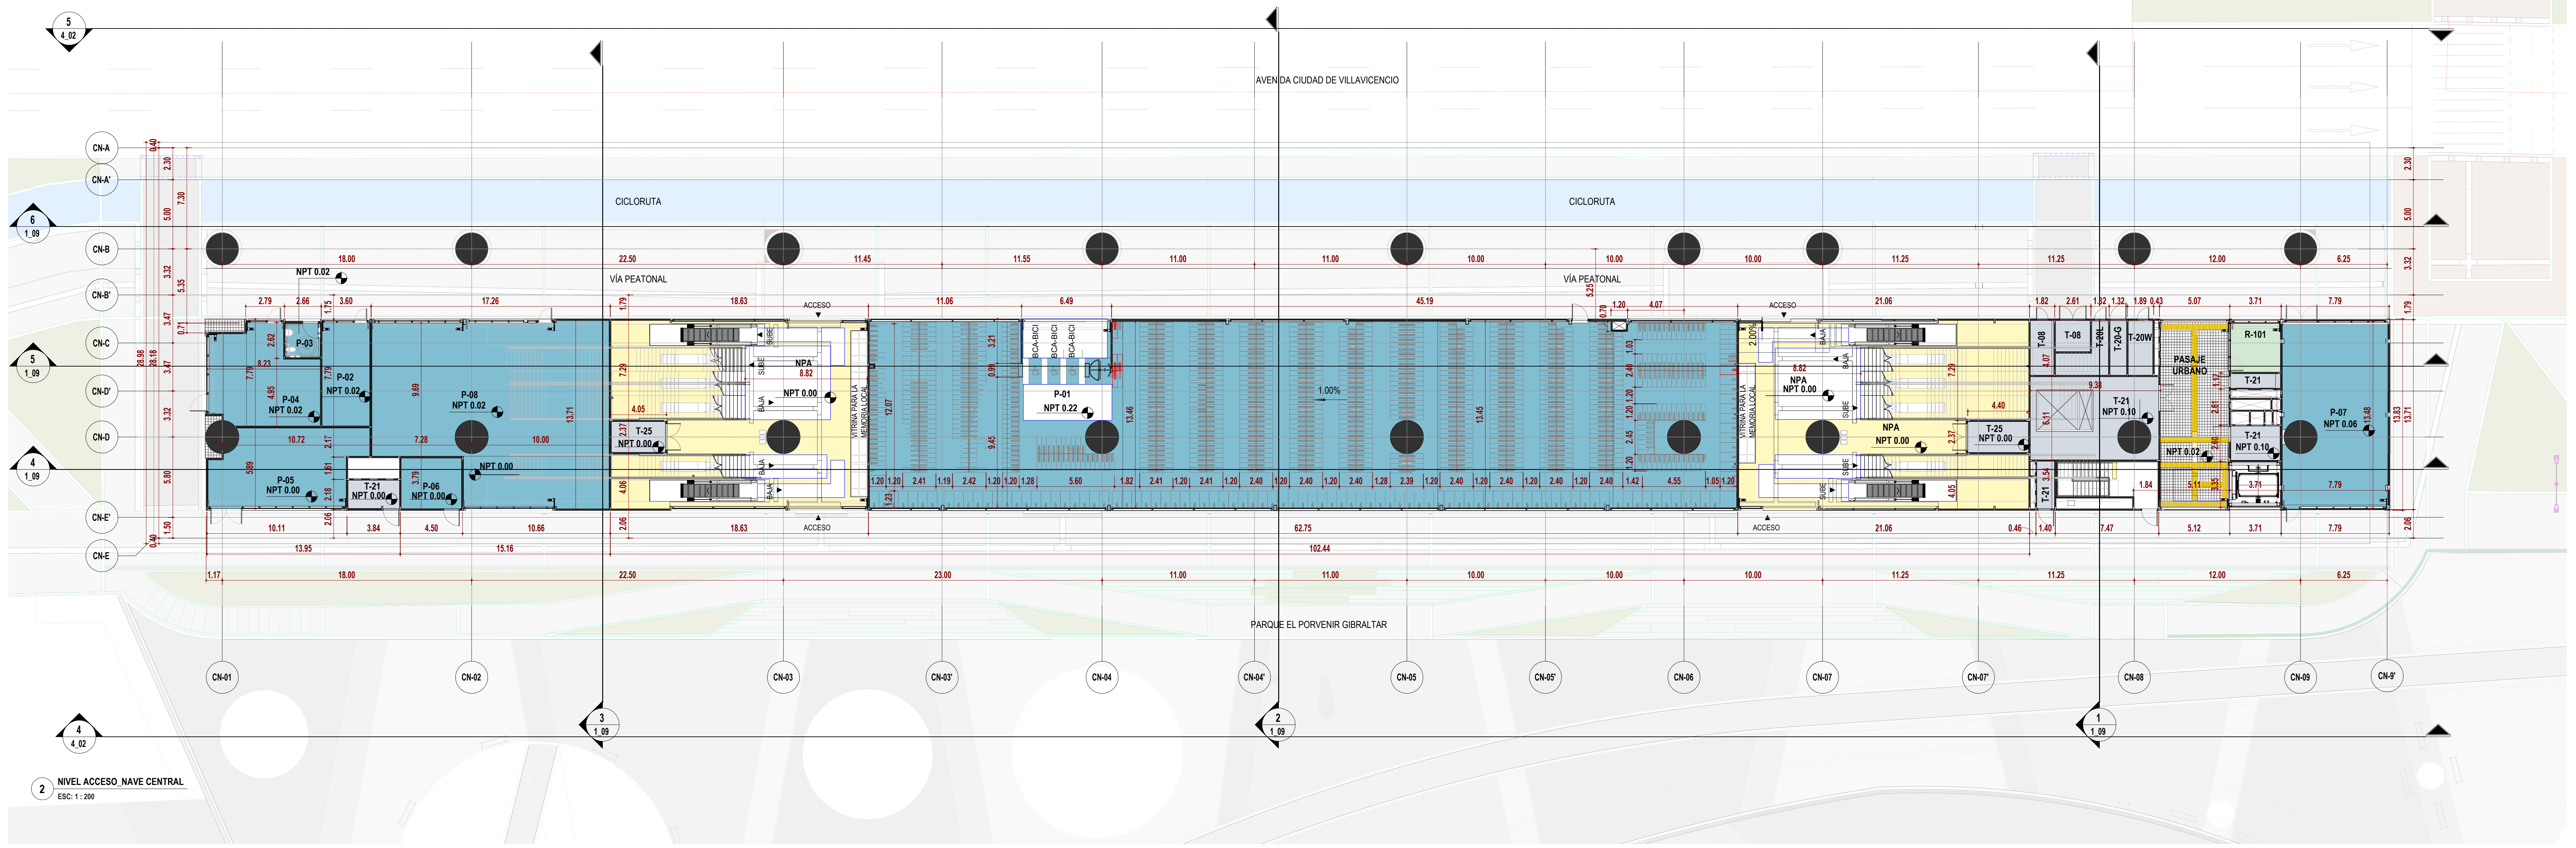

2 **NIVEL ACCESO_NAVE CENTRAL**
ESC: 1 : 200

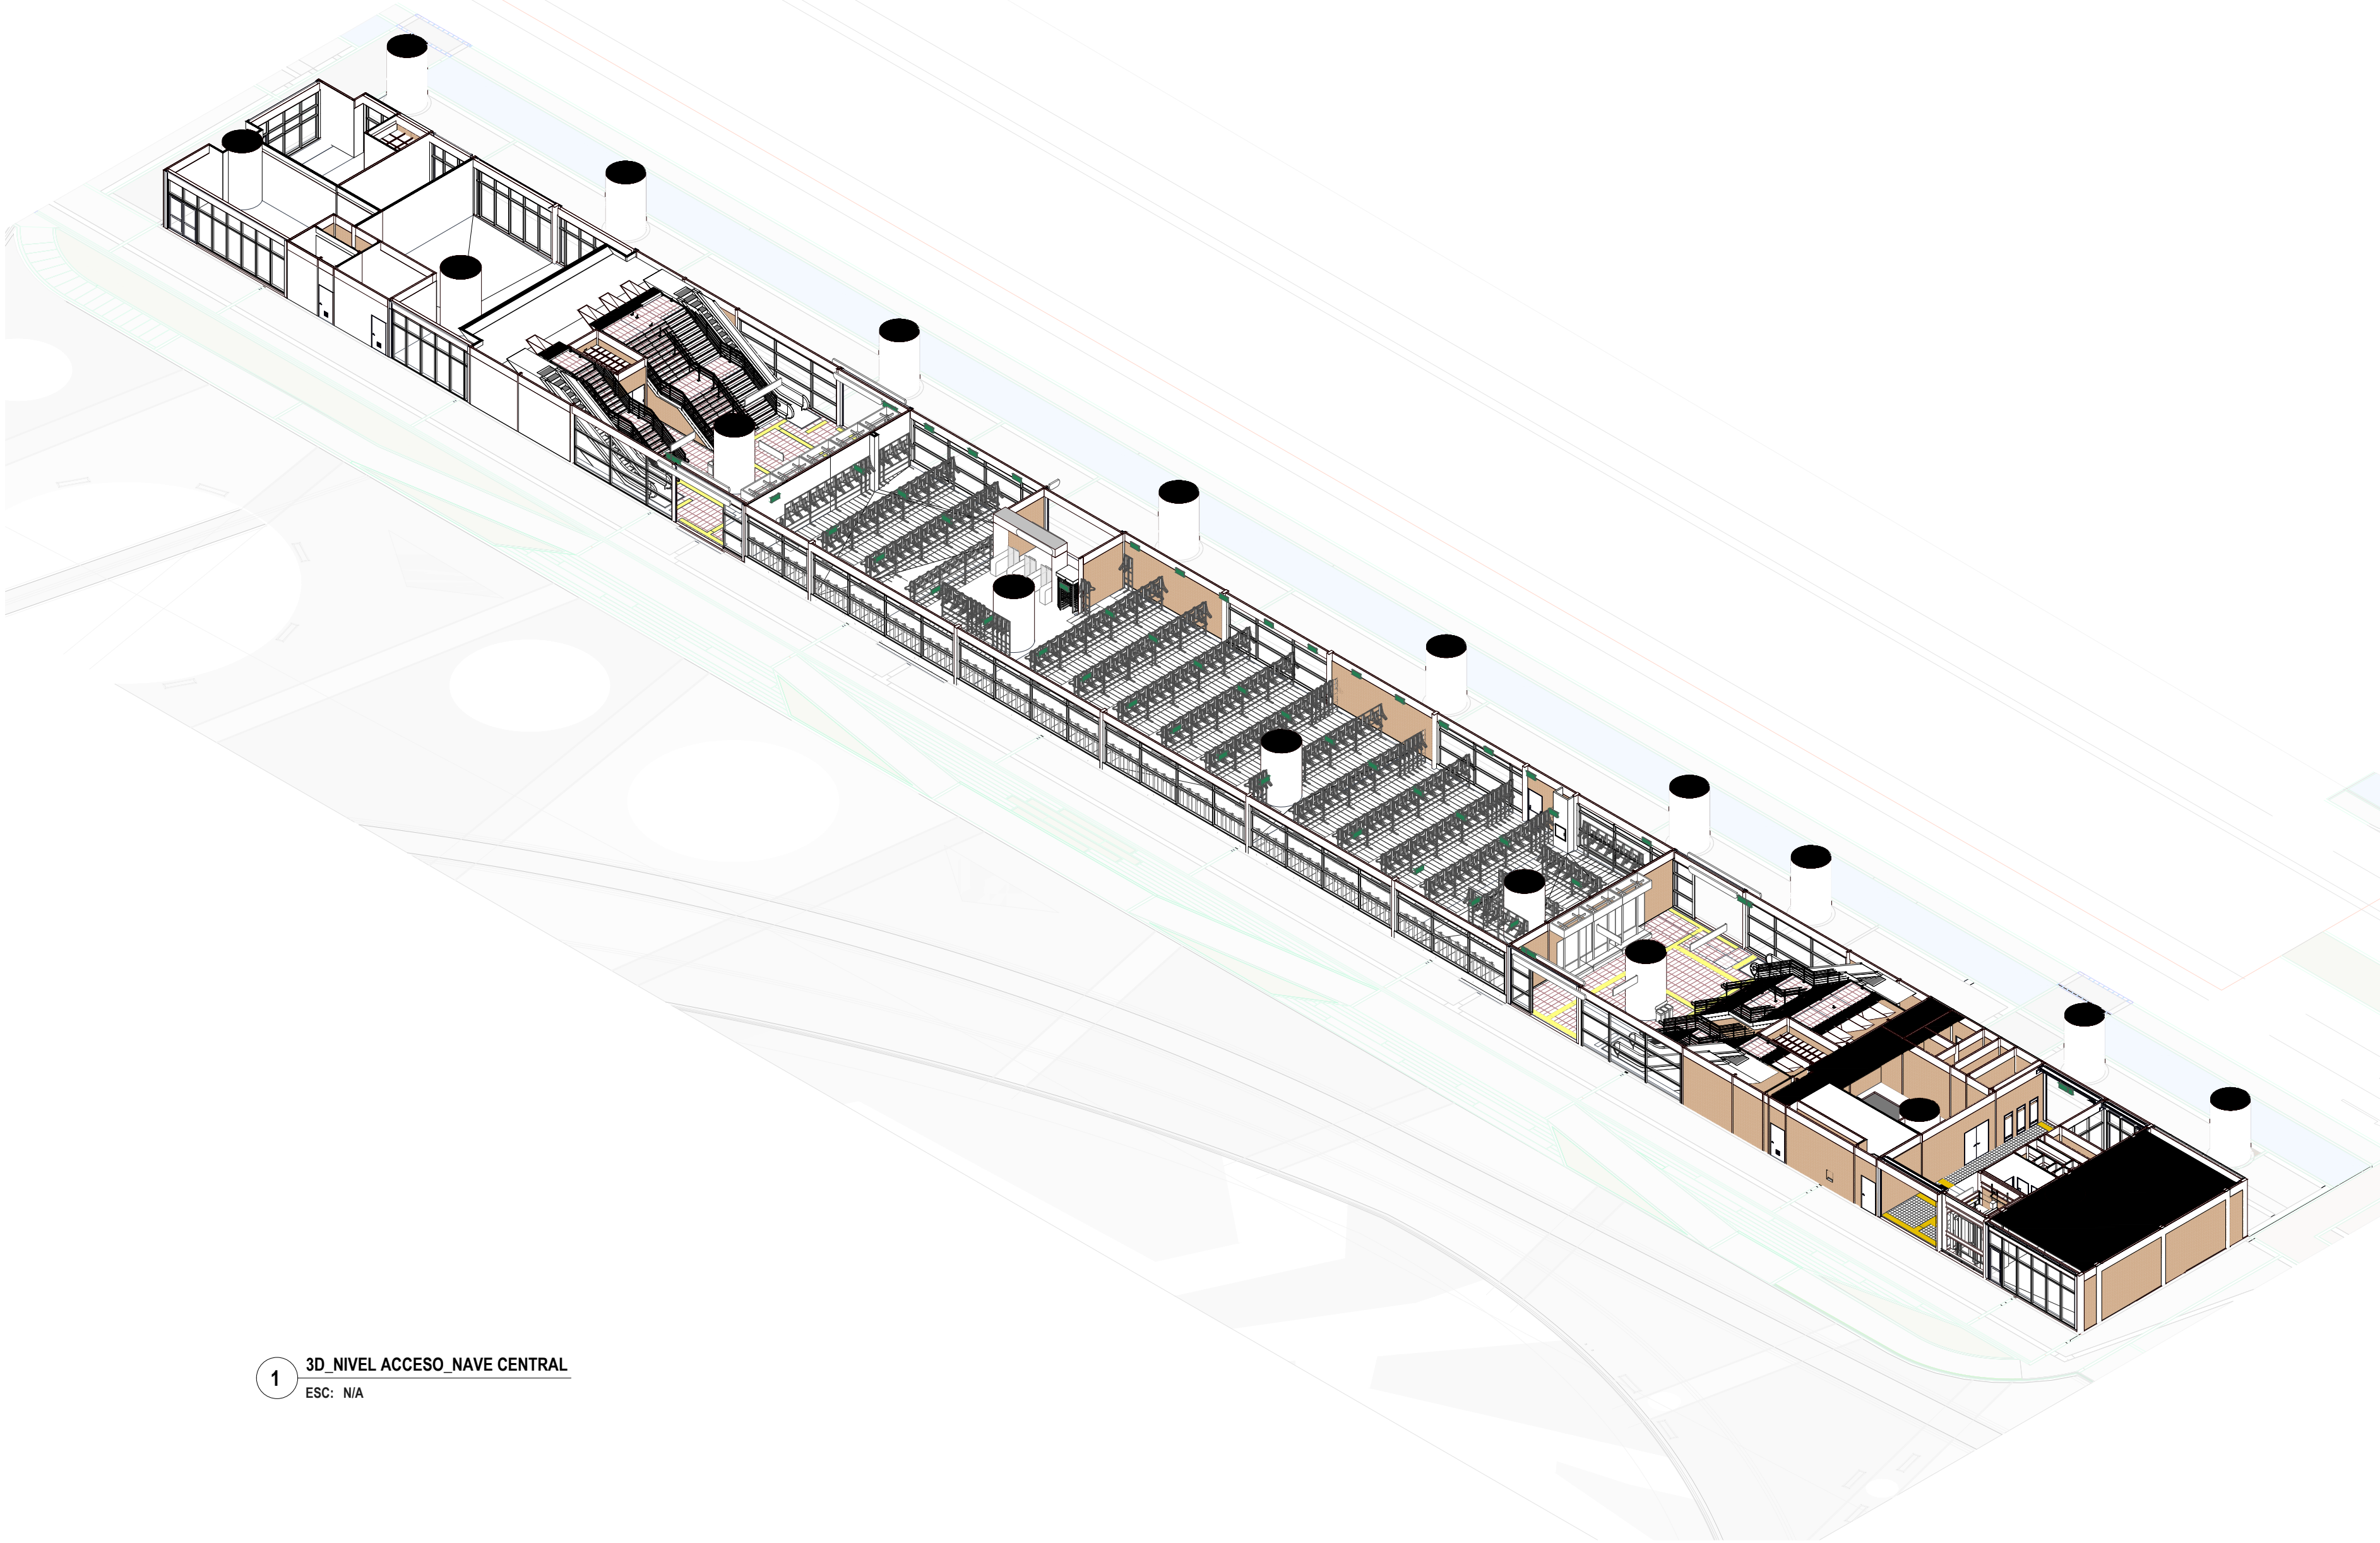

1 **3D_NIVEL ACCESO_NAVE CENTRAL**
ESC: N/A

09_TABLA DE ÁREAS ÚTILES (NIVEL ACCESO)			
CÓDIGO	**NOMBRE**	**ÁREA (m²)**	**DEPARTAMENTO**
ARC_PL_01.01			
C	ÁREAS DE USO CULTURAL	14.69	ÁREA CULTURAL
C	ÁREAS DE USO CULTURAL	8.80	ÁREA CULTURAL
NPA	ÁREA NO PAGA	219.96	ÁREA NO PAGA
NPA	ÁREA NO PAGA	256.88	ÁREA NO PAGA
P-01	ÁREA CICLO-PARQUEADEROS	831.18	ÁREA PÚBLICA
P-02	ÁREA OPERATIVA CICLO-PARQUEADEROS	26.27	ÁREA PÚBLICA
P-03	BAÑO OPERADOR CICLO-PARQUEADEROS	6.69	ÁREA PÚBLICA
P-04	TALLER DE BICICLETAS	51.05	ÁREA PÚBLICA
P-05	BIBLIOMETRO	58.27	ÁREA PÚBLICA
P-06	ESPACIO IPES (INSTITUTO PARA LA ECONOMÍA SOCIAL)	16.06	ÁREA PÚBLICA
P-07	SALÓN MULTIPLE EMB	98.77	ÁREA PÚBLICA
P-08	ESPACIO CARGA DE VEHICULOS ELECTRICOS	204.93	ÁREA PÚBLICA
PASAJE URBANO	ÁREA NO PAGA	68.73	ÁREA PÚBLICA
R-101	SERVICIOS ADICIONALES - ÁREA DE SERVICIOS	12.74	SERVICIOS ADICIONALES - ÁREA NO PAGA
T-08	CENTRO DE TRANSFORMACIÓN ENEL-CODENSA (CT)	5.62	ÁREA TÉCNICA
T-08	CENTRO DE TRANSFORMACIÓN (CT)	6.72	ÁREA TÉCNICA
T-20-G	MEDIDORES (GAS)	4.75	ÁREA TÉCNICA
T-20L	MEDIDORES (LUZ)	8.90	ÁREA TÉCNICA
T-20W	MEDIDORES (AGUA)	7.01	ÁREA TÉCNICA
T-21	ÁREA DE INSPECCIÓN	7.69	ÁREA TÉCNICA
T-21	ÁREA DE INSPECCIÓN	4.41	ÁREA TÉCNICA
T-21	ÁREA DE INSPECCIÓN	8.86	ÁREA TÉCNICA
T-21	ÁREA DE INSPECCIÓN	51.05	ÁREA TÉCNICA
T-21	ÁREA DE INSPECCIÓN	3.83	ÁREA TÉCNICA
T-25	NODO DE ACCESO DE TELECOMUNICACIONES	9.77	ÁREA TÉCNICA
T-25	NODO DE ACCESO DE TELECOMUNICACIONES	8.72	ÁREA TÉCNICA
TOTAL NIVEL ACCESO_NAVE CENTRAL		2002.35	

06_TABLA DE CICLO-PARQUEADEROS ESPECÍFICA		
TIPOLOGÍA	**CANTIDAD**	**USUARIO**
ARC_PRK_BIKE-PARKING-ASSISTED: ARC_PRK_BIKE-PARKING-ASSISTED_0.70x1.20x1.70m	1	EMPLEADOS
ARC_PRK_BIKE-PARKING-X1: ARC_PRK_BIKE-PARKING-X1_1.20x0.70x2.40m	5	EMPLEADOS
EMPLEADOS	6	
ARC_PRK_BIKE-PARKING-ASSISTED: ARC_PRK_BIKE-PARKING-ASSISTED_0.70x1.20x1.70m	99	VISITANTE
ARC_PRK_BIKE-PARKING-X1: ARC_PRK_BIKE-PARKING-X1_1.20x0.70x2.40m	80	VISITANTE
ARC_PRK_BIKE-PARKING-X6: ARC_PRK_BIKE-PARKING-X6_1.20x2.10x2.40m	816	VISITANTE
VISITANTE	995	
TOTAL CUPOS	1001	

08_TABLA DE ÁREAS POR DEPARTAMENTO (NIVEL ACCESO)	
DEPARTAMENTO	**ÁREA (m²)**
ÁREA PÚBLICA	68.73
SERVICIOS ADICIONALES - ÁREA NO PAGA	12.74
ÁREA CULTURAL	23.49
ÁREA NO PAGA	476.84
ÁREA PÚBLICA	1293.23
ÁREA TÉCNICA	127.32
TOTAL NIVEL	2002.35

LOCALIZACIÓN

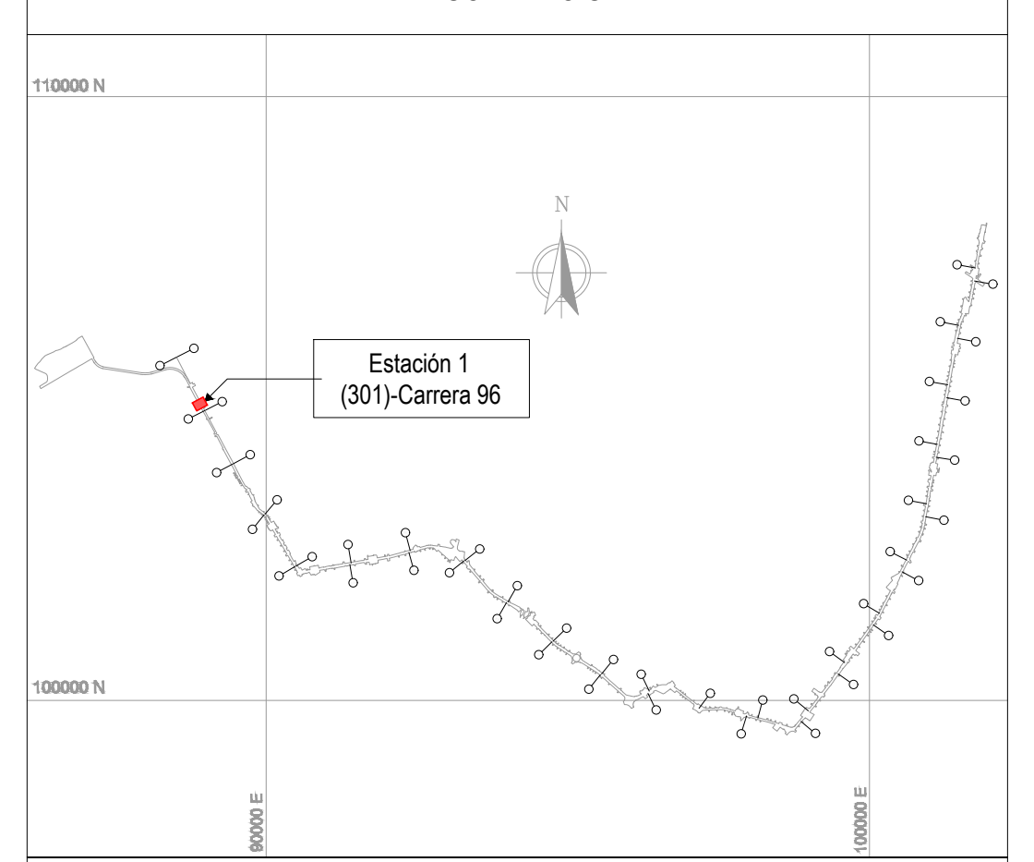

NOTAS

01 TODAS LAS DIMENSIONES ESTÁN CONFIGURADAS EN METROS A MENOS QUE SE INDIQUE UNA UNIDAD DE MEDIDA DIFERENTE.

02 TODAS LAS MEDIDAS, UBICACIÓN Y NIVELES DEBEN VERIFICARSE EN EL LUGAR DE CONSTRUCCIÓN.

03 EL NIVEL DE ACCESO AL EDIFICIO PL 01 CORRESPONDE AL +0,00 DE LA ESTACIÓN Y REFERENCIA AL NIVEL 2540.90 M.S.N.M

04 LOS NOMBRES ESPECIFICOS DE LAS ÁREAS PUEDEN SER CONSULTADAS EN EL PLANO NO. 3 O EN LAS VISTAS EN PLANTA.

05 LOS COLORES QUE SE MUESTRAN EN LOS PLANOS COMO PROYECCIÓN DE ELEMENTOS ARQUITECTÓNICOS COMO CUBIERTAS FACHADAS MUROS ETC. NO REPRESENTAN LA MATERIALIDAD Y REALIDAD DE ACABADOS DEL PROYECTO, SOLO SON INDICATIVOS PARA REALIZAR UNA CORRECTA LECTURA DE LA PLANIMETRÍA.

06 LAS ESCALERAS ELÉCTRICAS INDICAN SU SENTIDO CON LA SIGUIENTE NOMENCLATURA: "UP" SUBE Y "DW" BAJA.

07 EL NIVEL ESTRUCTURAL (NE) SE ENCUENTRA A (- 0.10m) POR DEBAJO DE LOS NIVELES DE PISO TERMINADO (NPT) MARCADOS EN LA PLANIMETRÍA.

08 PARA VER UBICACIÓN DE BAJANTES DE AGUAS LLUVIAS FAVOR REMITIRSE EL PLANO DE DISEÑO HIDROSANITARIO L1T1-1442-301-CON-ED-HID-PL-0014_VDD

- ARC_PL_00 = SÓTANO	/ NPT -5.80 m
- ARC_PL_01 = ACCESO	/ NPT -0.00 m
- ARC_PL_02 = INTERMEDIO	/ NPT -7.60 m
- ARC_PL_02.1 = PLACA INFERIOR VIGA CAJÓN	/ NPT -14.07 m
- ARC_PL_02.2 = TOPE DE RIEL (TOR)	/ NPT -16.20 m
- ARC_PL_03 = PLATAFORMA	/ NPT -17.34 m
- ARC_PL_05 = CUBIERTA NAVE CENTRAL	/ NPT -26.70 m

CONVENCIONES

🟥 - - -	LIMITE DE INTERVENCIÓN
🟦 - - -	AREAS DE ACUMULACIÓN
■	MURO DIVISORIO
— — —	PROYECCIÓN NIVEL SUPERIOR
🟩	SERVICIOS ADICIONALES - ÁREA NO PAGA
🟩	SERVICIOS ADICIONALES - ÁREA PAGA
🟩	SERVICIO PÚBLICO
🟦	ZONA DE REFUGIO
🟥	ÁREA CULTURAL
🟩	ÁREA JARDÍN
🟨	ÁREA NO PAGA
🟦	ÁREA OPERACIONAL
🟨	ÁREA PAGA
🟦	ÁREA PÚBLICA
⬜	ÁREA TÉCNICA

VB1
CAMBIOS REALIZADOS
1. SE ACTUALIZA AULA MÚLTIPLE, BICIPARQUEADEROS Y CUADRO DE ÁREAS

No.	PLANOS DE REFERENCIA	REV.

No.	MODELO BIM DE REFERENCIA	REV.
1	L1T1-1100-201-CON-ED-EST-MO-0001.rvt	V01
2	L1T1-1100-202-CON-ED-EST-MO-0001.rvt	V01
3	L1T1-1100-301-CON-ED-EST-MO-0001.rvt	V03
4	L1T1-1150-201-CON-ED-EST-MO-0001.rvt	V01
5	L1T1-1150-202-CON-ED-EST-MO-0001.rvt	V01
6	L1T1-1410-301-CON-ED-MEC-MO-0001.rvt	V00
7	L1T1-1420-301-CON-ED-MEC-MO-0001.rvt	V00
8	L1T1-1430-301-CON-ED-MEC-MO-0001.rvt	V00

No.	PAQUETE DE TRABAJO DE REFERENCIA	REV.
1	XREF-URBANISM_CONTEXT_ST01.rvt	

VB1

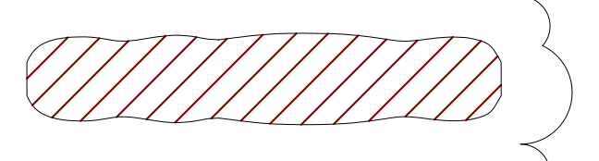

PLANO CLAVE ESTACIÓN 01

0 2 10m
1:200

METRO BOGOTÁ
GCS Consorcio Consultores PMO Bogotá
CONSORCIO SUPERVISOR PLMB
PEDELTA

DISEÑÓ:
OSCAR HIGUERA H.
Mat.:A20622022-1022410319

APROBÓ:
FELIPE SAAVEDRA
Mat:.25202-149684 CND

REVISÓ:
VERóNICA MIRANDA
Mat.:A25032002-52387701

DIBUJÓ:
EQUIPO PEDELTA

REVISIÓN No.	FECHA	DESCRIPCIÓN	REVISÓ	APROBÓ	APROBACIÓN CLIENTE
VB1	23/12/2025	EMITIDO PARA REVISIÓN Y COMENTARIOS DEL CLIENTE E INTERVENTORÍA	V.M.	F.S	
V00	23/08/2024	REVISIÓN NO OBJETADA - EMITIDO PARA CONSTRUCCIÓN	V.M.	F.S	
VDD	06/05/2024	EMITIDO PARA REVISIÓN Y COMENTARIOS DEL CLIENTE E INTERVENTORÍA	V.M.	F.S	
VCC	15/03/2024	EMITIDO PARA REVISIÓN Y COMENTARIOS DEL CLIENTE E INTERVENTORÍA	V.M.	F.S	
VBB	20/12/2023	EMITIDO PARA REVISIÓN Y COMENTARIOS DEL CLIENTE E INTERVENTORÍA	A.B.H	F.S	

METRO LÍNEA 1

METRO LÍNEA 1
CONTRATO DE CONCESIÓN No. 163 DE 2019

PROYECTO PRIMERA LÍNEA DEL METRO DE BOGOTÁ - TRAMO 1

DIRECTOR DE INTERVENTORÍA:
JAVIER DESCARGA N.
Mat.:2520268697 CND

ESPECIALISTA INTERVENTORÍA:
YOLANDA TARRIDA LÓPEZ
INT:

FECHA:
DICIEMBRE 2025

INFRAESTRUCTURA VIAL
ARQUITECTURA
ESTACIÓN METRO 1 (CARRERA 96)
NAVE CENTRAL
VISTA EN PLANTA - NIVEL ACCESO 01

PLANCHA No: L1T1-0000-301-CON-ED-ARQ-PL-0096_05_VB1
ARCHIVO: L1T1-0000-301-CON-ED-ARQ-MO-0001_V00.rvt
ESCALA: 1:200
FECHA: DICIEMBRE 2023
REVISIÓN No. VB1
PLANO No. 05 DE 45