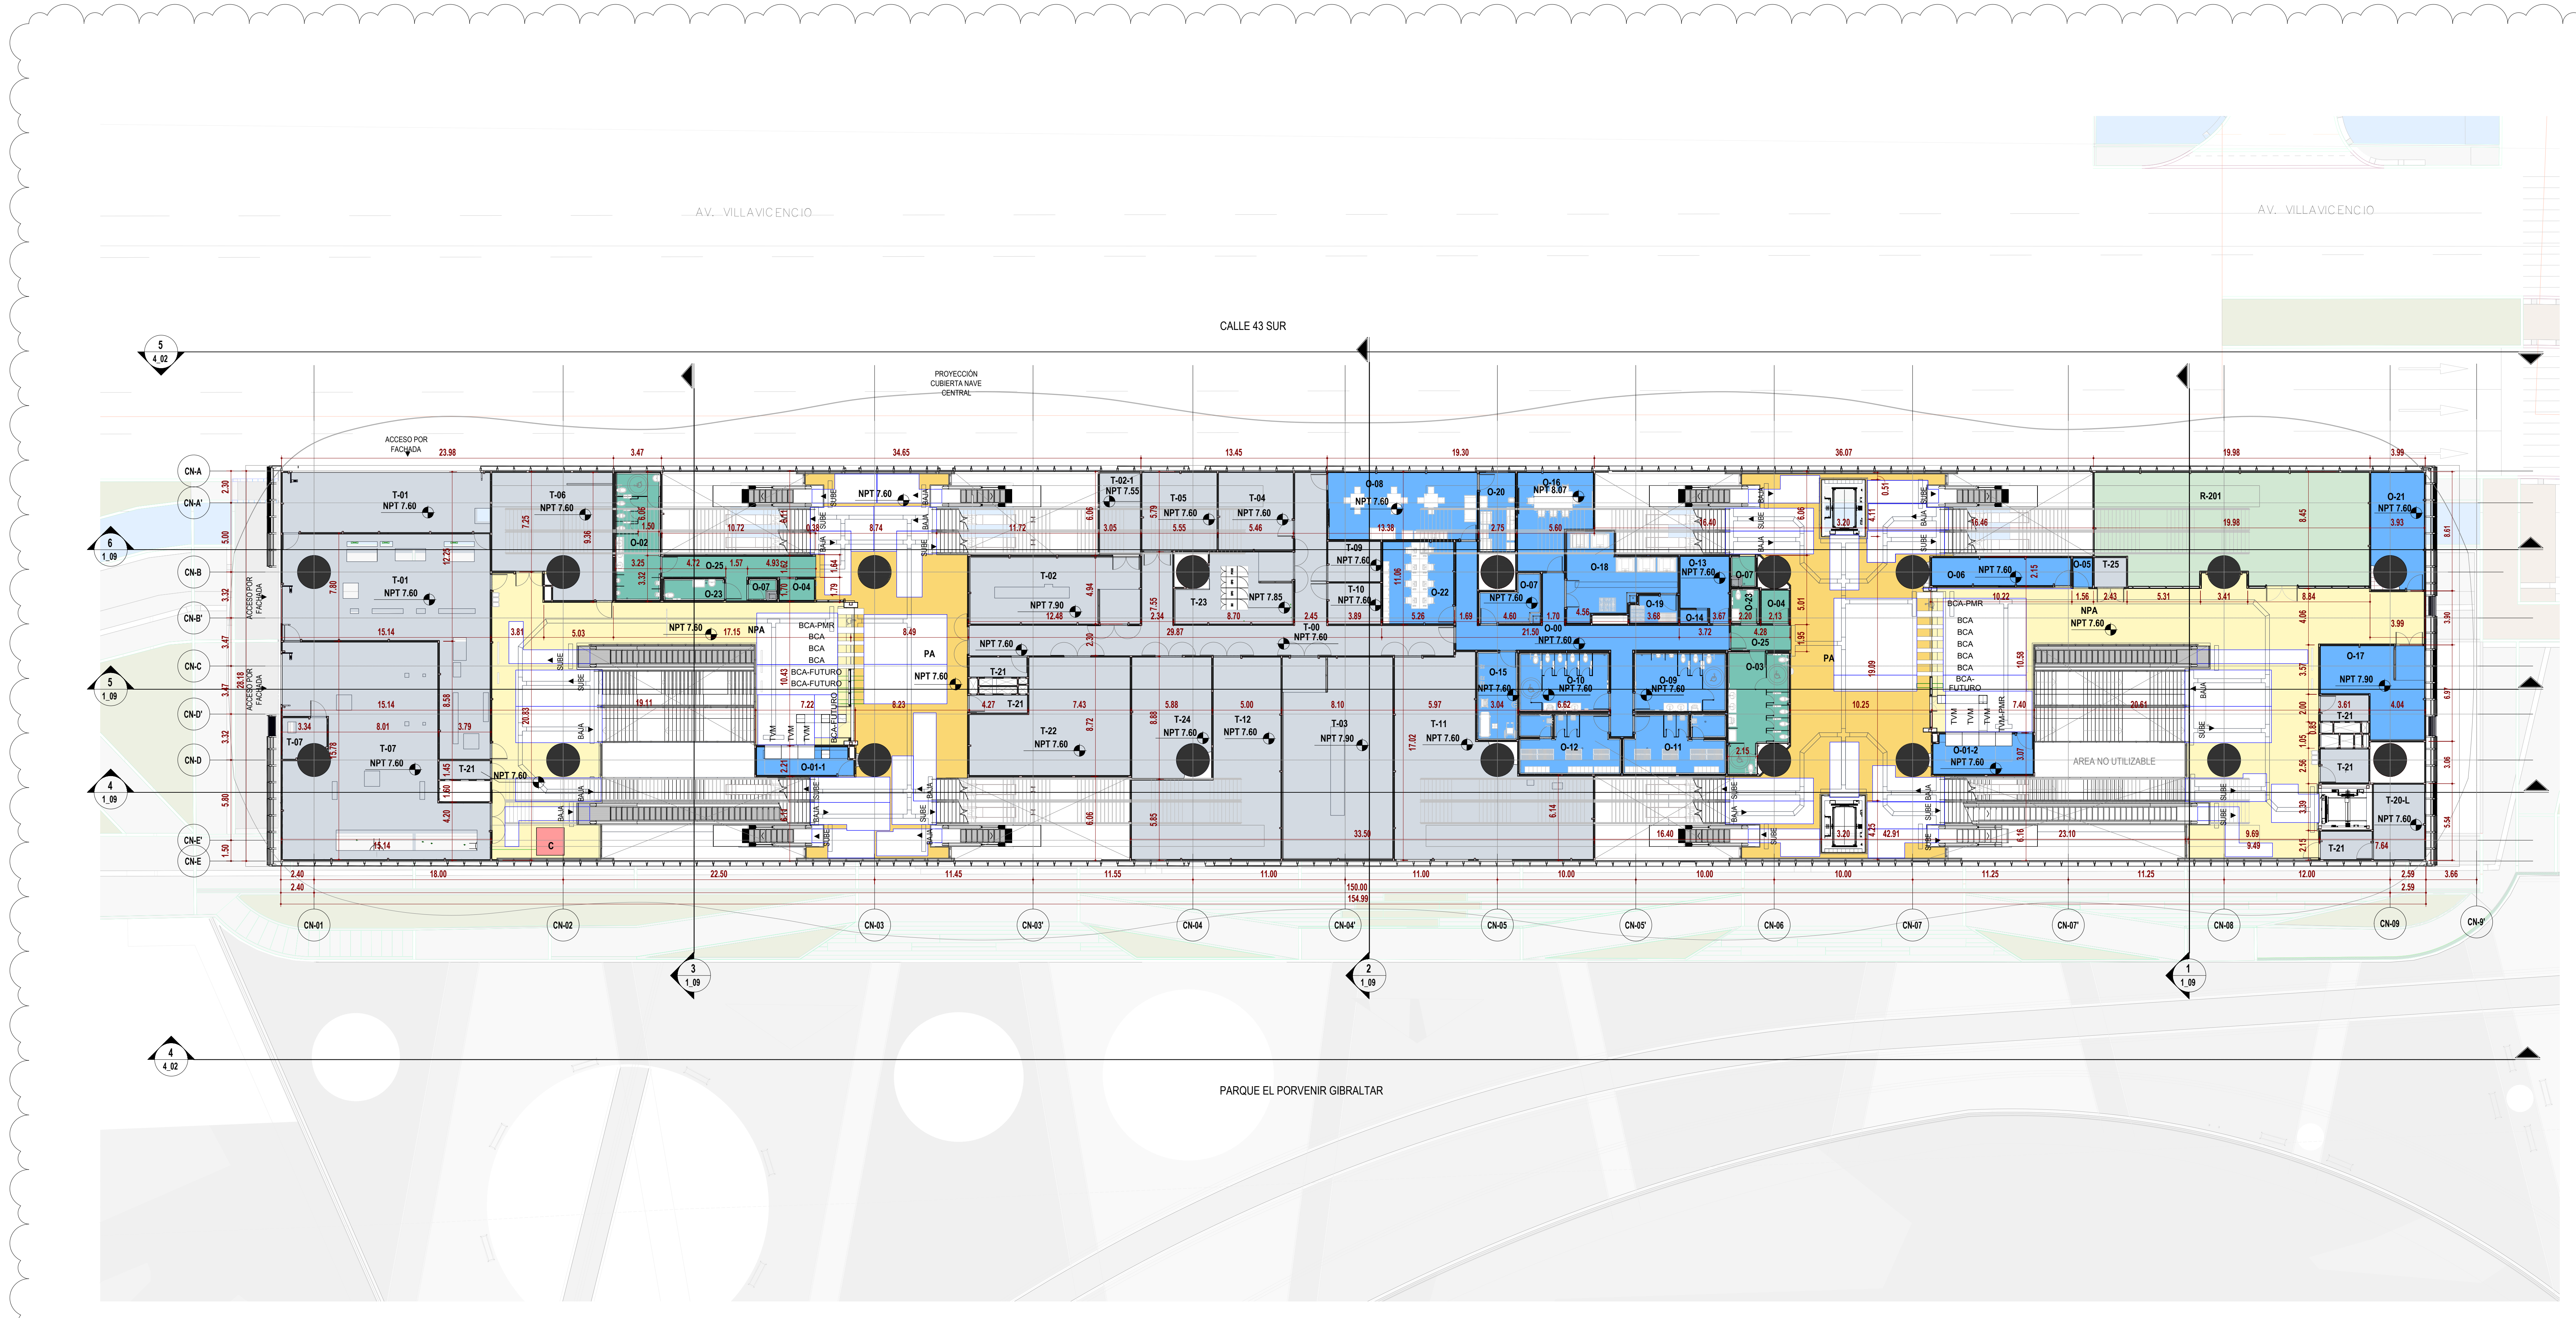

2 NIVEL INTERMEDIO_NAVE CENTRAL
ESC: 1 : 200

11_TABLA DE ÁREAS ÚTILES (NIVEL INTERMEDIO)

CÓDIGO	NOMBRE	ÁREA (m²)	DEPARTAMENTO
ARC_PL_02			
C	ÁREAS DE USO CULTURAL	4.01	ÁREA CULTURAL
NPA	ÁREA NO PAGA	342.09	ÁREA NO PAGA
NPA	ÁREA NO PAGA	249.52	ÁREA NO PAGA
O-00	CIRCULACIÓN ÁREAS OPERATIVAS	60.61	ÁREA OPERATIVA
O-01-1	VENTA AUTOMÁTICA DE BOLETOS	14.19	ÁREA OPERATIVA
O-01-2	VENTA AUTOMÁTICA DE BOLETOS	22.93	ÁREA OPERATIVA
O-02	BAÑOS PÚBLICOS - HOMBRES	29.56	SERVICIO PÚBLICO
O-03	BAÑOS PÚBLICOS - MUJERES	35.18	SERVICIO PÚBLICO
O-04	CONTROL DE ACCESO BAÑOS PÚBLICOS	4.88	SERVICIO PÚBLICO
O-04	CONTROL DE ACCESO BAÑOS PÚBLICOS	3.98	SERVICIO PÚBLICO
O-05	LOCAL DE INFORMACIÓN	2.97	ÁREA OPERATIVA
O-06	SUPERVISOR DE LA ESTACIÓN	20.24	ÁREA OPERATIVA
O-07	CUARTO DE LIMPIEZA	12.49	ÁREA OPERATIVA
O-07	CUARTO DE LIMPIEZA	2.73	SERVICIO PÚBLICO
O-07	CUARTO DE LIMPIEZA	3.38	SERVICIO PÚBLICO
O-08	SALA DE EMPLEADOS	52.08	ÁREA OPERATIVA
O-09	BAÑOS EMPLEADOS - HOMBRES	28.06	ÁREA OPERATIVA
O-10	BAÑOS EMPLEADOS - MUJERES	27.41	ÁREA OPERATIVA
O-11	VESTIDORES EMPLEADOS - HOMBRES	30.69	ÁREA OPERATIVA
O-12	VESTIDORES EMPLEADOS - MUJERES	30.16	ÁREA OPERATIVA
O-13	LOCAL DE POLICÍA	14.91	ÁREA OPERATIVA
O-14	CALABOZO	2.00	ÁREA OPERATIVA
O-15	LOCAL DE PRIMEROS AUXILIOS	18.45	ÁREA OPERATIVA
O-16	SALA DE REUNIÓN	32.81	ÁREA OPERATIVA
O-17	OPERADORES TELECOMUNICACIONES EXTERIORES	38.83	ÁREA OPERATIVA
O-18	CUARTO DE ALMACENAMIENTO DE RESIDUOS SÓLIDOS	36.42	ÁREA OPERATIVA
O-19	CUARTO DE ALMACENAMIENTO DE RESIDUOS PELIGROSOS	6.85	ÁREA OPERATIVA
O-20	SALA DE LACTANCIA	14.86	ÁREA OPERATIVA
O-21	ALMACENAMIENTO DE LA ESTACIÓN	27.50	ÁREA OPERATIVA
O-22	OFICINA DE MANTENIMIENTO	30.52	ÁREA OPERATIVA
O-23	BAÑO PÚBLICO - FAMILIAR	4.94	SERVICIO PÚBLICO
O-23	BAÑO PÚBLICO - FAMILIAR	6.86	SERVICIO PÚBLICO
O-25	BAÑO PÚBLICO - CORREDOR OPERACIONAL	19.24	SERVICIO PÚBLICO
O-25	BAÑO PÚBLICO - CORREDOR OPERACIONAL	7.71	SERVICIO PÚBLICO
PA	ÁREA PAGA	304.96	ÁREA PAGA
PA	ÁREA PAGA	239.88	ÁREA PAGA
R-201	SERVICIOS ADICIONALES - ÁREA DE COMIDAS	152.72	SERVICIOS ADICIONALES - ÁREA NO PAGA
T-00	CIRCULACIÓN TÉCNICA	113.74	ÁREA TÉCNICA
T-01	SUBESTACIÓN DE TRACCIÓN (SET)	209.15	ÁREA TÉCNICA
T-02	LOCAL DE CONDUCCIÓN AUTOMÁTICA (CBTC)	58.71	ÁREA TÉCNICA
T-02-1	UPS DEDICADA (CBTC)	17.11	ÁREA TÉCNICA
T-03	TELECOMUNICACIÓN ESTACIÓN - CORRIENTE DÉBIL	114.90	ÁREA TÉCNICA
T-04	EQUIPOS DE BOLETERÍA	30.40	ÁREA TÉCNICA
T-05	ALMACÉN PARA MANTENIMIENTO	30.58	ÁREA TÉCNICA
T-06	SALA DE TABLEROS	66.83	ÁREA TÉCNICA
T-07	CENTRO DE TRANSFORMACIÓN (CT)	187.11	ÁREA TÉCNICA
T-09	ALMACÉN EQUIPO ELÉCTRICO	11.03	ÁREA TÉCNICA
T-10	CUARTO DE EQUIPO ELECTROMECÁNICO	11.22	ÁREA TÉCNICA
T-11	CUARTO DE VENTILACIÓN	137.87	ÁREA TÉCNICA
T-12	PLANTA DE REFRIGERACIÓN PARA LA CLIMATIZACIÓN	104.98	ÁREA TÉCNICA
T-20-L	MEDIDORES (LUZ)	19.94	ÁREA TÉCNICA
T-21	ÁREA DE INSPECCIÓN	4.92	ÁREA TÉCNICA
T-21	ÁREA DE INSPECCIÓN	5.39	ÁREA TÉCNICA
T-21	ÁREA DE INSPECCIÓN	6.00	ÁREA TÉCNICA
T-21	ÁREA DE INSPECCIÓN	7.65	ÁREA TÉCNICA
T-21	ÁREA DE INSPECCIÓN	8.53	ÁREA TÉCNICA
T-21	ÁREA DE INSPECCIÓN	6.58	ÁREA TÉCNICA
T-22	CUARTO DE UPS	81.46	ÁREA TÉCNICA
T-23	CUARTO PDAP	37.20	ÁREA TÉCNICA
T-24	CUARTO DE UPS	41.27	ÁREA TÉCNICA
T-25	NODO DE ACCESO DE TELECOMUNICACIONES	4.88	ÁREA TÉCNICA
		3254.06	
TOTAL NIVEL INTERMEDIO_NAVE CENTRAL		3254.06	

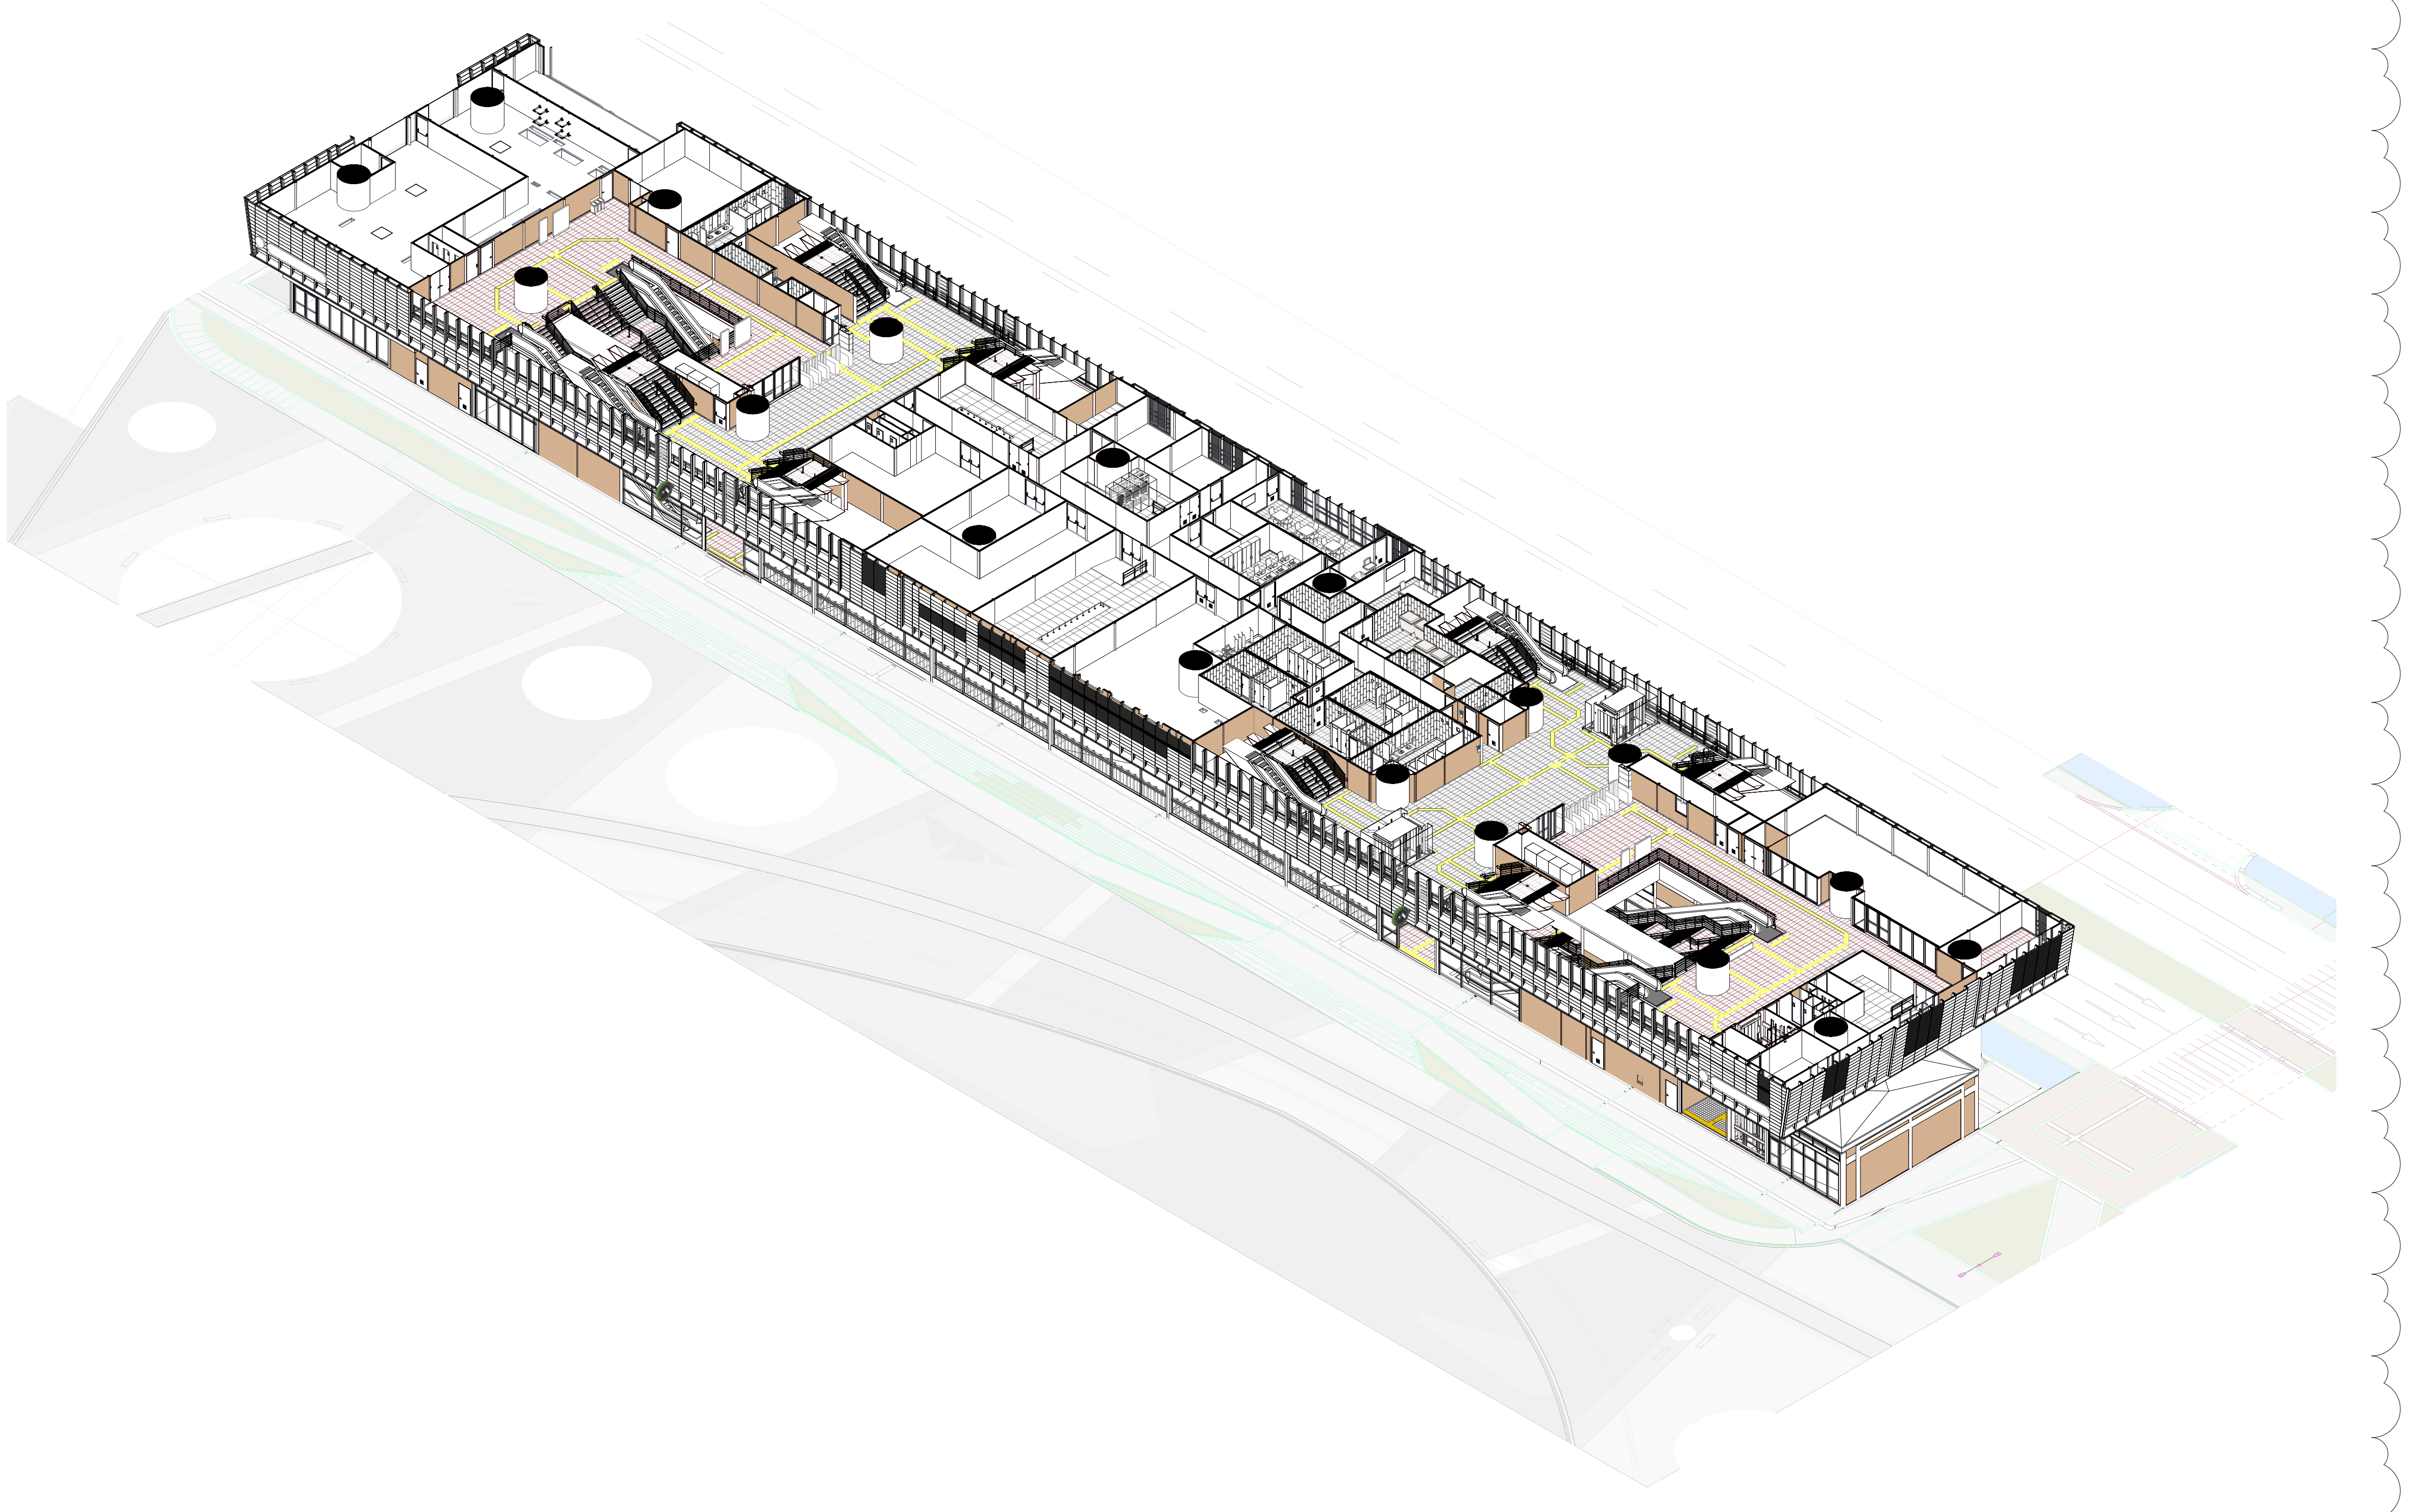

1 3D_NIVEL INTERMEDIO_NAVE CENTRAL
ESC: N/A

10_TABLA DE ÁREAS POR DEPARTAMENTO (NIVEL INTERMEDIO)

DEPARTAMENTO	ÁREA (m²)
SERVICIOS ADICIONALES - ÁREA NO PAGA	152.72
ÁREA CULTURAL	4.01
ÁREA NO PAGA	591.61
ÁREA OPERATIVA	524.97
ÁREA PAGA	544.84
SERVICIO PÚBLICO	118.47
ÁREA TÉCNICA	1317.45
TOTAL NIVEL	3254.06

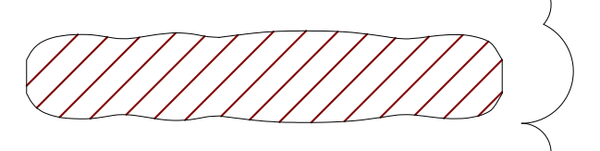

PLANO CLAVE ESTACIÓN 01

LOCALIZACIÓN

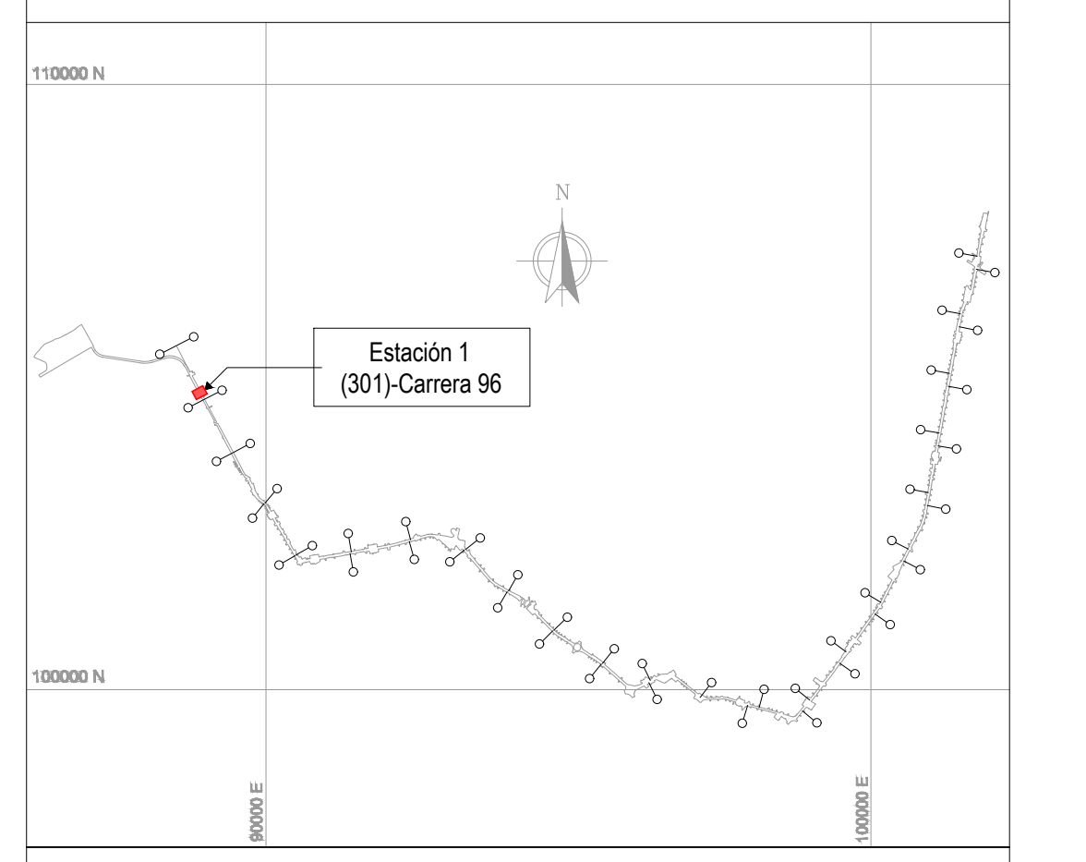

NOTAS

01 TODAS LAS DIMENSIONES ESTÁN CONFIGURADAS EN METROS A MENOS QUE SE INDIQUE UNA UNIDAD DE MEDIDA DIFERENTE.

02 TODAS LAS MEDIDAS, UBICACIÓN Y NIVELES DEBEN VERIFICARSE EN EL LUGAR DE CONSTRUCCIÓN.

03 EL NIVEL DE ACCESO AL EDIFICIO PL 01 CORRESPONDE AL +0,00 DE LA ESTACIÓN Y REFERENCIA AL NIVEL 2540.90 M.S.N.M

04 LOS NOMBRES ESPECIFICOS DE LAS ÁREAS PUEDEN SER CONSULTADAS EN EL PLANO NO. 3 O EN LAS VISTAS EN PLANTA.

05 LOS COLORES QUE SE MUESTRAN EN LOS PLANOS COMO PROYECCIÓN DE ELEMENTOS ARQUITECTÓNICOS COMO CUBIERTAS FACHADAS MUROS ETC. NO REPRESENTAN LA MATERIALIDAD Y REALIDAD DE ACABADOS DEL PROYECTO, SOLO SON INDICATIVOS PARA REALIZAR UNA CORRECTA LECTURA DE LA PLANIMETRÍA.

06 LAS ESCALERAS ELÉCTRICAS INDICAN SU SENTIDO CON LA SIGUIENTE NOMENCLATURA: "UP" SUBE Y "DW" BAJA.

07 EL NIVEL ESTRUCTURAL (NE) SE ENCUENTRA A (- 0.10m) POR DEBAJO DE LOS NIVELES DE PISO TERMINADO (NPT) MARCADOS EN LA PLANIMETRÍA.

08 PARA VER UBICACIÓN DE BAJANTES DE AGUAS LLUVIAS FAVOR REMITIRSE EL PLANO DE DISEÑO HIDROSANITARIO L1T1-1442-301-CON-ED-HID-PL-0014_VDD

- ARC_PL_00 = SÓTANO	/ NPT -5.80 m
- ARC_PL_01 = ACCESO	/ NPT -0.00 m
- ARC_PL_02 = INTERMEDIO	/ NPT -7.60 m
- ARC_PL_02.1 = PLACA INFERIOR VIGA CAJÓN	/ NPT -14.07 m
- ARC_PL_02.2 = TOPE DE RIEL (TOR)	/ NPT -16.20 m
- ARC_PL_03 = PLATAFORMA	/ NPT -17.34 m
- ARC_PL_05 = CUBIERTA NAVE CENTRAL	/ NPT -26.70 m

CONVENCIONES

- - -	LIMITE DE INTERVENCIÓN
- - -	AREAS DE ACUMULACIÓN
■	MURO DIVISORIO
— — —	PROYECCIÓN NIVEL SUPERIOR
▨	SERVICIOS ADICIONALES - ÁREA NO PAGA
🟩	SERVICIOS ADICIONALES - ÁREA PAGA
🟩	SERVICIO PÚBLICO
🟦	ZONA DE REFUGIO
🟥	ÁREA CULTURAL
🟩	ÁREA JARDÍN
🟨	ÁREA NO PAGA
🟦	ÁREA OPERACIONAL
🟧	ÁREA PAGA
🟦	ÁREA PÚBLICA
▨	ÁREA TÉCNICA

VB1 CAMBIOS REALIZADOS
1. AJUSTE DE ESCALERAS MECÁNICAS, CUARTOS TÉCNICOS T-02, T-02-1 Y CUADRO DE ÁREAS

No.	PLANOS DE REFERENCIA	REV.

No.	MODELO BIM DE REFERENCIA	REV.
1	L1T1-1100-201-CON-ED-EST-MO-0001.rvt	V01
2	L1T1-1100-202-CON-ED-EST-MO-0001.rvt	V01
3	L1T1-1100-301-CON-ED-EST-MO-0001.rvt	V03
4	L1T1-1150-201-CON-ED-EST-MO-0001.rvt	V01
5	L1T1-1150-202-CON-ED-EST-MO-0001.rvt	V01
6	L1T1-1410-301-CON-ED-MEC-MO-0001.rvt	V00
7	L1T1-1420-301-CON-ED-MEC-MO-0001.rvt	V00
8	L1T1-1430-301-CON-ED-MEC-MO-0001.rvt	V00

No.	PAQUETE DE TRABAJO DE REFERENCIA	REV.
1	XREF-URBANISM_CONTEXT_ST01.rvt	

0 2 10m
1:200

CONSORCIO SUPERVISOR PLMB

DISEÑO:	OSCAR HIGUERA H. Mat.:A20622022-1022410319
APROBÓ:	FELIPE SAAVEDRA Mat:.25202-149684 CND
REVISÓ:	VERóNICA MIRANDA Mat.:A25032002-52387701
DIBUJÓ:	EQUIPO PEDELTA

REVISIÓN No.	FECHA	DESCRIPCIÓN	REVISÓ	APROBÓ	APROBACIÓN CLIENTE
VB1	23/12/2025	EMITIDO PARA REVISIÓN Y COMENTARIOS DEL CLIENTE E INTERVENTORÍA	V.M.	F.S	
V00	23/08/2024	REVISIÓN NO OBJETADA - EMITIDO PARA CONSTRUCCIÓN	V.M.	F.S	
VDD	06/05/2024	EMITIDO PARA REVISIÓN Y COMENTARIOS DEL CLIENTE E INTERVENTORÍA	V.M.	F.S	
VCC	15/03/2024	EMITIDO PARA REVISIÓN Y COMENTARIOS DEL CLIENTE E INTERVENTORÍA	V.M.	F.S	
VBB	20/12/2023	EMITIDO PARA REVISIÓN Y COMENTARIOS DEL CLIENTE E INTERVENTORÍA	A.B.H	F.S	

METRO LÍNEA 1
CONTRATO DE CONCESIÓN No. 163 DE 2019

PROYECTO PRIMERA LÍNEA DEL METRO DE BOGOTÁ - TRAMO 1

DIRECTOR DE INTERVENTORÍA:
JAVIER DESCARGA N.
Mat.:2520268697 CND

ESPECIALISTA INTERVENTORÍA:
YOLANDA TARRIDA LÓPEZ
INT:

FECHA: DICIEMBRE 2025

INFRAESTRUCTURA VIAL
ARQUITECTURA
ESTACIÓN METRO 1 (CARRERA 96)
NAVE CENTRAL
VISTA EN PLANTA - NIVEL INTERMEDIO 01

PLANCHA No: L1T1-0000-301-CON-ED-ARQ-PL-0096_06_VB1	ESCALA: 1:200	REVISIÓN No. VB1	PLANO No. 06 DE 45
ARCHIVO: L1T1-0000-301-CON-ED-ARQ-MO-0001_V00.rvt	FECHA: DICIEMBRE 2023		