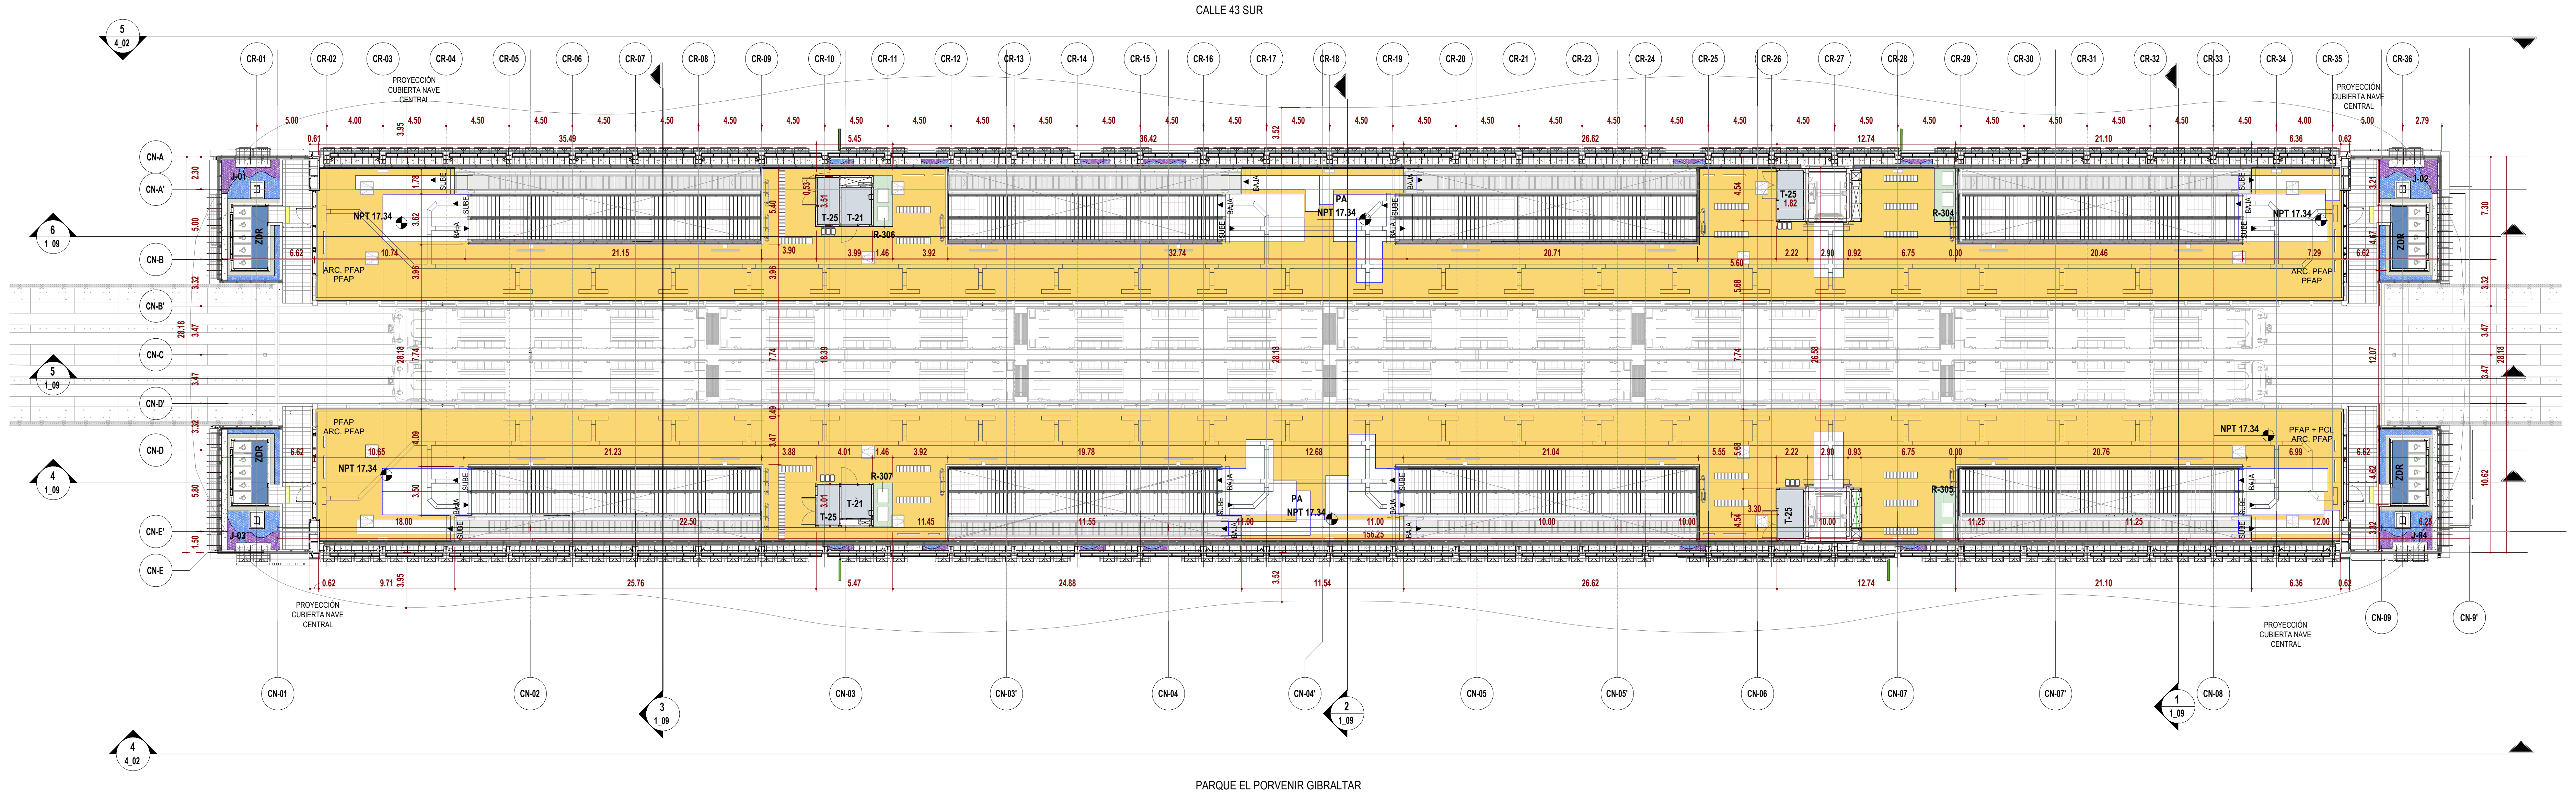

1 **NIVEL PLATAFORMA_NAVE CENTRAL**
ESC: 1 : 200

13_TABLA DE ÁREAS ÚTILES (NIVEL PLATAFORMA)

CÓDIGO	NOMBRE	ÁREA (m²)	DEPARTAMENTO
ARC_PL_03			
J-01	JARDÍN	15.28	JARDÍN
J-02	JARDÍN	15.28	JARDÍN
J-03	JARDÍN	15.28	JARDÍN
J-04	JARDÍN	19.46	JARDÍN
PA	ÁREA PAGA	891.88	ÁREA PAGA
PA	ÁREA PAGA	895.60	ÁREA PAGA
R-304	SERVICIOS ADICIONALES - MÁQUINAS EXPENDEDORAS/CAJEROS AUTOMÁTICOS	5.78	SERVICIOS ADICIONALES - ÁREA PAGA
R-305	SERVICIOS ADICIONALES - MÁQUINAS EXPENDEDORAS/CAJEROS AUTOMÁTICOS	5.68	SERVICIOS ADICIONALES - ÁREA PAGA
R-306	SERVICIOS ADICIONALES - MÁQUINAS EXPENDEDORAS/CAJEROS AUTOMÁTICOS	5.08	SERVICIOS ADICIONALES - ÁREA PAGA
R-307	SERVICIOS ADICIONALES - MÁQUINAS EXPENDEDORAS/CAJEROS AUTOMÁTICOS	4.38	SERVICIOS ADICIONALES - ÁREA PAGA
T-21	ÁREA DE INSPECCIÓN	5.75	ÁREA TÉCNICA
T-21	ÁREA DE INSPECCIÓN	5.13	ÁREA TÉCNICA
T-25	NODO DE ACCESO DE TELECOMUNICACIONES	4.48	ÁREA TÉCNICA
T-25	NODO DE ACCESO DE TELECOMUNICACIONES	5.20	ÁREA TÉCNICA
T-25	NODO DE ACCESO DE TELECOMUNICACIONES	6.34	ÁREA TÉCNICA
T-25	NODO DE ACCESO DE TELECOMUNICACIONES	6.36	ÁREA TÉCNICA
ZDR	ZONA DE REFUGIO (PMR)	10.83	ZONA DE REFUGIO
ZDR	ZONA DE REFUGIO (PMR)	10.84	ZONA DE REFUGIO
ZDR	ZONA DE REFUGIO (PMR)	10.84	ZONA DE REFUGIO
ZDR	ZONA DE REFUGIO (PMR)	10.84	ZONA DE REFUGIO
TOTAL NIVEL PLATAFORMA_NAVE CENTRAL		1950.31	

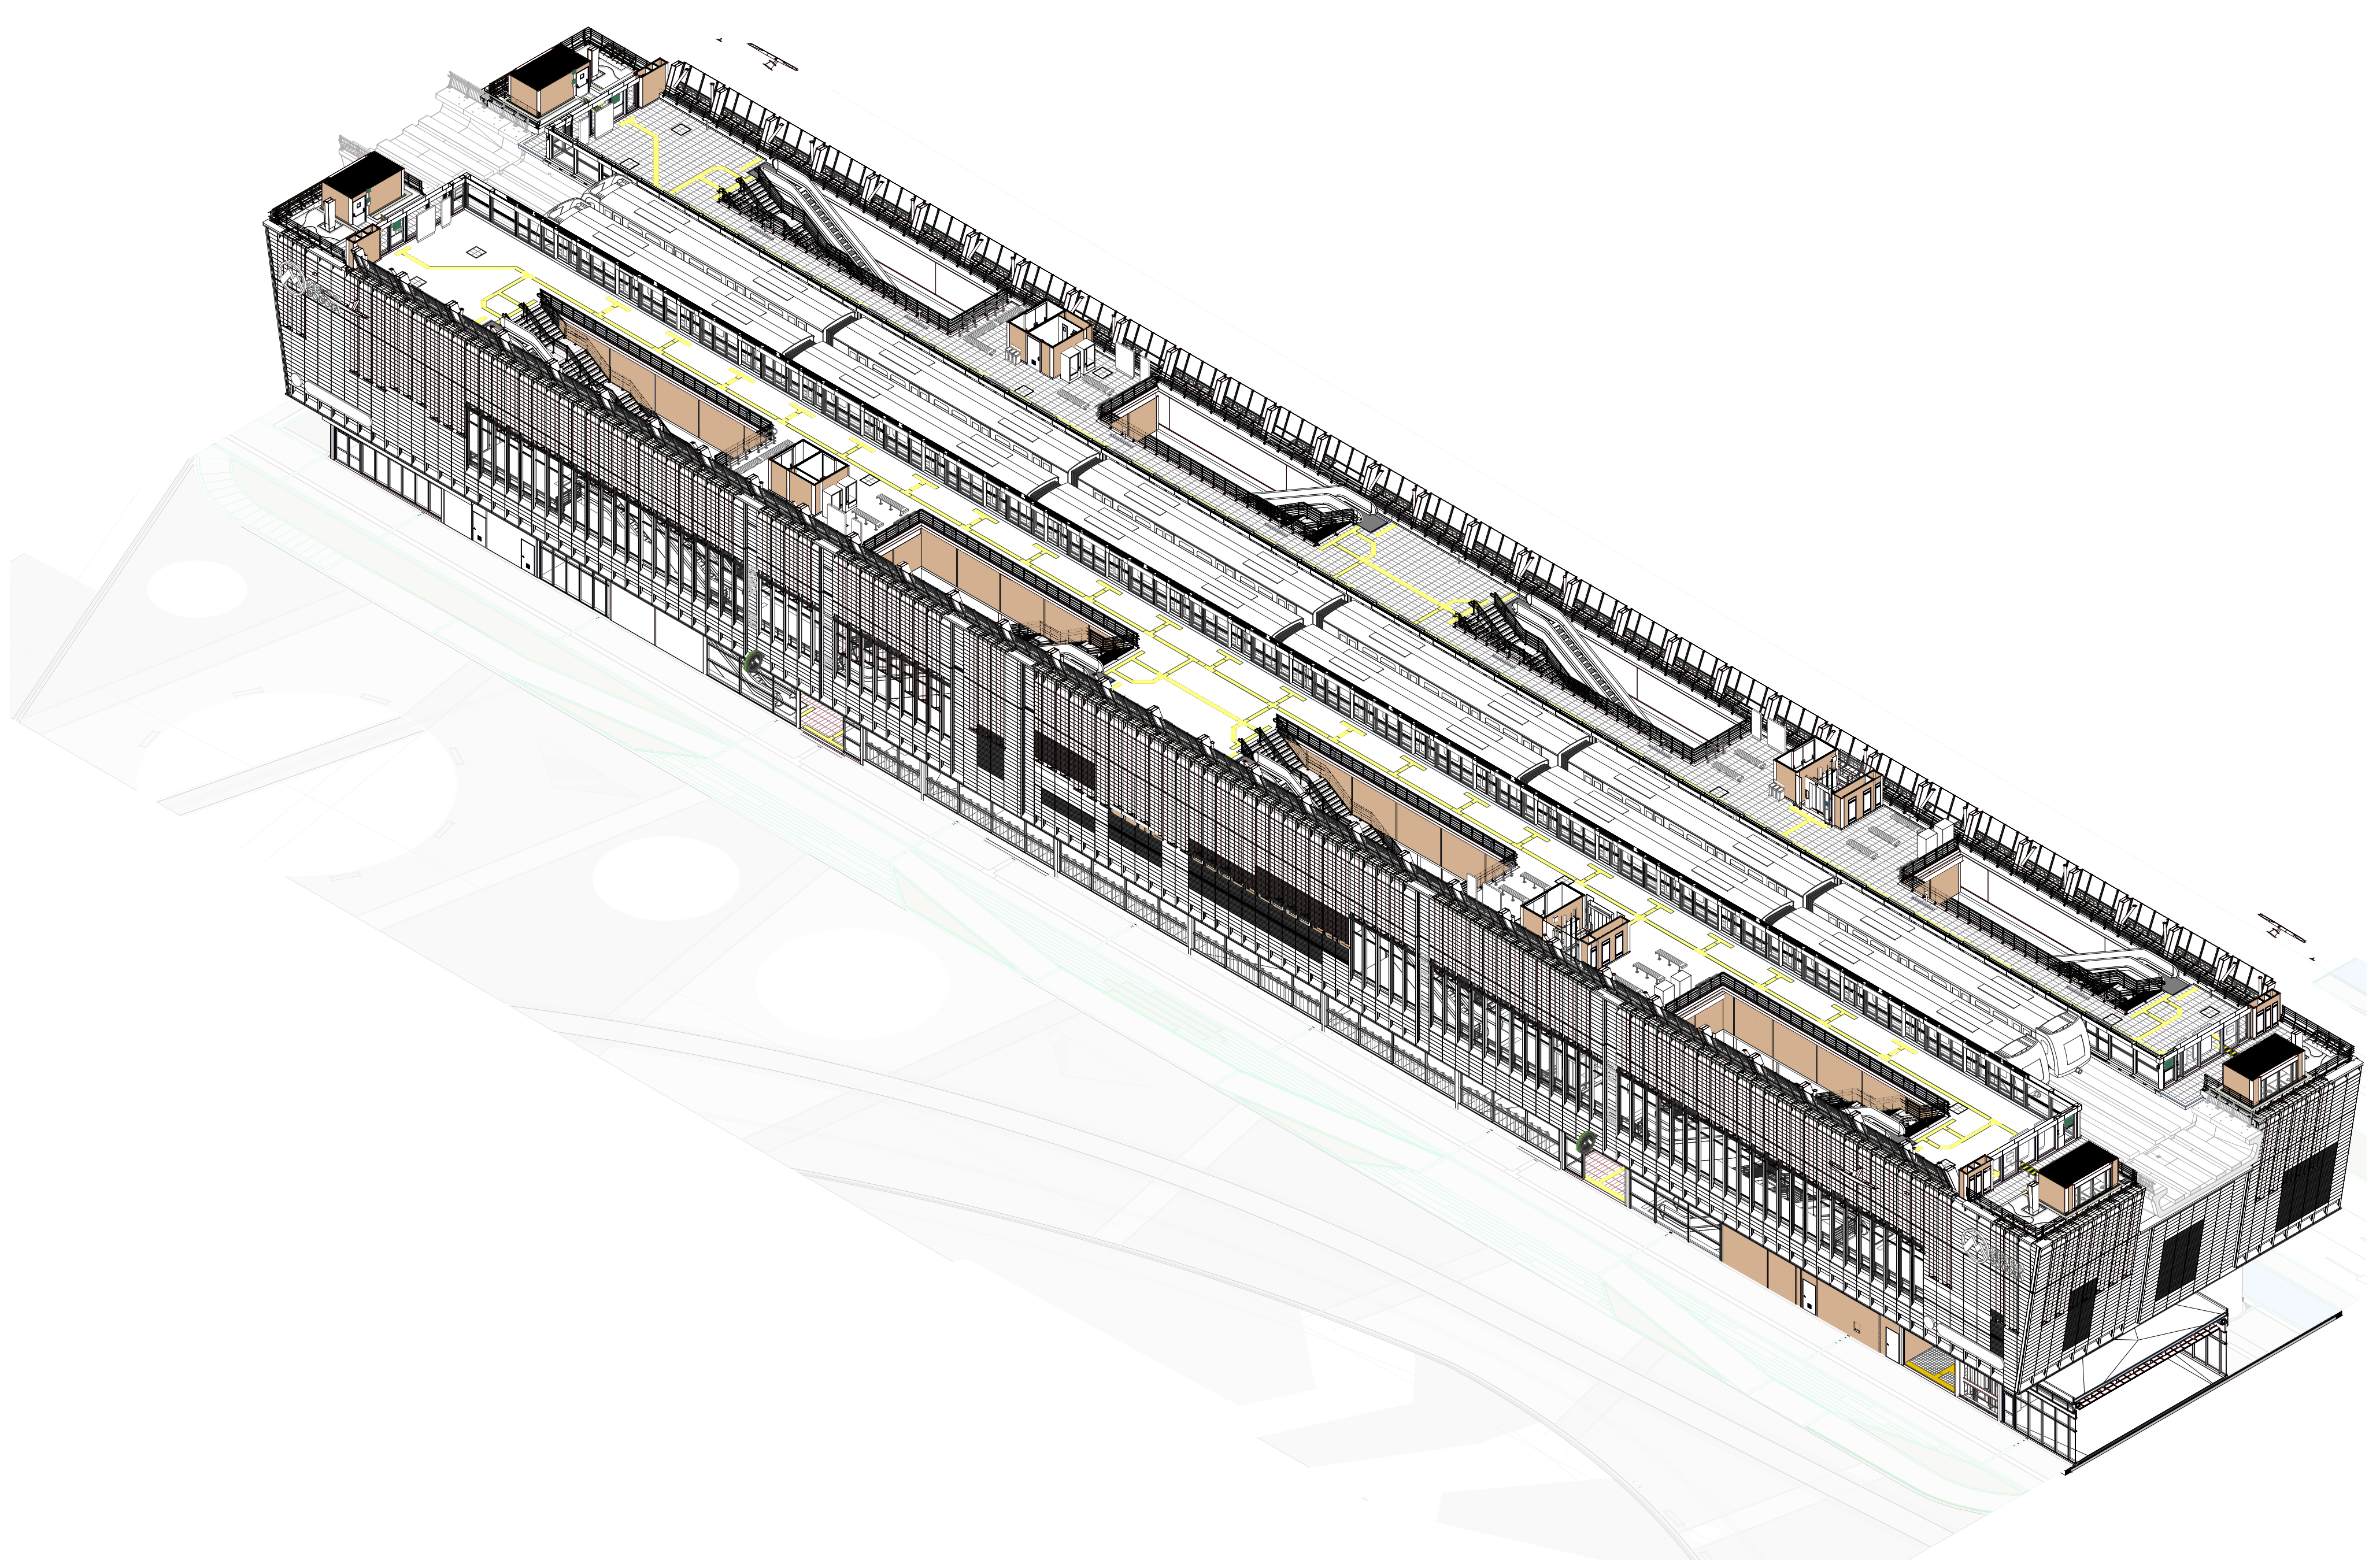

2 **3D_NIVEL PLATAFORMA_NAVE CENTRAL**
ESC: N/A

12_TABLA DE ÁREAS POR DEPARTAMENTO (NIVEL PLATAFORMA)

DEPARTAMENTO	ÁREA (m2)
SERVICIOS ADICIONALES - ÁREA PAGA	20.92
JARDÍN	65.31
ÁREA PAGA	1787.48
ZONA DE REFUGIO	43.34
ÁREA TÉCNICA	33.26
TOTAL NIVEL	1950.31

LOCALIZACIÓN

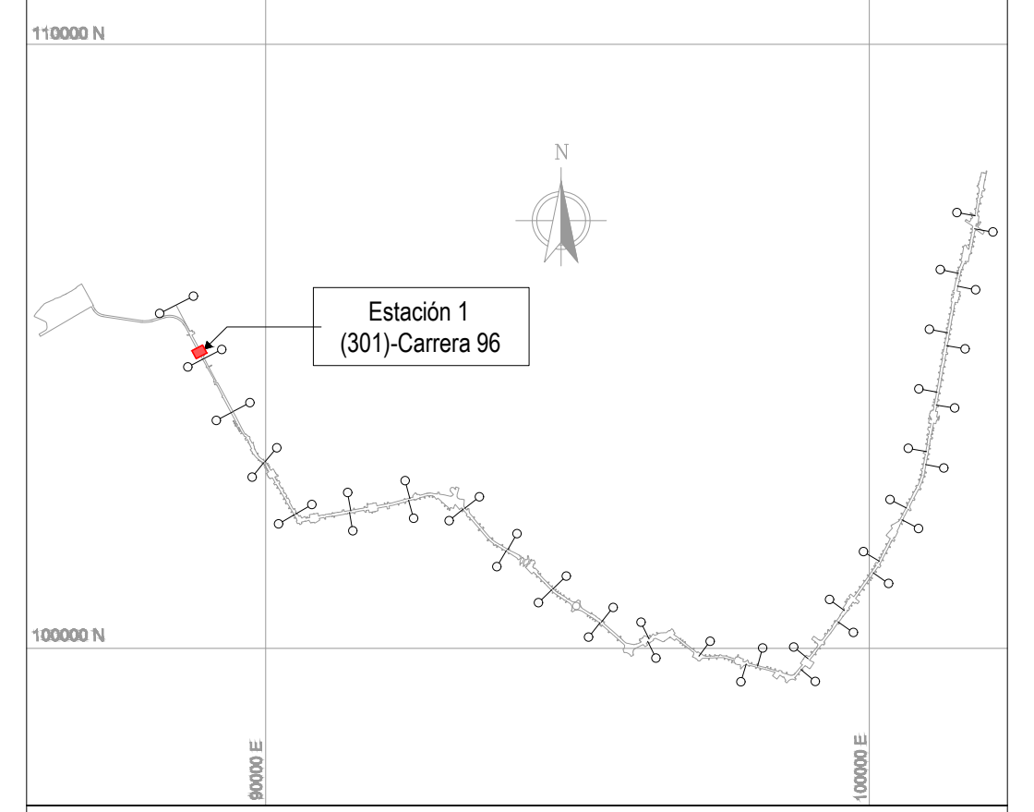

NOTAS

01 TODAS LAS DIMENSIONES ESTÁN CONFIGURADAS EN METROS A MENOS QUE SE INDIQUE UNA UNIDAD DE MEDIDA DIFERENTE.

02 TODAS LAS MEDIDAS, UBICACIÓN Y NIVELES DEBEN VERIFICARSE EN EL LUGAR DE CONSTRUCCIÓN.

03 EL NIVEL DE ACCESO AL EDIFICIO PL 01 CORRESPONDE AL +0,00 DE LA ESTACIÓN Y REFERENCIA AL NIVEL 2540.90 M.S.N.M

04 LOS NOMBRES ESPECIFICOS DE LAS ÁREAS PUEDEN SER CONSULTADAS EN EL PLANO NO. 3 O EN LAS VISTAS EN PLANTA.

05 LOS COLORES QUE SE MUESTRAN EN LOS PLANOS COMO PROYECCIÓN DE ELEMENTOS ARQUITECTÓNICOS COMO CUBIERTAS FACHADAS MUROS ETC. NO REPRESENTAN LA MATERIALIDAD Y REALIDAD DE ACABADOS DEL PROYECTO, SOLO SON INDICATIVOS PARA REALIZAR UNA CORRECTA LECTURA DE LA PLANIMETRÍA.

06 LAS ESCALERAS ELÉCTRICAS INDICAN SU SENTIDO CON LA SIGUIENTE NOMENCLATURA: "UP" SUBE Y "DW" BAJA.

07 EL NIVEL ESTRUCTURAL (NE) SE ENCUENTRA A (- 0.10m) POR DEBAJO DE LOS NIVELES DE PISO TERMINADO (NPT) MARCADOS EN LA PLANIMETRÍA.

08 PARA VER UBICACIÓN DE BAJANTES DE AGUAS LLUVIAS FAVOR REMITIRSE EL PLANO DE DISEÑO HIDROSANITARIO L1T1-1442-301-CON-ED-HID-PL-0014_VDD

- ARC_PL_00 = SÓTANO	/ NPT -5.80 m
- ARC_PL_01 = ACCESO	/ NPT -0.00 m
- ARC_PL_02 = INTERMEDIO	/ NPT -7.60 m
- ARC_PL_02.1 = PLACA INFERIOR VIGA CAJÓN	/ NPT -14.07 m
- ARC_PL_02.2 = TOPE DE RIEL (TOR)	/ NPT -16.20 m
- ARC_PL_03 = PLATAFORMA	/ NPT -17.34 m
- ARC_PL_05 = CUBIERTA NAVE CENTRAL	/ NPT -26.70 m

CONVENCIONES

▬ ▬ ▬	LIMITE DE INTERVENCIÓN
▬ ▬ ▬	AREAS DE ACUMULACIÓN
■	MURO DIVISORIO
— — —	PROYECCIÓN NIVEL SUPERIOR
▨	SERVICIOS ADICIONALES - ÁREA NO PAGA
🟩	SERVICIOS ADICIONALES - ÁREA PAGA
🟩	SERVICIO PÚBLICO
🟦	ZONA DE REFUGIO
🟥	ÁREA CULTURAL
🟩	ÁREA JARDÍN
🟨	ÁREA NO PAGA
🟦	ÁREA OPERACIONAL
🟧	ÁREA PAGA
🟦	ÁREA PÚBLICA
▨	ÁREA TÉCNICA

VB1 CAMBIOS REALIZADOS
1. AJUSTE DE ESCALERAS MECÁNICAS Y CUADRO DE ÁREAS

No.	PLANOS DE REFERENCIA	REV.

No.	MODELO BIM DE REFERENCIA	REV.
1	L1T1-1100-201-CON-ED-EST-MO-0001.rvt	V01
2	L1T1-1100-202-CON-ED-EST-MO-0001.rvt	V01
3	L1T1-1100-301-CON-ED-EST-MO-0001.rvt	V03
4	L1T1-1150-201-CON-ED-EST-MO-0001.rvt	V01
5	L1T1-1150-202-CON-ED-EST-MO-0001.rvt	V01
6	L1T1-1410-301-CON-ED-MEC-MO-0001.rvt	V00
7	L1T1-1420-301-CON-ED-MEC-MO-0001.rvt	V00
8	L1T1-1430-301-CON-ED-MEC-MO-0001.rvt	V00

No.	PAQUETE DE TRABAJO DE REFERENCIA	REV.
1	XREF-URBANISM_CONTEXT_ST01.rvt	

1 VB1

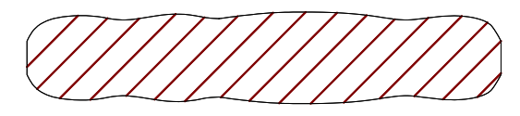

PLANO CLAVE ESTACIÓN 01

0 2 10m
1:200

METRO BOGOTÁ
GCS Consorcio Consultores PMO Bogotá
CONSORCIO SUPERVISOR PLMB
PEDELTA

DISEÑÓ:	OSCAR HIGUERA H. Mat.:A20622022-1022410319
APROBÓ:	FELIPE SAAVEDRA Mat.:25202-149684 CND
REVISÓ:	VERÓNICA MIRANDA Mat.:A25032002-52387701
DIBUJÓ:	EQUIPO PEDELTA

REVISIÓN No.	FECHA	DESCRIPCIÓN	REVISÓ	APROBÓ	APROBACIÓN CLIENTE
VB1	23/12/2025	EMITIDO PARA REVISIÓN Y COMENTARIOS DEL CLIENTE E INTERVENTORÍA	V.M.	F.S	
V00	23/08/2024	REVISIÓN NO OBJETADA - EMITIDO PARA CONSTRUCCIÓN	V.M.	F.S	
VDD	06/05/2024	EMITIDO PARA REVISIÓN Y COMENTARIOS DEL CLIENTE E INTERVENTORÍA	V.M.	F.S	
VCC	15/03/2024	EMITIDO PARA REVISIÓN Y COMENTARIOS DEL CLIENTE E INTERVENTORÍA	V.M.	F.S	
VBB	20/12/2023	EMITIDO PARA REVISIÓN Y COMENTARIOS DEL CLIENTE E INTERVENTORÍA	A.B.H	F.S	

METRO LÍNEA 1

METRO LÍNEA 1
CONTRATO DE CONCESIÓN No. 163 DE 2019

PROYECTO PRIMERA LÍNEA DEL METRO DE BOGOTÁ - TRAMO 1

DIRECTOR DE INTERVENTORÍA:
JAVIER DESCARGA N.
Mat.:2520268697 CND

ESPECIALISTA INTERVENTORÍA:
YOLANDA TARRIDA LÓPEZ
INT:

FECHA:
DICIEMBRE 2025

INFRAESTRUCTURA VIAL

ARQUITECTURA

ESTACIÓN METRO 1 (CARRERA 96)
NAVE CENTRAL
VISTA EN PLANTA - NIVEL PLATAFORMA 01

PLANCHA No: L1T1-0000-301-CON-ED-ARQ-PL-0096_07_VB1	ESCALA: 1:200	REVISIÓN No.	PLANO No.
ARCHIVO: L1T1-0000-301-CON-ED-ARQ-MO-0001_V00.rvt	FECHA: DICIEMBRE 2023	VB1	07 DE 45