L1T1-CON-CAL-FR-0120 - B1 : 1000x707mm

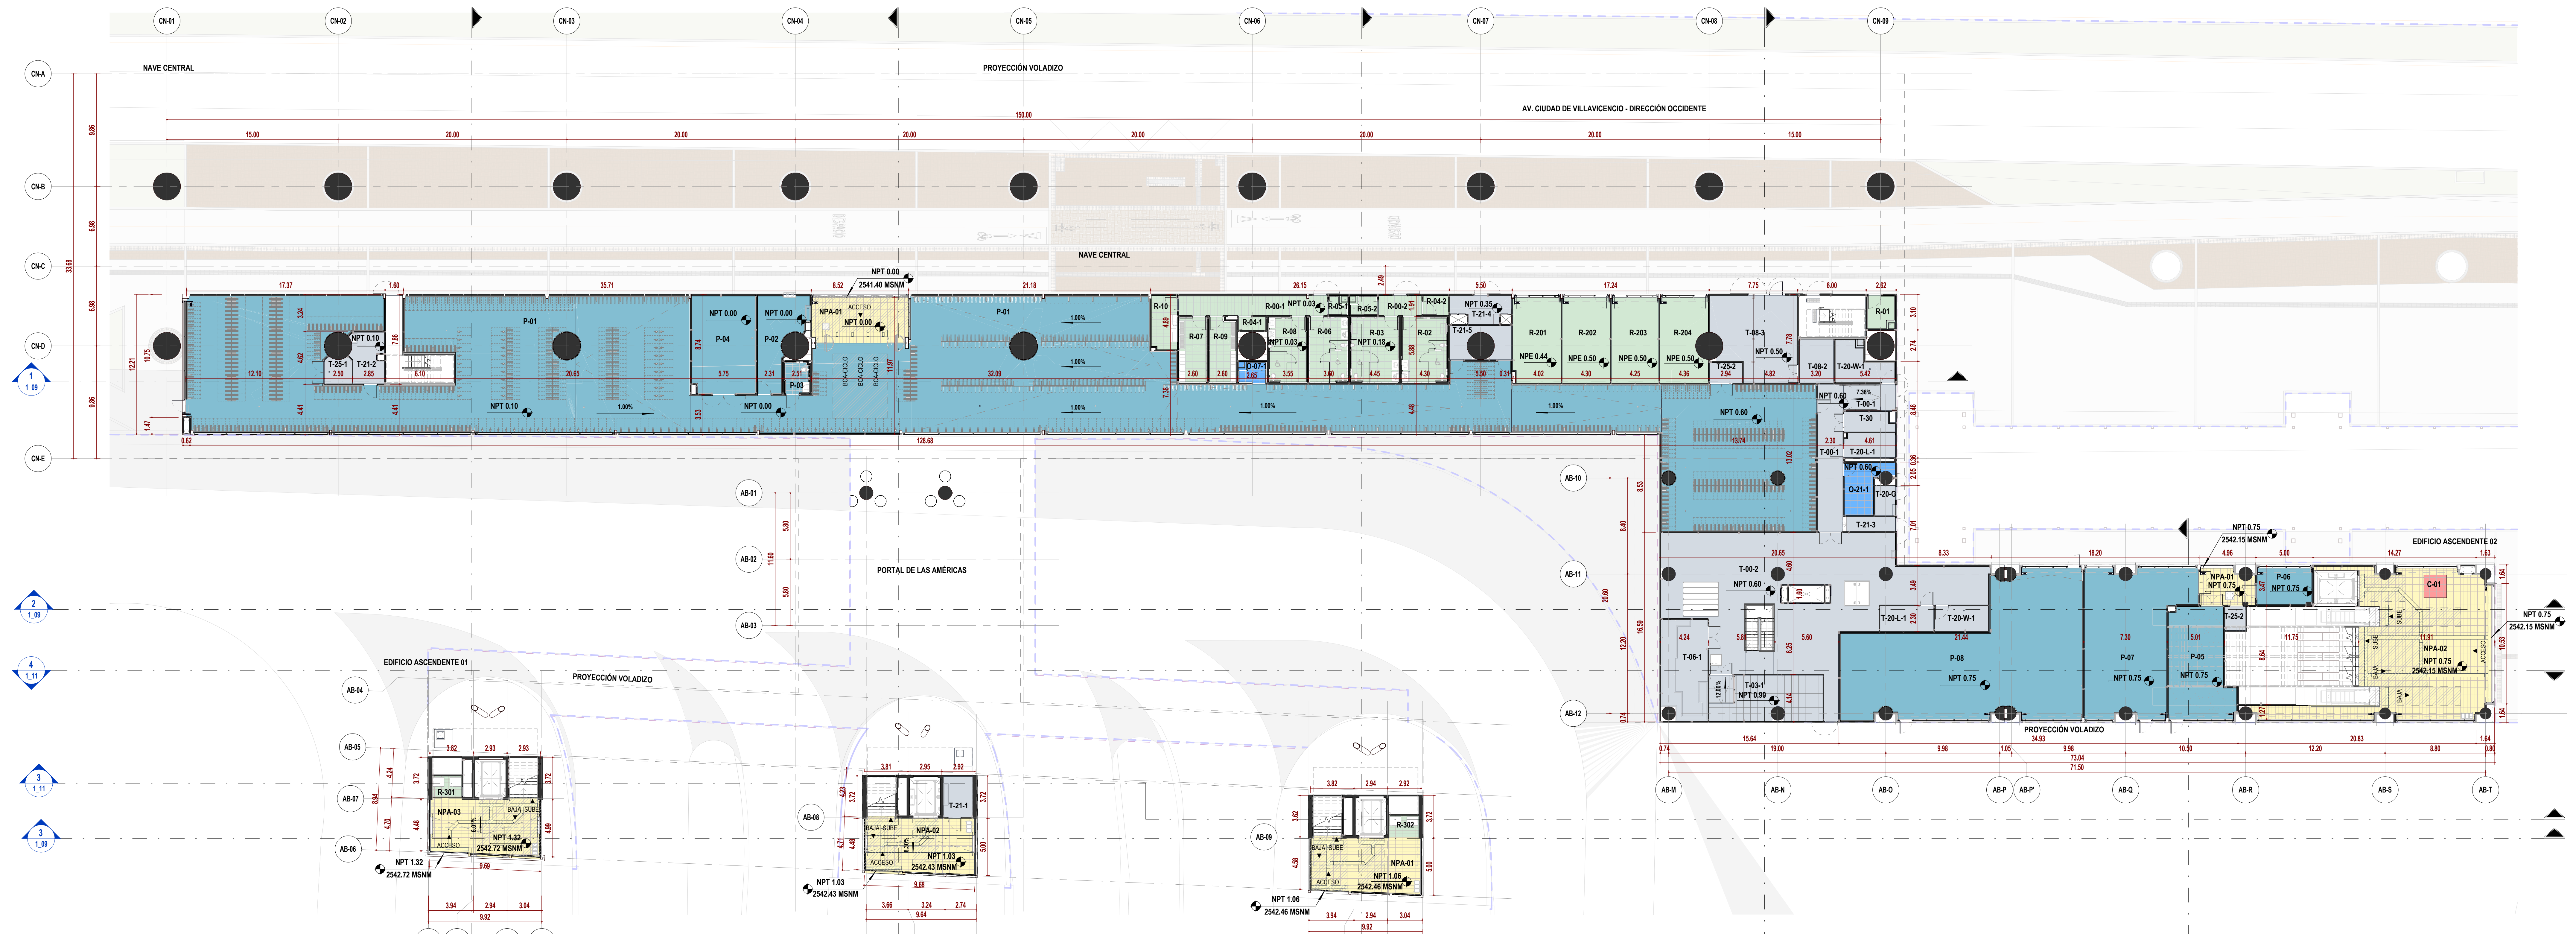

2 **NIVEL ACCESO_GENERAL**
ESC: 1 : 200

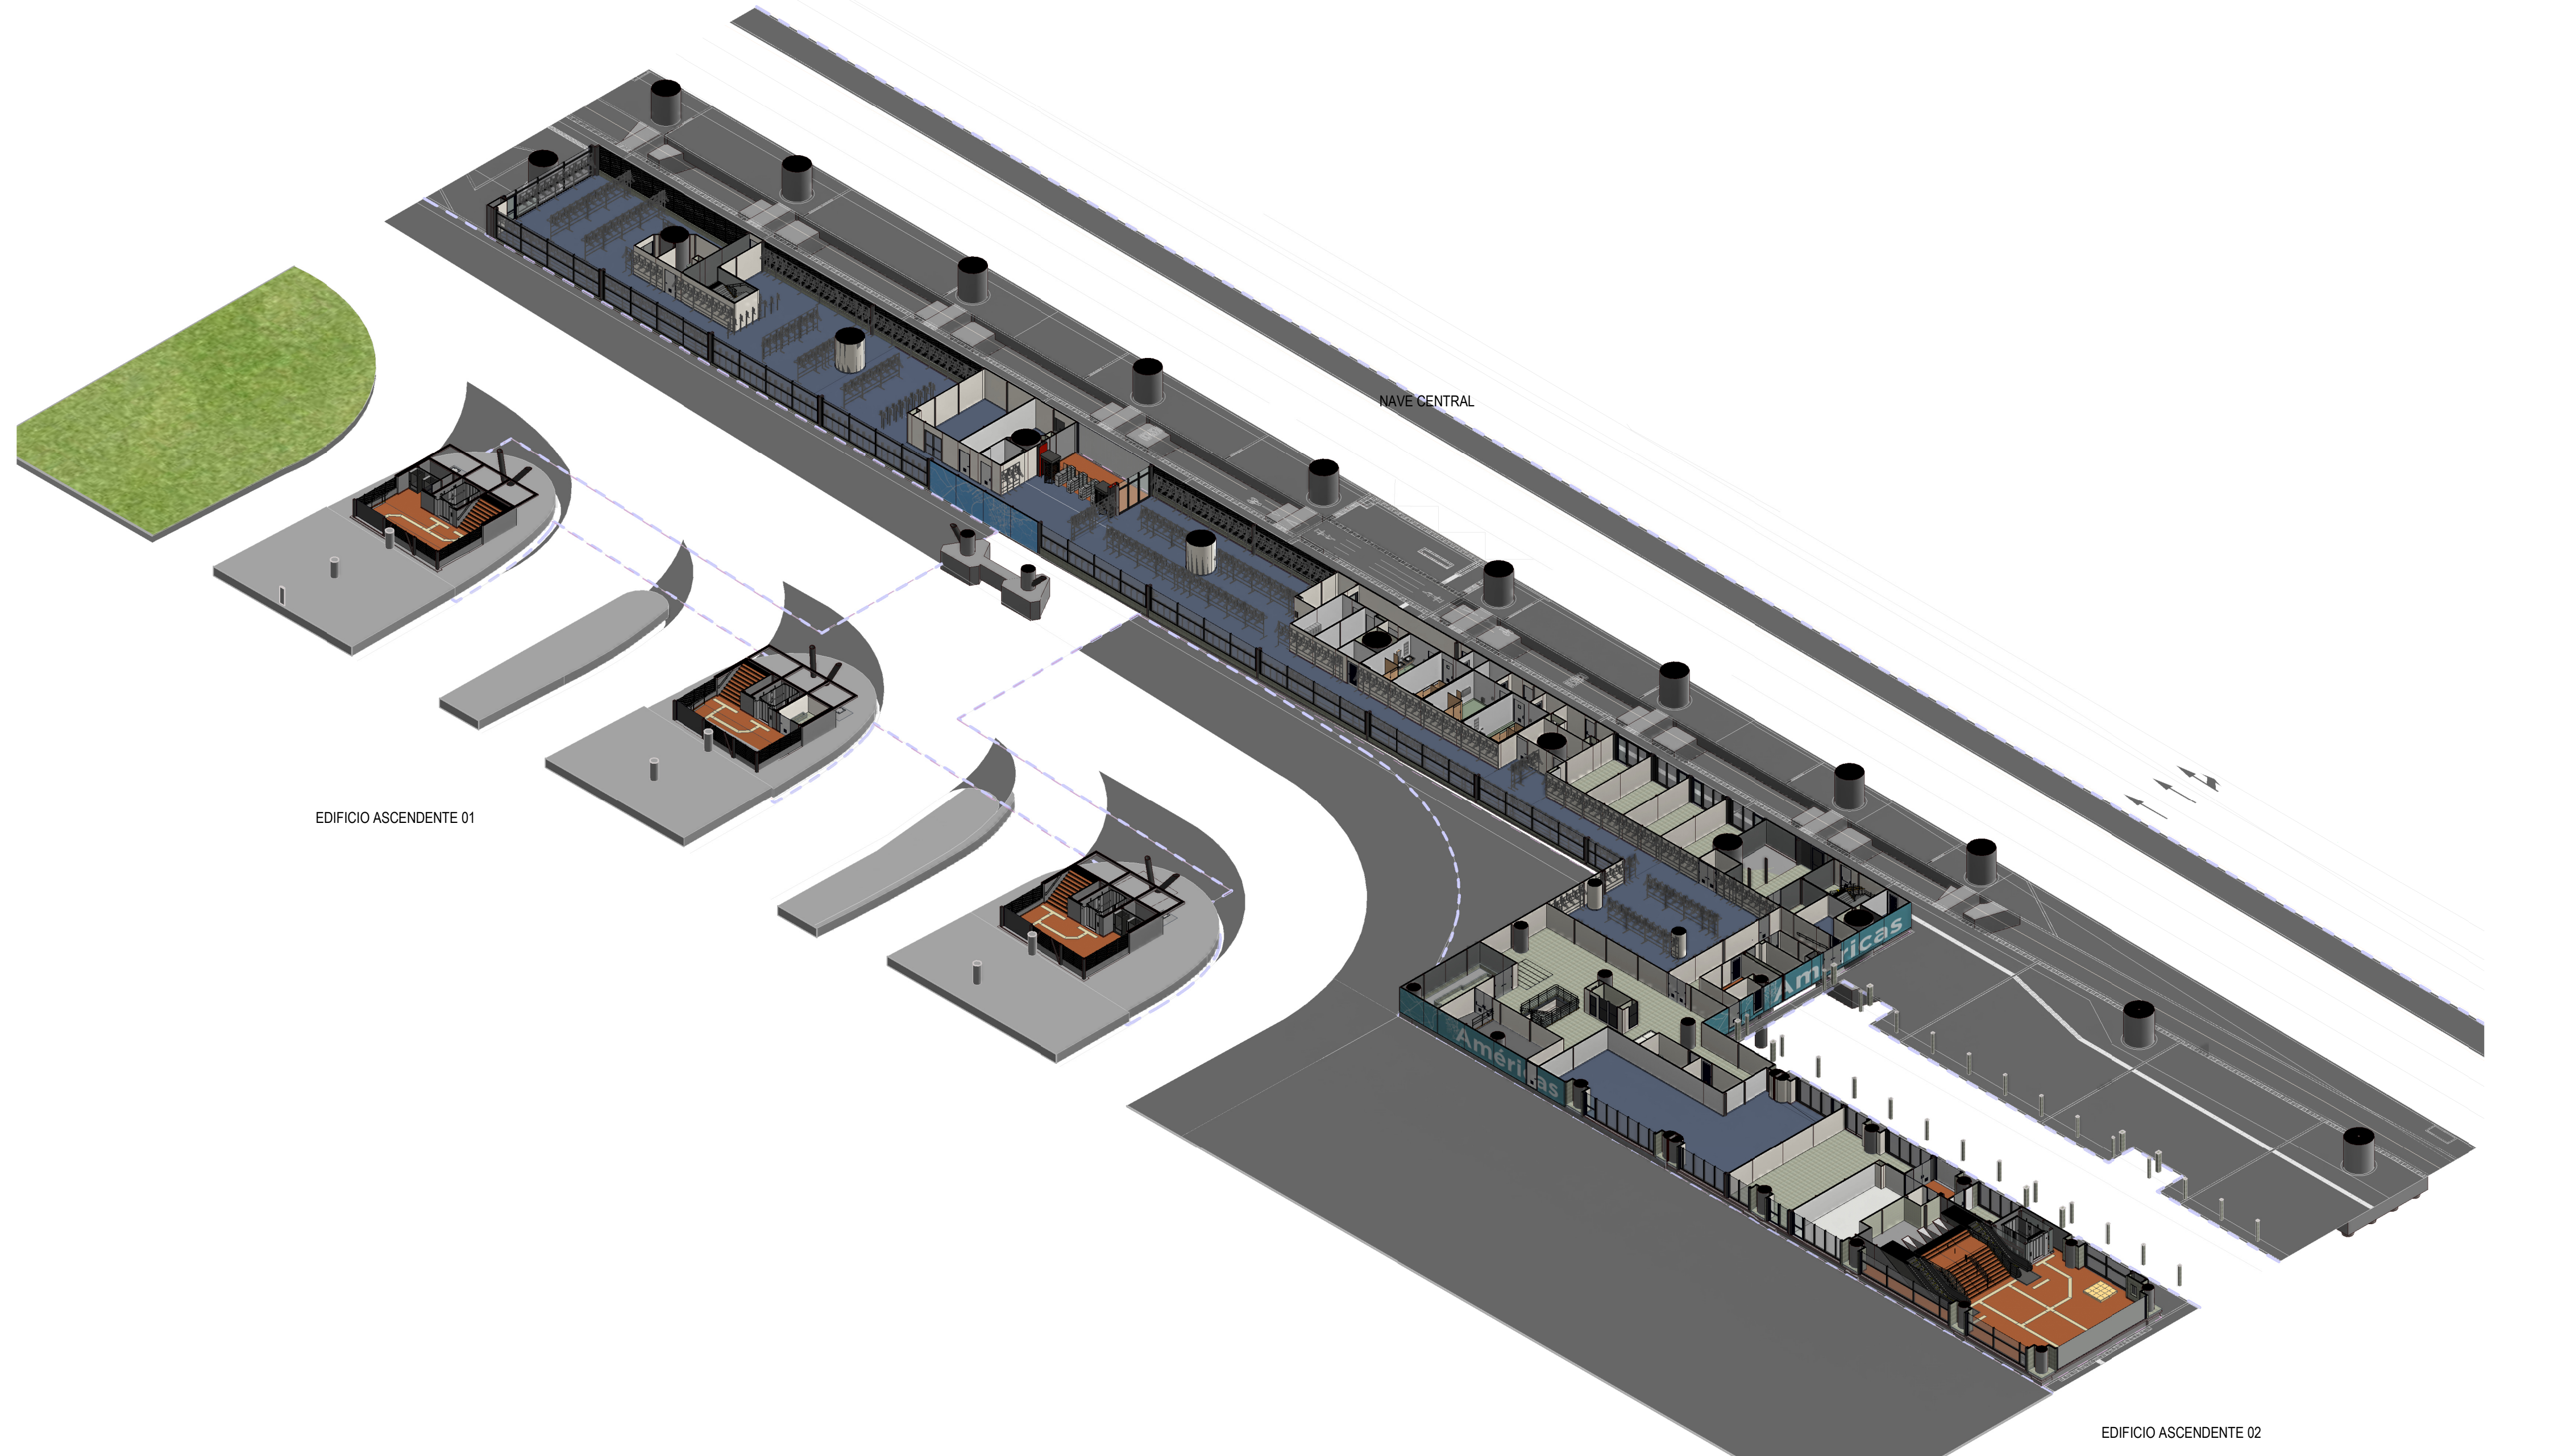

1 **3D_NIVEL ACCESO_GENERAL**
ESC: N/A

TABLA DE ÁREAS ÚTILES (NIVEL ACCESO)

CÓDIGO	NOMBRE	ÁREA (m²)	DEPARTAMENTO
EDIFICIO ASCENDENTE 01			
ARQ_PL_01.3_ACCESO			
NPA-02	ÁREA NO PAGA	46.46	ÁREA NO PAGA
		46.46	
ARQ_PL_01.4_ACCESO			
NPA-01	ÁREA NO PAGA	46.33	ÁREA NO PAGA
R-302	SERVICIOS ADICIONALES - MÁQUINAS EXPENDEDORAS/CAJEROS AUTOMÁTICOS	4.94	SERVICIOS ADICIONALES - ÁREA NO PAGA
		51.28	
ARQ_PL_01.5_ACCESO			
NPA-03	ÁREA NO PAGA	48.66	ÁREA NO PAGA
R-301	SERVICIOS ADICIONALES - MÁQUINAS EXPENDEDORAS/CAJEROS AUTOMÁTICOS	4.89	SERVICIOS ADICIONALES - ÁREA NO PAGA
T-21-1	ÁREA DE INSPECCIÓN	9.20	ÁREA TÉCNICA
		62.75	
EDIFICIO ASCENDENTE 02			
ARQ_PL_01.2_ACCESO			
T-00-2	CIRCULACIÓN TÉCNICA	226.95	ÁREA TÉCNICA
T-03-1	LOCAL SECUNDARIO DE TELECOMUNICACIONES	38.44	ÁREA TÉCNICA
T-06-1	LOCAL SECUNDARIO DE TABLEROS	34.69	ÁREA TÉCNICA
T-20-L-1	MEDIDORES (LUZ)	10.27	ÁREA TÉCNICA
T-20-W-1	MEDIDORES (AGUA)	10.19	ÁREA TÉCNICA
T-21-1	ÁREA DE INSPECCIÓN	5.11	ÁREA TÉCNICA
		325.65	
ARQ_PL_01.3_ACCESO			
C-01	ÁREAS DE USO CULTURAL	4.00	ÁREA CULTURAL
NPA-01	ÁREA NO PAGA	14.77	ÁREA NO PAGA

TABLA DE ÁREAS ÚTILES (NIVEL ACCESO)

CÓDIGO	NOMBRE	ÁREA (m²)	DEPARTAMENTO
NPA-02	ÁREA NO PAGA	156.83	ÁREA NO PAGA
P-05	BIBLIOMETRO	50.06	ÁREA PÚBLICA
P-06	ESPACIO IPES (INSTITUTO PARA LA ECONOMÍA SOCIAL)	15.09	ÁREA PÚBLICA
P-07	SALÓN MÚLTIPLE EMB	100.30	ÁREA PÚBLICA
P-08	ESPACIO CARGA DE VEHÍCULOS ELÉCTRICOS	200.61	ÁREA PÚBLICA
T-25-2	NODO DE ACCESO DE TELECOMUNICACIONES	3.68	ÁREA TÉCNICA
		545.33	
NAVE CENTRAL			
ARQ_PL_01_ACCESO			
NPA-01	ÁREA NO PAGA	34.29	ÁREA NO PAGA
P-01	ÁREA CICLO-PARQUEADEROS	1204.84	ÁREA PÚBLICA
P-02	ÁREA OPERATIVA CICLO-PARQUEADEROS	26.48	ÁREA PÚBLICA
P-03	BAÑO OPERADOR CICLO-PARQUEADEROS	6.18	ÁREA PÚBLICA
P-04	TALLER DE BICICLETAS	48.14	ÁREA PÚBLICA
R-00-1	SERVICIOS ADICIONALES - CORREDOR OPERATIVO	23.22	SERVICIOS ADICIONALES - ÁREA NO PAGA
R-04-1	SERVICIOS ADICIONALES - CONTROL DE ACCESO BAÑOS PÚBLICOS	2.94	SERVICIOS ADICIONALES - ÁREA NO PAGA
R-05-1	SERVICIOS ADICIONALES - CUARTO DE LIMPIEZA	3.02	SERVICIOS ADICIONALES - ÁREA NO PAGA
R-06	SERVICIOS ADICIONALES - BAÑOS EMPLEADOS MUJERES	19.69	SERVICIOS ADICIONALES - ÁREA NO PAGA
R-07	SERVICIOS ADICIONALES - VESTIDORES EMPLEADOS MUJERES	14.24	SERVICIOS ADICIONALES - ÁREA NO PAGA
R-08	SERVICIOS ADICIONALES - BAÑOS EMPLEADOS HOMBRES	19.53	SERVICIOS ADICIONALES - ÁREA NO PAGA
R-09	SERVICIOS ADICIONALES - VESTIDORES EMPLEADOS HOMBRES	13.87	SERVICIOS ADICIONALES - ÁREA NO PAGA
R-10	SERVICIOS ADICIONALES - SALA DE EMPLEADOS	10.80	SERVICIOS ADICIONALES - ÁREA NO PAGA
		1427.24	
ARQ_PL_01.1_ACCESO			
O-07-1	CUARTO DE LIMPIEZA COMPLEMENTARIO	4.75	ÁREA OPERATIVA
R-00-2	SERVICIOS ADICIONALES - CORREDOR OPERATIVO	6.81	SERVICIOS ADICIONALES - ÁREA NO PAGA
R-01	SERVICIOS ADICIONALES - CUARTO DE BASURAS PARA METRO	7.37	SERVICIOS ADICIONALES - ÁREA NO PAGA
R-02	SERVICIOS ADICIONALES - BAÑO PÚBLICO DE MUJERES	23.11	SERVICIOS ADICIONALES - ÁREA NO PAGA

TABLA DE ÁREAS ÚTILES (NIVEL ACCESO)

CÓDIGO	NOMBRE	ÁREA (m²)	DEPARTAMENTO
R-03	SERVICIOS ADICIONALES - BAÑO PÚBLICO DE HOMBRES	24.28	SERVICIOS ADICIONALES - ÁREA NO PAGA
R-04-2	SERVICIOS ADICIONALES - CONTROL DE ACCESO BAÑOS PÚBLICOS	4.02	SERVICIOS ADICIONALES - ÁREA NO PAGA
R-05-2	SERVICIOS ADICIONALES - CUARTO DE LIMPIEZA	4.29	SERVICIOS ADICIONALES - ÁREA NO PAGA
R-201	SERVICIOS ADICIONALES - ÁREA DE COMIDAS	31.30	SERVICIOS ADICIONALES - ÁREA NO PAGA
R-202	SERVICIOS ADICIONALES - ÁREA DE COMIDAS	31.45	SERVICIOS ADICIONALES - ÁREA NO PAGA
R-203	SERVICIOS ADICIONALES - ÁREA DE COMIDAS	31.08	SERVICIOS ADICIONALES - ÁREA NO PAGA
R-204	SERVICIOS ADICIONALES - ÁREA DE COMIDAS	29.75	SERVICIOS ADICIONALES - ÁREA NO PAGA
T-08-2	CENTRO DE TRANSFORMACIÓN ENEL-CODENSA (CT)_CUARTO BAJA TENSIÓN	11.75	ÁREA TÉCNICA
T-08-3	CENTRO DE TRANSFORMACIÓN ENEL-CODENSA (CT)_CUARTO MEDIA TENSIÓN	50.61	ÁREA TÉCNICA
T-21-2	ÁREA DE INSPECCIÓN	12.35	ÁREA TÉCNICA
T-21-4	ÁREA DE INSPECCIÓN	11.30	ÁREA TÉCNICA
T-21-5	ÁREA DE INSPECCIÓN	11.52	ÁREA TÉCNICA
T-25-1	NODO DE ACCESO DE TELECOMUNICACIONES	5.29	ÁREA TÉCNICA
		301.01	
ARQ_PL_01.2_ACCESO			
O-21-1	ALMACENAMIENTO DE LA ESTACIÓN	13.89	ÁREA OPERATIVA
T-00-1	CIRCULACIÓN TÉCNICA	36.69	ÁREA TÉCNICA
T-20-G	MEDIDORES (GAS)	4.80	ÁREA TÉCNICA
T-20-L-1	MEDIDORES (LUZ)	9.40	ÁREA TÉCNICA
T-20-W-1	MEDIDORES (AGUA)	14.72	ÁREA TÉCNICA
T-21-3	ÁREA DE INSPECCIÓN	5.96	ÁREA TÉCNICA
T-25-2	NODO DE ACCESO DE TELECOMUNICACIONES	5.05	ÁREA TÉCNICA
T-30	SISTEMA PROTECCIÓN CONTRA INCENDIO ENEL	7.22	ÁREA TÉCNICA
		97.72	
TOTAL NIVEL ACCESO		2857.42	

TABLA DE ÁREAS ÚTILES POR DEPARTAMENTO (NIVEL ACCESO)

DEPARTAMENTO	ÁREA (m²)
SERVICIOS ADICIONALES - ÁREA NO PAGA	310.59
ÁREA CULTURAL	4.00
ÁREA NO PAGA	347.34
ÁREA OPERATIVA	18.63
ÁREA PÚBLICA	1651.68
ÁREA TÉCNICA	525.18
TOTAL NIVEL ACCESO	2857.42

TABLA DE CICLO-PARQUEADEROS ESPECÍFICA

DESCRIPCIÓN	CANTIDAD (und)	USUARIOS
BICIPARQUEADERO ASISTIDO EN ACERO INOXIDABLE ASTM A240, a=0.70m X l=1.20m, h=1.70m.	1	EMPLEADOS
BICIPARQUEADERO DE COLGAR, 2 PUESTOS, a=1.20m X l=0.70m, h=2.40m. ACABADO EN PINTURA ELECTROSTÁTICA COLOR RAL9005 "NEGRO INTENSO".	4	EMPLEADOS
EMPLEADOS	5	
BICIPARQUEADERO ASISTIDO EN ACERO INOXIDABLE ASTM A240, a=0.70m X l=1.20m, h=1.70m.	124	VISITANTE
BICIPARQUEADERO DE COLGAR, 1 PUESTO, a=1.20m X l=0.70m, h=2.40m. ACABADO EN PINTURA ELECTROSTÁTICA COLOR RAL9005 "NEGRO INTENSO".	59	VISITANTE
BICIPARQUEADERO DE COLGAR, 2 PUESTOS, a=1.20m X l=0.70m, h=2.40m. ACABADO EN PINTURA ELECTROSTÁTICA COLOR RAL9005 "NEGRO INTENSO".	162	VISITANTE
BICIPARQUEADERO DE COLGAR DE 6 PUESTOS EN ACERO, a=1.20m X l=2.10m, h=2.40m. ACABADO EN PINTURA ELECTROSTÁTICA COLOR RAL9005 "NEGRO INTENSO".	900	VISITANTE
VISITANTE	1245	
TOTAL CUPOS	1250	

LOCALIZACIÓN

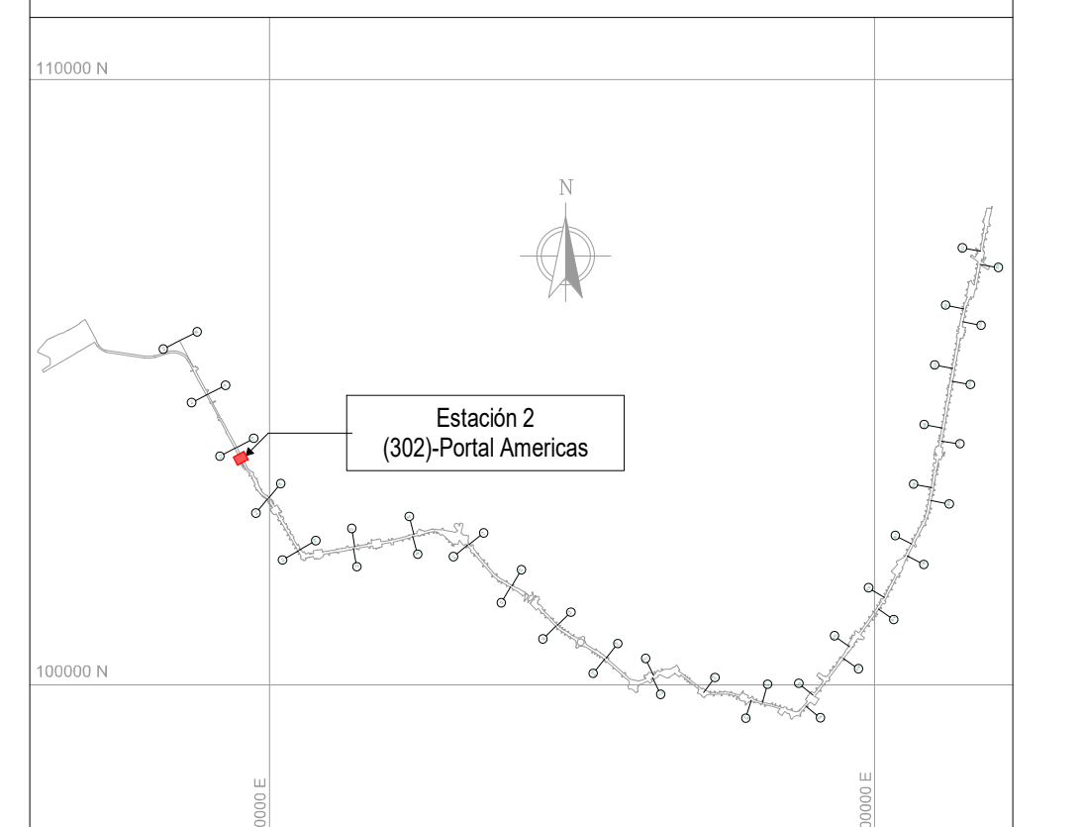

NOTAS

01 TODAS LAS DIMENSIONES ESTÁN CONFIGURADAS EN METROS A MENOS QUE SE INDIQUE UNA UNIDAD DE MEDIDA DIFERENTE.

02 TODAS LAS MEDIDAS, UBICACIÓN Y NIVELES DEBEN VERIFICARSE EN EL LUGAR DE CONSTRUCCIÓN.

03 EL NIVEL DE ACCESO AL EDIFICIO PL 01 CORRESPONDE AL +0,00 DE LA ESTACIÓN Y REFERENCIA AL NIVEL 2541.40 M.S.N.M.

04 LOS NOMBRES ESPECÍFICOS DE LAS ÁREAS PUEDEN SER CONSULTADAS EN EL PLANO NO. 3 Ó EN LAS VISTAS EN PLANTA.

05 LOS COLORES QUE SE MUESTRAN EN LOS PLANOS COMO PROYECCIÓN DE ELEMENTOS ARQUITECTÓNICOS COMO CUBIERTAS FACHADAS MUROS ETC. NO REPRESENTAN LA MATERIALIDAD Y REALIDAD DE ACABADOS DEL PROYECTO, SOLO SON INDICATIVOS PARA REALIZAR UNA CORRECTA LECTURA DE LA PLANIMETRÍA.

06 LAS ESCALERAS ELÉCTRICAS INDICAN SU SENTIDO CON LA SIGUIENTE NOMENCLATURA: “SUBE” Y “BAJA”.

07 SE DEBEN REVISAR LOS NIVELES ESTRUCTURALES PARA NIVEL DE ACCESO PL_01 Y SUBNIVELES, PL_02 (INTERMEDIO), PL_03 (PLATAFORMA) CON LA PLANIMETRIA DE PLACAS ESTRUCTURALES EN LOS ENTREGABLES L1T1-1200-302-CON-ED-EST-PL-0017, 18 Y L1T1-1300-402-CON-ED-EST-PL-0023, 26, 29, 66, 69, RESPECTIVAMENTE. EL NIVEL ESTRUCTURAL (NE) REFERENCIA LOS ESPACIOS DONDE SE DEBE ACONDICIONAR EL ACABADO DE PISO SEGÚN CORRESPONDA, CON LOS NIVELES DE PISO TERMINADO (NPT). LOS NIVELES PROYECTADOS DE EMPATE (NPE) EN LAS ÁREAS DE SERVICIOS ADICIONALES, REFERENCIAN LA ADECUACIÓN DE LOS DESNIVELES EN ESTAS ÁREAS; QUEDA COMO RESPONSABILIDAD DEL LOCATARIO DEFINIR Y ACONDICIONAR ESTE ACABADO DE PISO (NPE) EN LÍNEA CON EL NIVEL (NPT) DE ESPACIOS COLINDANTES. EL NIVEL ESTRUCTURAL (NE) SE ENCUENTRA A (- 0.10M) POR DEBAJO DE LOS NIVELES DE PISO TERMINADO (NPT) Y LOS NIVELES PROYECTADOS DE EMPATE (NPE) MARCADOS EN LA PLANIMETRÍA.

- ARQ_PL_00 = SÓTANO / NPT -5.40 m
- ARQ_PL_01 = ACCESO / NPT 0.00 m
- ARQ_PL_01.1 = ACCESO / NPT 0.10 m
- ARQ_PL_01.2 = ACCESO / NPT 0.60 m
- ARQ_PL_01.3 = ACCESO / NPT 0.75 m
- ARQ_PL_01.4 = ACCESO / NPT 1.06 m
- ARQ_PL_01.5 = ACCESO / NPT 1.15 m
- ARQ_PL_01.6 = ACCESO / NPT 1.33 m
- ARQ_PL_02 = INTERMEDIO / NPT 8.05 m
- ARQ_PL_02.1 = PLACA INFERIOR VIGA CAJÓN / NPT 14.27 m
- ARQ_PL_02.1' = CUBIERTA EDIFICACIONES / NPT 15.05 m
- ARQ_PL_02.2 = TOPE DE RIEL (TOR) / NPT 16.40 m
- ARQ_PL_03 = PLATAFORMA / NPT 17.54 m
- ARQ_PL_05 = CUBIERTA NAVE CENTRAL / NPT 26.94 m

CONVENCIONES

- - - -	LÍMITE DE INTERVENCIÓN
- - - -	HUELLA APÉNDICE TÉCNICO
▬	MURO DIVISORIO
— — —	PROYECCIÓN NIVEL SUPERIOR
🟩	SERVICIOS ADICIONALES - ÁREA NO PAGA
🟩	SERVICIOS ADICIONALES - ÁREA PAGA
🟩	SERVICIO PÚBLICO
🟦	ZONA DE REFUGIO
🟥	ÁREA CULTURAL
🟨	ÁREA NO PAGA
🟦	ÁREA OPERATIVA
🟧	ÁREA PAGA
🟦	ÁREA PÚBLICA
⬜	ÁREA TÉCNICA

No.	PLANOS DE REFERENCIA	REV.

No.	MODELO BIM DE REFERENCIA	REV.
1	L1T1-1100-202-CON-ED-EST-MO-0001.rvt	V00
2	L1T1-1100-203-CON-ED-EST-MO-0001.rvt	V00
3	L1T1-1100-302-CON-ED-EST-MO-0001.rvt	V00
4	L1T1-1150-202-CON-ED-EST-MO-0001.rvt	V00
5	L1T1-1150-203-CON-ED-EST-MO-0001.rvt	V00
6	L1T1-1150-302-CON-ED-EST-MO-0001.rvt	V00
7	L1T1-1200-302-CON-ED-CIV-MO-0001.rvt	V00
8	L1T1-1300-402-CON-ED-EST-MO-0001.rvt	V00
9	L1T1-1300-402-CON-ED-EST-MO-0002.rvt	V00
10	L1T1-1310-402-CON-ED-EST-MO-0001.rvt	V00
11	L1T1-1410-302-CON-ED-MEC-MO-0001.rvt	V00
12	L1T1-1420-302-CON-ED-MEC-MO-0001.rvt	V00
13	L1T1-5160-302-CON-ED-EST-MO-0001.rvt	V00
14	L1T1-5160-302-CON-ED-ARQ-MO-0001.rvt	V00
15	L1T1-5300-302-CON-ED-MEC-MO-0001.rvt	V00
16	L1T1-5600-302-CON-ED-INS-MO-0001.rvt	V00
17	L1T1-1270-302-CON-ED-ARQ-MO-0011.rvt	V00
18	L1T1-1330-402-CON-ED-ARQ-MO-0011.rvt	V00
19	L1T1-1330-402-CON-ED-ARQ-MO-0012.rvt	V00

No.	PAQUETE DE TRABAJO DE REFERENCIA	REV.
1	XREF-URBANISM_CONTEXT_ST02.RVT	

0 2 10m
1:200

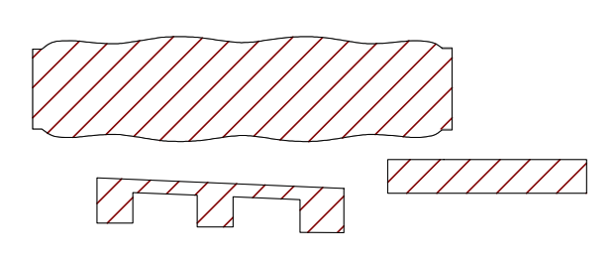

PLANO CLAVE ESTACIÓN 2

VÁLIDO PARA CONSTRUCCIÓN
01-03-26

METRO BOGOTÁ
GCS Consorcio Consultores PMO Bogotá
CONSORCIO SUPERVISOR PLMB
CHEC

DISEÑÓ:
REN ZHENHUA
Licencia de Arq.nivel I (China): 1101735-614

REVISÓ:
CARLOS MAURICIO BARRETO BARBOSA
Mat.: A4012012-14139353

APROBÓ:
DIEGO ERNESTO DUEÑAS
Mat.: 25202-53876 CND

DIBUJÓ:
EQUIPO CHEC

REVISIÓN No.	FECHA	DESCRIPCIÓN	REVISÓ	APROBÓ	APROBACIÓN CLIENTE
V01	01/03/2026	EMITIDO PARA CONSTRUCCIÓN	C.M.B.B	D.E.D	
V00	27/11/2024	REVISIÓN NO OBJETADA - EMITIDO PARA CONSTRUCCIÓN	F.B.R	E.O.M	
VGG	23/05/2024	EMITIDO PARA REVISIÓN Y COMENTARIOS DEL CLIENTE E INTERVENTORÍA - INCLUYE COMENTARIOS /(AJUSTES V4)	F.B.R	E.O.M	
VFF	11/12/2023	EMITIDO PARA REVISIÓN Y COMENTARIOS DEL CLIENTE E INTERVENTORÍA - INCLUYE COMENTARIOS /(AJUSTES V3)	F.B.R	M.B.M	
VEE	30/06/2023	EMITIDO PARA REVISIÓN Y COMENTARIOS DEL CLIENTE E INTERVENTORÍA - INCLUYE COMENTARIOS /(AJUSTES V2)	J.E.M	M.B.M	
VDD	18/12/2022	EMITIDO PARA REVISIÓN Y COMENTARIOS DEL CLIENTE E INTERVENTORÍA - INCLUYE COMENTARIOS /(AJUSTES)	J.E.M	M.B.M	
VCC	02/06/2022	EMITIDO PARA REVISIÓN Y COMENTARIOS DEL CLIENTE E INTERVENTORÍA - INCLUYE COMENTARIOS /(ENTREGA 90%)	J.E.M	M.B.M	
VBB	06/12/2021	EMITIDO PARA REVISIÓN Y COMENTARIOS DEL CLIENTE E INTERVENTORÍA	J.E.M	M.B.M	
VA0	30/06/2021	EMITIDO PARA COMENTARIOS INTERNOS - EMISIÓN PRELIMINAR PARA COMENTARIOS	J.E.M	M.B.M	

METRO LÍNEA 1

METRO LÍNEA 1
CONTRATO DE CONCESIÓN No. 163 DE 2019

PROYECTO PRIMERA LÍNEA DEL METRO DE BOGOTÁ - TRAMO 1

DIRECTOR DE INTERVENTORÍA:
JAVIER DESCARGA N.
Mat.:25202-68697 CND

ESPECIALISTA INTERVENTORÍA:
CARLOS ALBERTO HOYOS SOTO
Mat.:A25072000-14251682

FECHA:
MARZO 2026

INFRAESTRUCTURA VIAL

ARQUITECTURA

ESTACIÓN METRO 2 (PORTAL AMÉRICAS)
GENERAL
VISTA EN PLANTA Y 3D - NIVEL ACCESO

PLANCHA No: L1T1-0000-302-CON-ED-ARQ-PL-0001_05_V01
ARCHIVO: L1T1-0000-302-CON-ED-ARQ-MO-0001_V00.rvt
ESCALA: INDICADA
FECHA: JUNIO 2021
REVISIÓN No. V01
PLANO No. 05 DE 85