L1T1-CON-CAL-FR-0120 - B1 : 1000x707mm

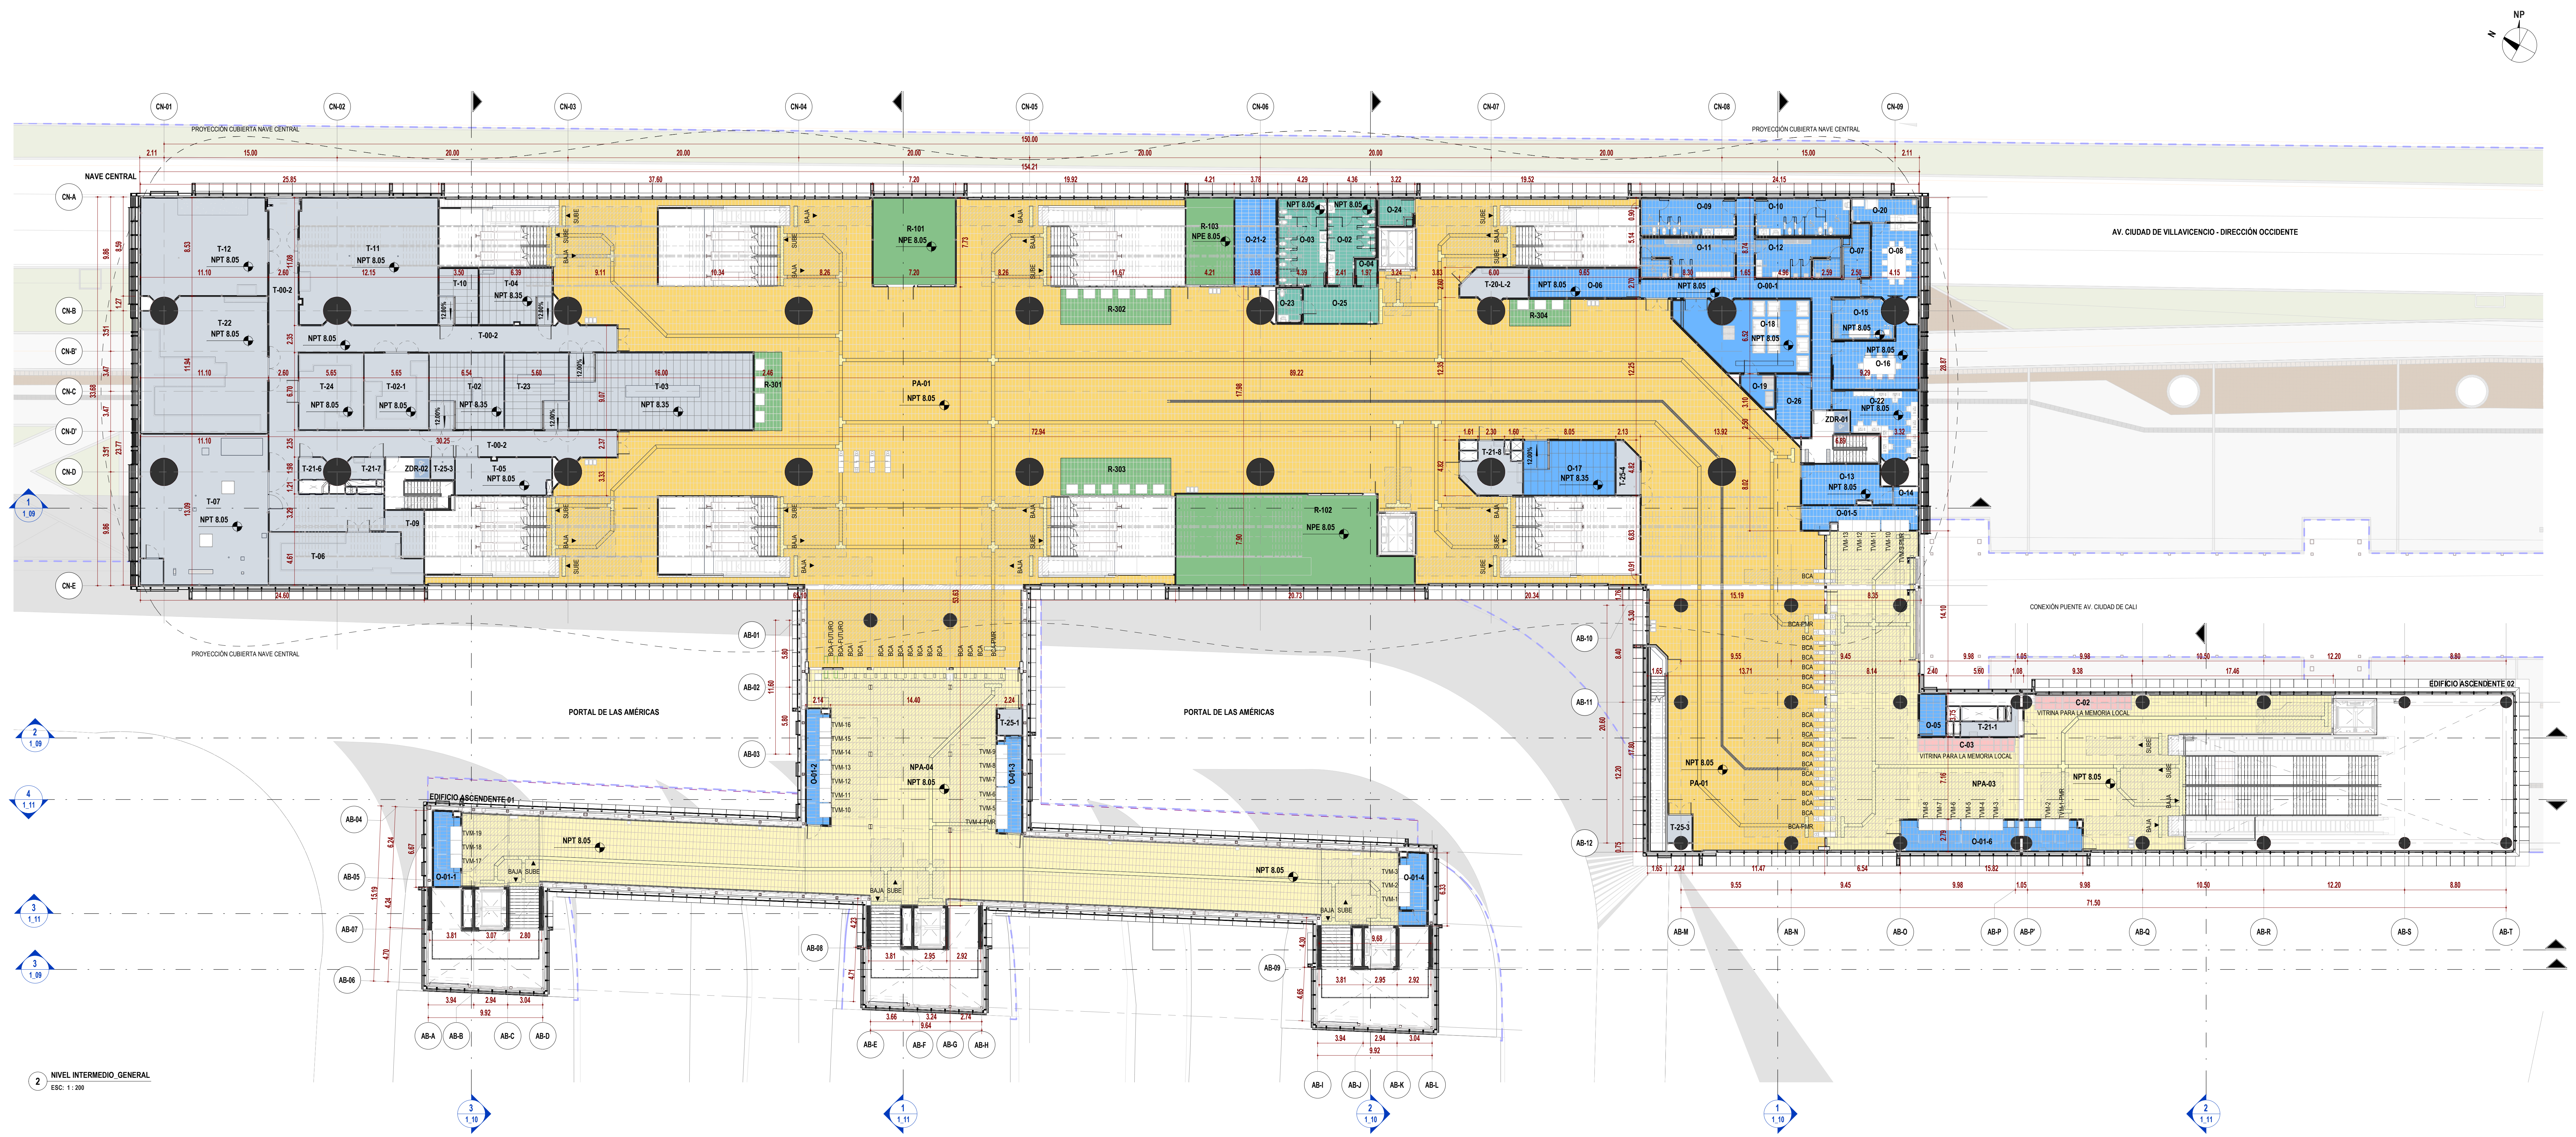

2 NIVEL INTERMEDIO_GENERAL
ESC: 1 : 200

TABLA DE ÁREAS ÚTILES (NIVEL INTERMEDIO)			
CÓDIGO	**NOMBRE**	**ÁREA (m²)**	**DEPARTAMENTO**
EDIFICIO ASCENDENTE 01			
ARQ_PL_02_INTERMEDIO			
NPA-04	ÁREA NO PAGA	715.65	ÁREA NO PAGA
O-00-1	CIRCULACIÓN ÁREAS OPERATIVAS	3.00	ÁREA OPERATIVA
O-01-1	VENTA AUTOMÁTICA DE BOLETOS	14.84	ÁREA OPERATIVA
O-01-2	VENTA AUTOMÁTICA DE BOLETOS	19.59	ÁREA OPERATIVA
O-01-3	VENTA AUTOMÁTICA DE BOLETOS	17.25	ÁREA OPERATIVA
O-01-4	VENTA AUTOMÁTICA DE BOLETOS	11.20	ÁREA OPERATIVA
T-25-1	NODO DE ACCESO DE TELECOMUNICACIONES	4.62	ÁREA TÉCNICA
		786.15	
EDIFICIO ASCENDENTE 02			
ARQ_PL_02_INTERMEDIO			
C-02	ÁREAS DE USO CULTURAL	10.63	ÁREA CULTURAL
C-03	ÁREAS DE USO CULTURAL	10.54	ÁREA CULTURAL
NPA-03	ÁREA NO PAGA	427.50	ÁREA NO PAGA
O-01-6	VENTA AUTOMÁTICA DE BOLETOS	38.81	ÁREA OPERATIVA
O-05	LOCAL DE INFORMACIÓN	8.23	ÁREA OPERATIVA
T-21-1	ÁREA DE INSPECCIÓN	7.67	ÁREA TÉCNICA
T-25-3	NODO DE ACCESO DE TELECOMUNICACIONES	4.41	ÁREA TÉCNICA
		507.78	
NAVE CENTRAL			
ARQ_PL_02_INTERMEDIO			
O-00-1	CIRCULACIÓN ÁREAS OPERATIVAS	56.69	ÁREA OPERATIVA
O-01-5	VENTA AUTOMÁTICA DE BOLETOS	20.64	ÁREA OPERATIVA
O-02	BAÑOS PÚBLICOS DE HOMBRES	26.50	SERVICIO PÚBLICO
O-03	BAÑOS PÚBLICOS DE MUJERES	31.07	SERVICIO PÚBLICO
O-04	CONTROL DE ACCESO BAÑOS PÚBLICOS	4.00	SERVICIO PÚBLICO

TABLA DE ÁREAS ÚTILES (NIVEL INTERMEDIO)			
CÓDIGO	**NOMBRE**	**ÁREA (m²)**	**DEPARTAMENTO**
O-06	OFICINA DEL SUPERVISOR DE LA ESTACIÓN	23.45	ÁREA OPERATIVA
O-07	CUARTO DE LIMPIEZA	10.18	ÁREA OPERATIVA
O-08	SALA DE DESCANSO PARA EMPLEADOS	27.27	ÁREA OPERATIVA
O-09	BAÑOS EMPLEADOS HOMBRES	25.97	ÁREA OPERATIVA
O-10	BAÑOS EMPLEADOS MUJERES	26.03	ÁREA OPERATIVA
O-11	VESTIDORES EMPLEADOS HOMBRES	27.59	ÁREA OPERATIVA
O-12	VESTIDORES EMPLEADOS MUJERES	25.01	ÁREA OPERATIVA
O-13	LOCAL DE POLICÍA	24.60	ÁREA OPERATIVA
O-14	CALABOZO	3.22	ÁREA OPERATIVA
O-15	LOCAL PRIMEROS AUXILIOS	16.99	ÁREA OPERATIVA
O-16	SALA DE REUNIONES	33.76	ÁREA OPERATIVA
O-17	OPERADORES TELECOMUNICACIONES EXTERIORES	36.53	ÁREA OPERATIVA
O-18	CUARTO DE ALMACENAMIENTO DE RESIDUOS SÓLIDOS	60.24	ÁREA OPERATIVA
O-19	CUARTO DE ALMACENAMIENTO DE RESIDUOS PELIGROSOS	6.75	ÁREA OPERATIVA
O-20	SALA DE LACTANCIA	11.90	ÁREA OPERATIVA
O-21-2	ALMACENAMIENTO DE LA ESTACIÓN	26.94	ÁREA OPERATIVA
O-22	OFICINA DE MANTENIMIENTO	31.10	ÁREA OPERATIVA
O-23	BAÑO PÚBLICO - FAMILIAR	6.22	SERVICIO PÚBLICO
O-24	CUARTO DE LIMPIEZA DE BAÑOS PÚBLICOS	7.14	SERVICIO PÚBLICO
O-25	BAÑO PÚBLICO - CORREDOR OPERACIONAL	20.42	SERVICIO PÚBLICO
O-26	ALMACENAMIENTO DE BASURAS METRO	15.54	ÁREA OPERATIVA
PA-01	ÁREA PAGA	2188.23	ÁREA PAGA
R-101	SERVICIOS ADICIONALES - ÁREA DE SERVICIO	52.70	SERVICIOS ADICIONALES - ÁREA PAGA
R-102	SERVICIOS ADICIONALES - ÁREA DE SERVICIO	142.40	SERVICIOS ADICIONALES - ÁREA PAGA
R-103	SERVICIOS ADICIONALES - ÁREA DE SERVICIO	30.65	SERVICIOS ADICIONALES - ÁREA PAGA
R-301	SERVICIOS ADICIONALES - MÁQUINAS EXPENDEDORAS/CAJEROS AUTOMÁTICOS	16.32	SERVICIOS ADICIONALES - ÁREA PAGA
R-302	SERVICIOS ADICIONALES - MÁQUINAS EXPENDEDORAS/CAJEROS AUTOMÁTICOS	29.34	SERVICIOS ADICIONALES - ÁREA PAGA

TABLA DE ÁREAS ÚTILES (NIVEL INTERMEDIO)			
CÓDIGO	**NOMBRE**	**ÁREA (m²)**	**DEPARTAMENTO**
R-303	SERVICIOS ADICIONALES - MÁQUINAS EXPENDEDORAS/CAJEROS AUTOMÁTICOS	30.75	SERVICIOS ADICIONALES - ÁREA PAGA
R-304	SERVICIOS ADICIONALES - MÁQUINAS EXPENDEDORAS/CAJEROS AUTOMÁTICOS	9.23	SERVICIOS ADICIONALES - ÁREA PAGA
T-00-2	CIRCULACIÓN TÉCNICA	221.75	ÁREA TÉCNICA
T-02	LOCAL DE CONDUCCIÓN AUTOMÁTICA (CBTC)	42.06	ÁREA TÉCNICA
T-02-1	UPS DEDICADA (CBTC)	36.27	ÁREA TÉCNICA
T-03	TELECOMUNICACIONES ESTACIÓN - CORRIENTE DÉBIL	106.06	ÁREA TÉCNICA
T-04	EQUIPO BOLETERÍA	29.72	ÁREA TÉCNICA
T-05	ALMACÉN PARA MANTENIMIENTO	25.93	ÁREA TÉCNICA
T-06	SALA DE TABLEROS	55.24	ÁREA TÉCNICA
T-07	CENTRO DE TRANSFORMACIÓN (CT)	137.35	ÁREA TÉCNICA
T-09	ALMACÉN EQUIPO ELÉCTRICO	10.31	ÁREA TÉCNICA
T-10	CUARTO DE EQUIPO ELECTROMECÁNICO	15.73	ÁREA TÉCNICA
T-11	CUARTO DE VENTILACIÓN	125.47	ÁREA TÉCNICA
T-12	PLANTA DE REFRIGERACIÓN PARA LA CLIMATIZACIÓN	92.52	ÁREA TÉCNICA
T-20-L-2	MEDIDORES (LUZ)	13.84	ÁREA TÉCNICA
T-21-6	ÁREA DE INSPECCIÓN	4.08	ÁREA TÉCNICA
T-21-7	ÁREA DE INSPECCIÓN	5.48	ÁREA TÉCNICA
T-21-8	ÁREA DE INSPECCIÓN	14.13	ÁREA TÉCNICA
T-22	CUARTO DE UPS	122.98	ÁREA TÉCNICA
T-23	CUARTO PDAP	35.87	ÁREA TÉCNICA
T-24	TETRA UPS	36.36	ÁREA TÉCNICA
T-25-3	NODO DE ACCESO DE TELECOMUNICACIONES	3.77	ÁREA TÉCNICA
T-25-4	NODO DE ACCESO DE TELECOMUNICACIONES	8.30	ÁREA TÉCNICA
ZDR-01	ZONA DE REFUGIO (PMR)	2.58	ZONA DE REFUGIO
ZDR-02	ZONA DE REFUGIO (PMR)	2.50	ZONA DE REFUGIO
		4253.68	
TOTAL NIVEL INTERMEDIO		5547.62	

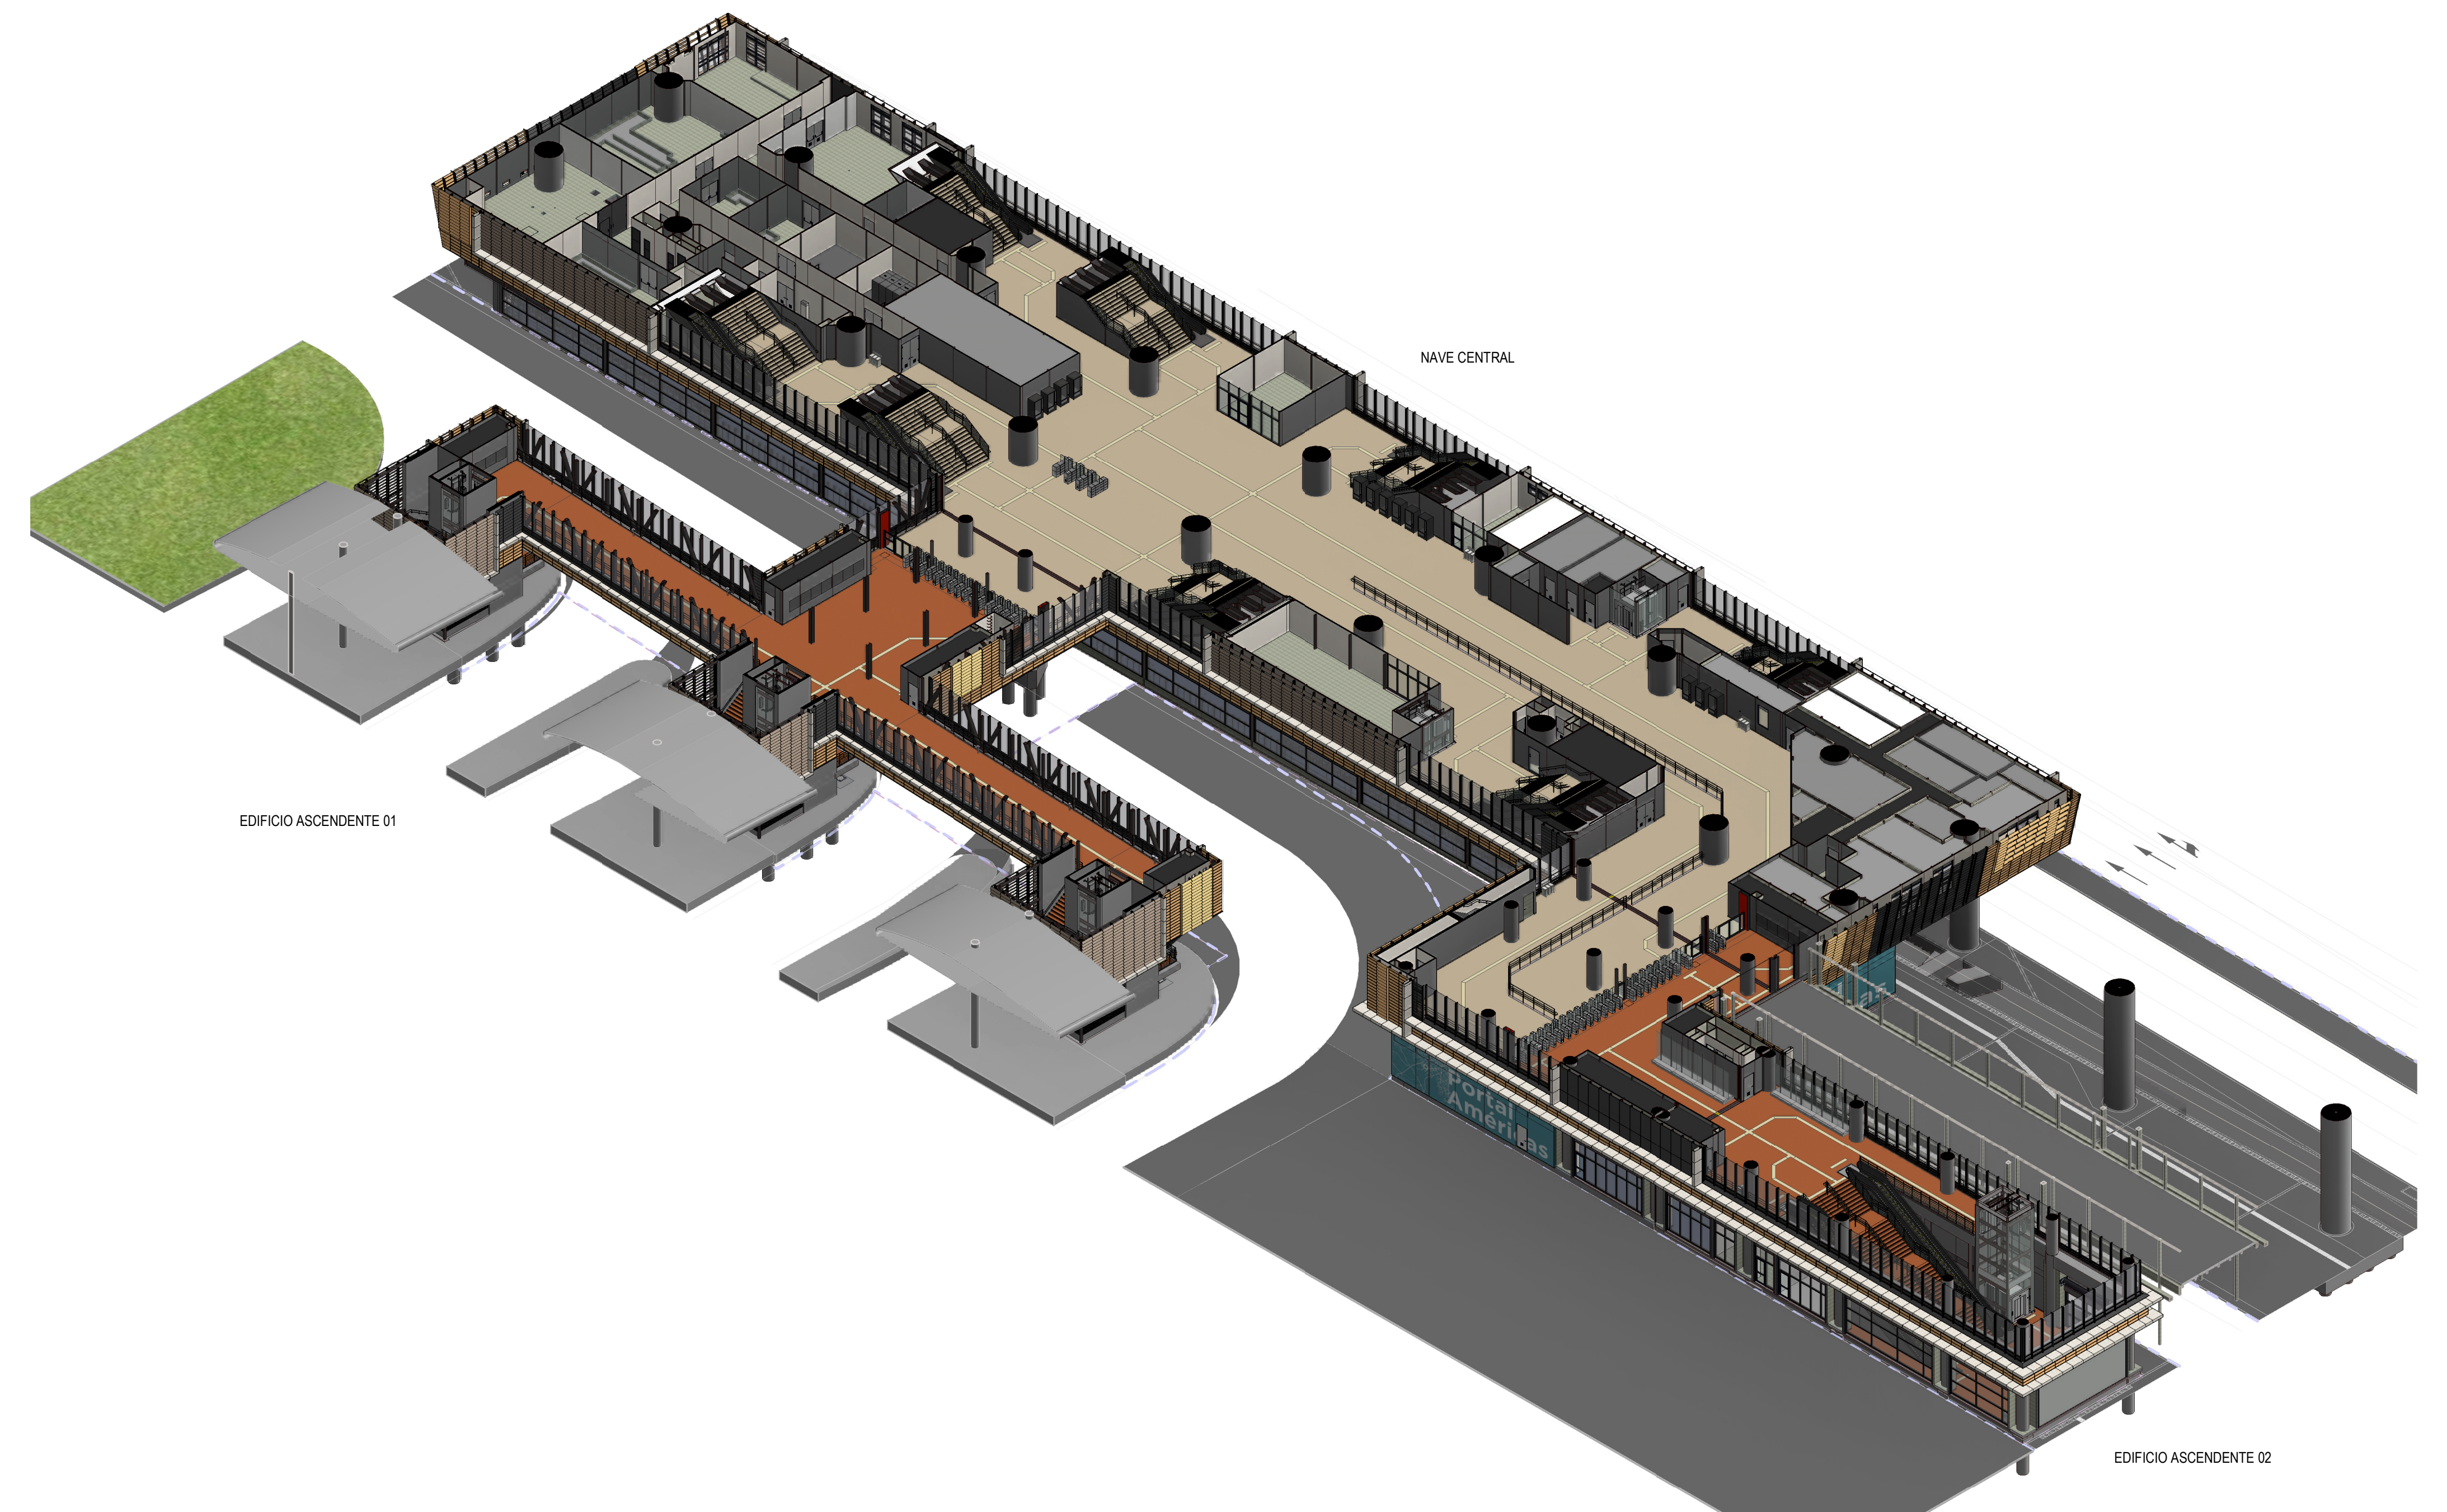

1 3D_NIVEL INTERMEDIO_GENERAL
ESC: N/A

TABLA DE ÁREAS ÚTILES POR DEPARTAMENTO (NIVEL INTERMEDIO)	
DEPARTAMENTO	**ÁREA (m²)**
SERVICIO PÚBLICO	95.35
SERVICIOS ADICIONALES - ÁREA PAGA	311.40
ZONA DE REFUGIO	5.08
ÁREA CULTURAL	21.17
ÁREA NO PAGA	1143.15
ÁREA OPERATIVA	623.32
ÁREA PAGA	2188.23
ÁREA TÉCNICA	1159.92
TOTAL NIVEL INTERMEDIO	5547.62

LOCALIZACIÓN

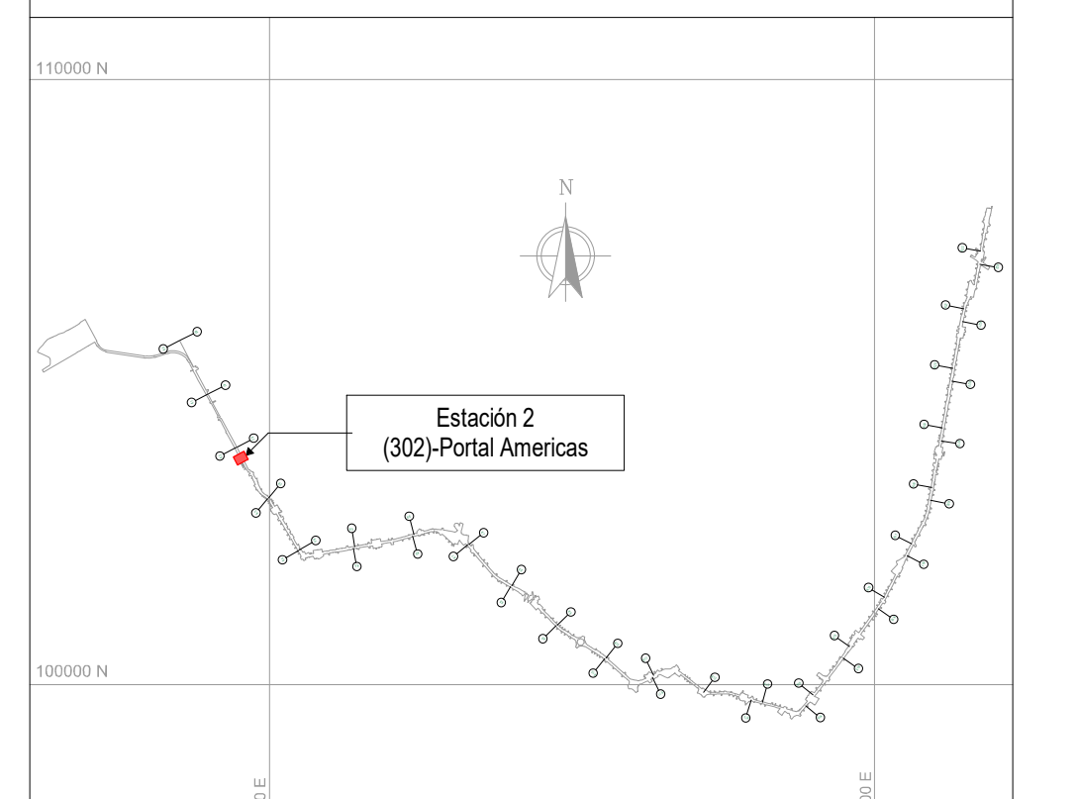

NOTAS

01 TODAS LAS DIMENSIONES ESTÁN CONFIGURADAS EN METROS A MENOS QUE SE INDIQUE UNA UNIDAD DE MEDIDA DIFERENTE.

02 TODAS LAS MEDIDAS, UBICACIÓN Y NIVELES DEBEN VERIFICARSE EN EL LUGAR DE CONSTRUCCIÓN.

03 EL NIVEL DE ACCESO AL EDIFICIO PL 01 CORRESPONDE AL +0,00 DE LA ESTACIÓN Y REFERENCIA AL NIVEL 2541.40 M.S.N.M.

04 LOS NOMBRES ESPECÍFICOS DE LAS ÁREAS PUEDEN SER CONSULTADAS EN EL PLANO NO. 3 Ó EN LAS VISTAS EN PLANTA.

05 LOS COLORES QUE SE MUESTRAN EN LOS PLANOS COMO PROYECCIÓN DE ELEMENTOS ARQUITECTÓNICOS COMO CUBIERTAS FACHADAS MUROS ETC. NO REPRESENTAN LA MATERIALIDAD Y REALIDAD DE ACABADOS DEL PROYECTO, SOLO SON INDICATIVOS PARA REALIZAR UNA CORRECTA LECTURA DE LA PLANIMETRÍA.

06 LAS ESCALERAS ELÉCTRICAS INDICAN SU SENTIDO CON LA SIGUIENTE NOMENCLATURA: "SUBE" Y "BAJA".

07 SE DEBEN REVISAR LOS NIVELES ESTRUCTURALES PARA NIVEL DE ACCESO PL_01 Y SUBNIVELES, PL_02 (INTERMEDIO), PL_03 (PLATAFORMA) CON LA PLANIMETRIA DE PLACAS ESTRUCTURALES EN LOS ENTREGABLES L1T1-1200-302-CON-ED-EST-PL-0017, 18 Y L1T1-1300-402-CON-ED-EST-PL-0023, 26, 29, 66, 69, RESPECTIVAMENTE. EL NIVEL ESTRUCTURAL (NE) REFERENCIA LOS ESPACIOS DONDE SE DEBE ACONDICIONAR EL ACABADO DE PISO SEGÚN CORRESPONDA, CON LOS NIVELES DE PISO TERMINADO (NPT). LOS NIVELES PROYECTADOS DE EMPATE (NPE) EN LAS ÁREAS DE SERVICIOS ADICIONALES, REFERENCIAN LA ADECUACIÓN DE LOS DESNIVELES EN ESTAS ÁREAS; QUEDA COMO RESPONSABILIDAD DEL LOCATARIO DEFINIR Y ACONDICIONAR ESTE ACABADO DE PISO (NPE) EN LÍNEA CON EL NIVEL (NPT) DE ESPACIOS COLINDANTES. EL NIVEL ESTRUCTURAL (NE) SE ENCUENTRA A (- 0.10M) POR DEBAJO DE LOS NIVELES DE PISO TERMINADO (NPT) Y LOS NIVELES PROYECTADOS DE EMPATE (NPE) MARCADOS EN LA PLANIMETRÍA.

- ARQ_PL_00 = SÓTANO	/ NPT -5.40 m
- ARQ_PL_01 = ACCESO	/ NPT 0.00 m
- ARQ_PL_01.1 = ACCESO	/ NPT 0.10 m
- ARQ_PL_01.2 = ACCESO	/ NPT 0.60 m
- ARQ_PL_01.3 = ACCESO	/ NPT 0.75 m
- ARQ_PL_01.4 = ACCESO	/ NPT 1.06 m
- ARQ_PL_01.5 = ACCESO	/ NPT 1.15 m
- ARQ_PL_01.6 = ACCESO	/ NPT 1.33 m
- ARQ_PL_02 = INTERMEDIO	/ NPT 8.05 m
- ARQ_PL_02.1 = PLACA INFERIOR VIGA CAJÓN	/ NPT 14.27 m
- ARQ_PL_02.1' = CUBIERTA EDIFICACIONES	/ NPT 15.05 m
- ARQ_PL_02.2 = TOPE DE RIEL (TOR)	/ NPT 16.40 m
- ARQ_PL_03 = PLATAFORMA	/ NPT 17.54 m
- ARQ_PL_05 = CUBIERTA NAVE CENTRAL	/ NPT 26.94 m

CONVENCIONES

- - - -	LÍMITE DE INTERVENCIÓN
- - - -	HUELLA APÉNDICE TÉCNICO
▬	MURO DIVISORIO
— — —	PROYECCIÓN NIVEL SUPERIOR
🟩	SERVICIOS ADICIONALES - ÁREA NO PAGA
🟩	SERVICIOS ADICIONALES - ÁREA PAGA
🟩	SERVICIO PÚBLICO
🟦	ZONA DE REFUGIO
🟥	ÁREA CULTURAL
🟨	ÁREA NO PAGA
🟦	ÁREA OPERATIVA
🟧	ÁREA PAGA
🟦	ÁREA PÚBLICA
⬜	ÁREA TÉCNICA

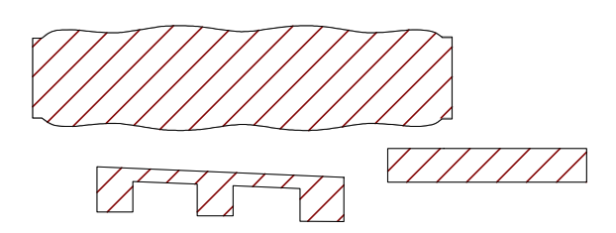

PLANO CLAVE ESTACIÓN 2

VÁLIDO PARA CONSTRUCCIÓN
01-03-26

No.	PLANOS DE REFERENCIA	REV.

No.	MODELO BIM DE REFERENCIA	REV.
1	L1T1-1100-202-CON-ED-EST-MO-0001.rvt	V00
2	L1T1-1100-203-CON-ED-EST-MO-0001.rvt	V00
3	L1T1-1100-302-CON-ED-EST-MO-0001.rvt	V00
4	L1T1-1150-202-CON-ED-EST-MO-0001.rvt	V00
5	L1T1-1150-203-CON-ED-EST-MO-0001.rvt	V00
6	L1T1-1150-302-CON-ED-EST-MO-0001.rvt	V00
7	L1T1-1200-302-CON-ED-CIV-MO-0001.rvt	V00
8	L1T1-1300-402-CON-ED-EST-MO-0001.rvt	V00
9	L1T1-1300-402-CON-ED-EST-MO-0002.rvt	V00
10	L1T1-1310-402-CON-ED-EST-MO-0001.rvt	V00
11	L1T1-1410-302-CON-ED-MEC-MO-0001.rvt	V00
12	L1T1-1420-302-CON-ED-MEC-MO-0001.rvt	V00
13	L1T1-5160-302-CON-ED-EST-MO-0001.rvt	V00
14	L1T1-5160-302-CON-ED-ARQ-MO-0001.rvt	V00
15	L1T1-5300-302-CON-ED-MEC-MO-0001.rvt	V00
16	L1T1-5600-302-CON-ED-INS-MO-0001.rvt	V00
17	L1T1-1270-302-CON-ED-ARQ-MO-0011.rvt	V00
18	L1T1-1330-402-CON-ED-ARQ-MO-0011.rvt	V00
19	L1T1-1330-402-CON-ED-ARQ-MO-0012.rvt	V00

No.	PAQUETE DE TRABAJO DE REFERENCIA	REV.
1	XREF-URBANISM_CONTEXT_ST02.RVT	

0 2 10m
1:200

METRO BOGOTÁ
Consorcio Consultores PMO Bogotá
CONSORCIO SUPERVISOR PLMB

DISEÑÓ:
REN ZHENHUA
Licencia de Arq.nivel I (China): 1101735-614

APROBÓ:
DIEGO ERNESTO DUEÑAS
Mat.: 25202-53876 CND

REVISÓ:
CARLOS MAURICIO BARRETO BARBOSA
Mat.: A4012012-14139353

DIBUJÓ:
EQUIPO CHEC

REVISIÓN No.	FECHA	DESCRIPCIÓN	REVISÓ	APROBÓ	APROBACIÓN CLIENTE
V01	01/03/2026	EMITIDO PARA CONSTRUCCIÓN	C.M.B.B	D.E.D	
V00	27/11/2024	REVISIÓN NO OBJETADA - EMITIDO PARA CONSTRUCCIÓN	F.B.R	E.O.M	
VGG	23/05/2024	EMITIDO PARA REVISIÓN Y COMENTARIOS DEL CLIENTE E INTERVENTORÍA - INCLUYE COMENTARIOS /(AJUSTES V4)	F.B.R	E.O.M	
VFF	11/12/2023	EMITIDO PARA REVISIÓN Y COMENTARIOS DEL CLIENTE E INTERVENTORÍA - INCLUYE COMENTARIOS /(AJUSTES V3)	F.B.R	M.B.M	
VEE	30/06/2023	EMITIDO PARA REVISIÓN Y COMENTARIOS DEL CLIENTE E INTERVENTORÍA - INCLUYE COMENTARIOS /(AJUSTES V2)	J.E.M	M.B.M	
VDD	18/12/2022	EMITIDO PARA REVISIÓN Y COMENTARIOS DEL CLIENTE E INTERVENTORÍA - INCLUYE COMENTARIOS /(AJUSTES)	J.E.M	M.B.M	
VCC	02/06/2022	EMITIDO PARA REVISIÓN Y COMENTARIOS DEL CLIENTE E INTERVENTORÍA - INCLUYE COMENTARIOS /(ENTREGA 90%)	J.E.M	M.B.M	
VBB	06/12/2021	EMITIDO PARA REVISIÓN Y COMENTARIOS DEL CLIENTE E INTERVENTORÍA	J.E.M	M.B.M	
VA0	30/06/2021	EMITIDO PARA COMENTARIOS INTERNOS - EMISIÓN PRELIMINAR PARA COMENTARIOS	J.E.M	M.B.M	

METRO LÍNEA 1

METRO LÍNEA 1
CONTRATO DE CONCESIÓN No. 163 DE 2019

PROYECTO PRIMERA LÍNEA DEL METRO DE BOGOTÁ - TRAMO 1

DIRECTOR DE INTERVENTORÍA:
JAVIER DESCARGA N.
Mat.:25202-68697 CND

ESPECIALISTA INTERVENTORÍA:
CARLOS ALBERTO HOYOS SOTO
Mat.:A25072000-14251682

FECHA:
MARZO 2026

INFRAESTRUCTURA VIAL

ARQUITECTURA

ESTACIÓN METRO 2 (PORTAL AMÉRICAS)
GENERAL
VISTA EN PLANTA Y 3D - NIVEL INTERMEDIO

PLANCHA No: L1T1-0000-302-CON-ED-ARQ-PL-0001_06_V01
ARCHIVO: L1T1-0000-302-CON-ED-ARQ-MO-0001_V00.rvt
ESCALA: INDICADA
FECHA: JUNIO 2021
REVISIÓN No. V01
PLANO No. 06 DE 85