L1T1-CON-CAL-FR-0120 - B1 : 1000x707mm

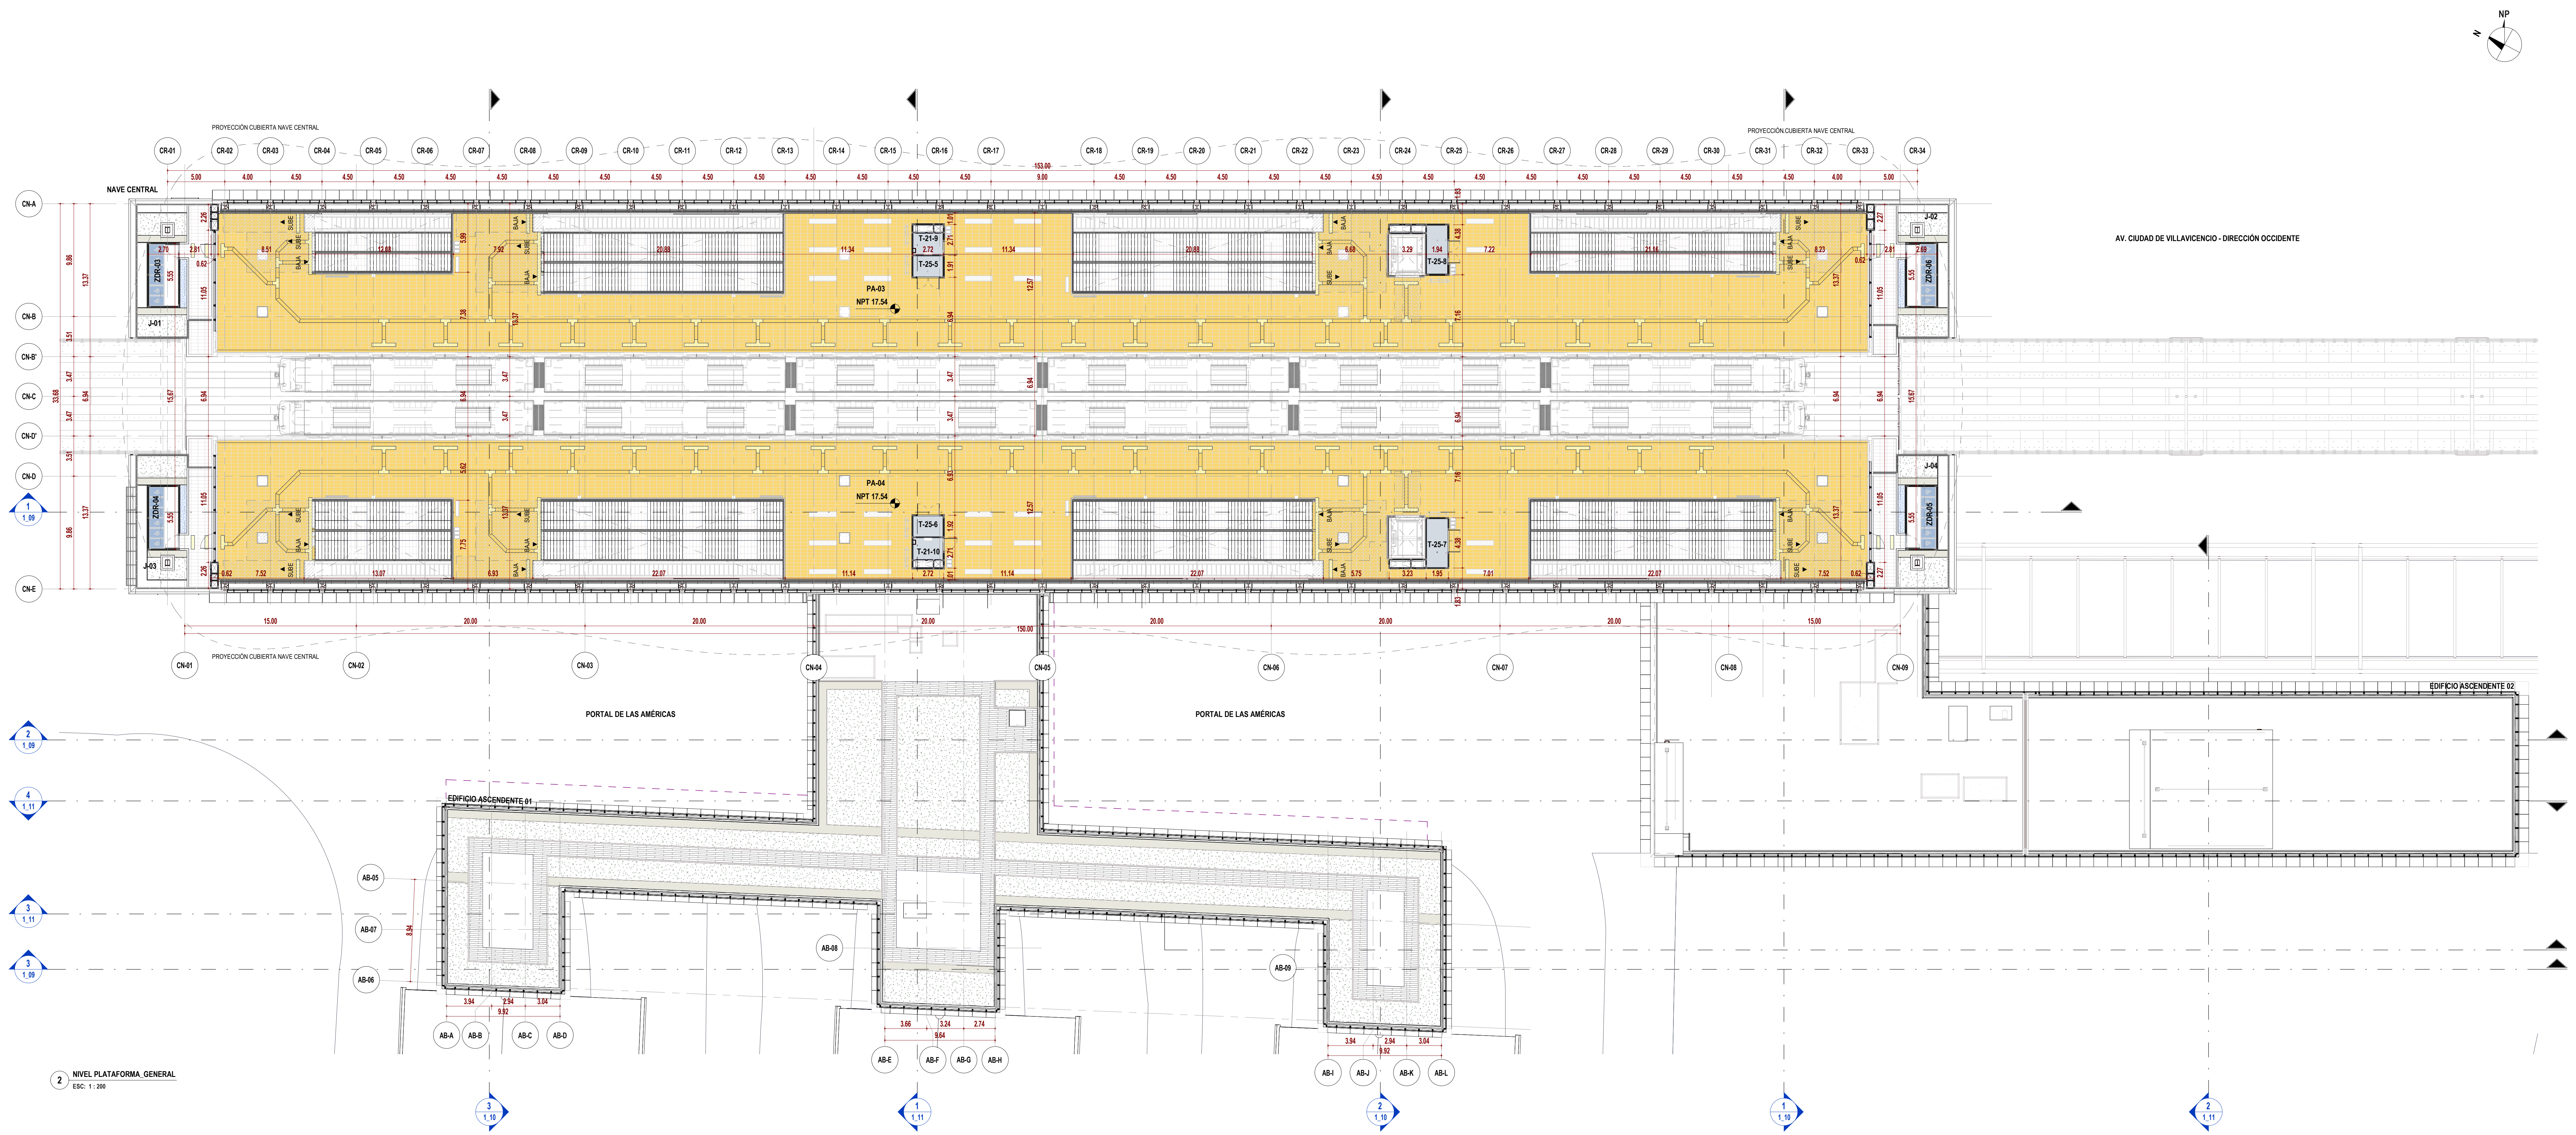

2 NIVEL PLATAFORMA_GENERAL
ESC: 1 : 200

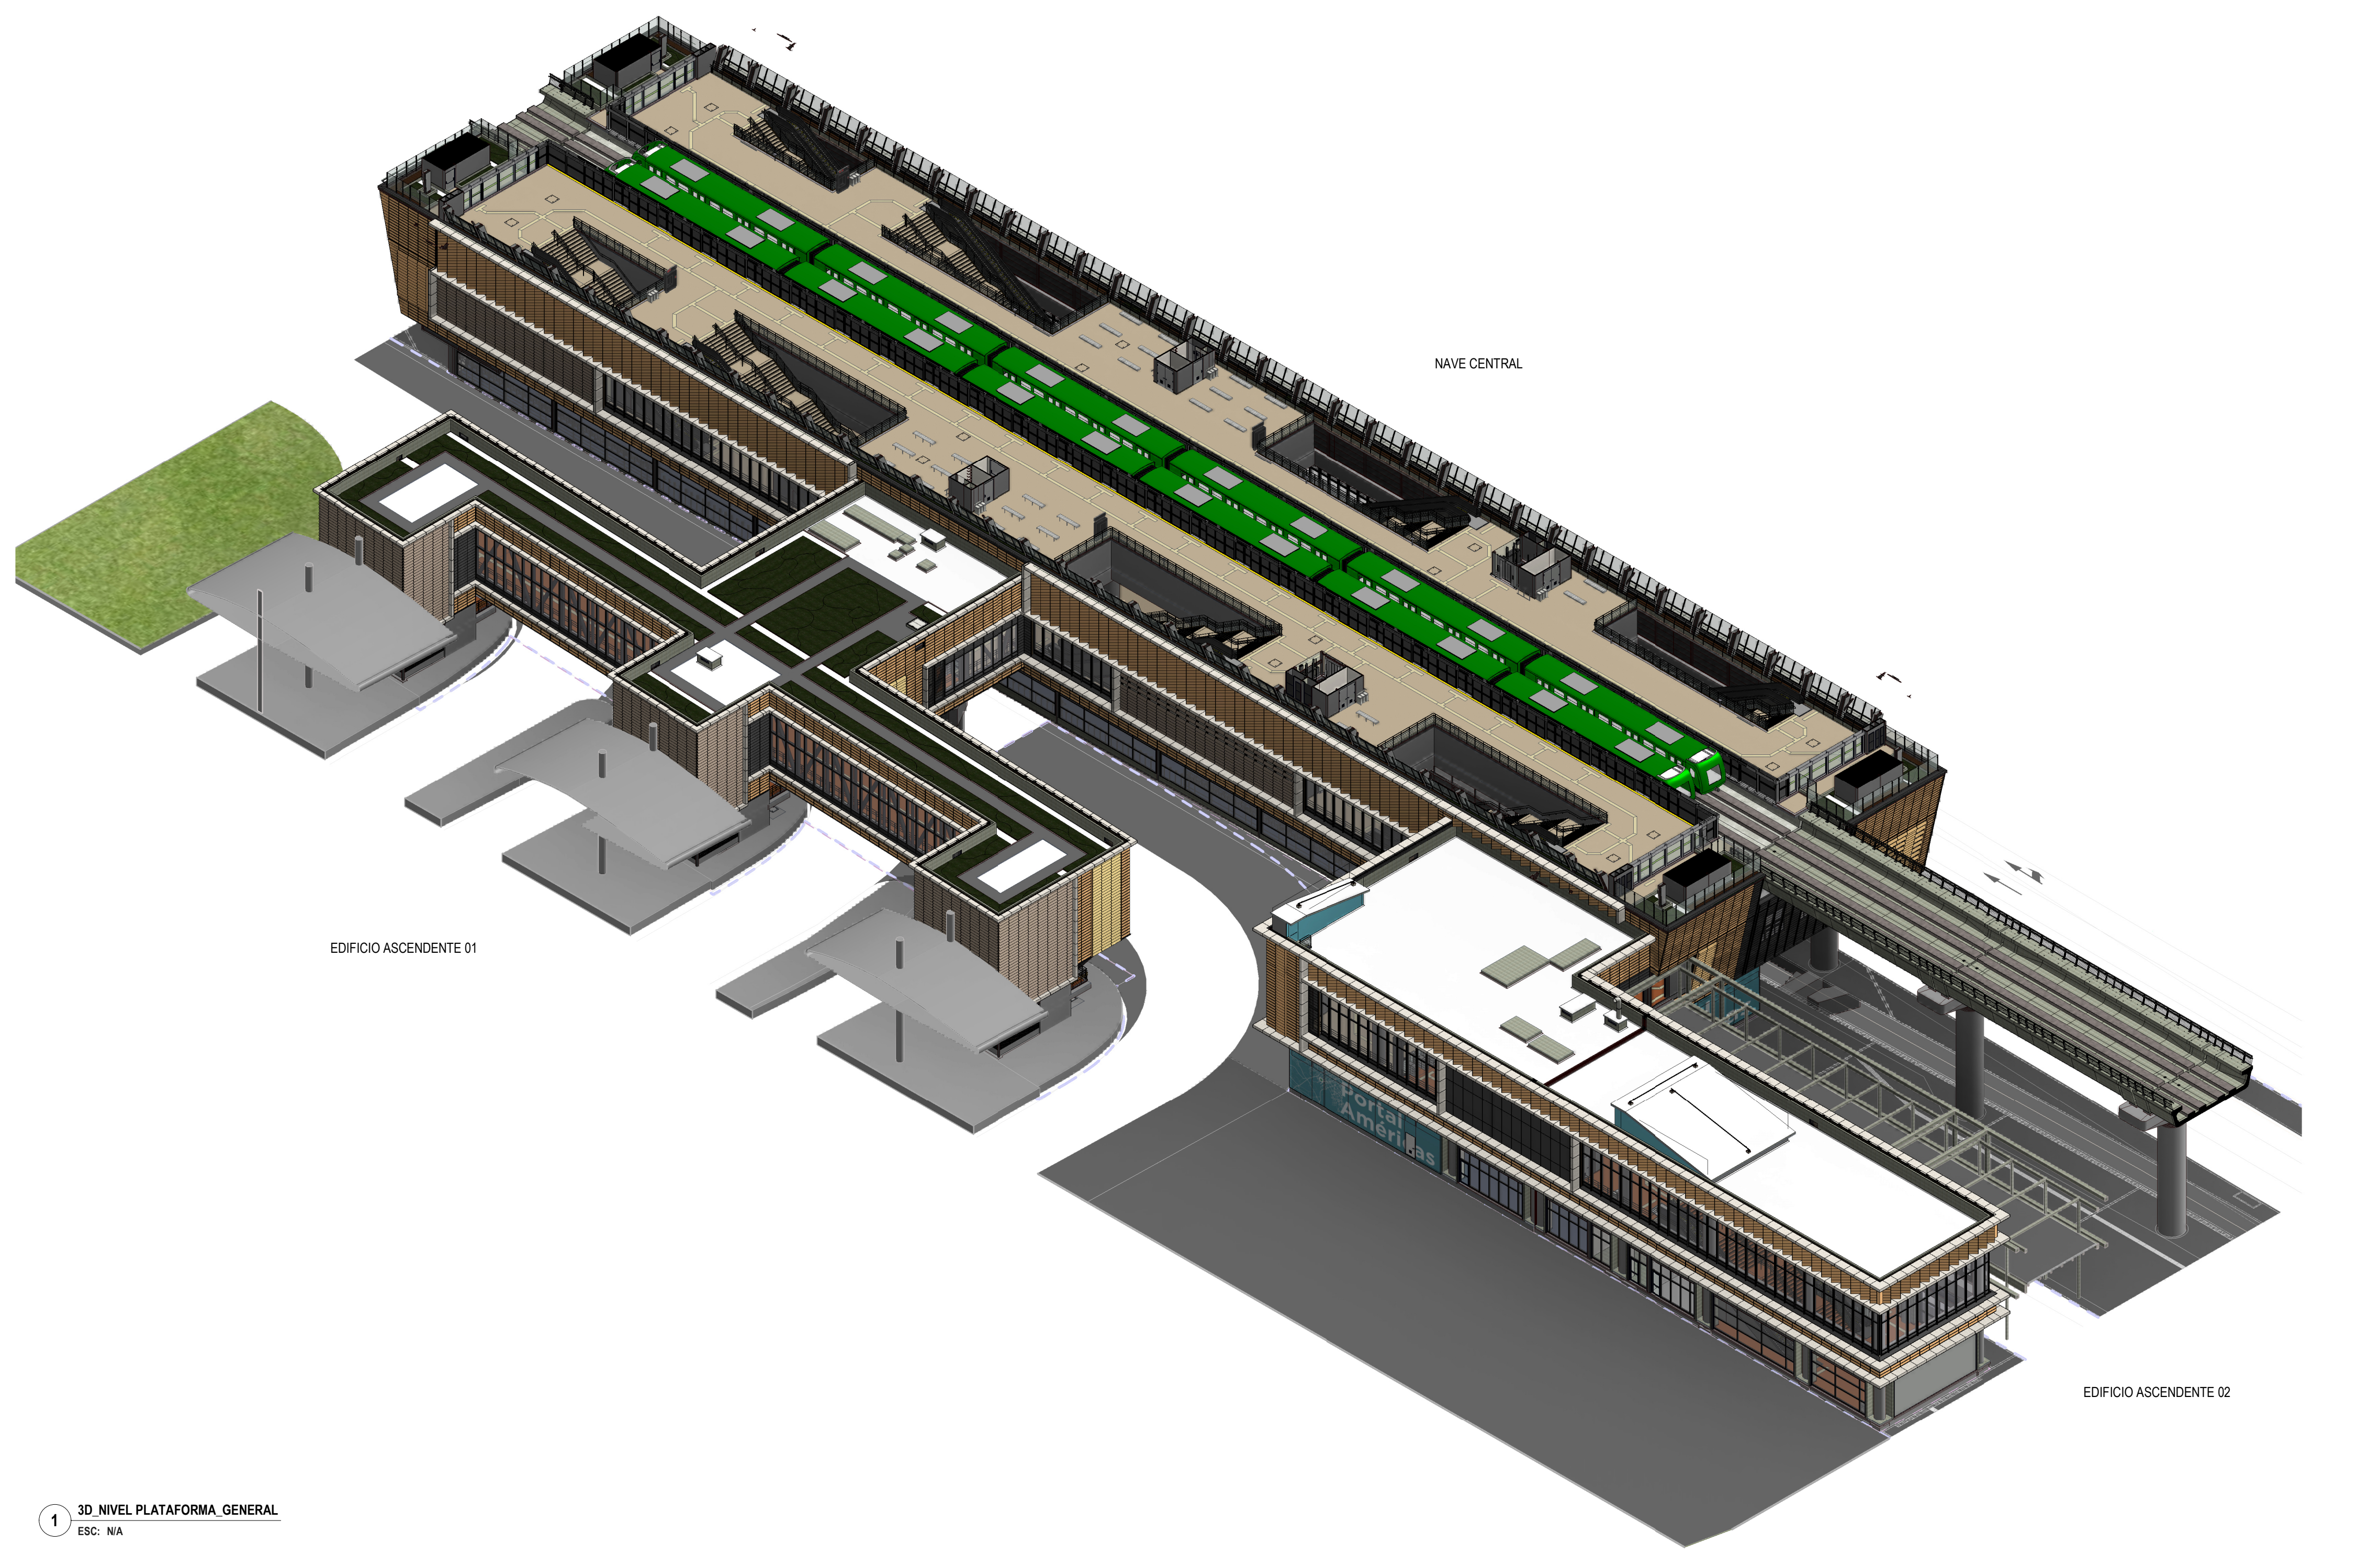

1 3D_NIVEL PLATAFORMA_GENERAL
ESC: N/A

TABLA DE ÁREAS ÚTILES (NIVEL PLATAFORMA)

CÓDIGO	NOMBRE	ÁREA (m²)	DEPARTAMENTO
NAVE CENTRAL			
ARQ_PL_03_PLATAFORMA			
J-01	JARDÍN	30.74	JARDÍN
J-02	JARDÍN	30.82	JARDÍN
J-03	JARDÍN	30.74	JARDÍN
J-04	JARDÍN	30.81	JARDÍN
PA-03	ÁREA PAGA	1248.18	ÁREA PAGA
PA-04	ÁREA PAGA	1194.12	ÁREA PAGA
T-21-9	ÁREA DE INSPECCIÓN	4.86	ÁREA TÉCNICA
T-21-10	ÁREA DE INSPECCIÓN	4.86	ÁREA TÉCNICA
T-25-5	NODO DE ACCESO DE TELECOMUNICACIONES	4.59	ÁREA TÉCNICA
T-25-6	NODO DE ACCESO DE TELECOMUNICACIONES	4.61	ÁREA TÉCNICA
T-25-7	NODO DE ACCESO DE TELECOMUNICACIONES	7.63	ÁREA TÉCNICA
T-25-8	NODO DE ACCESO DE TELECOMUNICACIONES	7.60	ÁREA TÉCNICA
ZDR-03	ZONA DE REFUGIO (PMR)	7.29	ZONA DE REFUGIO
ZDR-04	ZONA DE REFUGIO (PMR)	7.29	ZONA DE REFUGIO
ZDR-05	ZONA DE REFUGIO (PMR)	7.29	ZONA DE REFUGIO
ZDR-06	ZONA DE REFUGIO (PMR)	7.29	ZONA DE REFUGIO
TOTAL NIVEL PLATAFORMA		2628.71	

TABLA DE ÁREAS ÚTILES POR DEPARTAMENTO (NIVEL PLATAFORMA)

DEPARTAMENTO	ÁREA (m²)
JARDÍN	123.11
ZONA DE REFUGIO	29.16
ÁREA PAGA	2442.29
ÁREA TÉCNICA	34.15
TOTAL NIVEL PLATAFORMA	2628.71

LOCALIZACIÓN

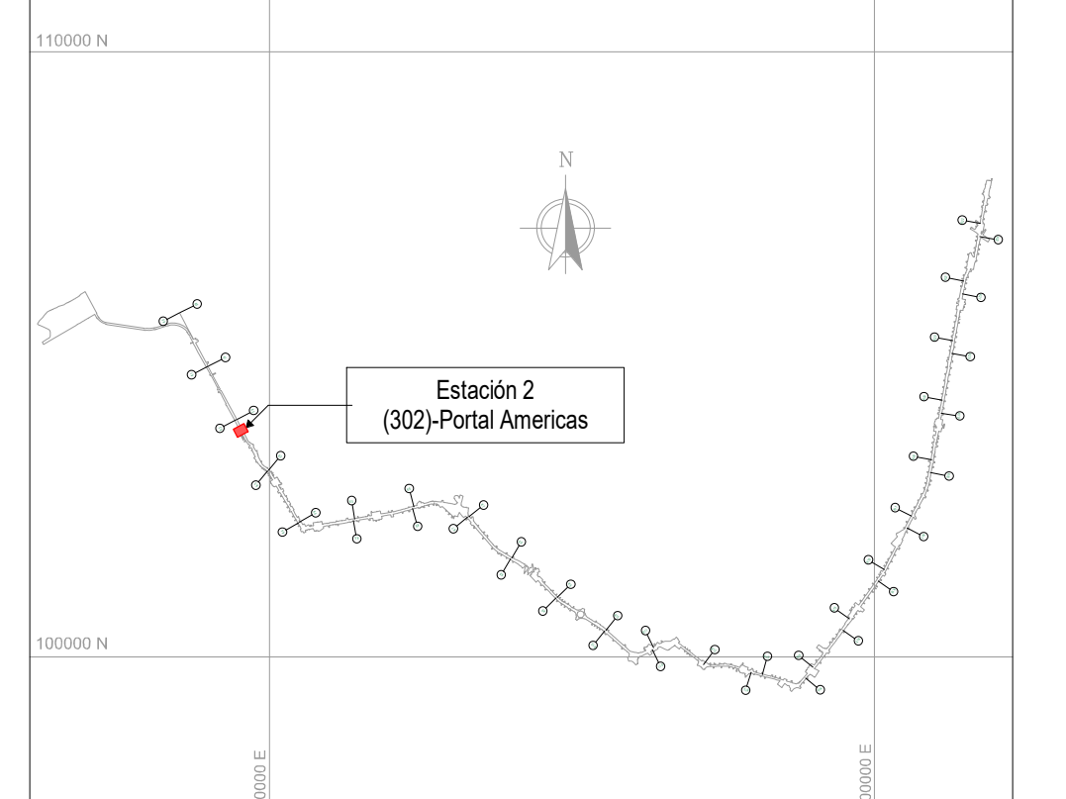

NOTAS

01 TODAS LAS DIMENSIONES ESTÁN CONFIGURADAS EN METROS A MENOS QUE SE INDIQUE UNA UNIDAD DE MEDIDA DIFERENTE.

02 TODAS LAS MEDIDAS, UBICACIÓN Y NIVELES DEBEN VERIFICARSE EN EL LUGAR DE CONSTRUCCIÓN.

03 EL NIVEL DE ACCESO AL EDIFICIO PL 01 CORRESPONDE AL +0,00 DE LA ESTACIÓN Y REFERENCIA AL NIVEL 2541.40 M.S.N.M.

04 LOS NOMBRES ESPECÍFICOS DE LAS ÁREAS PUEDEN SER CONSULTADAS EN EL PLANO NO. 3 Ó EN LAS VISTAS EN PLANTA.

05 LOS COLORES QUE SE MUESTRAN EN LOS PLANOS COMO PROYECCIÓN DE ELEMENTOS ARQUITECTÓNICOS COMO CUBIERTAS FACHADAS MUROS ETC. NO REPRESENTAN LA MATERIALIDAD Y REALIDAD DE ACABADOS DEL PROYECTO, SOLO SON INDICATIVOS PARA REALIZAR UNA CORRECTA LECTURA DE LA PLANIMETRÍA.

06 LAS ESCALERAS ELÉCTRICAS INDICAN SU SENTIDO CON LA SIGUIENTE NOMENCLATURA: “SUBE” Y “BAJA”.

07 SE DEBEN REVISAR LOS NIVELES ESTRUCTURALES PARA NIVEL DE ACCESO PL_01 Y SUBNIVELES, PL_02 (INTERMEDIO), PL_03 (PLATAFORMA) CON LA PLANIMETRIA DE PLACAS ESTRUCTURALES EN LOS ENTREGABLES L1T1-1200-302-CON-ED-EST-PL-0017, 18 Y L1T1-1300-402-CON-ED-EST-PL-0023, 26, 29, 66, 69, RESPECTIVAMENTE. EL NIVEL ESTRUCTURAL (NE) REFERENCIA LOS ESPACIOS DONDE SE DEBE ACONDICIONAR EL ACABADO DE PISO SEGÚN CORRESPONDA, CON LOS NIVELES DE PISO TERMINADO (NPT). LOS NIVELES PROYECTADOS DE EMPATE (NPE) EN LAS ÁREAS DE SERVICIOS ADICIONALES, REFERENCIAN LA ADECUACIÓN DE LOS DESNIVELES EN ESTAS ÁREAS; QUEDA COMO RESPONSABILIDAD DEL LOCATARIO DEFINIR Y ACONDICIONAR ESTE ACABADO DE PISO (NPE) EN LÍNEA CON EL NIVEL (NPT) DE ESPACIOS COLINDANTES. EL NIVEL ESTRUCTURAL (NE) SE ENCUENTRA A (- 0.10M) POR DEBAJO DE LOS NIVELES DE PISO TERMINADO (NPT) Y LOS NIVELES PROYECTADOS DE EMPATE (NPE) MARCADOS EN LA PLANIMETRÍA.

- ARQ_PL_00 = SÓTANO / NPT -5.40 m
- ARQ_PL_01 = ACCESO / NPT 0.00 m
- ARQ_PL_01.1 = ACCESO / NPT 0.10 m
- ARQ_PL_01.2 = ACCESO / NPT 0.60 m
- ARQ_PL_01.3 = ACCESO / NPT 0.75 m
- ARQ_PL_01.4 = ACCESO / NPT 1.06 m
- ARQ_PL_01.5 = ACCESO / NPT 1.15 m
- ARQ_PL_01.6 = ACCESO / NPT 1.33 m
- ARQ_PL_02 = INTERMEDIO / NPT 8.05 m
- ARQ_PL_02.1 = PLACA INFERIOR VIGA CAJÓN / NPT 14.27 m
- ARQ_PL_02.1' = CUBIERTA EDIFICACIONES / NPT 15.05 m
- ARQ_PL_02.2 = TOPE DE RIEL (TOR) / NPT 16.40 m
- ARQ_PL_03 = PLATAFORMA / NPT 17.54 m
- ARQ_PL_05 = CUBIERTA NAVE CENTRAL / NPT 26.94 m

CONVENCIONES

- ‐ ‐ ‐ LÍMITE DE INTERVENCIÓN
- ‐ ‐ ‐ HUELLA APÉNDICE TÉCNICO
- ▬ MURO DIVISORIO
- ‐ ‐ ‐ PROYECCIÓN NIVEL SUPERIOR
- ▨ SERVICIOS ADICIONALES - ÁREA NO PAGA
- ▨ SERVICIOS ADICIONALES - ÁREA PAGA
- ▨ SERVICIO PÚBLICO
- ▨ ZONA DE REFUGIO
- ▨ ÁREA CULTURAL
- ▨ ÁREA NO PAGA
- ▨ ÁREA OPERATIVA
- ▨ ÁREA PAGA
- ▨ ÁREA PÚBLICA
- ▨ ÁREA TÉCNICA

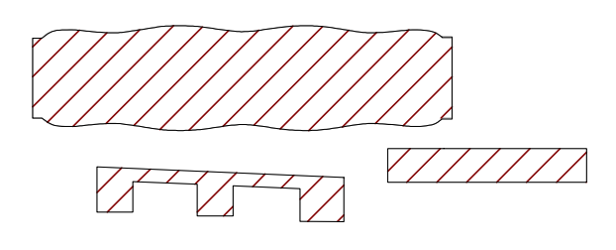

PLANO CLAVE ESTACIÓN 2

No.	PLANOS DE REFERENCIA	REV.
No.	**MODELO BIM DE REFERENCIA**	**REV.**
1	L1T1-1100-202-CON-ED-EST-MO-0001.rvt	V00
2	L1T1-1100-203-CON-ED-EST-MO-0001.rvt	V00
3	L1T1-1100-302-CON-ED-EST-MO-0001.rvt	V00
4	L1T1-1150-202-CON-ED-EST-MO-0001.rvt	V00
5	L1T1-1150-203-CON-ED-EST-MO-0001.rvt	V00
6	L1T1-1150-302-CON-ED-EST-MO-0001.rvt	V00
7	L1T1-1200-302-CON-ED-CIV-MO-0001.rvt	V00
8	L1T1-1300-402-CON-ED-EST-MO-0001.rvt	V00
9	L1T1-1300-402-CON-ED-EST-MO-0002.rvt	V00
10	L1T1-1310-402-CON-ED-EST-MO-0001.rvt	V00
11	L1T1-1410-302-CON-ED-MEC-MO-0001.rvt	V00
12	L1T1-1420-302-CON-ED-MEC-MO-0001.rvt	V00
13	L1T1-5160-302-CON-ED-EST-MO-0001.rvt	V00
14	L1T1-5160-302-CON-ED-ARQ-MO-0001.rvt	V00
15	L1T1-5300-302-CON-ED-MEC-MO-0001.rvt	V00
16	L1T1-5600-302-CON-ED-INS-MO-0001.rvt	V00
17	L1T1-1270-302-CON-ED-ARQ-MO-0011.rvt	V00
18	L1T1-1330-402-CON-ED-ARQ-MO-0011.rvt	V00
19	L1T1-1330-402-CON-ED-ARQ-MO-0012.rvt	V00
No.	**PAQUETE DE TRABAJO DE REFERENCIA**	**REV.**
1	XREF-URBANISM_CONTEXT_ST02.RVT	

0 2 10m
1:200

VÁLIDO PARA CONSTRUCCIÓN
01-03-26

METRO BOGOTÁ
GCS Consorcio Consultores PMO Bogotá
CONSORCIO SUPERVISOR PLMB
CHEC

DISEÑÓ:
REN ZHENHUA
Licencia de Arq.nivel I (China): 1101735-614

APROBÓ:
DIEGO ERNESTO DUEÑAS
Mat.: 25202-53876 CND

REVISÓ:
CARLOS MAURICIO BARRETO BARBOSA
Mat.: A4012012-14139353

DIBUJÓ:
EQUIPO CHEC

REVISIÓN No.	FECHA	DESCRIPCIÓN	REVISÓ	APROBÓ	APROBACIÓN CLIENTE
V01	01/03/2026	EMITIDO PARA CONSTRUCCIÓN	C.M.B.B	D.E.D	
V00	27/11/2024	REVISIÓN NO OBJETADA - EMITIDO PARA CONSTRUCCIÓN	F.B.R	E.O.M	
VGG	23/05/2024	EMITIDO PARA REVISIÓN Y COMENTARIOS DEL CLIENTE E INTERVENTORÍA - INCLUYE COMENTARIOS /(AJUSTES V4)	F.B.R	E.O.M	
VFF	11/12/2023	EMITIDO PARA REVISIÓN Y COMENTARIOS DEL CLIENTE E INTERVENTORÍA - INCLUYE COMENTARIOS /(AJUSTES V3)	F.B.R	M.B.M	
VEE	30/06/2023	EMITIDO PARA REVISIÓN Y COMENTARIOS DEL CLIENTE E INTERVENTORÍA - INCLUYE COMENTARIOS /(AJUSTES V2)	J.E.M	M.B.M	
VDD	18/12/2022	EMITIDO PARA REVISIÓN Y COMENTARIOS DEL CLIENTE E INTERVENTORÍA - INCLUYE COMENTARIOS /(AJUSTES)	J.E.M	M.B.M	
VCC	02/06/2022	EMITIDO PARA REVISIÓN Y COMENTARIOS DEL CLIENTE E INTERVENTORÍA - INCLUYE COMENTARIOS /(ENTREGA 90%)	J.E.M	M.B.M	
VBB	06/12/2021	EMITIDO PARA REVISIÓN Y COMENTARIOS DEL CLIENTE E INTERVENTORÍA	J.E.M	M.B.M	
VA0	30/06/2021	EMITIDO PARA COMENTARIOS INTERNOS - EMISIÓN PRELIMINAR PARA COMENTARIOS	J.E.M	M.B.M	

METRO LÍNEA 1

DIRECTOR DE INTERVENTORÍA:
JAVIER DESCARGA N.
Mat.:25202-68697 CND

ESPECIALISTA INTERVENTORÍA:
CARLOS ALBERTO HOYOS SOTO
Mat.:A25072000-14251682

FECHA:
MARZO 2026

METRO LÍNEA 1
CONTRATO DE CONCESIÓN No. 163 DE 2019

PROYECTO PRIMERA LÍNEA DEL METRO DE BOGOTÁ - TRAMO 1

INFRAESTRUCTURA VIAL

ARQUITECTURA

ESTACIÓN METRO 2 (PORTAL AMÉRICAS)
GENERAL
VISTA EN PLANTA Y 3D - NIVEL PLATAFORMA

PLANCHA No: L1T1-0000-302-CON-ED-ARQ-PL-0001_07_V01
ARCHIVO: L1T1-0000-302-CON-ED-ARQ-MO-0001_V00.rvt
ESCALA: INDICADA
FECHA: JUNIO 2021
REVISIÓN No. V01
PLANO No. 07 DE 85