L1T1-CON-CAL-FR-0120 - B1 : 1000x707mm

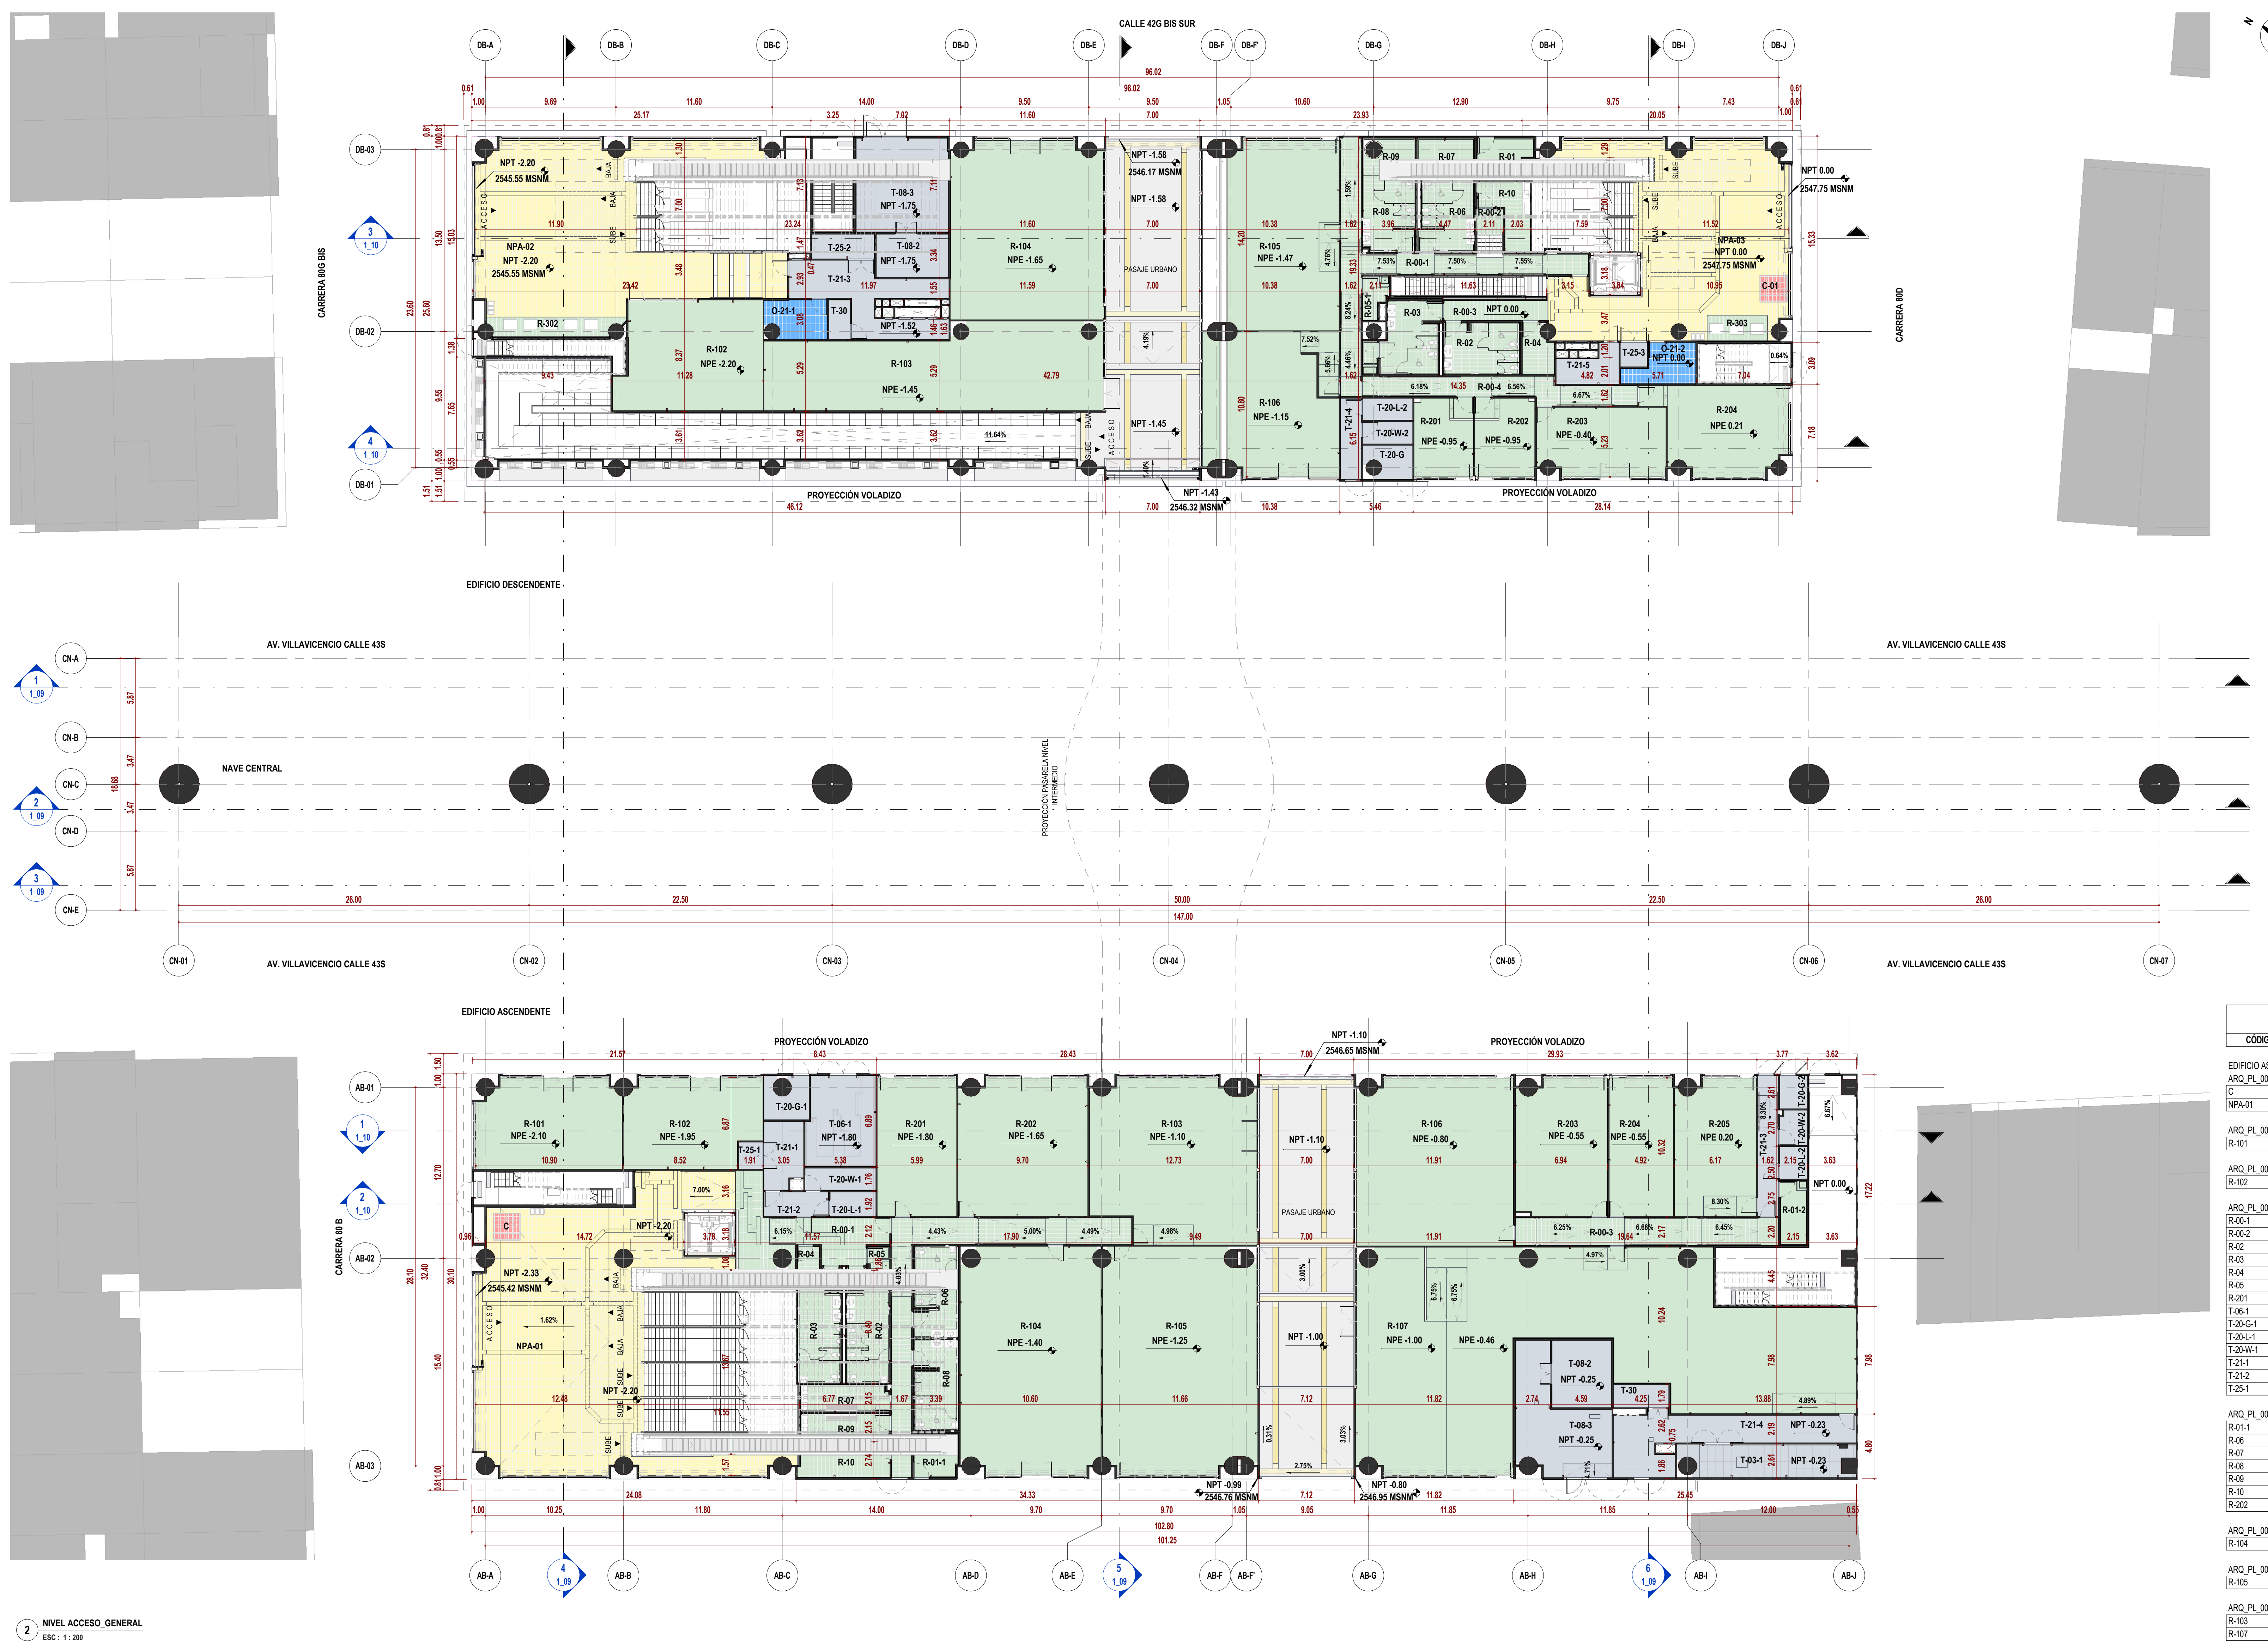

2 NIVEL_ACCESO_GENERAL
ESC: 1 : 200

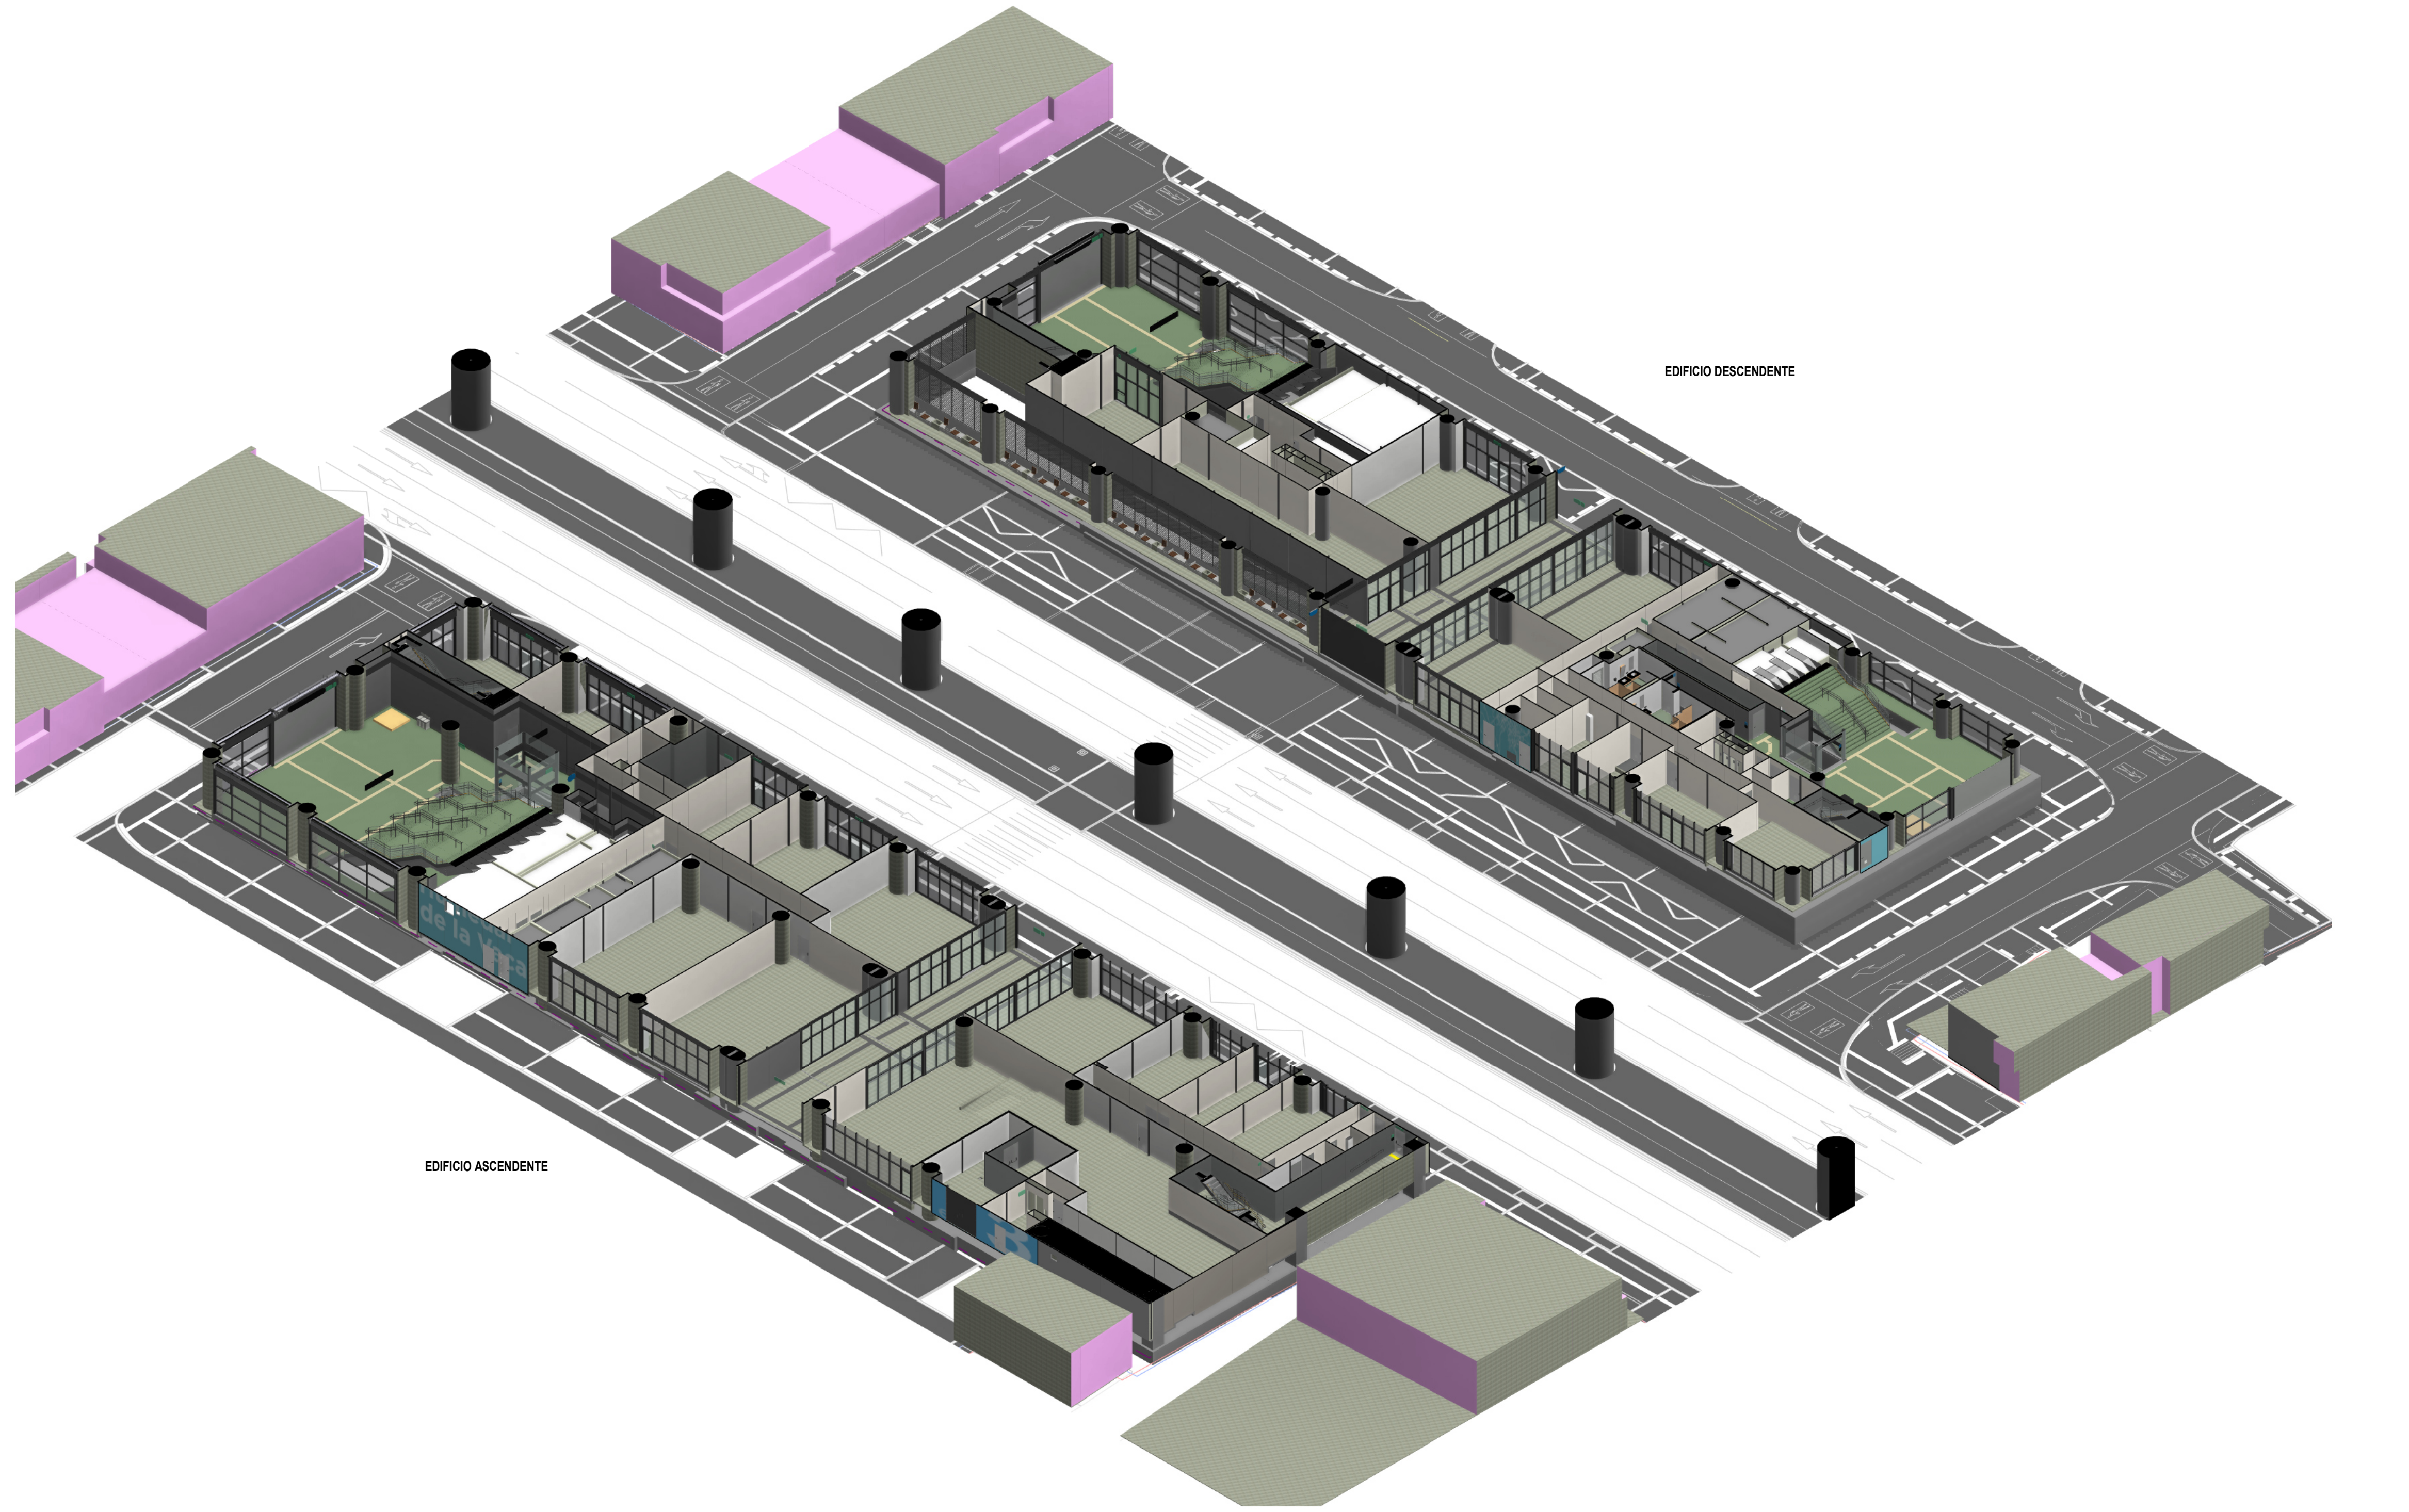

1 3D_NIVEL ACCESO_GENERAL
ESC : N/A

TABLA DE ÁREAS ÚTILES (NIVEL ACCESO)

CÓDIGO	NOMBRE	ÁREA (m²)	DEPARTAMENTO
EDIFICIO ASCENDENTE			
ARQ_PL_00.1_ACCESO			
C	ÁREAS DE USO CULTURAL	4.00	ÁREA CULTURAL
NPA-01	ÁREA NO PAGA	283.29	ÁREA NO PAGA
		287.29	
ARQ_PL_00.2_ACCESO			
R-101	SERVICIOS ADICIONALES - ÁREA DE SERVICIO	70.08	SERVICIOS ADICIONALES - ÁREA NO PAGA
		70.08	
ARQ_PL_00.3_ACCESO			
R-102	SERVICIOS ADICIONALES - ÁREA DE SERVICIO	64.74	SERVICIOS ADICIONALES - ÁREA NO PAGA
		64.74	
ARQ_PL_00.4_ACCESO			
R-00-1	SERVICIOS ADICIONALES - CORREDOR OPERATIVO	41.79	SERVICIOS ADICIONALES - ÁREA NO PAGA
R-00-2	SERVICIOS ADICIONALES - CORREDOR OPERATIVO	61.70	SERVICIOS ADICIONALES - ÁREA NO PAGA
R-02	SERVICIOS ADICIONALES - BAÑO PÚBLICO DE MUJERES	26.56	SERVICIOS ADICIONALES - ÁREA NO PAGA
R-03	SERVICIOS ADICIONALES - BAÑO PÚBLICO DE HOMBRES	26.49	SERVICIOS ADICIONALES - ÁREA NO PAGA
R-04	SERVICIOS ADICIONALES - CONTROL DE ACCESO BAÑOS PÚBLICOS	2.82	SERVICIOS ADICIONALES - ÁREA NO PAGA
R-05	SERVICIOS ADICIONALES - CUARTO DE LIMPIEZA	2.66	SERVICIOS ADICIONALES - ÁREA NO PAGA
R-201	SERVICIOS ADICIONALES - ÁREA DE COMIDAS	60.35	SERVICIOS ADICIONALES - ÁREA NO PAGA
T-06-1	LOCAL SECUNDARIO DE TABLEROS	33.97	ÁREA TÉCNICA
T-20-G-1	MEDIDORES (GAS)	9.44	ÁREA TÉCNICA
T-20-L-1	MEDIDORES (LUZ)	6.11	ÁREA TÉCNICA
T-20-W-1	MEDIDORES (AGUA)	8.69	ÁREA TÉCNICA
T-21-1	ÁREA DE INSPECCIÓN	13.97	ÁREA TÉCNICA
T-21-2	ÁREA DE INSPECCIÓN	8.57	ÁREA TÉCNICA
T-25-1	NODO DE ACCESO DE TELECOMUNICACIONES	3.58	ÁREA TÉCNICA
		306.70	
ARQ_PL_00.6_ACCESO			
R-01-1	SERVICIOS ADICIONALES - CUARTO DE BASURAS PARA METRO	10.64	SERVICIOS ADICIONALES - ÁREA NO PAGA
R-06	SERVICIOS ADICIONALES - BAÑOS EMPLEADOS MUJERES	21.47	SERVICIOS ADICIONALES - ÁREA NO PAGA
R-07	SERVICIOS ADICIONALES - VESTIDORES EMPLEADOS MUJERES	13.00	SERVICIOS ADICIONALES - ÁREA NO PAGA
R-08	SERVICIOS ADICIONALES - BAÑOS EMPLEADOS HOMBRES	21.36	SERVICIOS ADICIONALES - ÁREA NO PAGA
R-09	SERVICIOS ADICIONALES - VESTIDORES EMPLEADOS HOMBRES	13.17	SERVICIOS ADICIONALES - ÁREA NO PAGA
R-10	SERVICIOS ADICIONALES - SALA DE EMPLEADOS	17.46	SERVICIOS ADICIONALES - ÁREA NO PAGA
R-202	SERVICIOS ADICIONALES - ÁREA DE COMIDAS	96.13	SERVICIOS ADICIONALES - ÁREA NO PAGA
		193.22	
ARQ_PL_00.8_ACCESO			
R-104	SERVICIOS ADICIONALES - ÁREA DE SERVICIO	171.36	SERVICIOS ADICIONALES - ÁREA NO PAGA
		171.36	
ARQ_PL_00.9_ACCESO			
R-105	SERVICIOS ADICIONALES - ÁREA DE SERVICIO	186.49	SERVICIOS ADICIONALES - ÁREA NO PAGA
		186.49	
ARQ_PL_00.10_ACCESO			
R-103	SERVICIOS ADICIONALES - ÁREA DE SERVICIO	138.93	SERVICIOS ADICIONALES - ÁREA NO PAGA
R-107	SERVICIOS ADICIONALES - ÁREA DE SERVICIO	403.89	SERVICIOS ADICIONALES - ÁREA NO PAGA
		542.82	
ARQ_PL_00.11_ACCESO			
R-00-3	SERVICIOS ADICIONALES - CORREDOR OPERATIVO	40.38	SERVICIOS ADICIONALES - ÁREA NO PAGA
R-106	SERVICIOS ADICIONALES - ÁREA DE SERVICIO	142.48	SERVICIOS ADICIONALES - ÁREA NO PAGA
		182.86	
ARQ_PL_00.13_ACCESO			
R-203	SERVICIOS ADICIONALES - ÁREA DE COMIDAS	67.47	SERVICIOS ADICIONALES - ÁREA NO PAGA
R-204	SERVICIOS ADICIONALES - ÁREA DE COMIDAS	49.39	SERVICIOS ADICIONALES - ÁREA NO PAGA
		116.86	
ARQ_PL_00.15_ACCESO			
T-03-1	LOCAL SECUNDARIO DE TELECOMUNICACIONES	29.67	ÁREA TÉCNICA
T-08-2	CENTRO DE TRANSFORMACIÓN ENEL-CODENSA (CT)_CUARTO BAJA TENSIÓN	22.33	ÁREA TÉCNICA
T-08-3	CENTRO DE TRANSFORMACIÓN ENEL-CODENSA (CT)_CUARTO MEDIA TENSIÓN	46.46	ÁREA TÉCNICA
T-21-4	ÁREA DE INSPECCIÓN	48.16	ÁREA TÉCNICA
T-30	SISTEMA PROTECCIÓN CONTRA INCENDIO ENEL	6.92	ÁREA TÉCNICA
		153.55	
ARQ_PL_01_ACCESO			
R-01-2	SERVICIOS ADICIONALES - CUARTO DE BASURAS PARA METRO	9.52	SERVICIOS ADICIONALES - ÁREA NO PAGA
R-205	SERVICIOS ADICIONALES - ÁREA DE COMIDAS	60.13	SERVICIOS ADICIONALES - ÁREA NO PAGA
T-20-G-2	MEDIDORES (GAS)	5.11	ÁREA TÉCNICA
T-20-L-2	MEDIDORES (LUZ)	4.87	ÁREA TÉCNICA
T-20-W-2	MEDIDORES (AGUA)	5.12	ÁREA TÉCNICA
T-21-3	ÁREA DE INSPECCIÓN	16.10	ÁREA TÉCNICA
		100.86	
EDIFICIO DESCENDENTE			
ARQ_PL_00.1_ACCESO			
NPA-02	ÁREA NO PAGA	204.18	ÁREA NO PAGA
R-102	SERVICIOS ADICIONALES - ÁREA DE SERVICIO	84.72	SERVICIOS ADICIONALES - ÁREA NO PAGA
R-302	SERVICIOS ADICIONALES - MÁQUINAS EXPENDEDORAS/CAJEROS AUTOMÁTICOS	13.73	SERVICIOS ADICIONALES - ÁREA NO PAGA
		302.63	
ARQ_PL_00.5_ACCESO			
T-08-2	CENTRO DE TRANSFORMACIÓN ENEL-CODENSA (CT)_CUARTO BAJA TENSIÓN	17.18	ÁREA TÉCNICA
T-08-3	CENTRO DE TRANSFORMACIÓN ENEL-CODENSA (CT)_CUARTO MEDIA TENSIÓN	47.72	ÁREA TÉCNICA
		64.90	
ARQ_PL_00.6_ACCESO			
R-104	SERVICIOS ADICIONALES - ÁREA DE SERVICIO	146.79	SERVICIOS ADICIONALES - ÁREA NO PAGA
		146.79	
ARQ_PL_00.7_ACCESO			
O-21-1	ALMACENAMIENTO DE LA ESTACIÓN	12.75	ÁREA OPERATIVA
R-00-1	SERVICIOS ADICIONALES - CORREDOR OPERATIVO	54.82	SERVICIOS ADICIONALES - ÁREA NO PAGA
R-105	SERVICIOS ADICIONALES - ÁREA DE SERVICIO	115.59	SERVICIOS ADICIONALES - ÁREA NO PAGA
T-21-3	ÁREA DE INSPECCIÓN	39.53	ÁREA TÉCNICA
T-25-2	NODO DE ACCESO DE TELECOMUNICACIONES	8.66	ÁREA TÉCNICA
T-30	SISTEMA PROTECCIÓN CONTRA INCENDIO ENEL	4.81	ÁREA TÉCNICA
		236.15	
ARQ_PL_00.8_ACCESO			
R-00-2	SERVICIOS ADICIONALES - CORREDOR OPERATIVO	3.90	SERVICIOS ADICIONALES - ÁREA NO PAGA
R-01	SERVICIOS ADICIONALES - CUARTO DE BASURAS PARA METRO	11.68	SERVICIOS ADICIONALES - ÁREA NO PAGA
R-10	SERVICIOS ADICIONALES - SALA DE EMPLEADOS	14.06	SERVICIOS ADICIONALES - ÁREA NO PAGA
R-103	SERVICIOS ADICIONALES - ÁREA DE SERVICIO	143.65	SERVICIOS ADICIONALES - ÁREA NO PAGA
		173.29	
ARQ_PL_00.10_ACCESO			
R-106	SERVICIOS ADICIONALES - ÁREA DE SERVICIO	103.39	SERVICIOS ADICIONALES - ÁREA NO PAGA
T-20-G	MEDIDORES (GAS)	7.83	ÁREA TÉCNICA
T-20-L-2	MEDIDORES (LUZ)	6.15	ÁREA TÉCNICA
T-20-W-2	MEDIDORES (AGUA)	6.15	ÁREA TÉCNICA
T-21-4	ÁREA DE INSPECCIÓN	9.17	ÁREA TÉCNICA
		132.69	
ARQ_PL_00.11_ACCESO			
R-00-4	SERVICIOS ADICIONALES - CORREDOR OPERATIVO	31.93	SERVICIOS ADICIONALES - ÁREA NO PAGA
R-201	SERVICIOS ADICIONALES - ÁREA DE COMIDAS	25.31	SERVICIOS ADICIONALES - ÁREA NO PAGA
R-202	SERVICIOS ADICIONALES - ÁREA DE COMIDAS	25.62	SERVICIOS ADICIONALES - ÁREA NO PAGA
		82.86	
ARQ_PL_00.12_ACCESO			
R-05-1	SERVICIOS ADICIONALES - CUARTO DE LIMPIEZA	5.31	SERVICIOS ADICIONALES - ÁREA NO PAGA
		5.31	
ARQ_PL_00.14_ACCESO			
R-06	SERVICIOS ADICIONALES - BAÑOS EMPLEADOS MUJERES	22.13	SERVICIOS ADICIONALES - ÁREA NO PAGA
R-07	SERVICIOS ADICIONALES - VESTIDORES EMPLEADOS MUJERES	11.48	SERVICIOS ADICIONALES - ÁREA NO PAGA
R-08	SERVICIOS ADICIONALES - BAÑOS EMPLEADOS HOMBRES	21.41	SERVICIOS ADICIONALES - ÁREA NO PAGA
R-09	SERVICIOS ADICIONALES - VESTIDORES EMPLEADOS HOMBRES	8.96	SERVICIOS ADICIONALES - ÁREA NO PAGA
R-203	SERVICIOS ADICIONALES - ÁREA DE COMIDAS	48.00	SERVICIOS ADICIONALES - ÁREA NO PAGA
		111.97	
ARQ_PL_01_ACCESO			
C-01	ÁREAS DE USO CULTURAL	4.00	ÁREA CULTURAL
NPA-03	ÁREA NO PAGA	180.13	ÁREA NO PAGA
O-21-2	ALMACENAMIENTO DE LA ESTACIÓN	13.15	ÁREA OPERATIVA
R-00-3	SERVICIOS ADICIONALES - CORREDOR OPERATIVO	11.62	SERVICIOS ADICIONALES - ÁREA NO PAGA
R-02	SERVICIOS ADICIONALES - BAÑO PÚBLICO DE MUJERES	21.28	SERVICIOS ADICIONALES - ÁREA NO PAGA
R-03	SERVICIOS ADICIONALES - BAÑO PÚBLICO DE HOMBRES	22.23	SERVICIOS ADICIONALES - ÁREA NO PAGA
R-04	SERVICIOS ADICIONALES - CONTROL DE ACCESO BAÑOS PÚBLICOS	7.97	SERVICIOS ADICIONALES - ÁREA NO PAGA
R-05-2	SERVICIOS ADICIONALES - CUARTO DE LIMPIEZA	2.71	SERVICIOS ADICIONALES - ÁREA NO PAGA
R-204	SERVICIOS ADICIONALES - ÁREA DE COMIDAS	60.05	SERVICIOS ADICIONALES - ÁREA NO PAGA
R-303	SERVICIOS ADICIONALES - MÁQUINAS EXPENDEDORAS/CAJEROS AUTOMÁTICOS	8.44	SERVICIOS ADICIONALES - ÁREA NO PAGA
T-21-5	ÁREA DE INSPECCIÓN	10.73	ÁREA TÉCNICA
T-25-3	NODO DE ACCESO DE TELECOMUNICACIONES	3.60	ÁREA TÉCNICA
		345.90	
TOTAL NIVEL ACCESO		3979.31	

TABLA DE ÁREAS ÚTILES POR DEPARTAMENTO (NIVEL ACCESO)

DEPARTAMENTO	ÁREA (m²)
EDIFICIO ASCENDENTE	
ARQ_PL_00.1_ACCESO	
ÁREA CULTURAL	4.00
ÁREA NO PAGA	283.29
ARQ_PL_00.2_ACCESO	
SERVICIOS ADICIONALES - ÁREA NO PAGA	70.08
ARQ_PL_00.3_ACCESO	
SERVICIOS ADICIONALES - ÁREA NO PAGA	64.74
ARQ_PL_00.4_ACCESO	
SERVICIOS ADICIONALES - ÁREA NO PAGA	222.37
ÁREA TÉCNICA	84.34
ARQ_PL_00.6_ACCESO	
SERVICIOS ADICIONALES - ÁREA NO PAGA	193.22
ARQ_PL_00.8_ACCESO	
SERVICIOS ADICIONALES - ÁREA NO PAGA	171.36
ARQ_PL_00.9_ACCESO	
SERVICIOS ADICIONALES - ÁREA NO PAGA	186.49
ARQ_PL_00.10_ACCESO	
SERVICIOS ADICIONALES - ÁREA NO PAGA	542.82
ARQ_PL_00.11_ACCESO	
SERVICIOS ADICIONALES - ÁREA NO PAGA	182.86
ARQ_PL_00.13_ACCESO	
SERVICIOS ADICIONALES - ÁREA NO PAGA	116.86
ARQ_PL_00.15_ACCESO	
ÁREA TÉCNICA	153.55
ARQ_PL_01_ACCESO	
SERVICIOS ADICIONALES - ÁREA NO PAGA	69.65
ÁREA TÉCNICA	31.20

TABLA DE ÁREAS ÚTILES POR DEPARTAMENTO (NIVEL ACCESO)

DEPARTAMENTO	ÁREA (m²)
EDIFICIO DESCENDENTE	
ARQ_PL_00.1_ACCESO	
SERVICIOS ADICIONALES - ÁREA NO PAGA	98.45
ÁREA NO PAGA	204.18
ARQ_PL_00.5_ACCESO	
ÁREA TÉCNICA	64.90
ARQ_PL_00.6_ACCESO	
SERVICIOS ADICIONALES - ÁREA NO PAGA	146.79
ARQ_PL_00.7_ACCESO	
SERVICIOS ADICIONALES - ÁREA NO PAGA	170.41
ÁREA OPERATIVA	12.75
ÁREA TÉCNICA	53.00
ARQ_PL_00.8_ACCESO	
SERVICIOS ADICIONALES - ÁREA NO PAGA	173.29
ARQ_PL_00.10_ACCESO	
SERVICIOS ADICIONALES - ÁREA NO PAGA	103.39
ÁREA TÉCNICA	29.30
ARQ_PL_00.11_ACCESO	
SERVICIOS ADICIONALES - ÁREA NO PAGA	82.86
ARQ_PL_00.12_ACCESO	
SERVICIOS ADICIONALES - ÁREA NO PAGA	5.31
ARQ_PL_00.14_ACCESO	
SERVICIOS ADICIONALES - ÁREA NO PAGA	111.97
ARQ_PL_01_ACCESO	
SERVICIOS ADICIONALES - ÁREA NO PAGA	134.29
ÁREA CULTURAL	4.00
ÁREA NO PAGA	180.13
ÁREA OPERATIVA	13.15
ÁREA TÉCNICA	14.33
TOTAL NIVEL ACCESO	3979.31

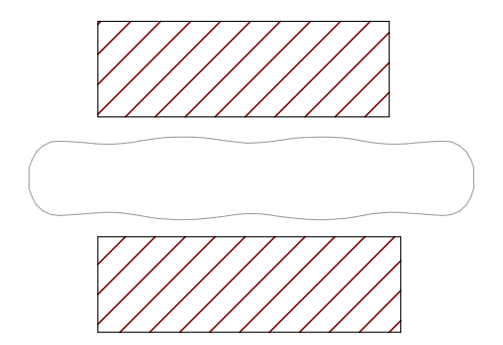

VÁLIDO PARA CONSTRUCCIÓN
01-03-26

PLANO CLAVE ESTACIÓN 3

LOCALIZACIÓN

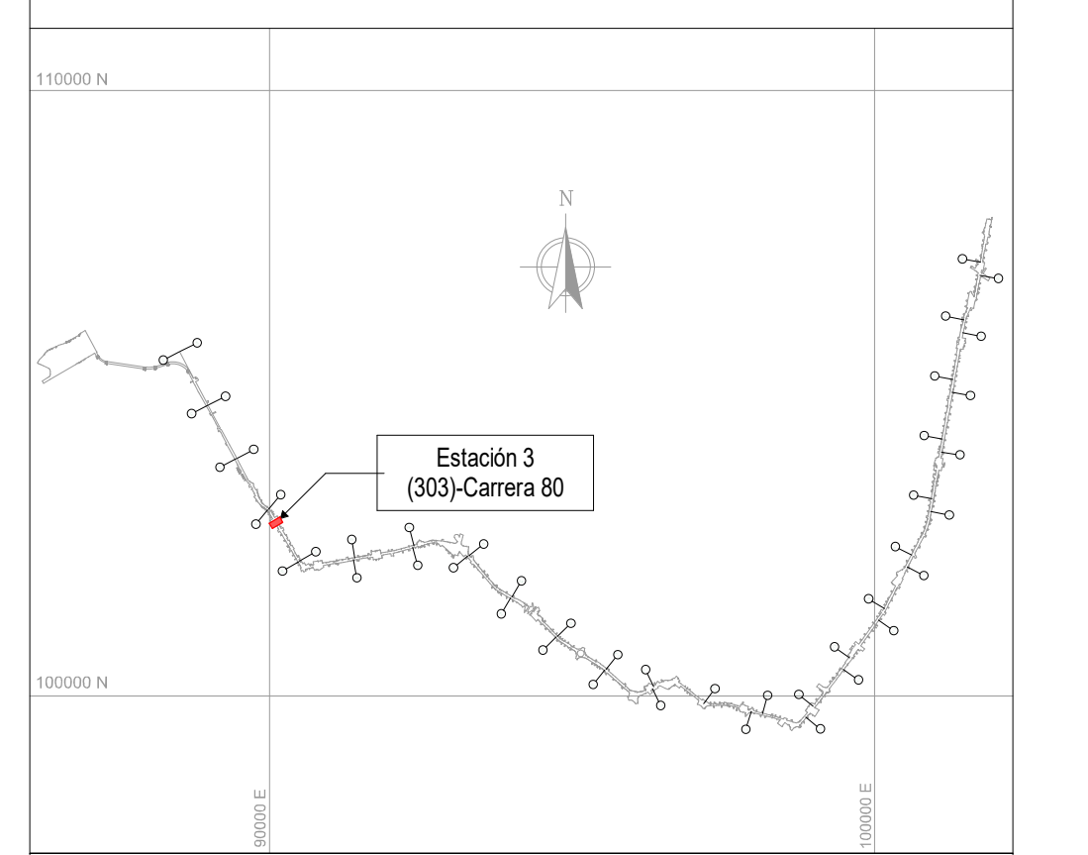

NOTAS

01 TODAS LAS DIMENSIONES ESTÁN CONFIGURADAS EN METROS A MENOS QUE SE INDIQUE UNA UNIDAD DE MEDIDA DIFERENTE.

02 TODAS LAS MEDIDAS, UBICACIÓN Y NIVELES DEBEN VERIFICARSE EN EL LUGAR DE CONSTRUCCIÓN.

03 EL NIVEL DE ACCESO AL EDIFICIO PL 01 CORRESPONDE AL +0,00 DE LA ESTACIÓN Y REFERENCIA AL NIVEL 2547.75 M.S.N.M.

04 LOS NOMBRES ESPECÍFICOS DE LAS ÁREAS PUEDEN SER CONSULTADAS EN EL PLANO NO. 3 Ó EN LAS VISTAS EN PLANTA.

05 LOS COLORES QUE SE MUESTRAN EN LOS PLANOS COMO PROYECCIÓN DE ELEMENTOS ARQUITECTÓNICOS COMO CUBIERTAS FACHADAS MUROS ETC. NO REPRESENTAN LA MATERIALIDAD Y REALIDAD DE ACABADOS DEL PROYECTO, SOLO SON INDICATIVOS PARA REALIZAR UNA CORRECTA LECTURA DE LA PLANIMETRÍA.

06 LAS ESCALERAS ELÉCTRICAS INDICAN SU SENTIDO CON LA SIGUIENTE NOMENCLATURA: “SUBE” Y “BAJA”.

07 SE DEBEN REVISAR LOS NIVELES ESTRUCTURALES PARA NIVEL DE ACCESO PL_01 Y SUBNIVELES, PL_02 (INTERMEDIO), PL_03 (PLATAFORMA) CON LA PLANIMETRÍA DE PLACAS ESTRUCTURALES EN LOS ENTREGABLES L1T1-1300-403-CON-ED-EST-PL-0038, 39, 78, 79, 82, 83 RESPECTIVAMENTE. EL NIVEL ESTRUCTURAL (NE) REFERENCIA LOS ESPACIOS DONDE SE DEBE ACONDICIONAR EL ACABADO DE PISO SEGÚN CORRESPONDA, CON LOS NIVELES DE PISO TERMINADO (NPT). LOS NIVELES PROYECTADOS DE EMPATE (NPE) EN LAS ÁREAS DE SERVICIOS ADICIONALES, REFERENCIAN LA ADECUACIÓN DE LOS DESNIVELES EN ESTAS ÁREAS; QUEDA COMO RESPONSABILIDAD DEL LOCATARIO DEFINIR Y ACONDICIONAR ESTE ACABADO DE PISO (NPE) EN LÍNEA CON EL NIVEL (NPT) DE ESPACIOS COLINDANTES. EL NIVEL ESTRUCTURAL (NE) SE ENCUENTRA A (- 0.10M) POR DEBAJO DE LOS NIVELES DE PISO TERMINADO (NPT) Y LOS NIVELES PROYECTADOS DE EMPATE (NPE) MARCADOS EN LA PLANIMETRÍA.

- ARQ_PL_00 = SÓTANO	/ NPT -8.50	- ARQ_PL_00.11 = ACCESO	/ NPT -0.95
- ARQ_PL_00.1 = ACCESO	/ NPT -2.20	- ARQ_PL_00.12 = ACCESO	/ NPT -0.75
- ARQ_PL_00.2 = ACCESO	/ NPT -2.10	- ARQ_PL_00.13 = ACCESO	/ NPT -0.55
- ARQ_PL_00.3 = ACCESO	/ NPT -1.95	- ARQ_PL_00.14 = ACCESO	/ NPT -0.45
- ARQ_PL_00.4 = ACCESO	/ NPT -1.80	- ARQ_PL_00.15 = ACCESO	/ NPT -0.35
- ARQ_PL_00.5 = ACCESO	/ NPT -1.75	- ARQ_PL_01 = ACCESO	/ NPT 0.00
- ARQ_PL_00.6 = ACCESO	/ NPT -1.65	- ARQ_PL_02 = INTERMEDIO	/ NPT 7.60
- ARQ_PL_00.7 = ACCESO	/ NPT -1.55	- ARQ_PL_02.2 = TOPE DE RIEL	/ NPT 15.20
- ARQ_PL_00.8 = ACCESO	/ NPT -1.45	- ARQ_PL_03 = PLATAFORMA	/ NPT 16.34
- ARQ_PL_00.9 = ACCESO	/ NPT -1.25	- ARQ_PL_04 = CUBIERTA EDIFICACIONES	/ NPT 22.94
- ARQ_PL_00.10 = ACCESO	/ NPT -1.15	- ARQ_PL_05 = CUBIERTA NAVE CENTRAL	/ NPT 25.59

CONVENCIONES

▬ ▬ ▬	LÍMITE DE INTERVENCIÓN
▬ ▬ ▬	HUELLA APÉNDICE TÉCNICO
■	MURO DIVISORIO
— — —	PROYECCIÓN NIVEL SUPERIOR
🟩	SERVICIOS ADICIONALES - ÁREA NO PAGA
🟩	SERVICIOS ADICIONALES - ÁREA PAGA
🟩	SERVICIO PÚBLICO
🟦	ZONA DE REFUGIO
🟥	ÁREA CULTURAL
🟨	ÁREA NO PAGA
🟦	ÁREA OPERATIVA
🟧	ÁREA PAGA
🟦	ÁREA PÚBLICA
⬜	ÁREA TÉCNICA

No.	PLANOS DE REFERENCIA	REV.

No.	MODELO BIM DE REFERENCIA	REV.
1	L1T1-1100-203-CON-ED-EST-MO-0001.rvt	V00
2	L1T1-1100-204-CON-ED-EST-MO-0001.rvt	V00
3	L1T1-1100-303-CON-ED-EST-MO-0001.rvt	V00
4	L1T1-1150-203-CON-ED-EST-MO-0001.rvt	V00
5	L1T1-1150-204-CON-ED-EST-MO-0001.rvt	V00
6	L1T1-1150-303-CON-ED-EST-MO-0001.rvt	V00
7	L1T1-1200-303-CON-ED-EST-MO-0001.rvt	V00
8	L1T1-1300-403-CON-ED-EST-MO-0001.rvt	V00
9	L1T1-1300-403-CON-ED-EST-MO-0002.rvt	V00
10	L1T1-1310-403-CON-ED-EST-MO-0001.rvt	V00
11	L1T1-1410-403-CON-ED-MEC-MO-0001.rvt	V00
12	L1T1-1420-403-CON-ED-MEC-MO-0001.rvt	V00
13	L1T1-5160-303-CON-ED-EST-MO-0001.rvt	V00
14	L1T1-5160-303-CON-ED-ARQ-MO-0001.rvt	V00
15	L1T1-5300-303-CON-ED-MEC-MO-0001.rvt	V00
16	L1T1-5600-303-CON-ED-INS-MO-0001.rvt	V00
17	L1T1-1330-403-CON-ED-ARQ-MO-0011.rvt	V00
18	L1T1-1330-403-CON-ED-ARQ-MO-0012.rvt	V00

No.	PAQUETE DE TRABAJO DE REFERENCIA	REV.
1	XREF-URBANISMO_CONTEXT_ST03.rvt	
2	XREF-SECONDARY-STRUCTURE-ST03.rvt	

0 2 10m
1:200

METRO BOGOTÁ
GCS Consorcio Consultores PMO Bogotá
CONSORCIO SUPERVISOR PLMB
HEC

DISEÑÓ:
REN ZHENHUA
Licencia de Arq.nivel I (China): 1101735-614

APROBÓ:
DIEGO ERNESTO DUEÑAS
Mat.: 25202-53876 CND

REVISÓ:
CARLOS MAURICIO BARRETO BARBOSA
Mat.: A4012012-14139353

DIBUJÓ:
EQUIPO CHEC

REVISIÓN No.	FECHA	DESCRIPCIÓN	REVISÓ	APROBÓ	APROBACIÓN CLIENTE
V01	01/03/2026	EMITIDO PARA CONSTRUCCIÓN	C.M.B.B	D.E.D	
V00	20/12/2024	REVISIÓN NO OBJETADA - EMITIDO PARA CONSTRUCCIÓN	F.B.R	E.O.M	
VFF	28/06/2024	EMITIDO PARA REVISIÓN Y COMENTARIOS DEL CLIENTE E INTERVENTORÍA - INCLUYE COMENTARIOS /(AJUSTES V3)	F.B.R	E.O.M	
VEE	22/08/2023	EMITIDO PARA REVISIÓN Y COMENTARIOS DEL CLIENTE E INTERVENTORÍA - INCLUYE COMENTARIOS /(AJUSTES V2)	J.E.M	M.B.M	
VDD	18/12/2022	EMITIDO PARA REVISIÓN Y COMENTARIOS DEL CLIENTE E INTERVENTORÍA - INCLUYE COMENTARIOS /(AJUSTES)	J.E.M	M.B.M	
VCC	20/06/2022	EMITIDO PARA REVISIÓN Y COMENTARIOS DEL CLIENTE E INTERVENTORÍA - INCLUYE COMENTARIOS /(ENTREGA 90%)	J.E.M	M.B.M	
VBB	06/12/2021	EMITIDO PARA REVISIÓN Y COMENTARIOS DEL CLIENTE E INTERVENTORÍA	J.E.M	M.B.M	
VA0	30/06/2021	EMITIDO PARA COMENTARIOS INTERNOS - EMISIÓN PRELIMINAR PARA COMENTARIOS	J.E.M	M.B.M	

METRO LÍNEA 1

DIRECTOR DE INTERVENTORÍA:
JAVIER DESCARGA N.
Mat.:25202-68697 CND

METRO LÍNEA 1
CONTRATO DE CONCESIÓN No. 163 DE 2019

PROYECTO PRIMERA LÍNEA DEL METRO DE BOGOTÁ - TRAMO 1

ESPECIALISTA INTERVENTORÍA:
CARLOS ALBERTO HOYOS SOTO
Mat.:A25072000-14251682

FECHA:
MARZO 2026

INFRAESTRUCTURA VIAL
ARQUITECTURA
ESTACIÓN METRO 3 (CARRERA 80)
GENERAL
VISTA EN PLANTA Y 3D - NIVEL ACCESO

PLANCHA No:	ESCALA:	REVISIÓN No.	PLANO No.
L1T1-0000-303-CON-ED-ARQ-PL-0001_05_V01	INDICADA	V01	05 DE 96
ARCHIVO: L1T1-0000-303-CON-ED-ARQ-MO-0001_V00.rvt	FECHA: JUNIO 2021		