L1T1-CON-CAL-FR-0120 - B1 : 1000x707mm

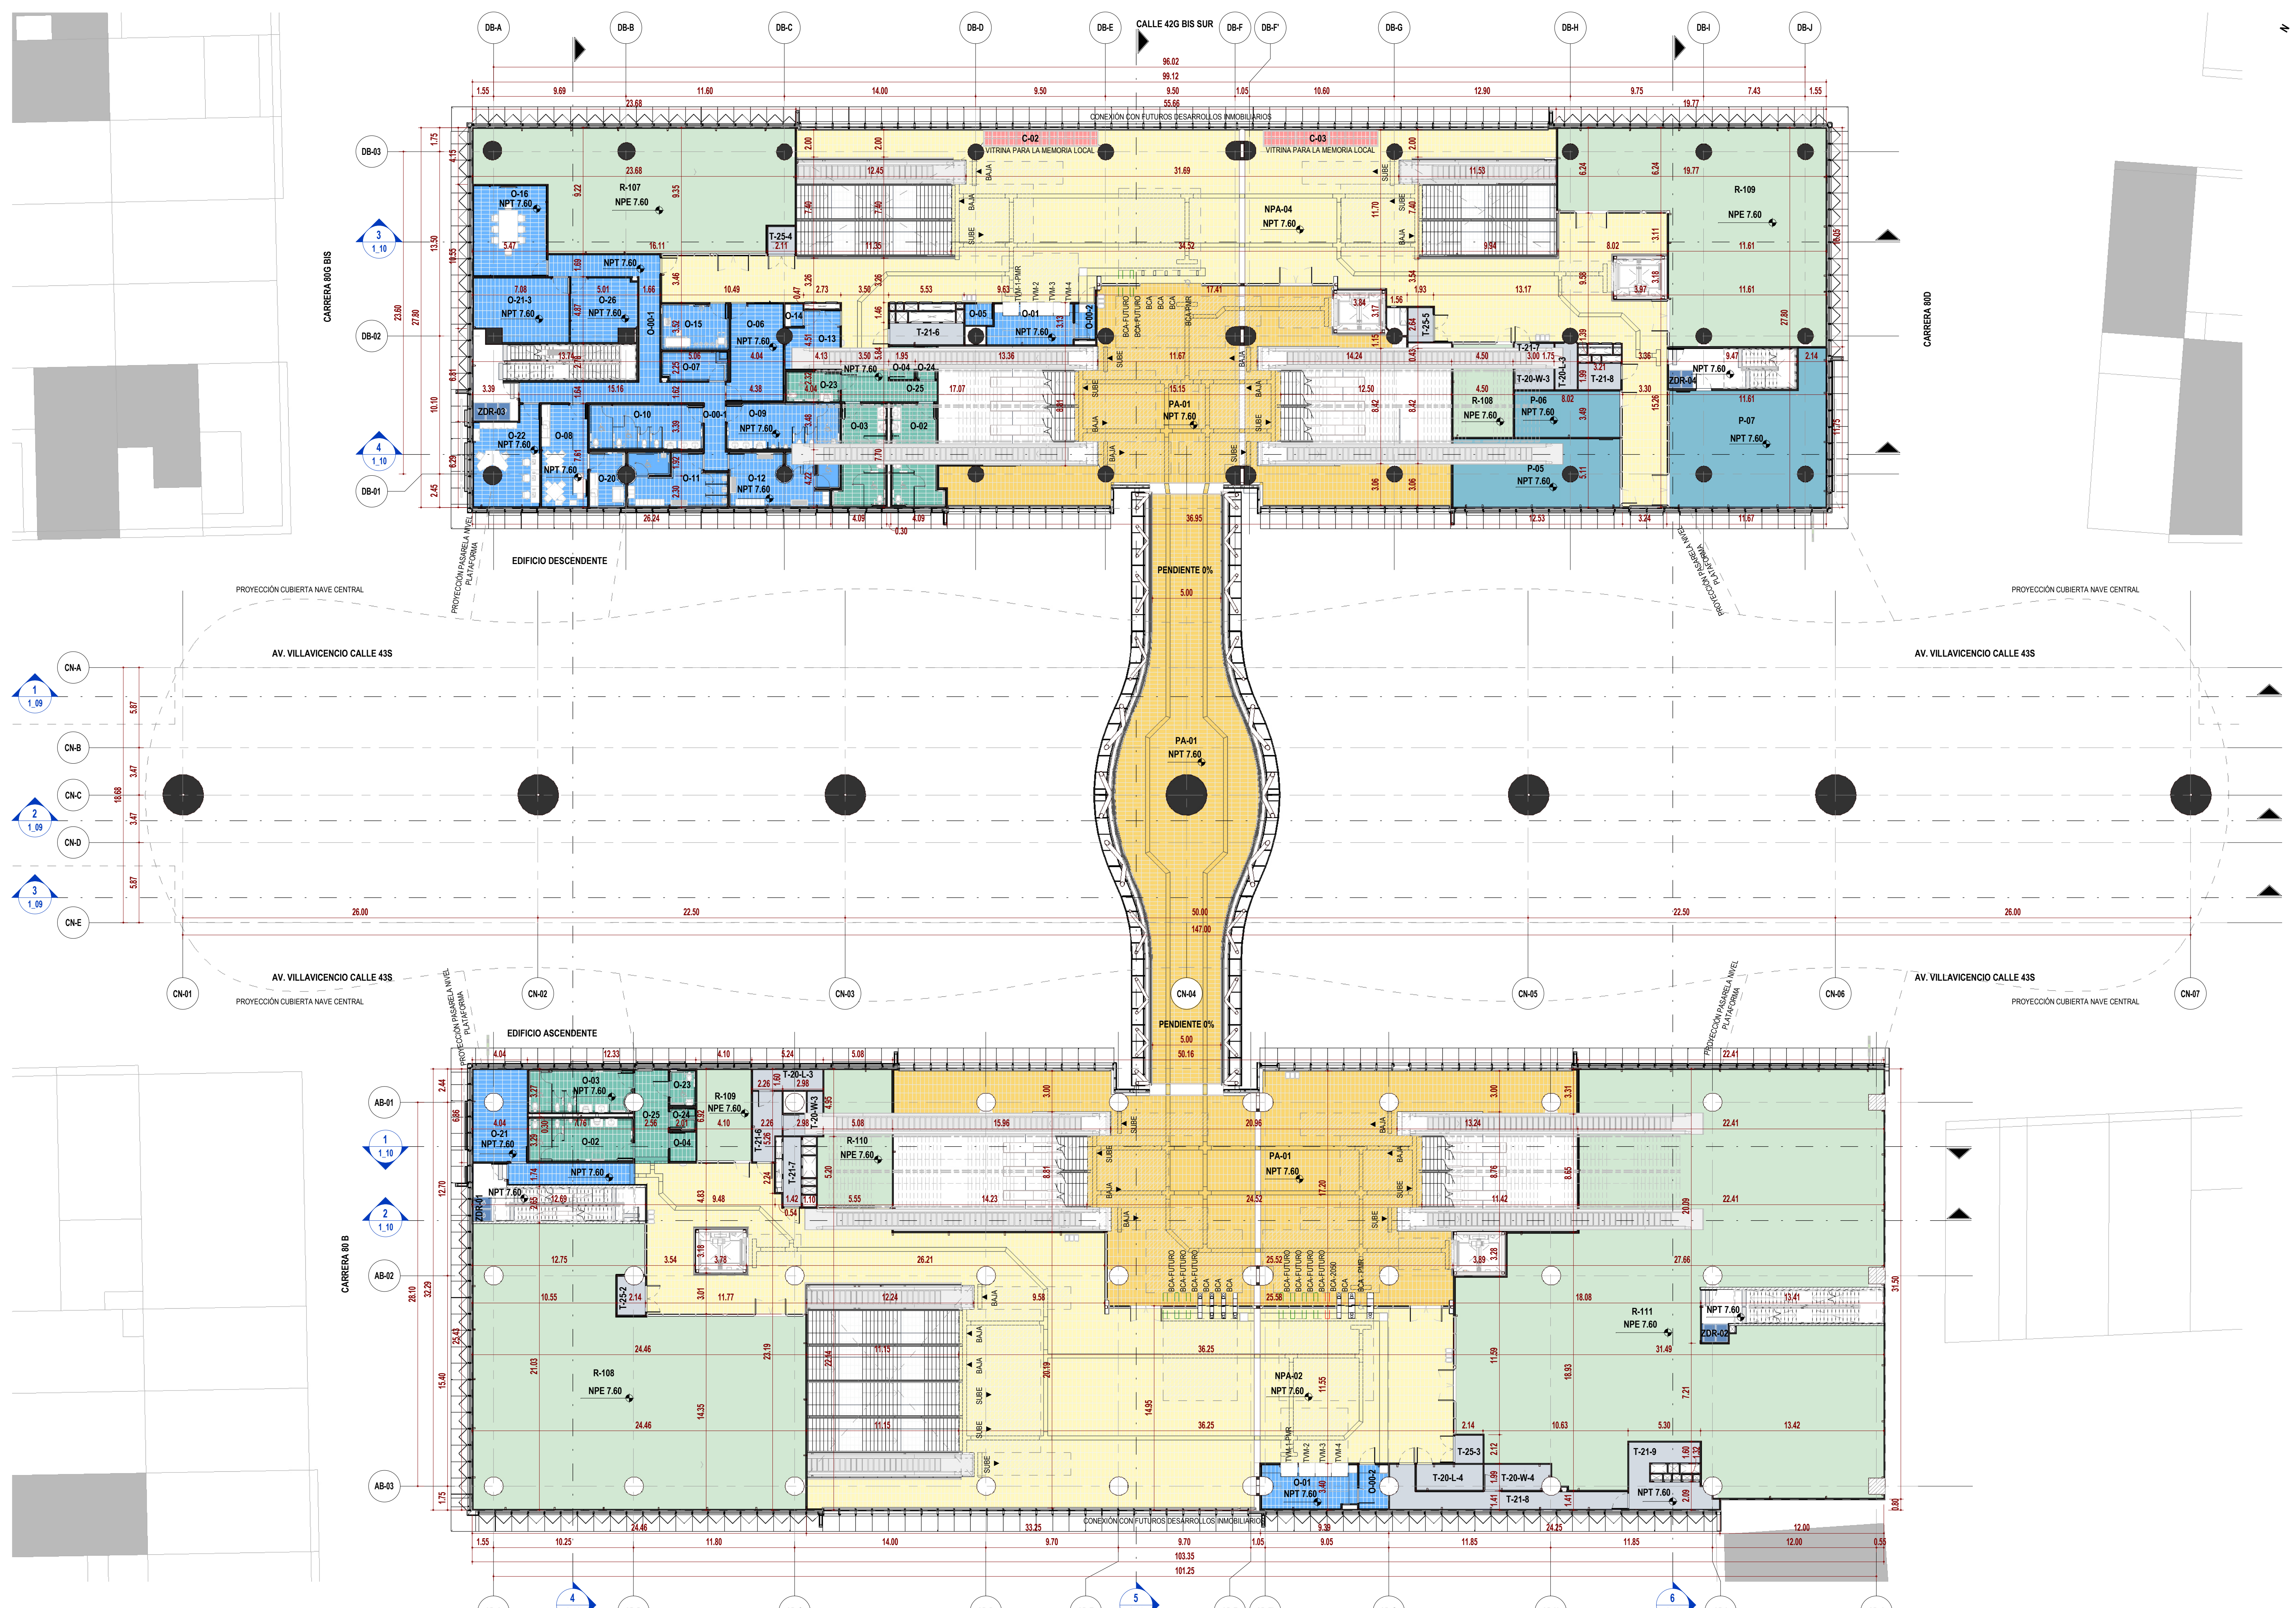

2 NIVEL INTERMEDIO_GENERAL
ESC : 1 : 200

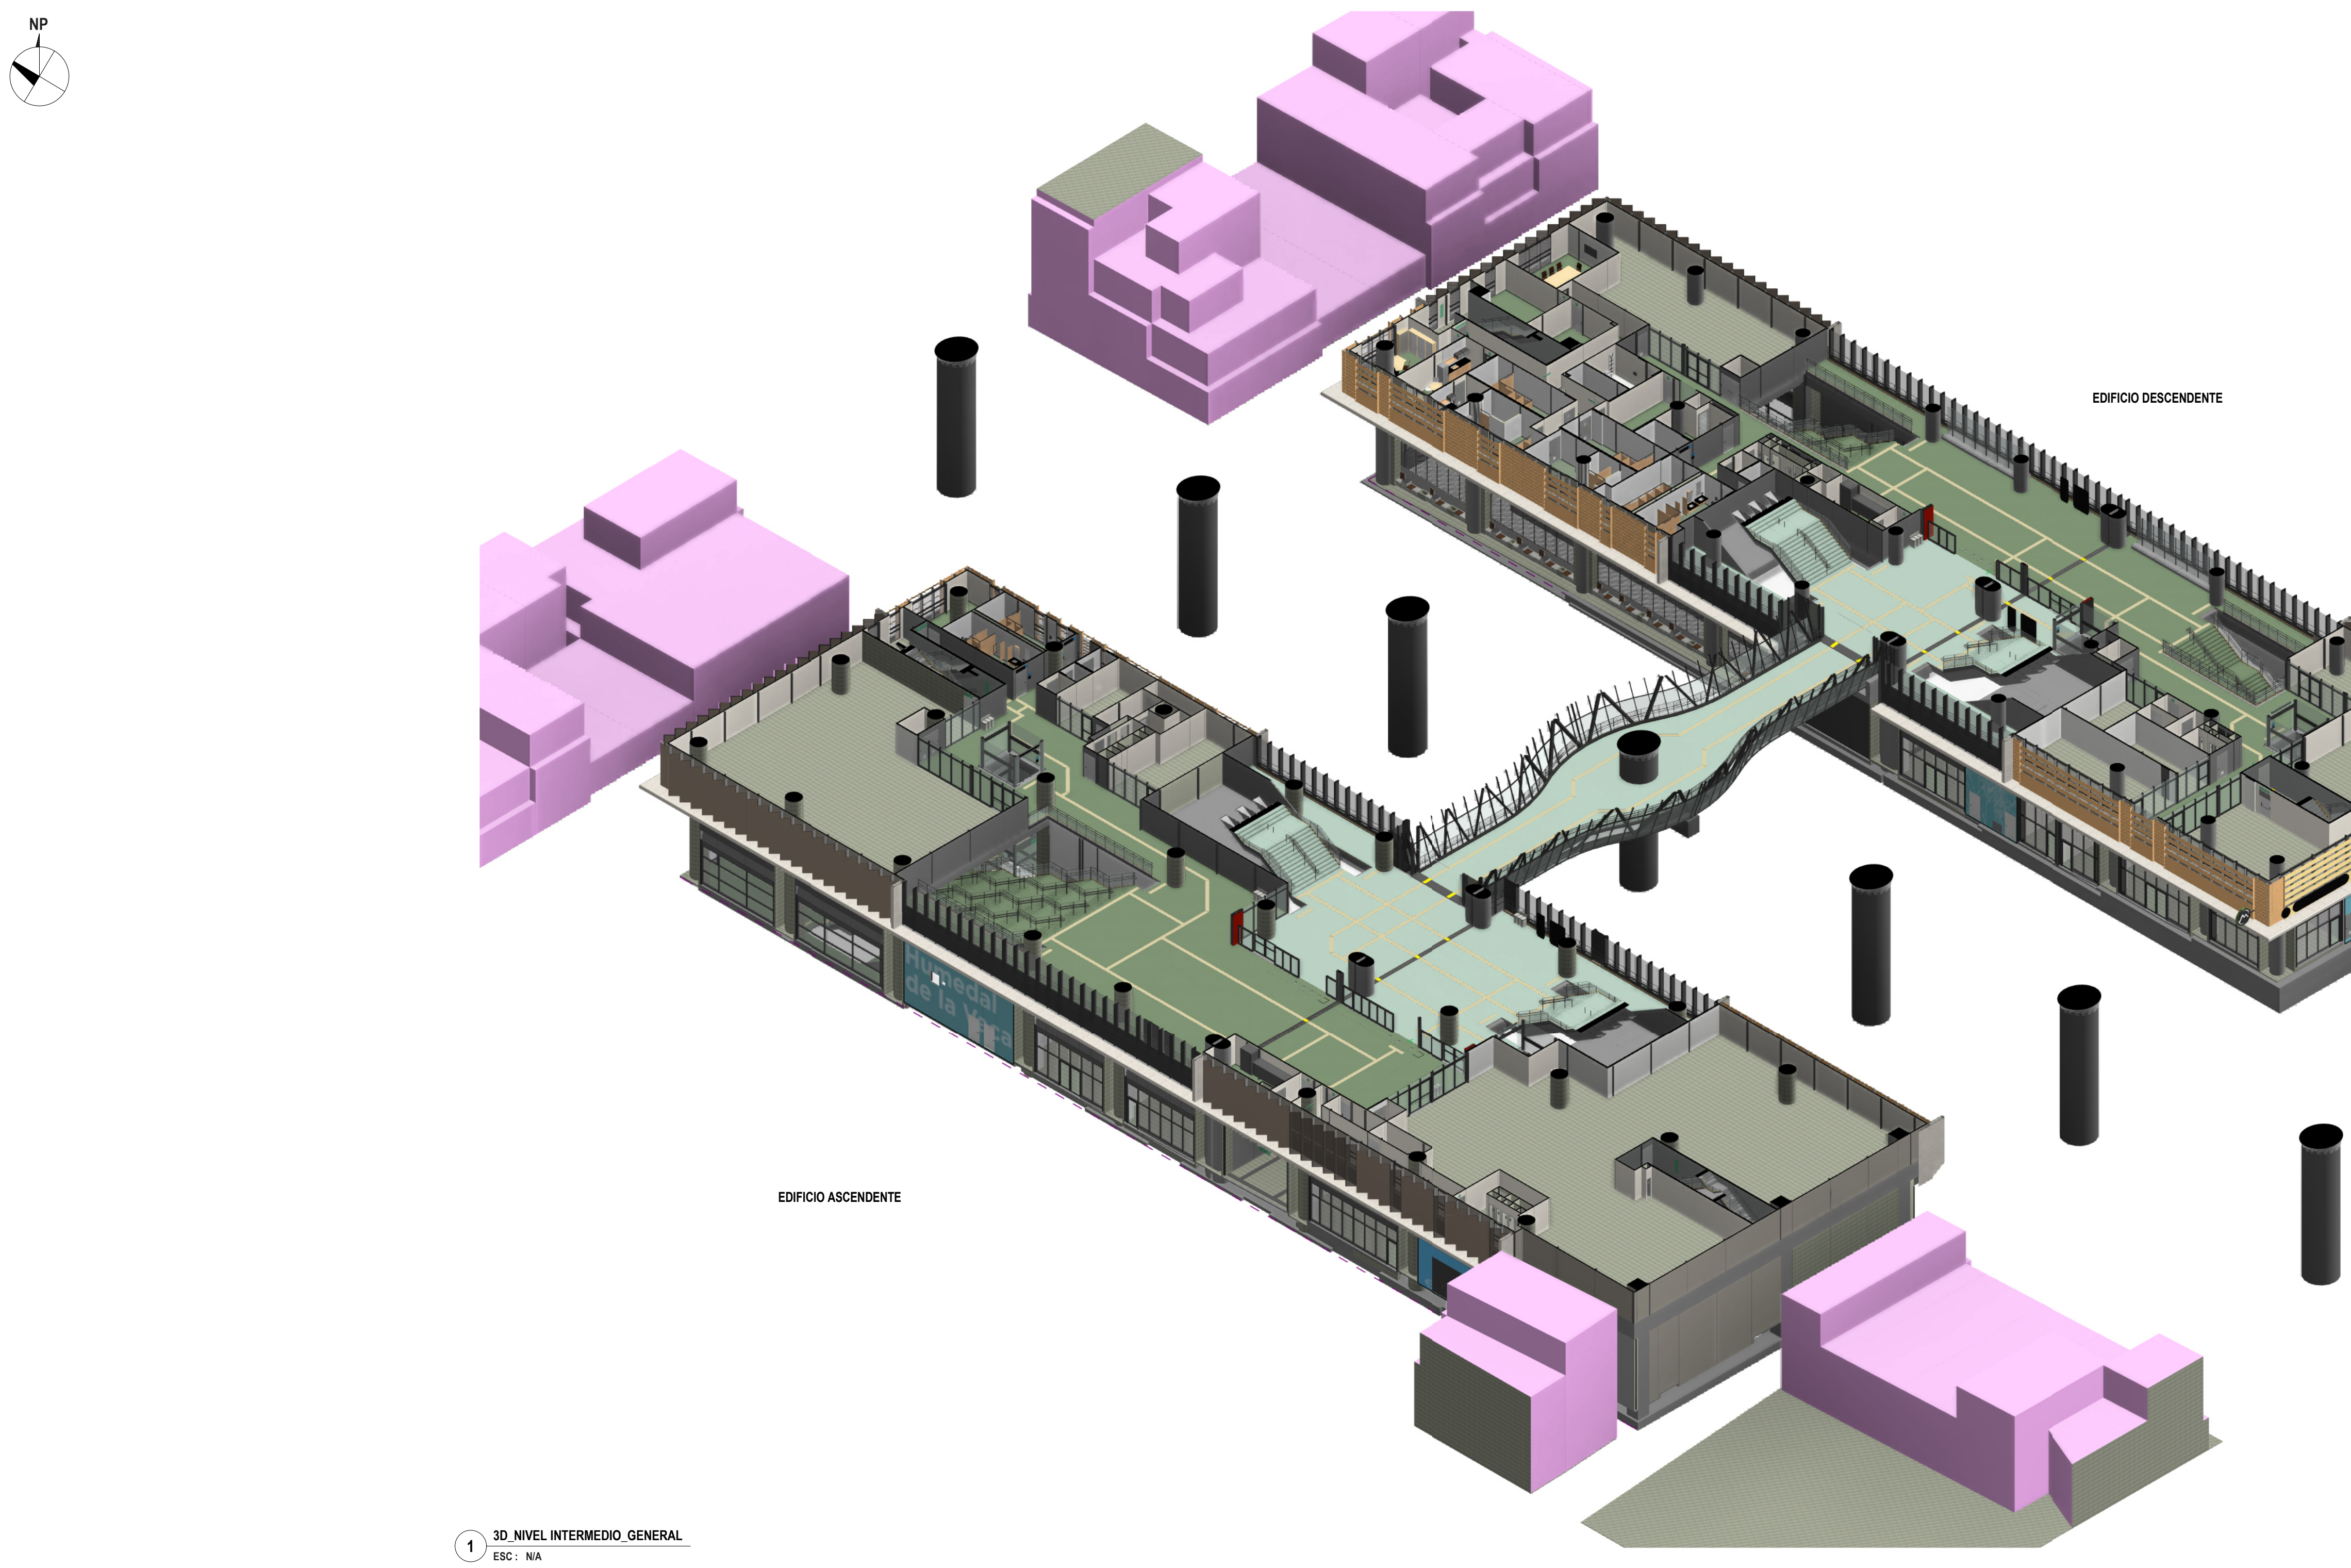

1 3D_NIVEL INTERMEDIO_GENERAL
ESC : N/A

TABLA DE ÁREAS ÚTILES (NIVEL INTERMEDIO)

CÓDIGO	NOMBRE	ÁREA (m²)	DEPARTAMENTO
EDIFICIO ASCENDENTE			
ARQ_PL_02_INTERMEDIO			
NPA-02	ÁREA NO PAGA	721.03	ÁREA NO PAGA
O-00-1	CIRCULACIÓN ÁREAS OPERATIVAS	14.38	ÁREA OPERATIVA
O-00-2	CIRCULACIÓN ÁREAS OPERATIVAS	6.34	ÁREA OPERATIVA
O-01	VENTA AUTOMÁTICA DE BOLETOS	21.47	ÁREA OPERATIVA
O-02	BAÑOS PÚBLICOS DE HOMBRES	23.59	SERVICIO PÚBLICO
O-03	BAÑOS PÚBLICOS DE MUJERES	22.91	SERVICIO PÚBLICO
O-04	CONTROL DE ACCESO BAÑOS PÚBLICOS	4.01	SERVICIO PÚBLICO
O-21	ALMACENAMIENTO DE LA ESTACIÓN	24.96	ÁREA OPERATIVA
O-23	BAÑO PÚBLICO - FAMILIAR	4.60	SERVICIO PÚBLICO
O-24	CUARTO DE LIMPIEZA DE BAÑOS PÚBLICOS	2.89	SERVICIO PÚBLICO
O-25	BAÑO PÚBLICO - CORREDOR OPERACIONAL	16.21	SERVICIO PÚBLICO
PA-01	ÁREA PAGA	464.56	ÁREA PAGA
R-108	SERVICIOS ADICIONALES - ÁREA DE SERVICIO	414.72	SERVICIOS ADICIONALES - ÁREA NO PAGA
R-109	SERVICIOS ADICIONALES - ÁREA DE SERVICIO	26.65	SERVICIOS ADICIONALES - ÁREA NO PAGA
R-110	SERVICIOS ADICIONALES - ÁREA DE SERVICIO	51.69	SERVICIOS ADICIONALES - ÁREA NO PAGA
R-111	SERVICIOS ADICIONALES - ÁREA DE SERVICIO	760.24	SERVICIOS ADICIONALES - ÁREA NO PAGA
T-20-L-3	MEDIDORES (LUZ)	7.65	ÁREA TÉCNICA
T-20-L-4	MEDIDORES (LUZ)	9.06	ÁREA TÉCNICA
T-20-W-3	MEDIDORES (AGUA)	6.33	ÁREA TÉCNICA
T-20-W-4	MEDIDORES (AGUA)	8.57	ÁREA TÉCNICA
T-21-6	ÁREA DE INSPECCIÓN	10.00	ÁREA TÉCNICA
T-21-7	ÁREA DE INSPECCIÓN	6.54	ÁREA TÉCNICA
T-21-8	ÁREA DE INSPECCIÓN	25.29	ÁREA TÉCNICA
T-21-9	ÁREA DE INSPECCIÓN	21.65	ÁREA TÉCNICA
T-25-2	NODO DE ACCESO DE TELECOMUNICACIONES	4.94	ÁREA TÉCNICA
T-25-3	NODO DE ACCESO DE TELECOMUNICACIONES	3.97	ÁREA TÉCNICA
ZDR-01	ZONA DE REFUGIO (PMR)	2.43	ZONA DE REFUGIO
ZDR-02	ZONA DE REFUGIO (PMR)	2.59	ZONA DE REFUGIO
		2689.26	

TABLA DE ÁREAS ÚTILES (NIVEL INTERMEDIO)

CÓDIGO	NOMBRE	ÁREA (m²)	DEPARTAMENTO
EDIFICIO DESCENDENTE			
ARQ_PL_02_INTERMEDIO			
C-02	ÁREAS DE USO CULTURAL	11.92	ÁREA CULTURAL
C-03	ÁREAS DE USO CULTURAL	11.92	ÁREA CULTURAL
NPA-04	ÁREA NO PAGA	681.21	ÁREA NO PAGA
O-00-1	CIRCULACIÓN ÁREAS OPERATIVAS	55.29	ÁREA OPERATIVA
O-00-2	CIRCULACIÓN ÁREAS OPERATIVAS	3.90	ÁREA OPERATIVA
O-01	VENTA AUTOMÁTICA DE BOLETOS	17.95	ÁREA OPERATIVA
O-02	BAÑOS PÚBLICOS DE HOMBRES	25.14	SERVICIO PÚBLICO
O-03	BAÑOS PÚBLICOS DE MUJERES	24.86	SERVICIO PÚBLICO
O-04	CONTROL DE ACCESO BAÑOS PÚBLICOS	4.25	SERVICIO PÚBLICO
O-05	LOCAL DE INFORMACIÓN	3.16	ÁREA OPERATIVA
O-06	OFICINA DEL SUPERVISOR DE LA ESTACIÓN	27.32	ÁREA OPERATIVA
O-07	CUARTO DE LIMPIEZA	10.01	ÁREA OPERATIVA
O-08	SALA DE DESCANSO PARA EMPLEADOS	25.12	ÁREA OPERATIVA
O-09	BAÑOS EMPLEADOS HOMBRES	27.40	ÁREA OPERATIVA
O-10	BAÑOS EMPLEADOS MUJERES	26.75	ÁREA OPERATIVA
O-11	VESTIDORES EMPLEADOS HOMBRES	25.42	ÁREA OPERATIVA
O-12	VESTIDORES EMPLEADOS MUJERES	29.31	ÁREA OPERATIVA
O-13	LOCAL DE POLICÍA	15.10	ÁREA OPERATIVA
O-14	CALABOZO	2.15	ÁREA OPERATIVA
O-15	LOCAL PRIMEROS AUXILIOS	16.41	ÁREA OPERATIVA
O-16	SALA DE REUNIONES	34.94	ÁREA OPERATIVA
O-20	SALA DE LACTANCIA	9.95	ÁREA OPERATIVA
O-21-3	ALMACENAMIENTO DE LA ESTACIÓN	30.80	ÁREA OPERATIVA
O-22	OFICINA DE MANTENIMIENTO	30.14	ÁREA OPERATIVA
O-23	BAÑO PÚBLICO - FAMILIAR	8.29	SERVICIO PÚBLICO
O-24	CUARTO DE LIMPIEZA DE BAÑOS PÚBLICOS	3.34	SERVICIO PÚBLICO
O-25	BAÑO PÚBLICO - CORREDOR OPERACIONAL	13.04	SERVICIO PÚBLICO
O-26	ALMACENAMIENTO DE BASURAS METRO	21.58	ÁREA OPERATIVA
P-05	BIBLIOMETRO	55.49	ÁREA PÚBLICA
P-06	ESPACIO IPES (INSTITUTO PARA LA ECONOMÍA SOCIAL)	25.83	ÁREA PÚBLICA
P-07	SALÓN MÚLTIPLE EMB	100.85	ÁREA PÚBLICA
PA-01	ÁREA PAGA	288.83	ÁREA PAGA
R-107	SERVICIOS ADICIONALES - ÁREA DE SERVICIO	178.19	SERVICIOS ADICIONALES - ÁREA NO PAGA
R-108	SERVICIOS ADICIONALES - ÁREA DE SERVICIO	29.48	SERVICIOS ADICIONALES - ÁREA NO PAGA
R-109	SERVICIOS ADICIONALES - ÁREA DE SERVICIO	225.63	SERVICIOS ADICIONALES - ÁREA NO PAGA
T-20-L-3	MEDIDORES (LUZ)	5.49	ÁREA TÉCNICA
T-20-W-3	MEDIDORES (AGUA)	4.45	ÁREA TÉCNICA
T-21-6	ÁREA DE INSPECCIÓN	8.37	ÁREA TÉCNICA
T-21-7	ÁREA DE INSPECCIÓN	4.91	ÁREA TÉCNICA
T-21-8	ÁREA DE INSPECCIÓN	5.79	ÁREA TÉCNICA
T-25-4	NODO DE ACCESO DE TELECOMUNICACIONES	3.92	ÁREA TÉCNICA
T-25-5	NODO DE ACCESO DE TELECOMUNICACIONES	4.52	ÁREA TÉCNICA
ZDR-03	ZONA DE REFUGIO (PMR)	3.66	ZONA DE REFUGIO
ZDR-04	ZONA DE REFUGIO (PMR)	2.43	ZONA DE REFUGIO
		2144.53	
NAVE CENTRAL			
ARQ_PL_02_INTERMEDIO			
PA-01	ÁREA PAGA	278.11	ÁREA PAGA
		278.11	
TOTAL NIVEL INTERMEDIO		5111.90	

TABLA DE ÁREAS ÚTILES POR DEPARTAMENTO (NIVEL INTERMEDIO)

DEPARTAMENTO	ÁREA (m²)
EDIFICIO ASCENDENTE	
ARQ_PL_02_INTERMEDIO	
SERVICIO PÚBLICO	74.21
SERVICIOS ADICIONALES - ÁREA NO PAGA	1253.30
ZONA DE REFUGIO	5.02
ÁREA NO PAGA	721.03
ÁREA OPERATIVA	67.15
ÁREA PAGA	464.56
ÁREA TÉCNICA	103.99
EDIFICIO DESCENDENTE	
ARQ_PL_02_INTERMEDIO	
SERVICIO PÚBLICO	78.92
SERVICIOS ADICIONALES - ÁREA NO PAGA	433.30
ZONA DE REFUGIO	6.09
ÁREA CULTURAL	23.84
ÁREA NO PAGA	681.21
ÁREA OPERATIVA	412.71
ÁREA PAGA	288.83
ÁREA PÚBLICA	182.18
ÁREA TÉCNICA	37.45
NAVE CENTRAL	
ARQ_PL_02_INTERMEDIO	
ÁREA PAGA	278.11
TOTAL NIVEL INTERMEDIO	5111.90

LOCALIZACIÓN

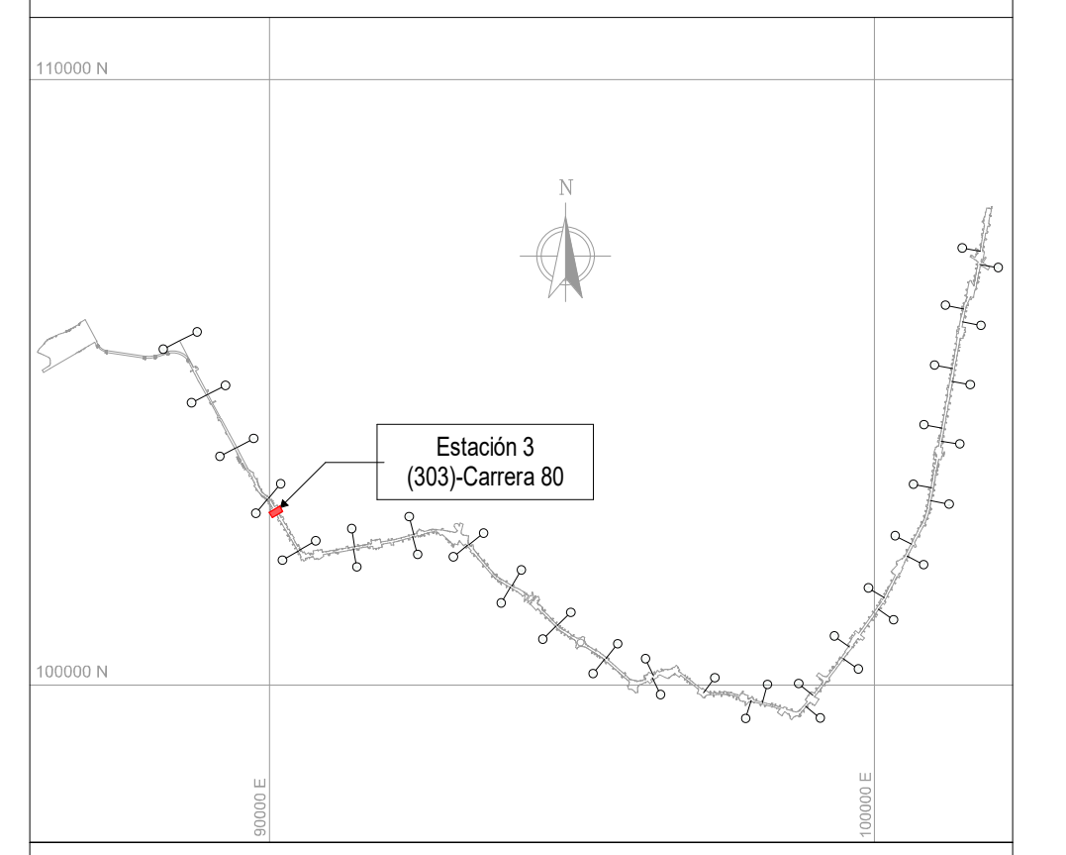

NOTAS

01 TODAS LAS DIMENSIONES ESTÁN CONFIGURADAS EN METROS A MENOS QUE SE INDIQUE UNA UNIDAD DE MEDIDA DIFERENTE.

02 TODAS LAS MEDIDAS, UBICACIÓN Y NIVELES DEBEN VERIFICARSE EN EL LUGAR DE CONSTRUCCIÓN.

03 EL NIVEL DE ACCESO AL EDIFICIO PL 01 CORRESPONDE AL +0,00 DE LA ESTACIÓN Y REFERENCIA AL NIVEL 2547.75 M.S.N.M.

04 LOS NOMBRES ESPECÍFICOS DE LAS ÁREAS PUEDEN SER CONSULTADAS EN EL PLANO NO. 3 Ó EN LAS VISTAS EN PLANTA.

05 LOS COLORES QUE SE MUESTRAN EN LOS PLANOS COMO PROYECCIÓN DE ELEMENTOS ARQUITECTÓNICOS COMO CUBIERTAS FACHADAS MUROS ETC. NO REPRESENTAN LA MATERIALIDAD Y REALIDAD DE ACABADOS DEL PROYECTO, SOLO SON INDICATIVOS PARA REALIZAR UNA CORRECTA LECTURA DE LA PLANIMETRÍA.

06 LAS ESCALERAS ELÉCTRICAS INDICAN SU SENTIDO CON LA SIGUIENTE NOMENCLATURA: "SUBE" Y "BAJA".

07 SE DEBEN REVISAR LOS NIVELES ESTRUCTURALES PARA NIVEL DE ACCESO PL_01 Y SUBNIVELES, PL_02 (INTERMEDIO), PL_03 (PLATAFORMA) CON LA PLANIMETRÍA DE PLACAS ESTRUCTURALES EN LOS ENTREGABLES L1T1-1300-403-CON-ED-EST-PL-0038, 39, 78, 79, 82, 83 RESPECTIVAMENTE. EL NIVEL ESTRUCTURAL (NE) REFERENCIA LOS ESPACIOS DONDE SE DEBE ACONDICIONAR EL ACABADO DE PISO SEGÚN CORRESPONDA, CON LOS NIVELES DE PISO TERMINADO (NPT). LOS NIVELES PROYECTADOS DE EMPATE (NPE) EN LAS ÁREAS DE SERVICIOS ADICIONALES, REFERENCIAN LA ADECUACIÓN DE LOS DESNIVELES EN ESTAS ÁREAS; QUEDA COMO RESPONSABILIDAD DEL LOCATARIO DEFINIR Y ACONDICIONAR ESTE ACABADO DE PISO (NPE) EN LÍNEA CON EL NIVEL (NPT) DE ESPACIOS COLINDANTES. EL NIVEL ESTRUCTURAL (NE) SE ENCUENTRA A (- 0.10M) POR DEBAJO DE LOS NIVELES DE PISO TERMINADO (NPT) Y LOS NIVELES PROYECTADOS DE EMPATE (NPE) MARCADOS EN LA PLANIMETRÍA.

- ARQ_PL_00 = SÓTANO	/ NPT -8.50	- ARQ_PL_00.11 = ACCESO	/ NPT -0.95
- ARQ_PL_00.1 = ACCESO	/ NPT -2.20	- ARQ_PL_00.12 = ACCESO	/ NPT -0.75
- ARQ_PL_00.2 = ACCESO	/ NPT -2.10	- ARQ_PL_00.13 = ACCESO	/ NPT -0.55
- ARQ_PL_00.3 = ACCESO	/ NPT -1.95	- ARQ_PL_00.14 = ACCESO	/ NPT -0.45
- ARQ_PL_00.4 = ACCESO	/ NPT -1.80	- ARQ_PL_00.15 = ACCESO	/ NPT -0.35
- ARQ_PL_00.5 = ACCESO	/ NPT -1.75	- ARQ_PL_01 = ACCESO	/ NPT 0.00
- ARQ_PL_00.6 = ACCESO	/ NPT -1.65	- ARQ_PL_02 = INTERMEDIO	/ NPT 7.60
- ARQ_PL_00.7 = ACCESO	/ NPT -1.55	- ARQ_PL_02.2 = TOPE DE RIEL	/ NPT 15.20
- ARQ_PL_00.8 = ACCESO	/ NPT -1.45	- ARQ_PL_03 = PLATAFORMA	/ NPT 16.34
- ARQ_PL_00.9 = ACCESO	/ NPT -1.25	- ARQ_PL_04 = CUBIERTA EDIFICACIONES	/ NPT 22.94
- ARQ_PL_00.10 = ACCESO	/ NPT -1.15	- ARQ_PL_05 = CUBIERTA NAVE CENTRAL	/ NPT 25.59

CONVENCIONES

- - - -	LÍMITE DE INTERVENCIÓN
- - - -	HUELLA APÉNDICE TÉCNICO
▬	MURO DIVISORIO
— — —	PROYECCIÓN NIVEL SUPERIOR
🟩	SERVICIOS ADICIONALES - ÁREA NO PAGA
🟩	SERVICIOS ADICIONALES - ÁREA PAGA
🟩	SERVICIO PÚBLICO
🟦	ZONA DE REFUGIO
🟥	ÁREA CULTURAL
🟨	ÁREA NO PAGA
🟦	ÁREA OPERATIVA
🟧	ÁREA PAGA
🟦	ÁREA PÚBLICA
⬜	ÁREA TÉCNICA

No.	PLANOS DE REFERENCIA	REV.

No.	MODELO BIM DE REFERENCIA	REV.
1	L1T1-1100-203-CON-ED-EST-MO-0001.rvt	V00
2	L1T1-1100-204-CON-ED-EST-MO-0001.rvt	V00
3	L1T1-1100-303-CON-ED-EST-MO-0001.rvt	V00
4	L1T1-1150-203-CON-ED-EST-MO-0001.rvt	V00
5	L1T1-1150-204-CON-ED-EST-MO-0001.rvt	V00
6	L1T1-1150-303-CON-ED-EST-MO-0001.rvt	V00
7	L1T1-1200-303-CON-ED-EST-MO-0001.rvt	V00
8	L1T1-1300-403-CON-ED-EST-MO-0001.rvt	V00
9	L1T1-1300-403-CON-ED-EST-MO-0002.rvt	V00
10	L1T1-1310-403-CON-ED-EST-MO-0001.rvt	V00
11	L1T1-1410-403-CON-ED-MEC-MO-0001.rvt	V00
12	L1T1-1420-403-CON-ED-MEC-MO-0001.rvt	V00
13	L1T1-5160-303-CON-ED-EST-MO-0001.rvt	V00
14	L1T1-5160-303-CON-ED-ARQ-MO-0001.rvt	V00
15	L1T1-5300-303-CON-ED-MEC-MO-0001.rvt	V00
16	L1T1-5600-303-CON-ED-INS-MO-0001.rvt	V00
17	L1T1-1330-403-CON-ED-ARQ-MO-0011.rvt	V00
18	L1T1-1330-403-CON-ED-ARQ-MO-0012.rvt	V00

No.	PAQUETE DE TRABAJO DE REFERENCIA	REV.
1	XREF-URBANISMO_CONTEXT_ST03.rvt	
2	XREF-SECONDARY-STRUCTURE-ST03.rvt	

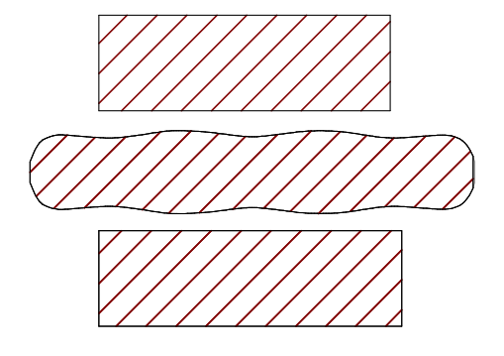

PLANO CLAVE ESTACIÓN 3

VÁLIDO PARA CONSTRUCCIÓN
01-03-26

0 2 10m
1:200

METRO BOGOTÁ
GCS Consorcio Consultores PMO Bogotá
CONSORCIO SUPERVISOR PLMB
CHEC

DISEÑÓ:
REN ZHENHUA
Licencia de Arq.nivel I (China): 1101735-614

APROBÓ:
DIEGO ERNESTO DUEÑAS
Mat.: 25202-53876 CND

REVISÓ:
CARLOS MAURICIO BARRETO BARBOSA
Mat.: A4012012-14139353

DIBUJÓ:
EQUIPO CHEC

REVISIÓN No.	FECHA	DESCRIPCIÓN	REVISÓ	APROBÓ	APROBACIÓN CLIENTE
V01	01/03/2026	EMITIDO PARA CONSTRUCCIÓN	C.M.B.B	D.E.D	
V00	20/12/2024	REVISIÓN NO OBJETADA - EMITIDO PARA CONSTRUCCIÓN	F.B.R	E.O.M	
VFF	28/06/2024	EMITIDO PARA REVISIÓN Y COMENTARIOS DEL CLIENTE E INTERVENTORÍA - INCLUYE COMENTARIOS /(AJUSTES V3)	F.B.R	E.O.M	
VEE	22/08/2023	EMITIDO PARA REVISIÓN Y COMENTARIOS DEL CLIENTE E INTERVENTORÍA - INCLUYE COMENTARIOS /(AJUSTES V2)	J.E.M	M.B.M	
VDD	18/12/2022	EMITIDO PARA REVISIÓN Y COMENTARIOS DEL CLIENTE E INTERVENTORÍA - INCLUYE COMENTARIOS /(AJUSTES)	J.E.M	M.B.M	
VCC	20/06/2022	EMITIDO PARA REVISIÓN Y COMENTARIOS DEL CLIENTE E INTERVENTORÍA - INCLUYE COMENTARIOS /(ENTREGA 90%)	J.E.M	M.B.M	
VBB	06/12/2021	EMITIDO PARA REVISIÓN Y COMENTARIOS DEL CLIENTE E INTERVENTORÍA	J.E.M	M.B.M	
VA0	30/06/2021	EMITIDO PARA COMENTARIOS INTERNOS - EMISIÓN PRELIMINAR PARA COMENTARIOS	J.E.M	M.B.M	

METRO LÍNEA 1

METRO LÍNEA 1
CONTRATO DE CONCESIÓN No. 163 DE 2019

PROYECTO PRIMERA LÍNEA DEL METRO DE BOGOTÁ - TRAMO 1

DIRECTOR DE INTERVENTORÍA:
JAVIER DESCARGA N.
Mat.:25202-68697 CND

ESPECIALISTA INTERVENTORÍA:
CARLOS ALBERTO HOYOS SOTO
Mat.:A25072000-14251682

FECHA:
MARZO 2026

INFRAESTRUCTURA VIAL

ARQUITECTURA

ESTACIÓN METRO 3 (CARRERA 80)
GENERAL
VISTA EN PLANTA Y 3D - NIVEL INTERMEDIO

PLANCHA No: L1T1-0000-303-CON-ED-ARQ-PL-0001_06_V01
ARCHIVO: L1T1-0000-303-CON-ED-ARQ-MO-0001_V00.rvt
ESCALA: INDICADA
FECHA: JUNIO 2021
REVISIÓN No. V01
PLANO No. 06 DE 96