L1T1-CON-CAL-FR-0120 - B1 : 1000x707mm

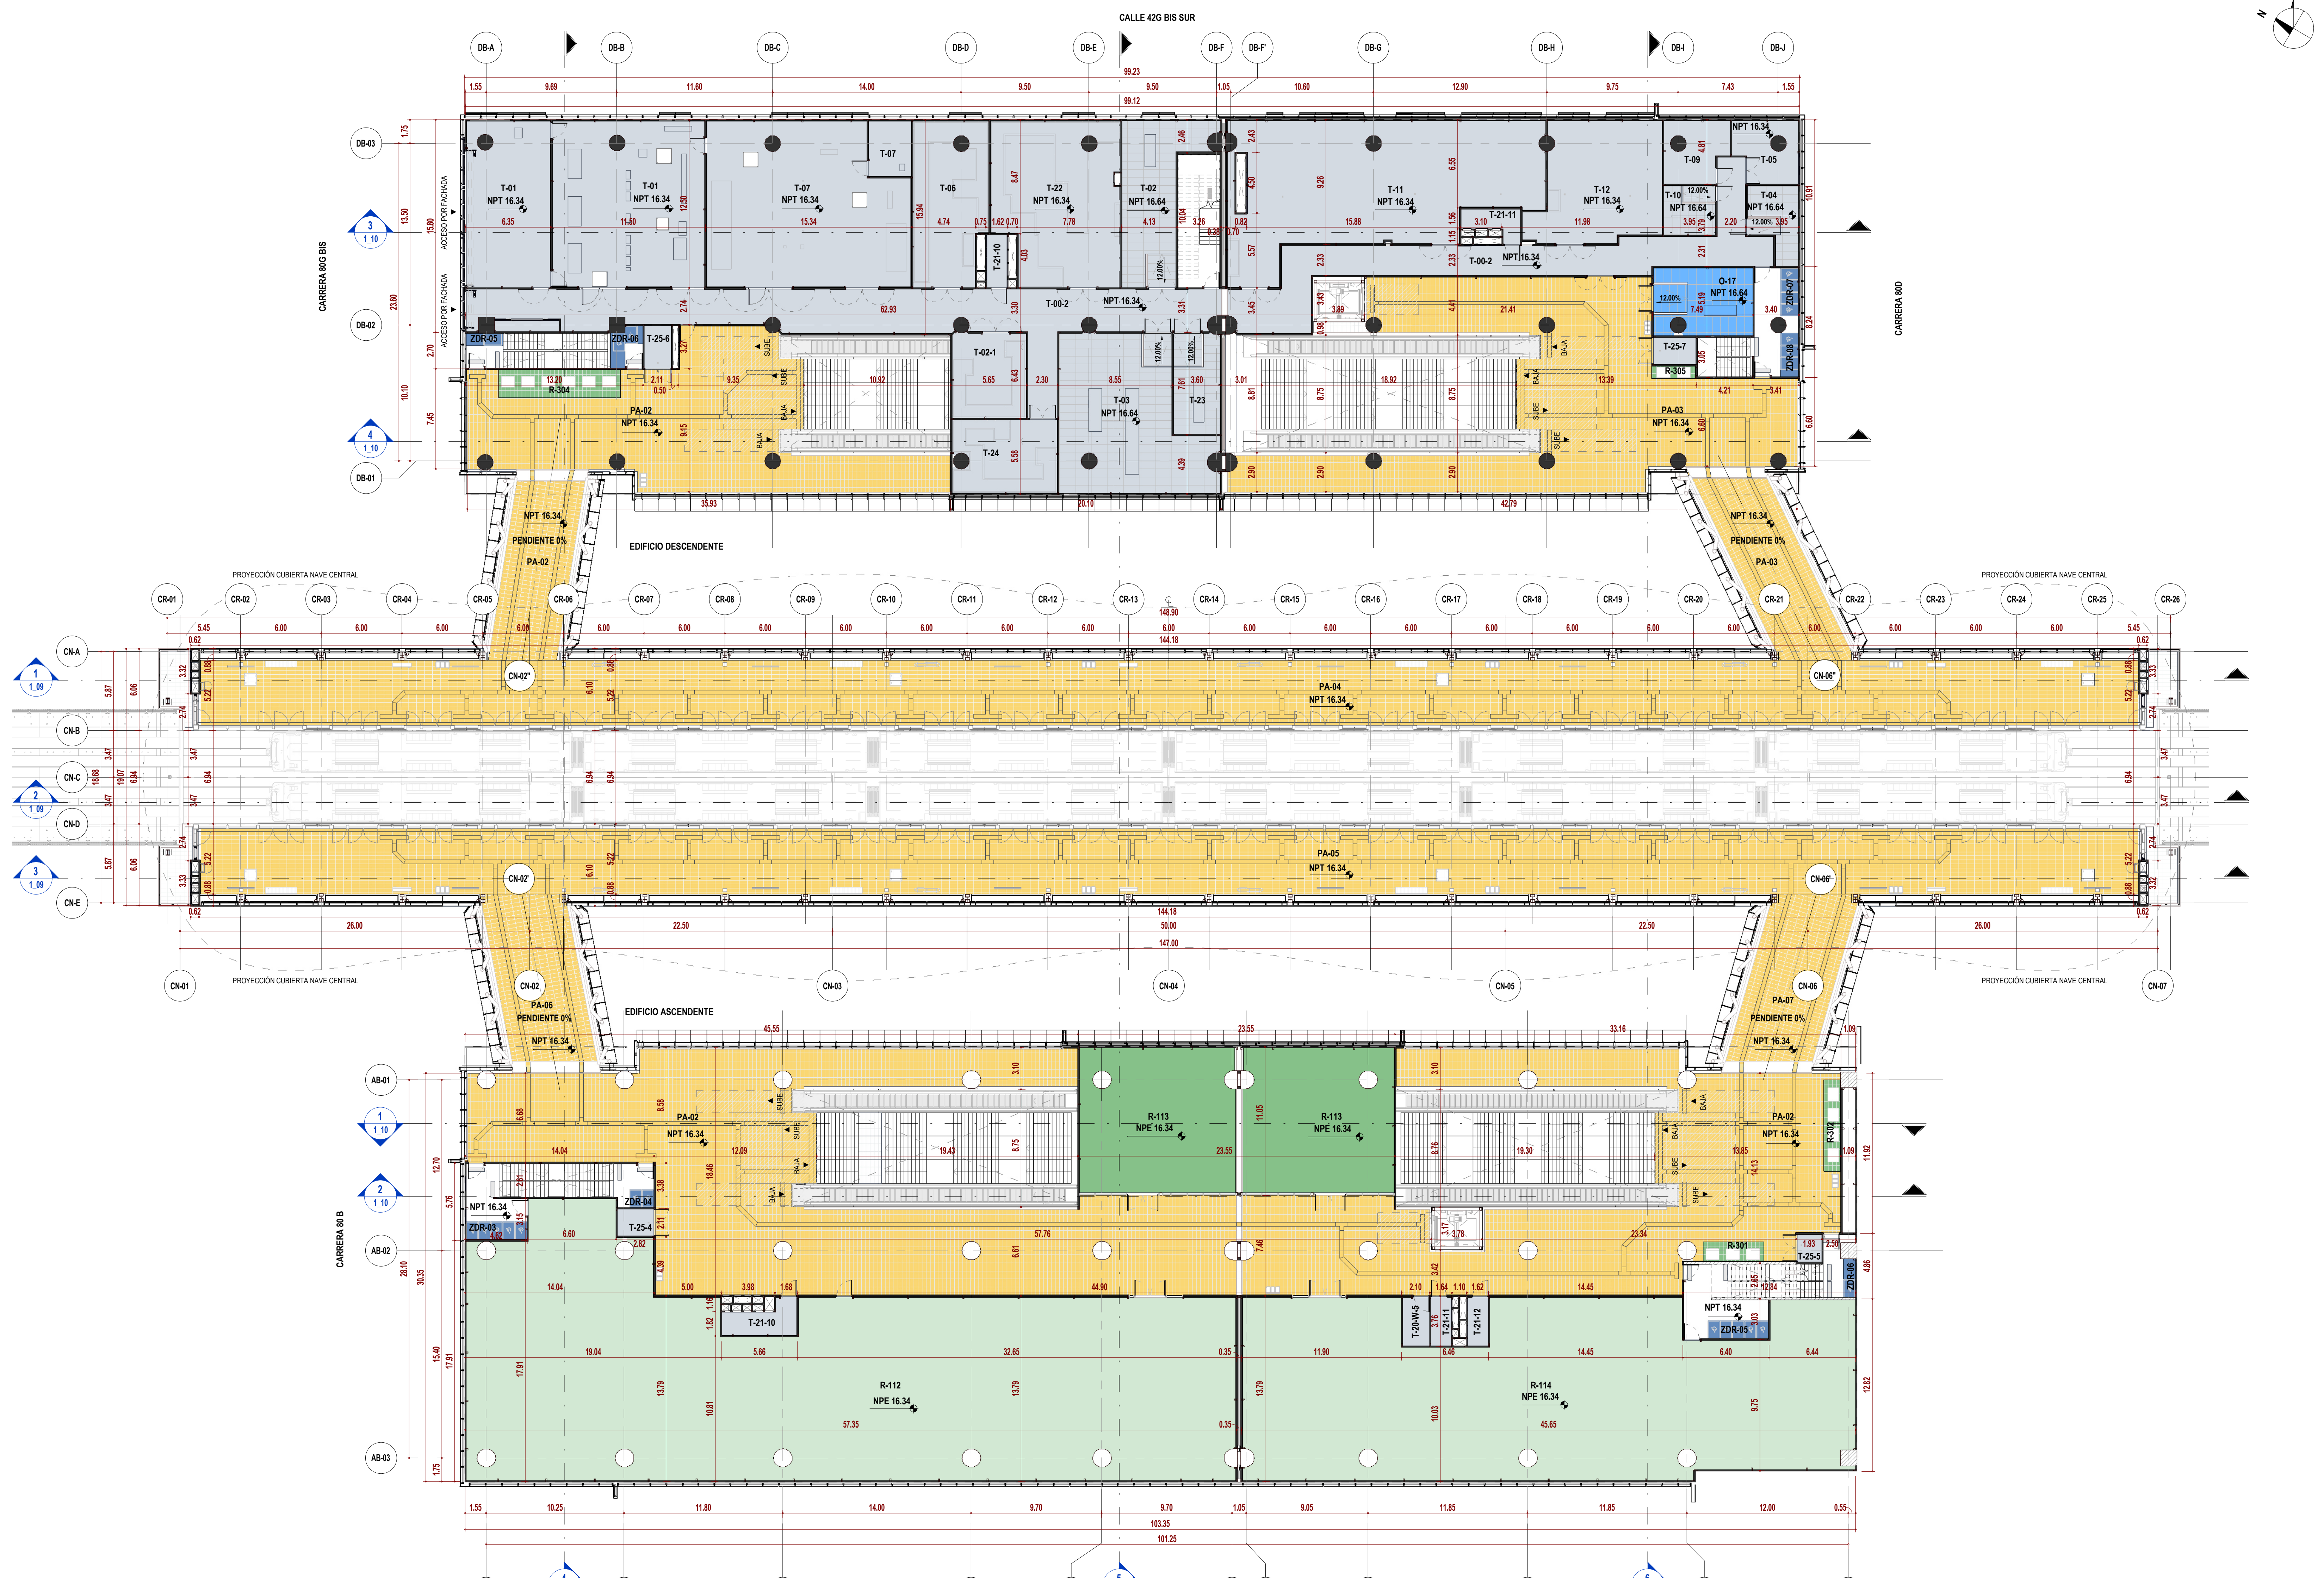

2 **NIVEL PLATAFORMA_GENERAL**
ESC : 1 : 200

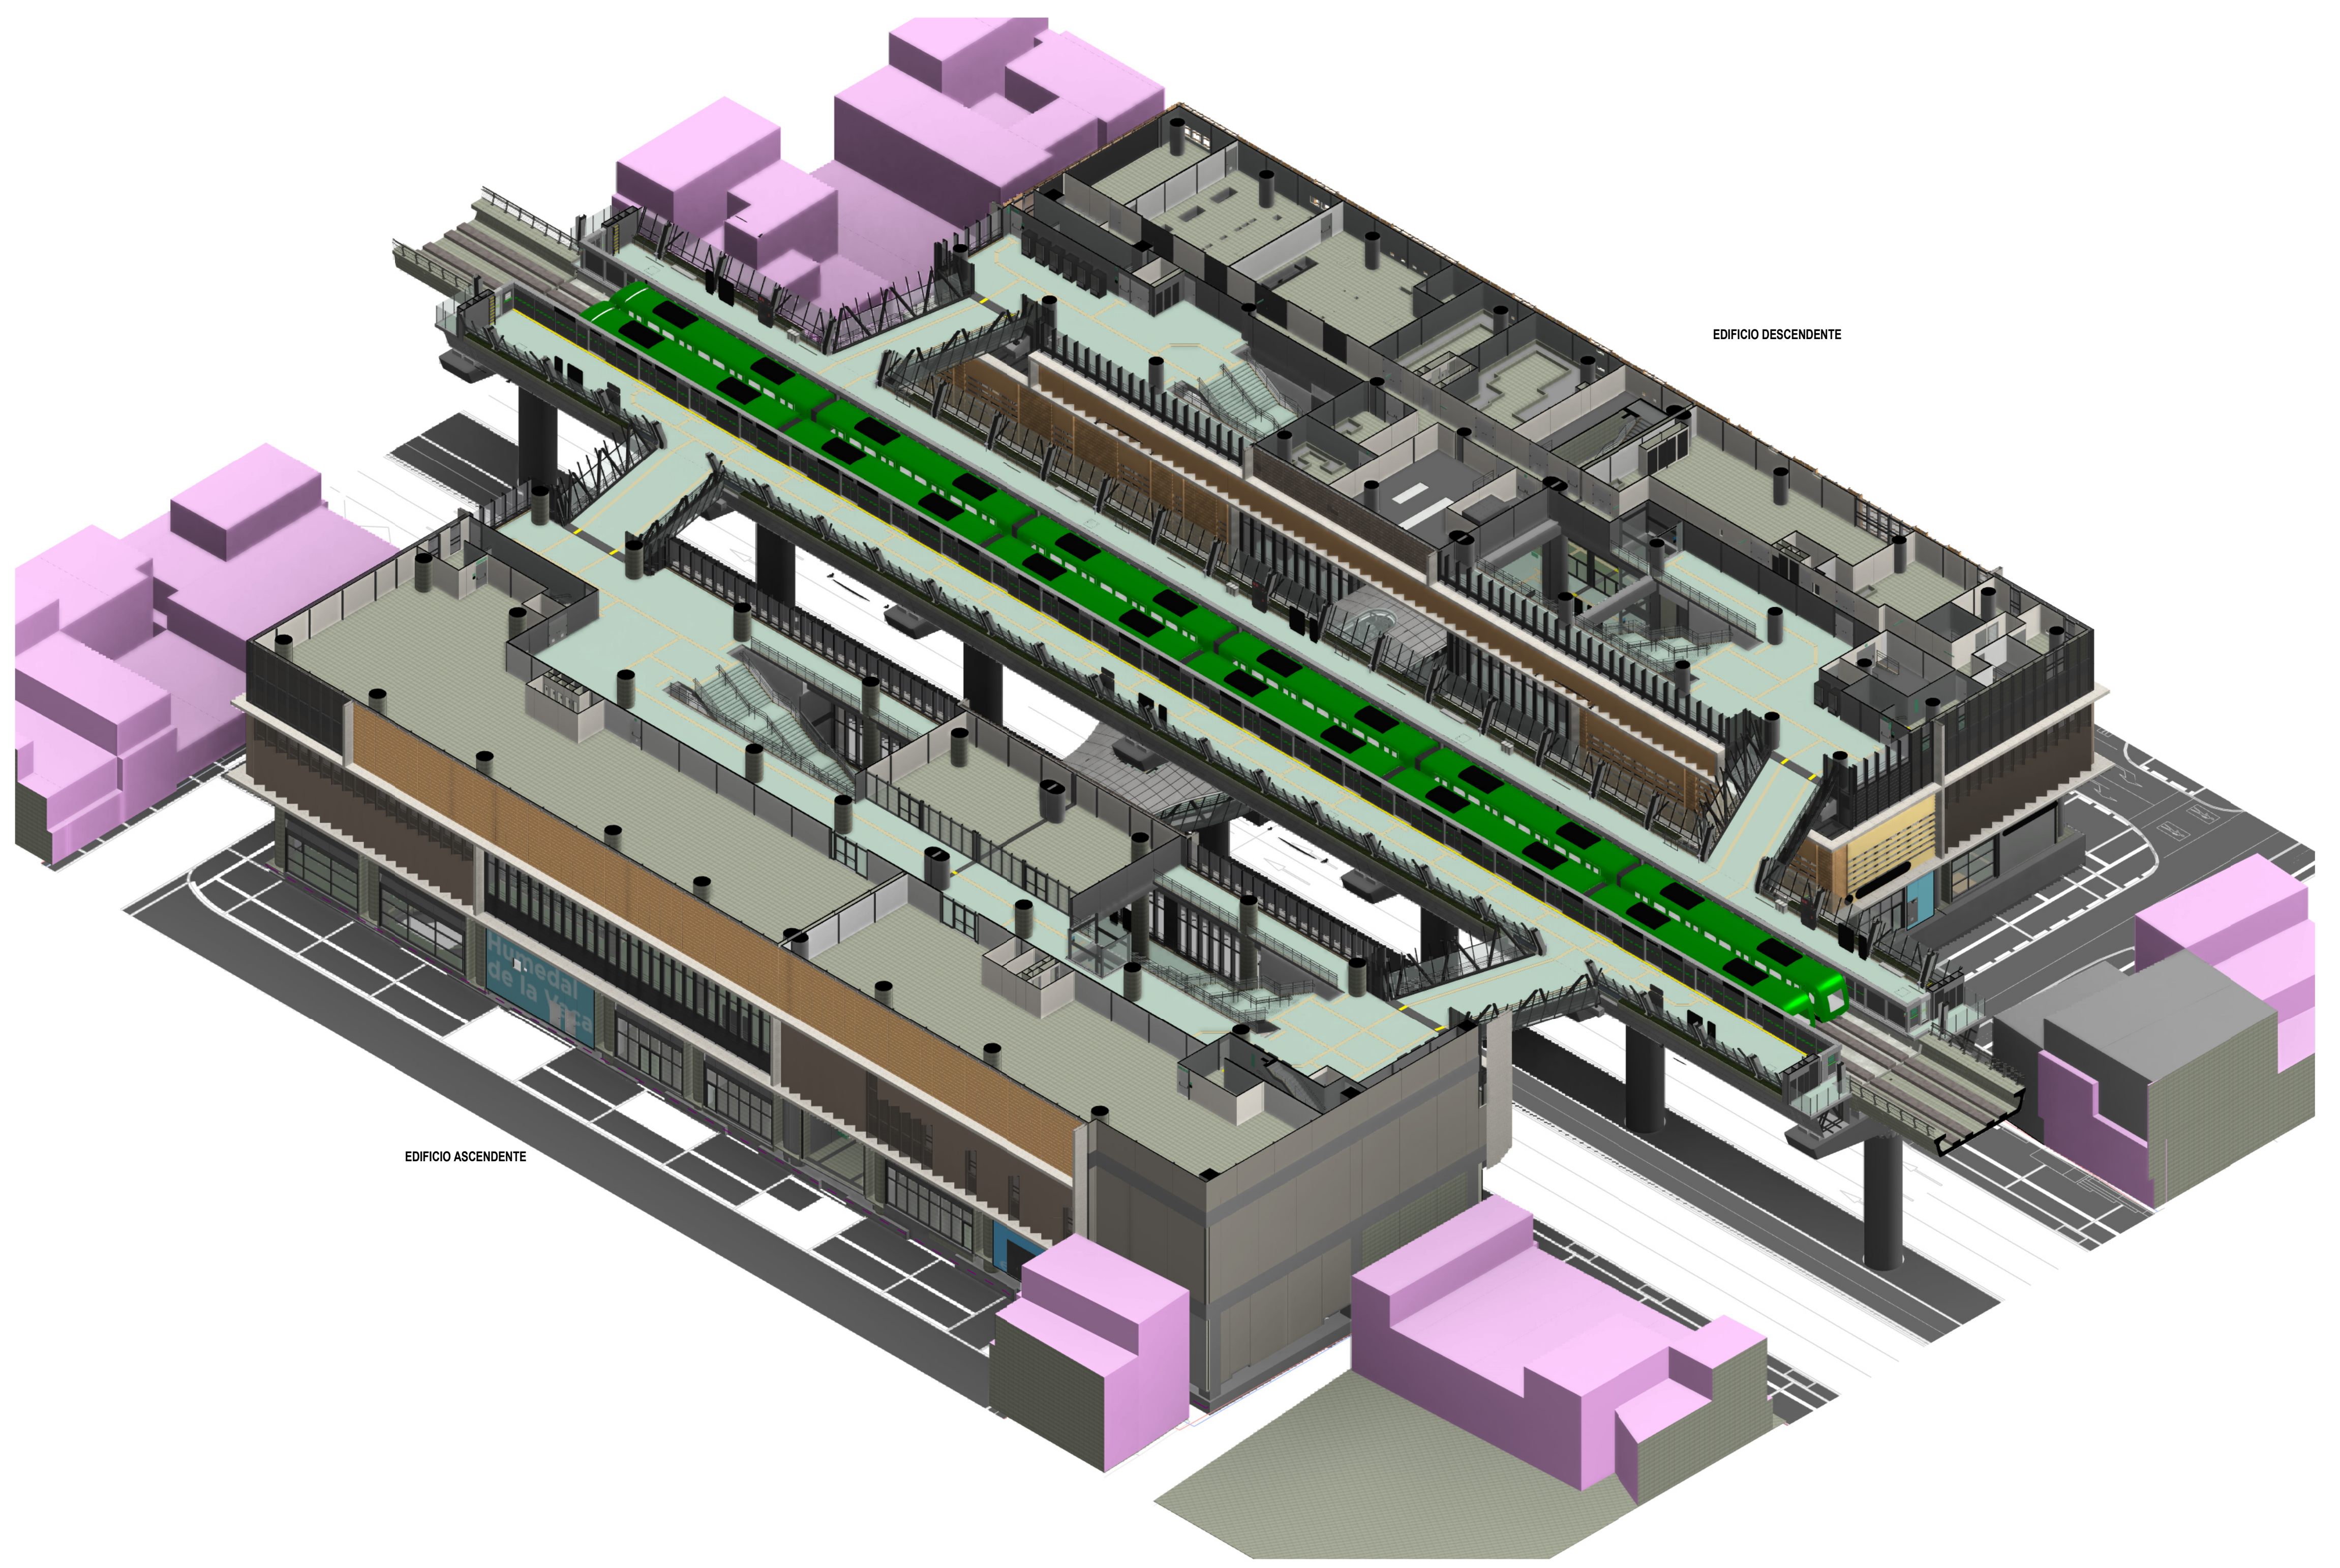

1 **3D_NIVEL PLATAFORMA_GENERAL**
ESC : N/A

TABLA DE ÁREAS ÚTILES (NIVEL PLATAFORMA)

CÓDIGO	NOMBRE	ÁREA (m²)	DEPARTAMENTO
EDIFICIO ASCENDENTE			
ARQ_PL_03_PLATAFORMA			
PA-02	ÁREA PAGA	990.86	ÁREA PAGA
R-112	SERVICIOS ADICIONALES - ÁREA DE SERVICIO	829.52	SERVICIOS ADICIONALES - ÁREA NO PAGA
R-113	SERVICIOS ADICIONALES - ÁREA DE SERVICIO	246.89	SERVICIOS ADICIONALES - ÁREA PAGA
R-114	SERVICIOS ADICIONALES - ÁREA DE SERVICIO	557.08	SERVICIOS ADICIONALES - ÁREA NO PAGA
R-301	SERVICIOS ADICIONALES - MÁQUINAS EXPENDEDORAS/CAJEROS AUTOMÁTICOS	6.54	SERVICIOS ADICIONALES - ÁREA NO PAGA
R-302	SERVICIOS ADICIONALES - MÁQUINAS EXPENDEDORAS/CAJEROS AUTOMÁTICOS	8.14	SERVICIOS ADICIONALES - ÁREA NO PAGA
T-20-W-5	MEDIDORES (AGUA)	7.15	ÁREA TÉCNICA
T-21-10	ÁREA DE INSPECCIÓN	11.23	ÁREA TÉCNICA
T-21-11	ÁREA DE INSPECCIÓN	5.48	ÁREA TÉCNICA
T-21-12	ÁREA DE INSPECCIÓN	5.42	ÁREA TÉCNICA
T-25-4	NODO DE ACCESO DE TELECOMUNICACIONES	5.38	ÁREA TÉCNICA
T-25-5	NODO DE ACCESO DE TELECOMUNICACIONES	3.70	ÁREA TÉCNICA
ZDR-03	ZONA DE REFUGIO (PMR)	6.08	ZONA DE REFUGIO
ZDR-04	ZONA DE REFUGIO (PMR)	2.43	ZONA DE REFUGIO
ZDR-05	ZONA DE REFUGIO (PMR)	6.08	ZONA DE REFUGIO
ZDR-06	ZONA DE REFUGIO (PMR)	2.64	ZONA DE REFUGIO
EDIFICIO ASCENDENTE		2694.62	
EDIFICIO DESCENDENTE			
ARQ_PL_03_PLATAFORMA			
O-17	OPERADORES TELECOMUNICACIONES EXTERIORES	35.86	ÁREA OPERATIVA
PA-02	ÁREA PAGA	241.36	ÁREA PAGA
PA-03	ÁREA PAGA	328.12	ÁREA PAGA
R-304	SERVICIOS ADICIONALES - MÁQUINAS EXPENDEDORAS/CAJEROS AUTOMÁTICOS	18.91	SERVICIOS ADICIONALES - ÁREA NO PAGA
R-305	SERVICIOS ADICIONALES - MÁQUINAS EXPENDEDORAS/CAJEROS AUTOMÁTICOS	3.09	SERVICIOS ADICIONALES - ÁREA NO PAGA
T-00-2	CIRCULACIÓN TÉCNICA	294.59	ÁREA TÉCNICA
T-01	SUBESTACIÓN DE TRACCIÓN (SET)	216.40	ÁREA TÉCNICA
T-02	LOCAL DE CONDUCCIÓN AUTOMÁTICA (CBTC)	55.81	ÁREA TÉCNICA
T-02-1	UPS DEDICADA (CBTC)	34.77	ÁREA TÉCNICA
T-03	TELECOMUNICACIONES ESTACIÓN - CORRIENTE DÉBIL	113.65	ÁREA TÉCNICA
T-04	EQUIPO BOLETERÍA	18.20	ÁREA TÉCNICA
T-05	ALMACÉN PARA MANTENIMIENTO	19.78	ÁREA TÉCNICA
T-06	SALA DE TABLEROS	64.22	ÁREA TÉCNICA
T-07	CENTRO DE TRANSFORMACIÓN (CT)	185.81	ÁREA TÉCNICA
T-09	ALMACÉN EQUIPO ELÉCTRICO	19.78	ÁREA TÉCNICA
T-10	CUARTO DE EQUIPO ELECTROMECÁNICO	14.06	ÁREA TÉCNICA
T-11	CUARTO DE VENTILACIÓN	204.12	ÁREA TÉCNICA
T-12	PLANTA DE REFRIGERACIÓN PARA LA CLIMATIZACIÓN	78.79	ÁREA TÉCNICA
T-21-09	ÁREA DE INSPECCIÓN	4.53	ÁREA TÉCNICA
T-21-10	ÁREA DE INSPECCIÓN	5.92	ÁREA TÉCNICA
T-21-11	ÁREA DE INSPECCIÓN	7.85	ÁREA TÉCNICA
T-22	CUARTO DE UPS	110.08	ÁREA TÉCNICA
T-23	CUARTO PDAP	26.07	ÁREA TÉCNICA
T-24	TETRA UPS	41.30	ÁREA TÉCNICA
T-25-6	NODO DE ACCESO DE TELECOMUNICACIONES	6.29	ÁREA TÉCNICA
T-25-7	NODO DE ACCESO DE TELECOMUNICACIONES	6.32	ÁREA TÉCNICA
ZDR-05	ZONA DE REFUGIO (PMR)	2.47	ZONA DE REFUGIO
ZDR-06	ZONA DE REFUGIO (PMR)	4.56	ZONA DE REFUGIO
ZDR-07	ZONA DE REFUGIO (PMR)	4.86	ZONA DE REFUGIO
ZDR-08	ZONA DE REFUGIO (PMR)	4.36	ZONA DE REFUGIO
EDIFICIO DESCENDENTE		2171.92	
NAVE CENTRAL			
ARQ_PL_03_PLATAFORMA			
PA-02	ÁREA PAGA	69.45	ÁREA PAGA
PA-03	ÁREA PAGA	81.34	ÁREA PAGA
PA-04	ÁREA PAGA	696.07	ÁREA PAGA
PA-05	ÁREA PAGA	696.07	ÁREA PAGA
PA-06	ÁREA PAGA	80.22	ÁREA PAGA
PA-07	ÁREA PAGA	81.25	ÁREA PAGA
NAVE CENTRAL		1704.38	
TOTAL NIVEL PLATAFORMA		6570.93	

TABLA DE ÁREAS ÚTILES POR DEPARTAMENTO (NIVEL PLATAFORMA)

DEPARTAMENTO	ÁREA (m²)
EDIFICIO ASCENDENTE	
ARQ_PL_03_PLATAFORMA	
SERVICIOS ADICIONALES - ÁREA NO PAGA	1401.28
SERVICIOS ADICIONALES - ÁREA PAGA	246.89
ZONA DE REFUGIO	17.22
ÁREA PAGA	990.86
ÁREA TÉCNICA	38.36
EDIFICIO DESCENDENTE	
ARQ_PL_03_PLATAFORMA	
SERVICIOS ADICIONALES - ÁREA NO PAGA	22.00
ZONA DE REFUGIO	16.25
ÁREA OPERATIVA	35.86
ÁREA PAGA	569.49
ÁREA TÉCNICA	1528.33
NAVE CENTRAL	
ARQ_PL_03_PLATAFORMA	
ÁREA PAGA	1704.38
TOTAL NIVEL PLATAFORMA	6570.93

LOCALIZACIÓN

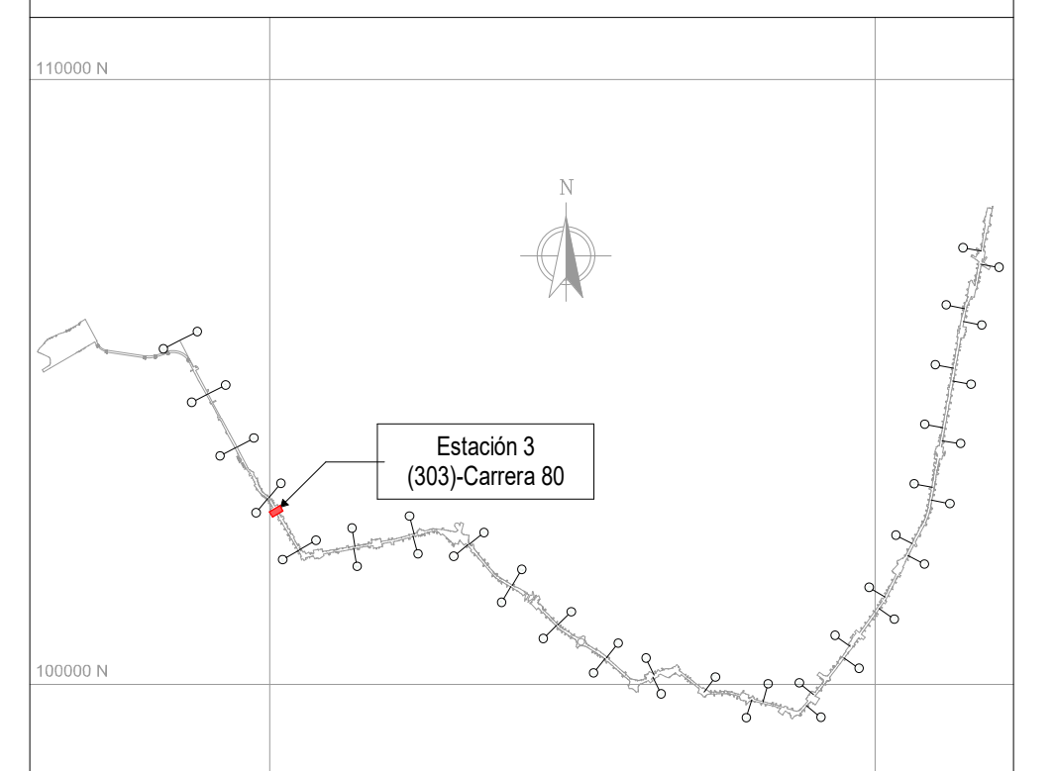

NOTAS

01 TODAS LAS DIMENSIONES ESTÁN CONFIGURADAS EN METROS A MENOS QUE SE INDIQUE UNA UNIDAD DE MEDIDA DIFERENTE.

02 TODAS LAS MEDIDAS, UBICACIÓN Y NIVELES DEBEN VERIFICARSE EN EL LUGAR DE CONSTRUCCIÓN.

03 EL NIVEL DE ACCESO AL EDIFICIO PL 01 CORRESPONDE AL +0,00 DE LA ESTACIÓN Y REFERENCIA AL NIVEL 2547.75 M.S.N.M.

04 LOS NOMBRES ESPECÍFICOS DE LAS ÁREAS PUEDEN SER CONSULTADAS EN EL PLANO NO. 3 Ó EN LAS VISTAS EN PLANTA.

05 LOS COLORES QUE SE MUESTRAN EN LOS PLANOS COMO PROYECCIÓN DE ELEMENTOS ARQUITECTÓNICOS COMO CUBIERTAS FACHADAS MUROS ETC. NO REPRESENTAN LA MATERIALIDAD Y REALIDAD DE ACABADOS DEL PROYECTO, SOLO SON INDICATIVOS PARA REALIZAR UNA CORRECTA LECTURA DE LA PLANIMETRÍA.

06 LAS ESCALERAS ELÉCTRICAS INDICAN SU SENTIDO CON LA SIGUIENTE NOMENCLATURA: “SUBE” Y “BAJA”.

07 SE DEBEN REVISAR LOS NIVELES ESTRUCTURALES PARA NIVEL DE ACCESO PL_01 Y SUBNIVELES, PL_02 (INTERMEDIO), PL_03 (PLATAFORMA) CON LA PLANIMETRÍA DE PLACAS ESTRUCTURALES EN LOS ENTREGABLES L1T1-1300-403-CON-ED-EST-PL-0038, 39, 78, 79, 82, 83 RESPECTIVAMENTE. EL NIVEL ESTRUCTURAL (NE) REFERENCIA LOS ESPACIOS DONDE SE DEBE ACONDICIONAR EL ACABADO DE PISO SEGÚN CORRESPONDA, CON LOS NIVELES DE PISO TERMINADO (NPT). LOS NIVELES PROYECTADOS DE EMPATE (NPE) EN LAS ÁREAS DE SERVICIOS ADICIONALES, REFERENCIAN LA ADECUACIÓN DE LOS DESNIVELES EN ESTAS ÁREAS; QUEDA COMO RESPONSABILIDAD DEL LOCATARIO DEFINIR Y ACONDICIONAR ESTE ACABADO DE PISO (NPE) EN LÍNEA CON EL NIVEL (NPT) DE ESPACIOS COLINDANTES. EL NIVEL ESTRUCTURAL (NE) SE ENCUENTRA A (- 0.10M) POR DEBAJO DE LOS NIVELES DE PISO TERMINADO (NPT) Y LOS NIVELES PROYECTADOS DE EMPATE (NPE) MARCADOS EN LA PLANIMETRÍA.

- ARQ_PL_00 = SÓTANO	/ NPT -8.50	- ARQ_PL_00.11 = ACCESO	/ NPT -0.95
- ARQ_PL_00.1 = ACCESO	/ NPT -2.20	- ARQ_PL_00.12 = ACCESO	/ NPT -0.75
- ARQ_PL_00.2 = ACCESO	/ NPT -2.10	- ARQ_PL_00.13 = ACCESO	/ NPT -0.55
- ARQ_PL_00.3 = ACCESO	/ NPT -1.95	- ARQ_PL_00.14 = ACCESO	/ NPT -0.45
- ARQ_PL_00.4 = ACCESO	/ NPT -1.80	- ARQ_PL_00.15 = ACCESO	/ NPT -0.35
- ARQ_PL_00.5 = ACCESO	/ NPT -1.75	- ARQ_PL_01 = ACCESO	/ NPT 0.00
- ARQ_PL_00.6 = ACCESO	/ NPT -1.65	- ARQ_PL_02 = INTERMEDIO	/ NPT 7.60
- ARQ_PL_00.7 = ACCESO	/ NPT -1.55	- ARQ_PL_02.2 = TOPE DE RIEL	/ NPT 15.20
- ARQ_PL_00.8 = ACCESO	/ NPT -1.45	- ARQ_PL_03 = PLATAFORMA	/ NPT 16.34
- ARQ_PL_00.9 = ACCESO	/ NPT -1.25	- ARQ_PL_04 = CUBIERTA EDIFICACIONES	/ NPT 22.94
- ARQ_PL_00.10 = ACCESO	/ NPT -1.15	- ARQ_PL_05 = CUBIERTA NAVE CENTRAL	/ NPT 25.59

CONVENCIONES

- - - -	LÍMITE DE INTERVENCIÓN
- - - -	HUELLA APÉNDICE TÉCNICO
▬	MURO DIVISORIO
— — —	PROYECCIÓN NIVEL SUPERIOR
🟩	SERVICIOS ADICIONALES - ÁREA NO PAGA
🟩	SERVICIOS ADICIONALES - ÁREA PAGA
🟩	SERVICIO PÚBLICO
🟦	ZONA DE REFUGIO
🟥	ÁREA CULTURAL
🟨	ÁREA NO PAGA
🟦	ÁREA OPERATIVA
🟧	ÁREA PAGA
🟦	ÁREA PÚBLICA
⬜	ÁREA TÉCNICA

No.	PLANOS DE REFERENCIA	REV.

No.	MODELO BIM DE REFERENCIA	REV.
1	L1T1-1100-203-CON-ED-EST-MO-0001.rvt	V00
2	L1T1-1100-204-CON-ED-EST-MO-0001.rvt	V00
3	L1T1-1100-303-CON-ED-EST-MO-0001.rvt	V00
4	L1T1-1150-203-CON-ED-EST-MO-0001.rvt	V00
5	L1T1-1150-204-CON-ED-EST-MO-0001.rvt	V00
6	L1T1-1150-303-CON-ED-EST-MO-0001.rvt	V00
7	L1T1-1200-303-CON-ED-EST-MO-0001.rvt	V00
8	L1T1-1300-403-CON-ED-EST-MO-0001.rvt	V00
9	L1T1-1300-403-CON-ED-EST-MO-0002.rvt	V00
10	L1T1-1310-403-CON-ED-EST-MO-0001.rvt	V00
11	L1T1-1410-403-CON-ED-MEC-MO-0001.rvt	V00
12	L1T1-1420-403-CON-ED-MEC-MO-0001.rvt	V00
13	L1T1-5160-303-CON-ED-EST-MO-0001.rvt	V00
14	L1T1-5160-303-CON-ED-ARQ-MO-0001.rvt	V00
15	L1T1-5300-303-CON-ED-MEC-MO-0001.rvt	V00
16	L1T1-5600-303-CON-ED-INS-MO-0001.rvt	V00
17	L1T1-1330-403-CON-ED-ARQ-MO-0011.rvt	V00
18	L1T1-1330-403-CON-ED-ARQ-MO-0012.rvt	V00

No.	PAQUETE DE TRABAJO DE REFERENCIA	REV.
1	XREF-URBANISMO_CONTEXT_ST03.rvt	
2	XREF-SECONDARY-STRUCTURE-ST03.rvt	

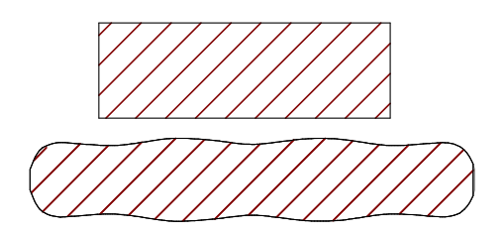

PLANO CLAVE ESTACIÓN 3

VÁLIDO PARA CONSTRUCCIÓN
01-03-26

METRO BOGOTÁ
GCS Consorcio Consultores PMO Bogotá
CONSORCIO SUPERVISOR PLMB
CHEC

DISEÑÓ: REN ZHENHUA Licencia de Arq.nivel I (China): 1101735-614	APROBÓ: DIEGO ERNESTO DUEÑAS Mat.: 25202-53876 CND
REVISÓ: CARLOS MAURICIO BARRETO BARBOSA Mat.: A4012012-14139353	DIBUJÓ: EQUIPO CHEC

REVISIÓN No.	FECHA	DESCRIPCIÓN	REVISÓ	APROBÓ	APROBACIÓN CLIENTE
V01	01/03/2026	EMITIDO PARA CONSTRUCCIÓN	C.M.B.B	D.E.D	
V00	20/12/2024	REVISIÓN NO OBJETADA - EMITIDO PARA CONSTRUCCIÓN	F.B.R	E.O.M	
VFF	28/06/2024	EMITIDO PARA REVISIÓN Y COMENTARIOS DEL CLIENTE E INTERVENTORÍA - INCLUYE COMENTARIOS /(AJUSTES V3)	F.B.R	E.O.M	
VEE	22/08/2023	EMITIDO PARA REVISIÓN Y COMENTARIOS DEL CLIENTE E INTERVENTORÍA - INCLUYE COMENTARIOS /(AJUSTES V2)	J.E.M	M.B.M	
VDD	18/12/2022	EMITIDO PARA REVISIÓN Y COMENTARIOS DEL CLIENTE E INTERVENTORÍA - INCLUYE COMENTARIOS /(AJUSTES)	J.E.M	M.B.M	
VCC	20/06/2022	EMITIDO PARA REVISIÓN Y COMENTARIOS DEL CLIENTE E INTERVENTORÍA - INCLUYE COMENTARIOS /(ENTREGA 90%)	J.E.M	M.B.M	
VBB	06/12/2021	EMITIDO PARA REVISIÓN Y COMENTARIOS DEL CLIENTE E INTERVENTORÍA	J.E.M	M.B.M	
VA0	30/06/2021	EMITIDO PARA COMENTARIOS INTERNOS - EMISIÓN PRELIMINAR PARA COMENTARIOS	J.E.M	M.B.M	

METRO LÍNEA 1

METRO LÍNEA 1
CONTRATO DE CONCESIÓN No. 163 DE 2019

PROYECTO PRIMERA LÍNEA DEL METRO DE BOGOTÁ - TRAMO 1

INFRAESTRUCTURA VIAL

ARQUITECTURA

ESTACIÓN METRO 3 (CARRERA 80)
GENERAL
VISTA EN PLANTA Y 3D - NIVEL PLATAFORMA

DIRECTOR DE INTERVENTORÍA:
JAVIER DESCARGA N.
Mat.:25202-68697 CND

ESPECIALISTA INTERVENTORÍA:
CARLOS ALBERTO HOYOS SOTO
Mat.:A25072000-14251682

FECHA: MARZO 2026

PLANCHA No: L1T1-0000-303-CON-ED-ARQ-PL-0001_07_V01
ARCHIVO: L1T1-0000-303-CON-ED-ARQ-MO-0001_V00.rvt
ESCALA: INDICADA
FECHA: JUNIO 2021
REVISIÓN No. V01
PLANO No. 07 DE 96