L1T1-CON-CAL-FR-0120 - B1 : 1000x707mm

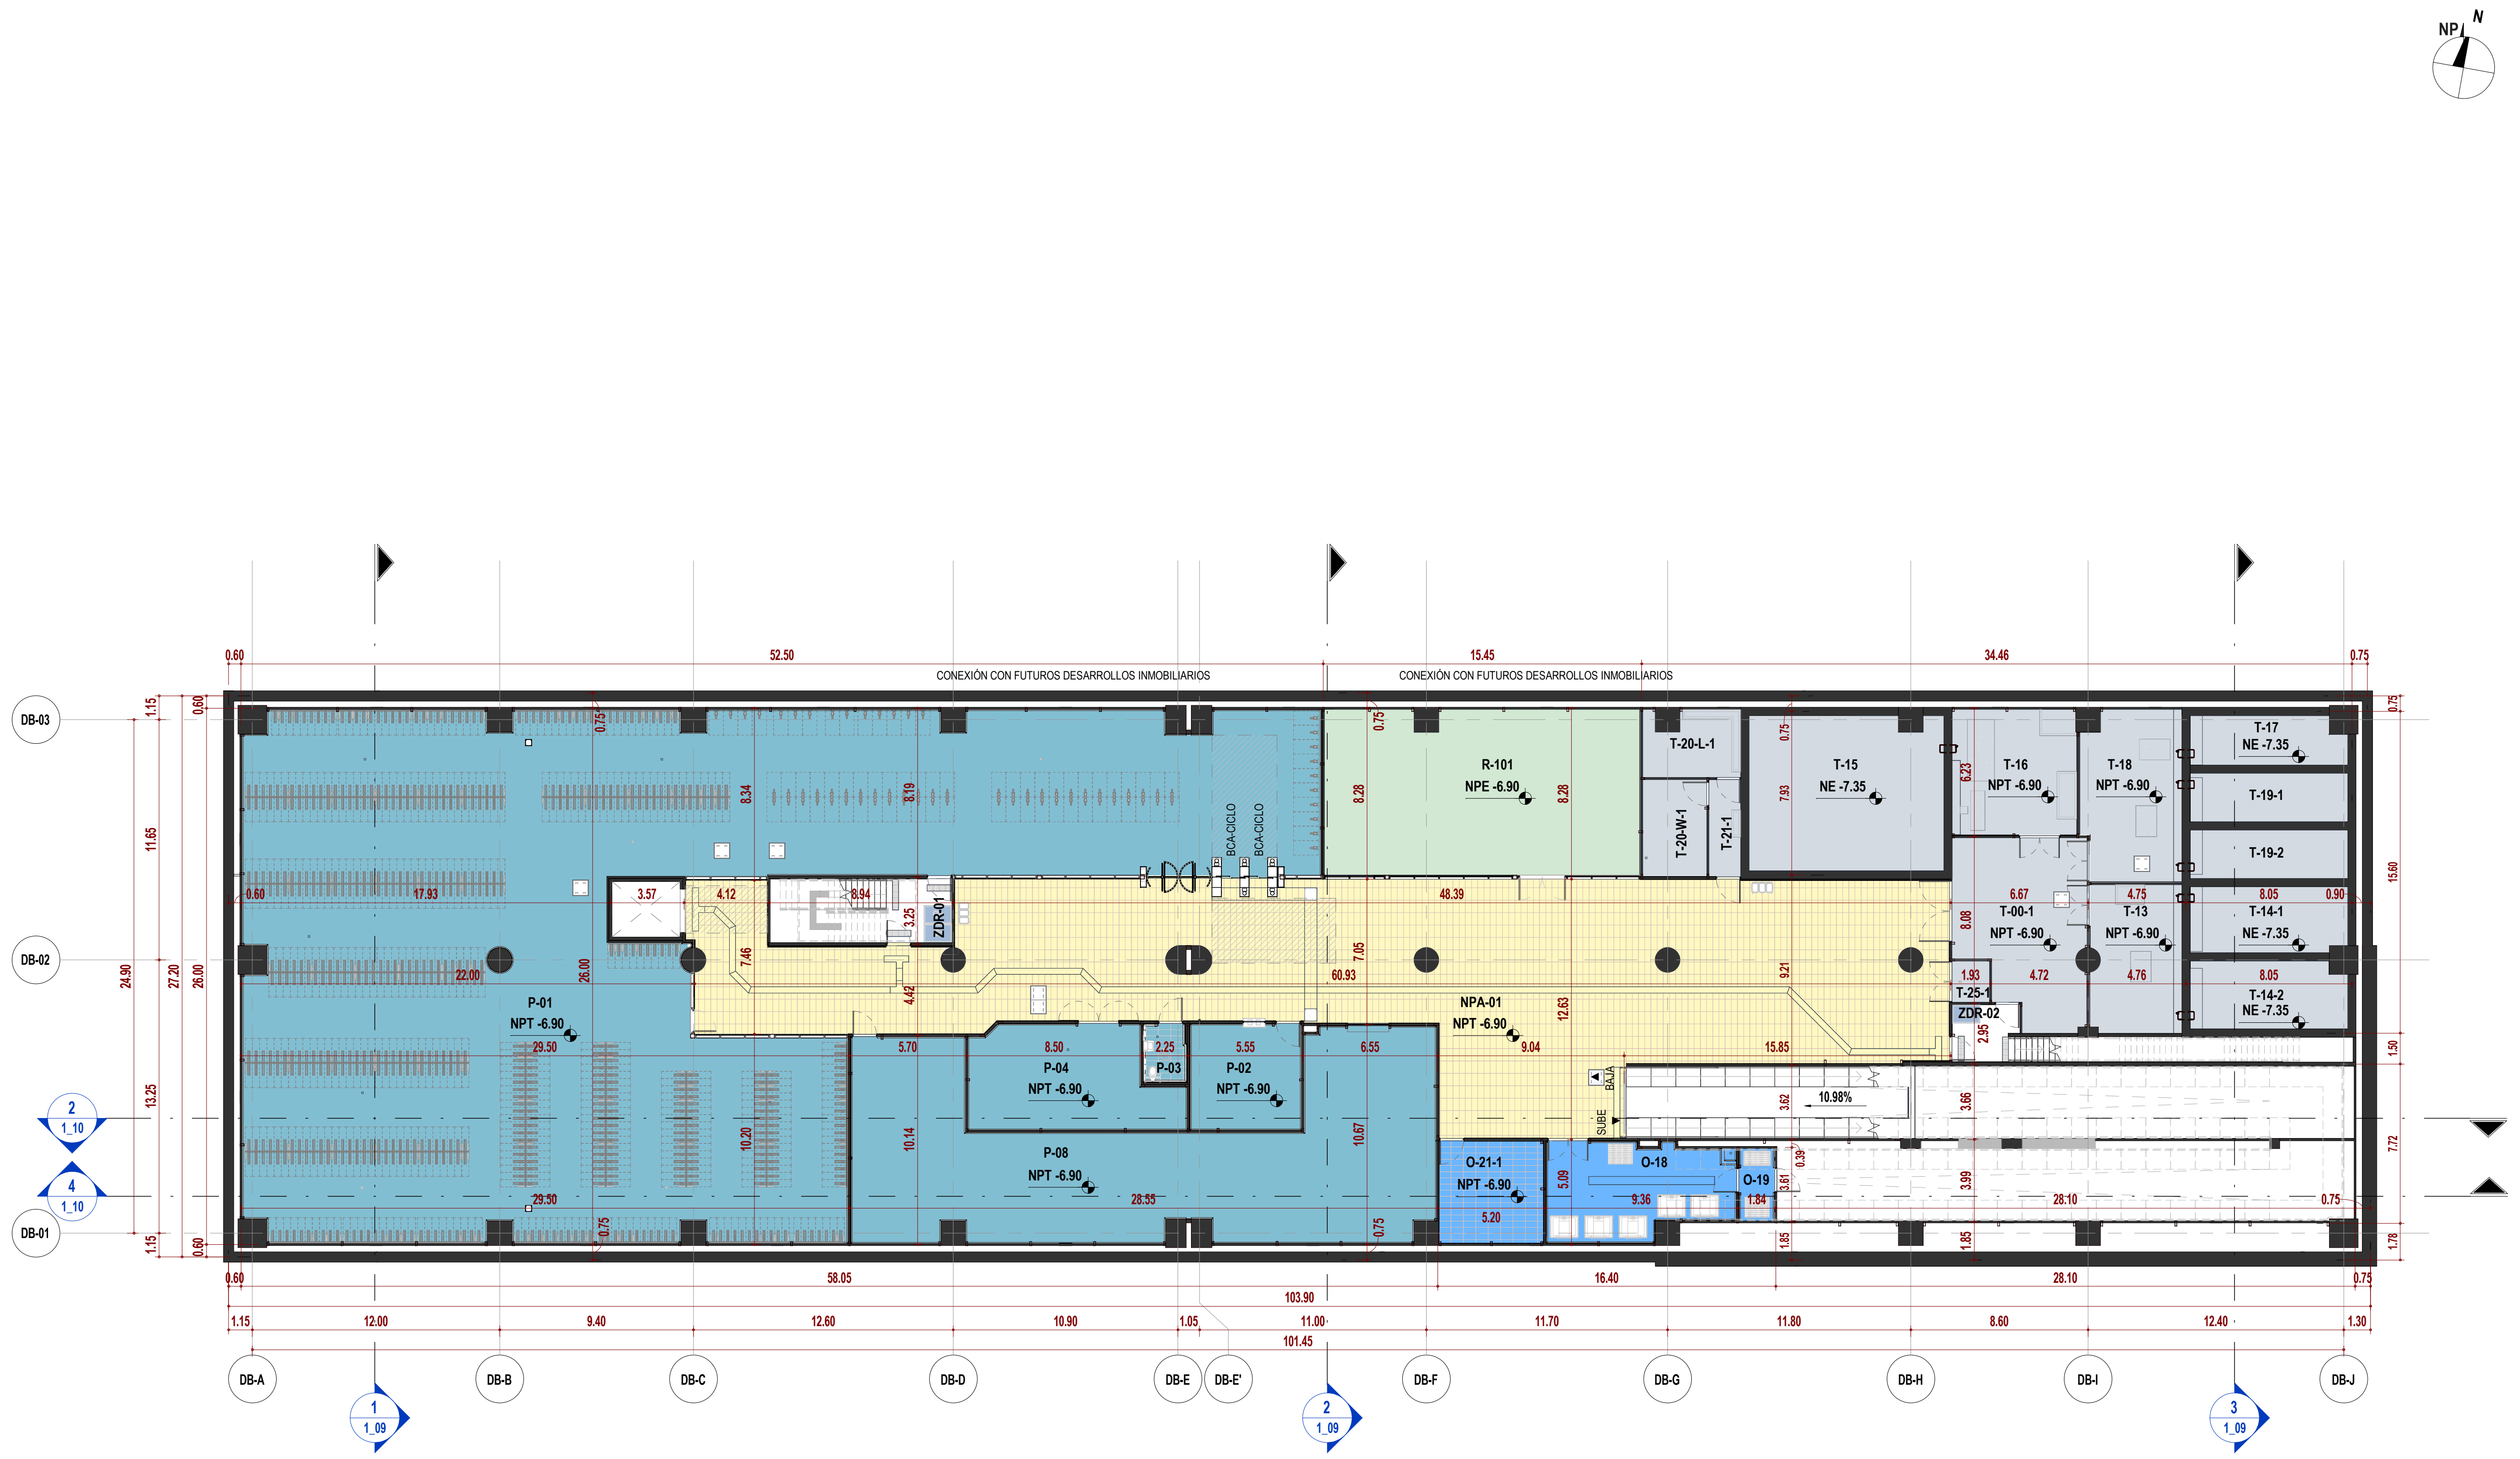

② NIVEL SÓTANO_EDIFICIO DESCENDENTE
ESC : 1 : 200

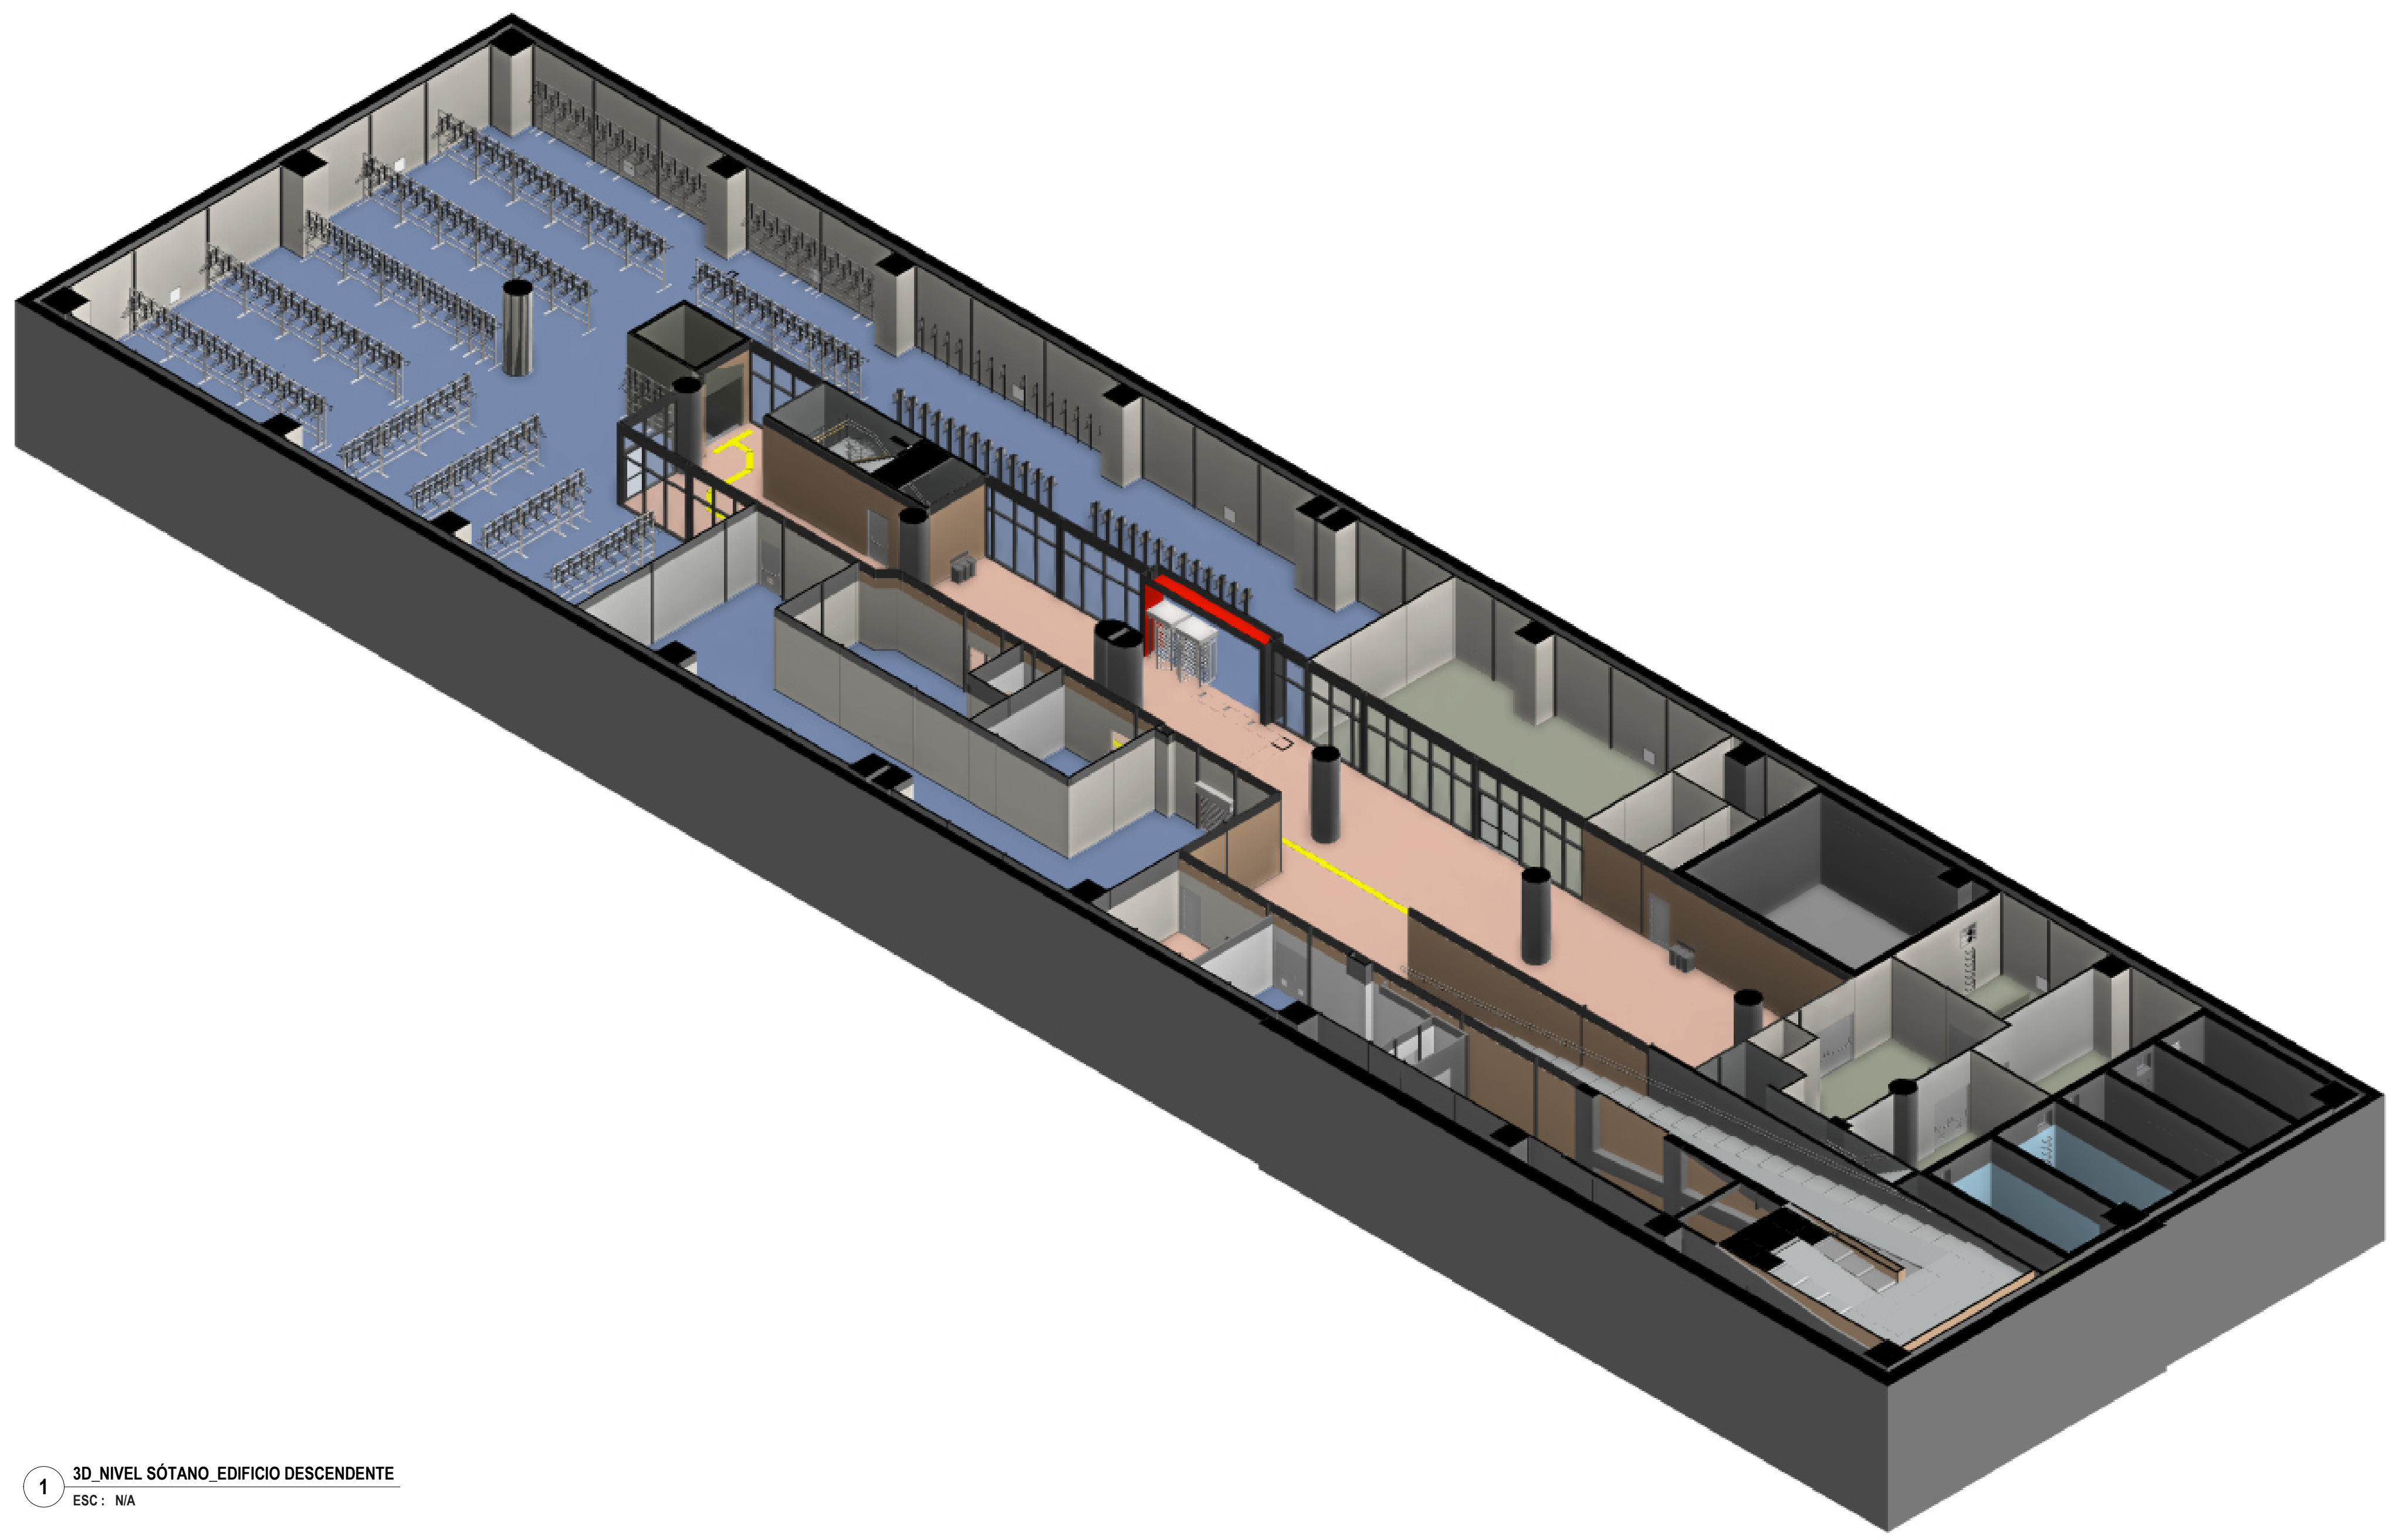

① 3D_NIVEL SÓTANO_EDIFICIO DESCENDENTE
ESC : N/A

LOCALIZACIÓN

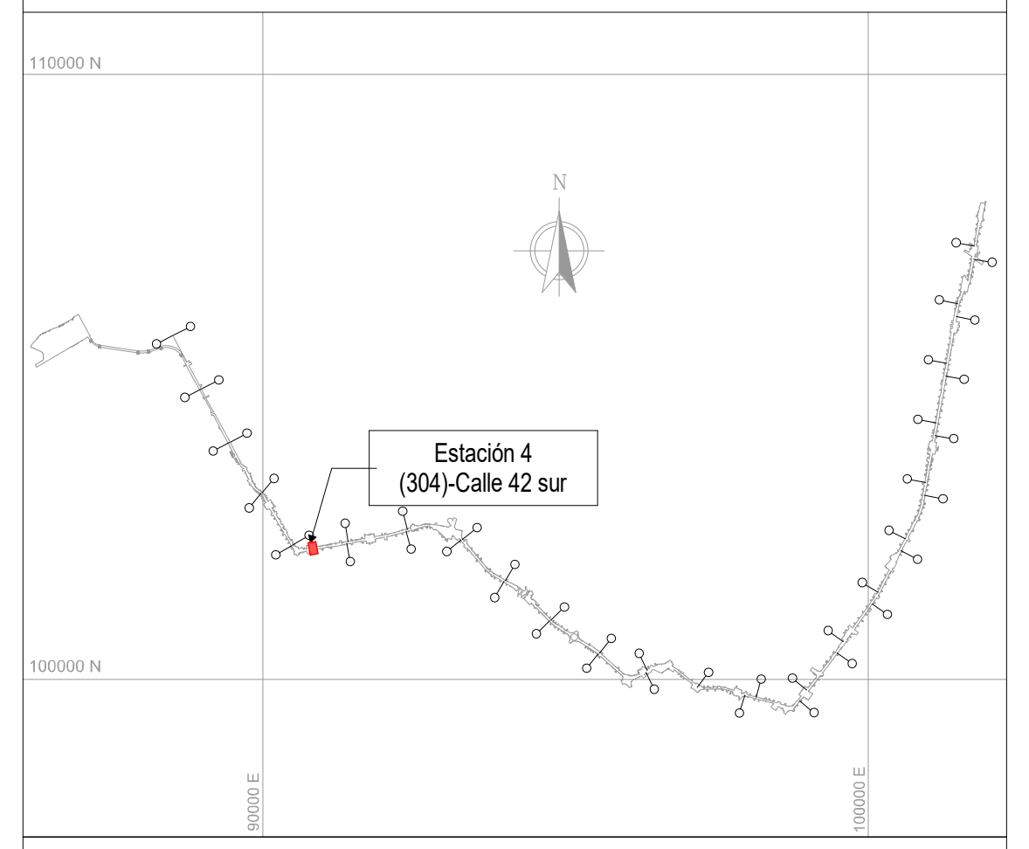

NOTAS

01 TODAS LAS DIMENSIONES ESTÁN CONFIGURADAS EN METROS A MENOS QUE SE INDIQUE UNA UNIDAD DE MEDIDA DIFERENTE.

02 TODAS LAS MEDIDAS, UBICACIÓN Y NIVELES DEBEN VERIFICARSE EN EL LUGAR DE CONSTRUCCIÓN.

03 EL NIVEL DE ACCESO AL EDIFICIO PL 01 CORRESPONDE AL +0,00 DE LA ESTACIÓN Y REFERENCIA AL NIVEL 2555.00 M.S.N.M

04 LOS NOMBRES ESPECÍFICOS DE LAS ÁREAS PUEDEN SER CONSULTADAS EN EL PLANO NO. 3 Ó EN LAS VISTAS EN PLANTA.

05 LOS COLORES QUE SE MUESTRAN EN LOS PLANOS COMO PROYECCIÓN DE ELEMENTOS ARQUITECTÓNICOS COMO CUBIERTAS, FACHADAS, MUROS, ETC. NO REPRESENTAN LA MATERIALIDAD Y REALIDAD DE ACABADOS DEL PROYECTO, SOLO SON INDICATIVOS PARA REALIZAR UNA CORRECTA LECTURA DE LA PLANIMETRÍA.

06 SE DEBEN REVISAR LOS NIVELES ESTRUCTURALES PARA NIVEL DE ACCESO PL_01 Y SUBNIVELES, PL_02 (INTERMEDIO), PL_03 (PLATAFORMA) CON LA PLANIMETRÍA DE PLACAS ESTRUCTURALES EN LOS ENTREGABLES L1T1-1300-404-CON-ED-EST-PL-0038, 39, 88, 89, 92, 93, RESPECTIVAMENTE. EL NIVEL ESTRUCTURAL (NE) REFERENCIA LOS ESPACIOS DONDE SE DEBE ACONDICIONAR EL ACABADO DE PISO SEGÚN CORRESPONDA, CON LOS NIVELES DE PISO TERMINADO (NPT). LOS NIVELES PROYECTADOS DE EMPATE (NPE) EN LAS ÁREAS DE SERVICIOS ADICIONALES, REFERENCIAN LA ADECUACIÓN DE LOS DESNIVELES EN ESTAS ÁREAS; QUEDA COMO RESPONSABILIDAD DEL LOCATARIO DEFINIR Y ACONDICIONAR ESTE ACABADO DE PISO (NPE) EN LÍNEA CON EL NIVEL (NPT) DE ESPACIOS COLINDANTES. EL NIVEL ESTRUCTURAL (NE) SE ENCUENTRA A (- 0.10M) POR DEBAJO DE LOS NIVELES DE PISO TERMINADO (NPT) Y LOS NIVELES PROYECTADOS DE EMPATE (NPE) MARCADOS EN LA PLANIMETRÍA.

- ARQ_PL_00 = SÓTANO / NPT -6.90m
- ARQ_PL_00.1 = ACCESO / NPT -0.50m
- ARQ_PL_00.2 = ACCESO / NPT -0.45m
- ARQ_PL_00.3 = ACCESO / NPT -0.38m
- ARQ_PL_00.4 = ACCESO / NPT -0.30m
- ARQ_PL_00.5 = ACCESO / NPT -0.25m
- ARQ_PL_00.6 = ACCESO / NPT -0.20m
- ARQ_PL_01 = ACCESO / NPT 0.00m
- ARQ_PL_01.1 = ACCESO / NPT 0.14m
- ARQ_PL_01.2 = ACCESO / NPT 0.25m
- ARQ_PL_02 = INTERMEDIO / NPT 6.60m
- ARQ_PL_02.2 = TOPE DE RIEL (TOR) / NPT 14.20m
- ARQ_PL_03 = PLATAFORMA / NPT 15.34m
- ARQ_PL_04 = CUBIERTA EDIFICACIONES / NPT 21.94m
- ARQ_PL_05 = CUBIERTA NAVE CENTRAL / NPT 24.59m

CONVENCIONES

🟩	SERVICIOS ADICIONALES - ÁREA NO PAGA
🟩	SERVICIOS ADICIONALES - ÁREA PAGA
🟩	SERVICIO PÚBLICO
🟦	ZONA DE REFUGIO
🟥	ÁREA CULTURAL
🟨	ÁREA NO PAGA
🟦	ÁREA OPERATIVA
🟧	ÁREA PAGA
🟦	ÁREA PÚBLICA
⬜	ÁREA TÉCNICA

TABLA DE ÁREAS ÚTILES (NIVEL SÓTANO_EDIFICIO DESCENDENTE)

CÓDIGO	NOMBRE	ÁREA (m²)	DEPARTAMENTO
EDIFICIO DESCENDENTE			
ARQ_PL_00_SÓTANO			
NPA-01	ÁREA NO PAGA	476.52	ÁREA NO PAGA
O-18	CUARTO DE ALMACENAMIENTO DE RESIDUOS SÓLIDOS	39.45	ÁREA OPERATIVA
O-19	CUARTO DE ALMACENAMIENTO DE RESIDUOS PELIGROSOS	5.82	ÁREA OPERATIVA
O-21-1	ALMACENAMIENTO DE LA ESTACIÓN	25.27	ÁREA OPERATIVA
P-01	ÁREA CICLO-PARQUEADEROS	855.87	ÁREA PÚBLICA
P-02	ÁREA OPERATIVA CICLO-PARQUEADEROS	27.87	ÁREA PÚBLICA
P-03	BAÑO OPERADOR CICLO-PARQUEADEROS	5.77	ÁREA PÚBLICA
P-04	TALLER DE BICICLETAS	47.32	ÁREA PÚBLICA
P-08	ESPACIO CARGA DE VEHÍCULOS ELÉCTRICOS	206.14	ÁREA PÚBLICA
R-101	SERVICIOS ADICIONALES - ÁREA DE SERVICIO	121.43	SERVICIOS ADICIONALES - ÁREA NO PAGA
T-00-1	CIRCULACIÓN TÉCNICA	52.22	ÁREA TÉCNICA
T-13	CUARTO DE BOMBAS DE SUMINISTRO DE AGUA	31.53	ÁREA TÉCNICA

TABLA DE ÁREAS ÚTILES (NIVEL SÓTANO_EDIFICIO DESCENDENTE)

CÓDIGO	NOMBRE	ÁREA (m²)	DEPARTAMENTO
T-14-1	TANQUE DE SUMINISTRO DE AGUA	24.06	ÁREA TÉCNICA
T-14-2	TANQUE DE SUMINISTRO DE AGUA	24.44	ÁREA TÉCNICA
T-15	TANQUE SISTEMA DE EXTINCIÓN DE INCENDIOS (RCI)	70.04	ÁREA TÉCNICA
T-16	CUARTO DE BOMBAS PARA ROCIADORES	36.62	ÁREA TÉCNICA
T-17	TANQUE RECUPERACIÓN AGUAS LLUVIAS	17.46	ÁREA TÉCNICA
T-18	CUARTO DE BOMBAS DE RECUPERACIÓN DE AGUAS LLUVIAS Y EQUIPO DE FILTRACIÓN	39.06	ÁREA TÉCNICA
T-19-1	TANQUE DE AGUA TRATADA	17.89	ÁREA TÉCNICA
T-19-2	TANQUE DE AGUA TRATADA	17.88	ÁREA TÉCNICA
T-20-L-1	MEDIDORES (LUZ)	14.31	ÁREA TÉCNICA
T-20-W-1	MEDIDORES (AGUA)	14.56	ÁREA TÉCNICA
T-21-1	ÁREA DE INSPECCIÓN	7.23	ÁREA TÉCNICA
T-25-1	NODO DE ACCESO DE TELECOMUNICACIONES	3.60	ÁREA TÉCNICA
ZDR-01	ZONA DE REFUGIO (PMR)	2.43	ZONA DE REFUGIO
ZDR-02	ZONA DE REFUGIO (PMR)	1.22	ZONA DE REFUGIO
TOTAL NIVEL SÓTANO_EDIFICIO DESCENDENTE		2186.02	

TABLA DE ÁREAS ÚTILES POR DEPARTAMENTO (NIVEL SÓTANO_EDIFICIO DESCENDENTE)

DEPARTAMENTO	ÁREA (m²)
EDIFICIO DESCENDENTE	
ARQ_PL_00_SÓTANO	
SERVICIOS ADICIONALES - ÁREA NO PAGA	121.43
ZONA DE REFUGIO	3.64
ÁREA NO PAGA	476.52
ÁREA OPERATIVA	70.55
ÁREA PÚBLICA	1142.96
ÁREA TÉCNICA	370.91
TOTAL NIVEL SÓTANO	2186.02

TABLA DE CICLO-PARQUEADEROS ESPECÍFICA

DESCRIPCIÓN	CANTIDAD (und)	USUARIOS
ARQ_PL_00_SÓTANO		
BICIPARQUEADERO ASISTIDO EN ACERO INOXIDABLE ASTM A240, a=0.70m X l=1.20m, h=1.70m.	1	EMPLEADOS
BICIPARQUEADERO DE COLGAR, 2 PUESTOS, a=1.20m X l=0.70m, h=2.40m. ACABADO EN PINTURA ELECTROSTÁTICA COLOR RAL9005 "NEGRO INTENSO".	4	EMPLEADOS
EMPLEADOS	5	
BICIPARQUEADERO ASISTIDO EN ACERO INOXIDABLE ASTM A240, a=0.70m X l=1.20m, h=1.70m.	75	VISITANTE
BICIPARQUEADERO DE COLGAR DE 6 PUESTOS EN ACERO, a=1.20m X l=2.10m, h=2.40m. ACABADO EN PINTURA ELECTROSTÁTICA COLOR RAL9005 "NEGRO INTENSO".	558	VISITANTE
BICIPARQUEADERO DE COLGAR, 1 PUESTO, a=1.20m X l=0.70m, h=2.40m. ACABADO EN PINTURA ELECTROSTÁTICA COLOR RAL9005 "NEGRO INTENSO".	14	VISITANTE
BICIPARQUEADERO DE COLGAR, 2 PUESTOS, a=1.20m X l=0.70m, h=2.40m. ACABADO EN PINTURA ELECTROSTÁTICA COLOR RAL9005 "NEGRO INTENSO".	98	VISITANTE
VISITANTE	745	
TOTAL CUPOS	750	

No.	PLANOS DE REFERENCIA	REV.

No.	MODELO BIM DE REFERENCIA	REV.
1	L1T1-1100-204-CON-ED-EST-MO-0001.rvt	V00
2	L1T1-1100-205-CON-ED-EST-MO-0001.rvt	V00
3	L1T1-1100-304-CON-ED-EST-MO-0001.rvt	V00
4	L1T1-1150-204-CON-ED-EST-MO-0001.rvt	V00
5	L1T1-1150-205-CON-ED-EST-MO-0001.rvt	V00
6	L1T1-1150-304-CON-ED-EST-MO-0001.rvt	V00
7	L1T1-1200-304-CON-ED-EST-MO-0001.rvt	V00
8	L1T1-1300-404-CON-ED-EST-MO-0001.rvt	V00
9	L1T1-1300-404-CON-ED-EST-MO-0002.rvt	V00
10	L1T1-1310-404-CON-ED-EST-MO-0001.rvt	V00
11	L1T1-1410-304-CON-ED-MEC-MO-0001.rvt	V00
12	L1T1-1420-404-CON-ED-MEC-MO-0001.rvt	V00
13	L1T1-5160-304-CON-ED-EST-MO-0001.rvt	V00
14	L1T1-5160-304-CON-ED-ARQ-MO-0001.rvt	V00
15	L1T1-5300-304-CON-ED-MEC-MO-0001.rvt	V00
16	L1T1-5600-304-CON-ED-INS-MO-0001.rvt	V00
17	L1T1-1330-404-CON-ED-ARQ-MO-0011.rvt	V00
18	L1T1-1330-404-CON-ED-ARQ-MO-0012.rvt	V00

No.	PAQUETE DE TRABAJO DE REFERENCIA	REV.
1	XREF-URBANISM_CONTEXT_ST04.rvt	
2	XREF-SECONDARY-STRUCTURE-ST04.rvt	

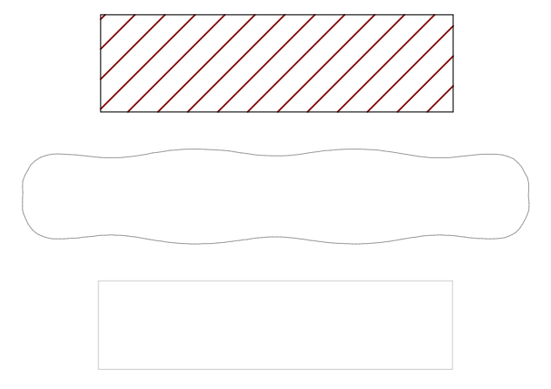

PLANO CLAVE ESTACIÓN 4

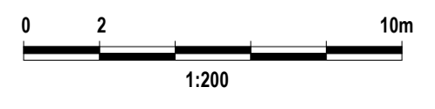

VÁLIDO PARA CONSTRUCCIÓN
01-03-26

METRO BOGOTÁ
Consorcio Consultores PMO Bogotá
CONSORCIO SUPERVISOR PLMB

DISEÑÓ:
REN ZHENHUA
Licencia de Arq.nivel I (China): 1101735-614

APROBÓ:
DIEGO ERNESTO DUEÑAS
Mat.: 25202-53876 CND

REVISÓ:
CARLOS MAURICIO BARRETO BARBOSA
Mat.: A4012012-14139353

DIBUJÓ:
EQUIPO CHEC

REVISIÓN No.	FECHA	DESCRIPCIÓN	REVISÓ	APROBÓ	APROBACIÓN CLIENTE
V01	01/03/2026	EMITIDO PARA CONSTRUCCIÓN	C.M.B.B	D.E.D	
V00	20/12/2024	REVISIÓN NO OBJETADA - EMITIDO PARA CONSTRUCCIÓN	F.B.R	E.O.M	
VFF	28/06/2024	EMITIDO PARA REVISIÓN Y COMENTARIOS DEL CLIENTE E INTERVENTORÍA - INCLUYE COMENTARIOS /(AJUSTES V3)	F.B.R	E.O.M	
VEE	01/09/2023	EMITIDO PARA REVISIÓN Y COMENTARIOS DEL CLIENTE E INTERVENTORÍA - INCLUYE COMENTARIOS /(AJUSTES V2)	J.E.M	M.B.M	
VDD	18/12/2022	EMITIDO PARA REVISIÓN Y COMENTARIOS DEL CLIENTE E INTERVENTORÍA - INCLUYE COMENTARIOS /(AJUSTES)	J.E.M	M.B.M	
VCC	02/06/2022	EMITIDO PARA REVISIÓN Y COMENTARIOS DEL CLIENTE E INTERVENTORÍA - INCLUYE COMENTARIOS /(ENTREGA 90%)	J.E.M	M.B.M	
VBB	06/12/2021	EMITIDO PARA REVISIÓN Y COMENTARIOS DEL CLIENTE E INTERVENTORÍA	J.E.M	M.B.M	
VA0	30/06/2021	EMITIDO PARA COMENTARIOS INTERNOS - EMISIÓN PRELIMINAR PARA COMENTARIOS	J.E.M	M.B.M	

METRO LÍNEA 1

METRO LÍNEA 1
CONTRATO DE CONCESIÓN No. 163 DE 2019

PROYECTO PRIMERA LÍNEA DEL METRO DE BOGOTÁ - TRAMO 1

DIRECTOR DE INTERVENTORÍA:
JAVIER DESCARGA N.
Mat.:25202-68697 CND

ESPECIALISTA INTERVENTORÍA:
CARLOS ALBERTO HOYOS SOTO
Mat.:A25072000-14251682

FECHA:
MARZO 2026

INFRAESTRUCTURA VIAL

ARQUITECTURA

ESTACIÓN METRO 4 (CALLE 42 SUR)
EDIFICIO DESCENDENTE
VISTA EN PLANTA Y 3D - NIVEL SÓTANO

PLANCHA No: L1T1-0000-304-CON-ED-ARQ-PL-0001_04_V01
ARCHIVO: L1T1-0000-304-CON-ED-ARQ-MO-0001_V00.rvt
ESCALA: INDICADA
FECHA: JUNIO 2021
REVISIÓN No. V01
PLANO No. 04 DE 97