L1T1-CON-CAL-FR-0120 - B1 : 1000x707mm

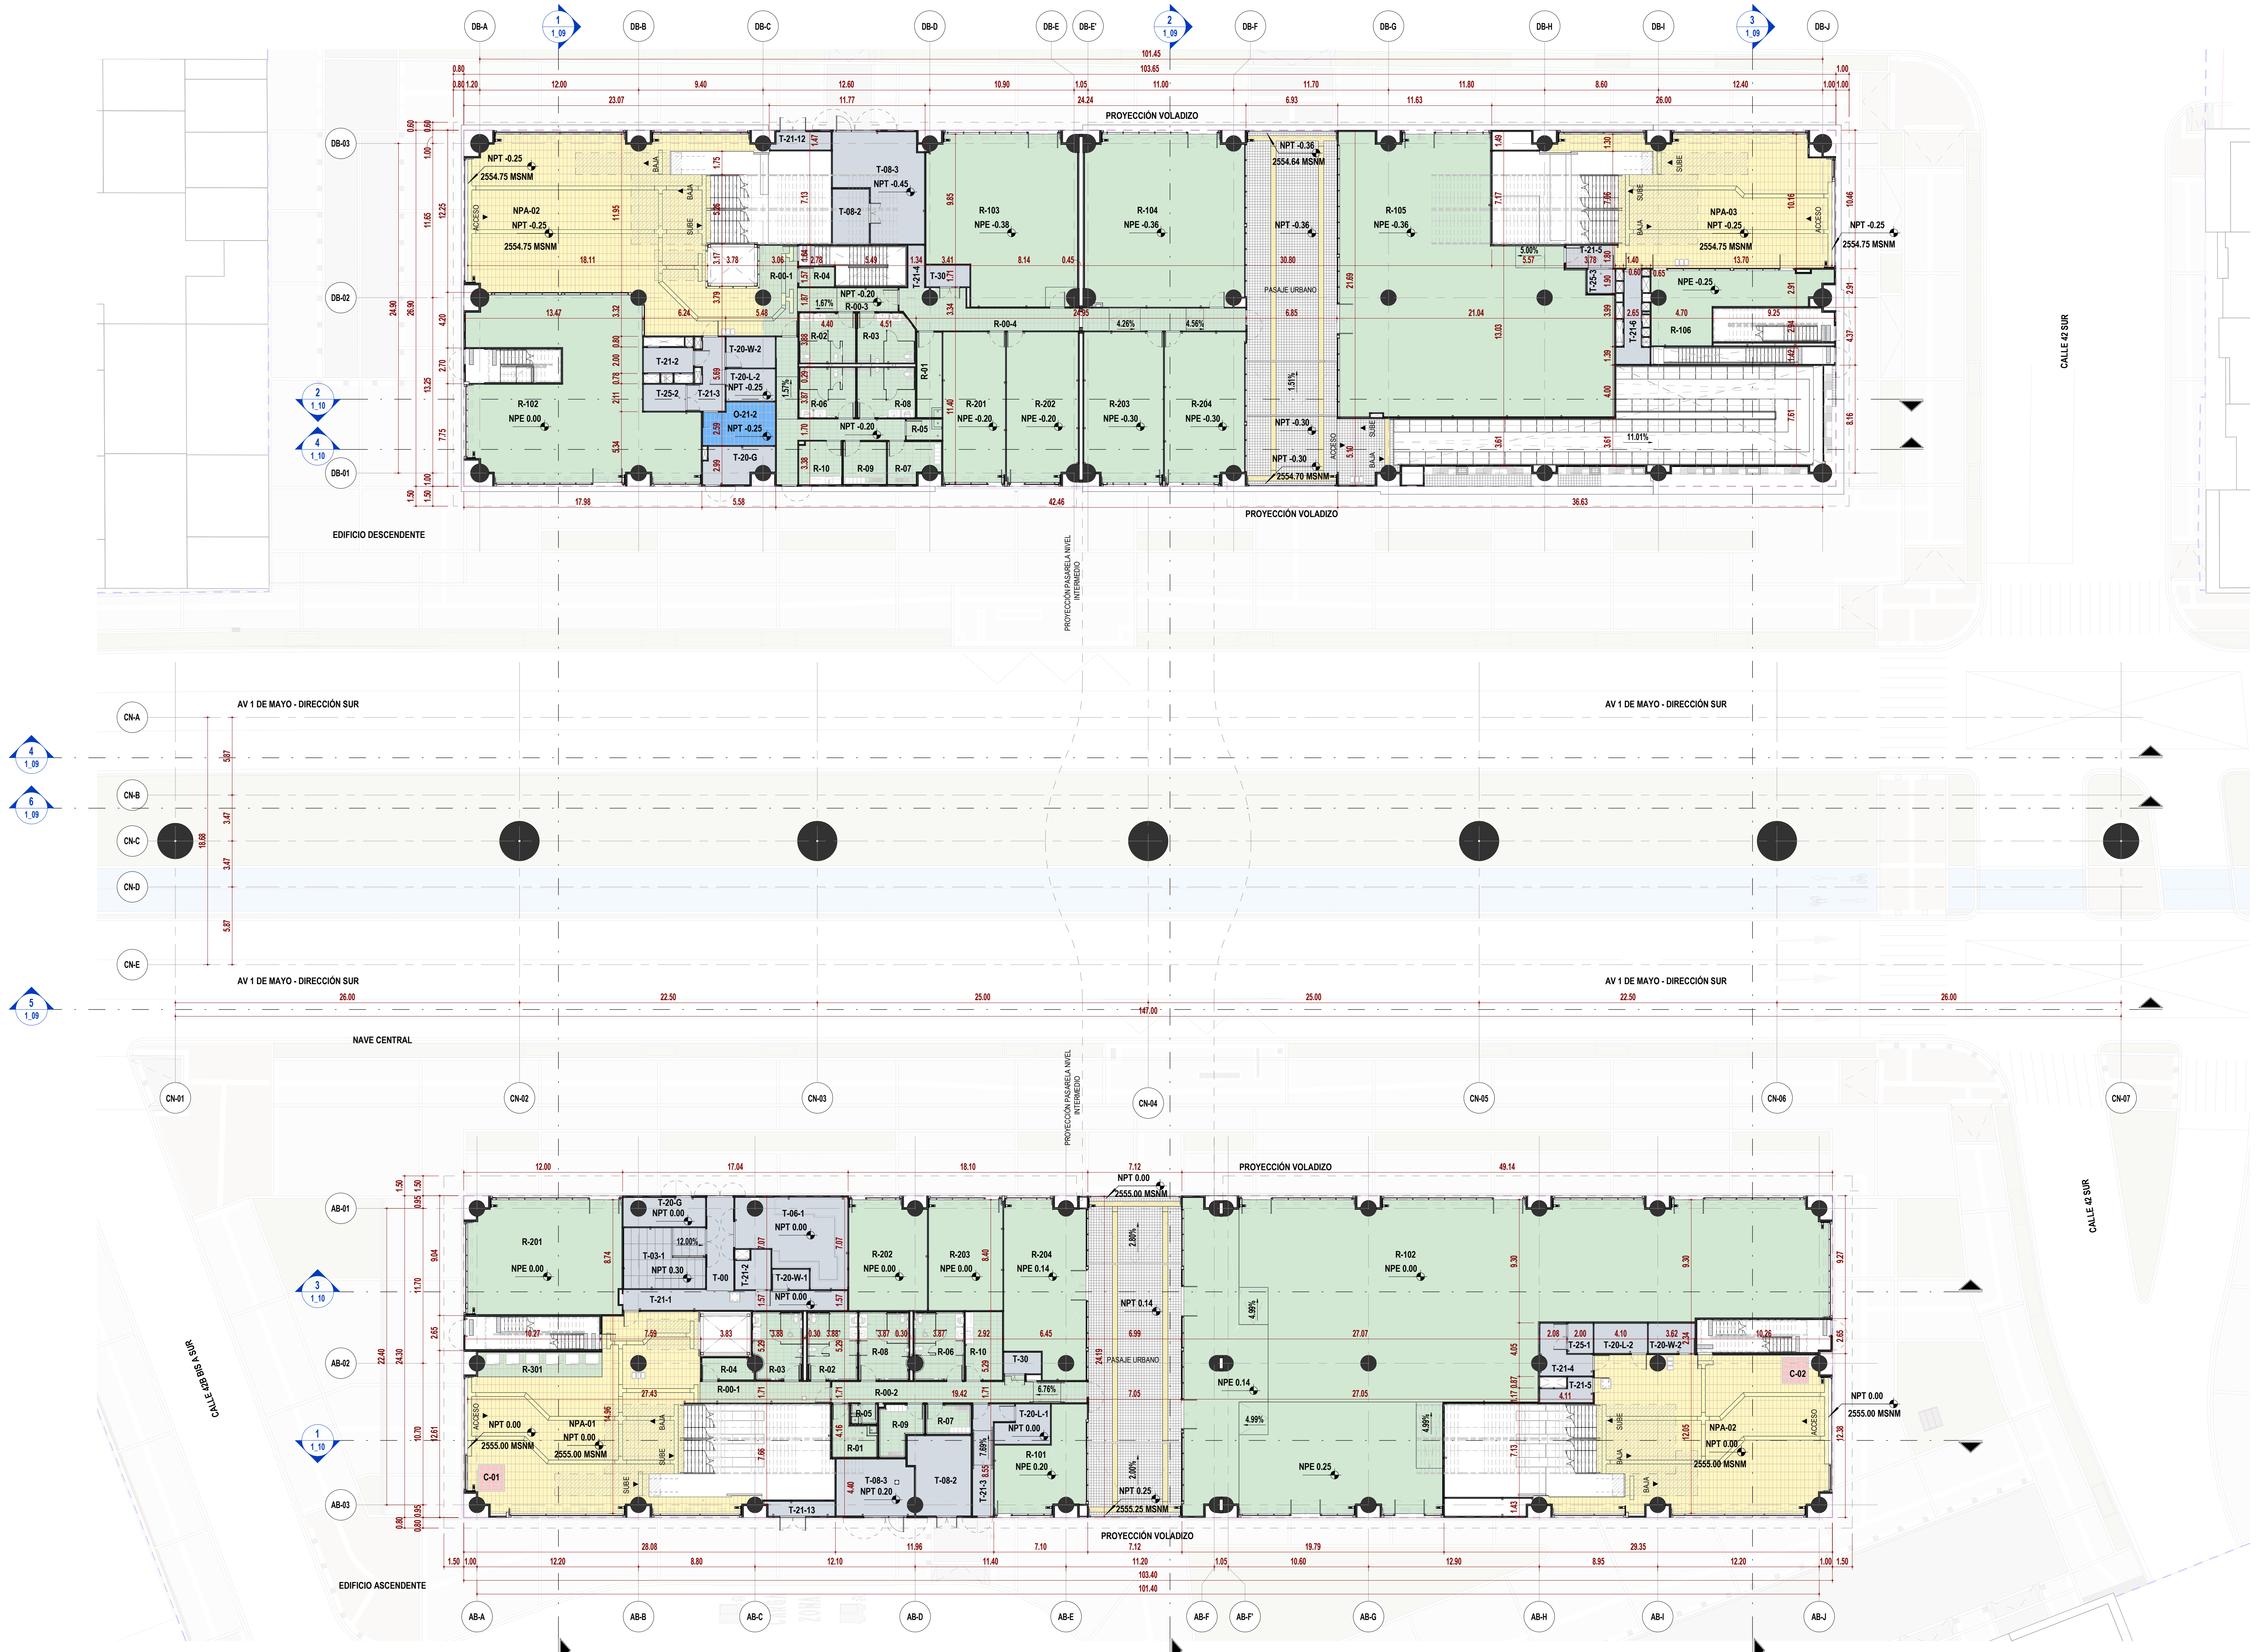

2 NIVEL ACCESO_GENERAL
ESC.: 1:200

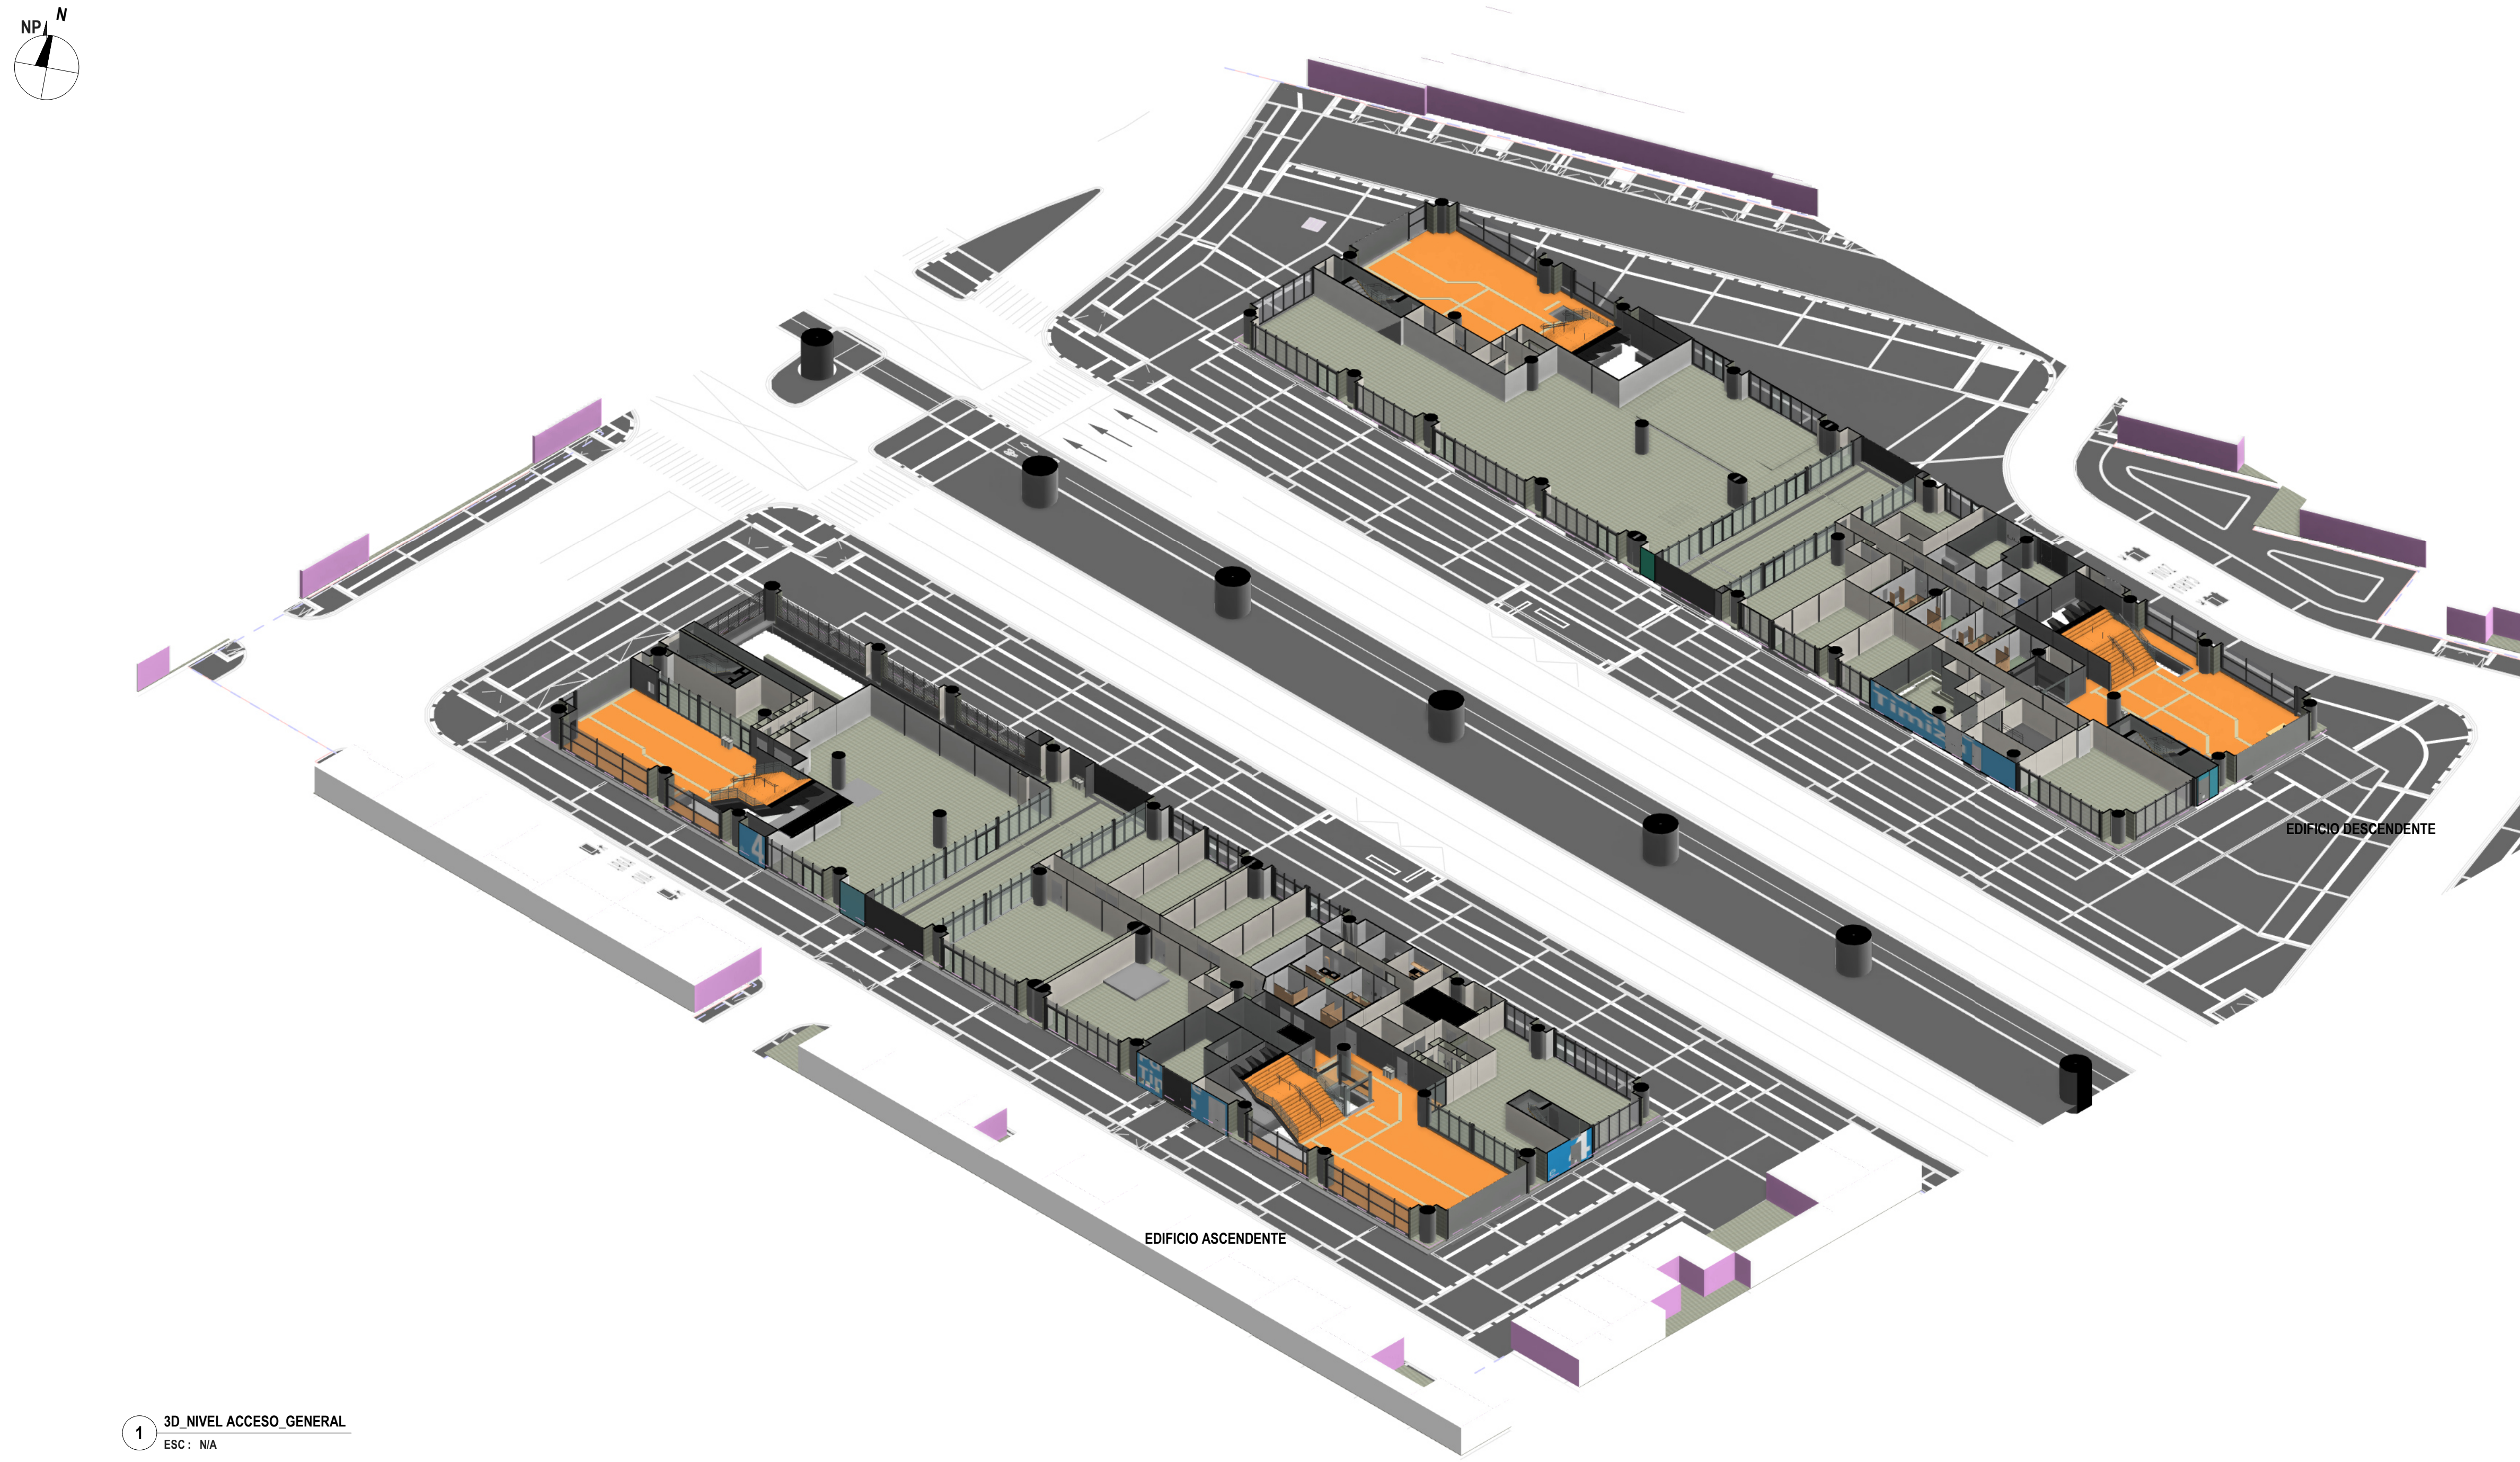

1 3D_NIVEL ACCESO_GENERAL
ESC : N/A

TABLA ÁREAS ÚTILES (NIVEL ACCESO)

CÓDIGO	NOMBRE	ÁREA (m²)	DEPARTAMENTO
EDIFICIO ASCENDENTE			
ARQ_PL_01_ACCESO			
C-01	ÁREAS DE USO CULTURAL	4.00	ÁREA CULTURAL
C-02	ÁREAS DE USO CULTURAL	4.00	ÁREA CULTURAL
NPA-01	ÁREA NO PAGA	200.84	ÁREA NO PAGA
NPA-02	ÁREA NO PAGA	199.58	ÁREA NO PAGA
R-00-1	SERVICIOS ADICIONALES - CORREDOR OPERATIVO	15.66	SERVICIOS ADICIONALES - ÁREA NO PAGA
R-00-2	SERVICIOS ADICIONALES - CORREDOR OPERATIVO	31.69	SERVICIOS ADICIONALES - ÁREA NO PAGA
R-01	SERVICIOS ADICIONALES - CUARTO DE BASURAS PARA METRO	10.21	SERVICIOS ADICIONALES - ÁREA NO PAGA
R-02	SERVICIOS ADICIONALES - BAÑO PÚBLICO DE MUJERES	18.84	SERVICIOS ADICIONALES - ÁREA NO PAGA
R-03	SERVICIOS ADICIONALES - BAÑO PÚBLICO DE HOMBRES	17.80	SERVICIOS ADICIONALES - ÁREA NO PAGA
R-04	SERVICIOS ADICIONALES - CONTROL DE ACCESO BAÑOS PÚBLICOS	6.16	SERVICIOS ADICIONALES - ÁREA NO PAGA
R-05	SERVICIOS ADICIONALES - CUARTO DE LIMPIEZA	2.88	SERVICIOS ADICIONALES - ÁREA NO PAGA
R-06	SERVICIOS ADICIONALES - BAÑOS EMPLEADOS MUJERES	18.31	SERVICIOS ADICIONALES - ÁREA NO PAGA
R-07	SERVICIOS ADICIONALES - VESTIDORES EMPLEADOS MUJERES	7.57	SERVICIOS ADICIONALES - ÁREA NO PAGA
R-08	SERVICIOS ADICIONALES - BAÑOS EMPLEADOS HOMBRES	18.89	SERVICIOS ADICIONALES - ÁREA NO PAGA
R-09	SERVICIOS ADICIONALES - VESTIDORES EMPLEADOS HOMBRES	10.94	SERVICIOS ADICIONALES - ÁREA NO PAGA
R-10	SERVICIOS ADICIONALES - SALA DE EMPLEADOS	14.49	SERVICIOS ADICIONALES - ÁREA NO PAGA
R-102	SERVICIOS ADICIONALES - ÁREA DE SERVICIO	754.10	SERVICIOS ADICIONALES - ÁREA NO PAGA
R-201	SERVICIOS ADICIONALES - ÁREA DE COMIDAS	98.33	SERVICIOS ADICIONALES - ÁREA NO PAGA
R-202	SERVICIOS ADICIONALES - ÁREA DE COMIDAS	47.42	SERVICIOS ADICIONALES - ÁREA NO PAGA
R-203	SERVICIOS ADICIONALES - ÁREA DE COMIDAS	46.62	SERVICIOS ADICIONALES - ÁREA NO PAGA
R-301	SERVICIOS ADICIONALES - MÁQUINAS EXPENDEDORAS/CAJEROS AUTOMÁTICOS	16.85	SERVICIOS ADICIONALES - ÁREA NO PAGA
T-00	CIRCULACIÓN TÉCNICA	14.37	ÁREA TÉCNICA
T-03-1	LOCAL SECUNDARIO DE TELECOMUNICACIONES	28.07	ÁREA TÉCNICA
T-06-1	LOCAL SECUNDARIO DE TABLEROS	44.00	ÁREA TÉCNICA
T-20-G	MEDIDORES (GAS)	12.29	ÁREA TÉCNICA
T-20-L-1	MEDIDORES (LUZ)	10.30	ÁREA TÉCNICA
T-20-L-2	MEDIDORES (LUZ)	8.84	ÁREA TÉCNICA
T-20-W-1	MEDIDORES (AGUA)	4.18	ÁREA TÉCNICA
T-20-W-2	MEDIDORES (AGUA)	7.73	ÁREA TÉCNICA
T-21-1	ÁREA DE INSPECCIÓN	25.13	ÁREA TÉCNICA
T-21-2	ÁREA DE INSPECCIÓN	7.09	ÁREA TÉCNICA
T-21-3	ÁREA DE INSPECCIÓN	15.10	ÁREA TÉCNICA
T-21-4	ÁREA DE INSPECCIÓN	10.47	ÁREA TÉCNICA
T-21-5	ÁREA DE INSPECCIÓN	5.77	ÁREA TÉCNICA
T-25-1	NODO DE ACCESO DE TELECOMUNICACIONES	4.23	ÁREA TÉCNICA
T-30	SISTEMA PROTECCIÓN CONTRA INCENDIO ENEL	4.48	ÁREA TÉCNICA
		1747.22	
ARQ_PL_01.1_ACCESO			
R-101	SERVICIOS ADICIONALES - ÁREA DE SERVICIO	41.46	SERVICIOS ADICIONALES - ÁREA NO PAGA
R-204	SERVICIOS ADICIONALES - ÁREA DE COMIDAS	74.42	SERVICIOS ADICIONALES - ÁREA NO PAGA
T-08-2	CENTRO DE TRANSFORMACIÓN ENEL-CODENSA (CT)_CUARTO BAJA TENSIÓN	26.14	ÁREA TÉCNICA
T-08-3	CENTRO DE TRANSFORMACIÓN ENEL-CODENSA (CT)_CUARTO MEDIA TENSIÓN	24.42	ÁREA TÉCNICA
T-21-13	ÁREA DE INSPECCIÓN	5.58	ÁREA TÉCNICA
		172.02	
EDIFICIO DESCENDENTE			
ARQ_PL_00.2_ACCESO			
T-08-2	CENTRO DE TRANSFORMACIÓN ENEL-CODENSA (CT)_CUARTO BAJA TENSIÓN	11.20	ÁREA TÉCNICA
T-08-3	CENTRO DE TRANSFORMACIÓN ENEL-CODENSA (CT)_CUARTO MEDIA TENSIÓN	45.14	ÁREA TÉCNICA
T-21-12	ÁREA DE INSPECCIÓN	5.64	ÁREA TÉCNICA
		61.98	

TABLA ÁREAS ÚTILES (NIVEL ACCESO)

CÓDIGO	NOMBRE	ÁREA (m²)	DEPARTAMENTO
ARQ_PL_00.3_ACCESO			
R-00-5	SERVICIOS ADICIONALES - CORREDOR OPERATIVO	20.77	SERVICIOS ADICIONALES - ÁREA NO PAGA
R-103	SERVICIOS ADICIONALES - ÁREA DE SERVICIO	134.29	SERVICIOS ADICIONALES - ÁREA NO PAGA
R-104	SERVICIOS ADICIONALES - ÁREA DE SERVICIO	151.26	SERVICIOS ADICIONALES - ÁREA NO PAGA
R-105	SERVICIOS ADICIONALES - ÁREA DE SERVICIO	344.61	SERVICIOS ADICIONALES - ÁREA NO PAGA
		650.93	
ARQ_PL_00.4_ACCESO			
R-203	SERVICIOS ADICIONALES - ÁREA DE COMIDAS	66.38	SERVICIOS ADICIONALES - ÁREA NO PAGA
R-204	SERVICIOS ADICIONALES - ÁREA DE COMIDAS	66.37	SERVICIOS ADICIONALES - ÁREA NO PAGA
		132.75	
ARQ_PL_00.5_ACCESO			
NPA-02	ÁREA NO PAGA	241.66	ÁREA NO PAGA
NPA-03	ÁREA NO PAGA	159.86	ÁREA NO PAGA
O-21-2	ALMACENAMIENTO DE LA ESTACIÓN	16.38	ÁREA OPERATIVA
R-00-1	SERVICIOS ADICIONALES - CORREDOR OPERATIVO	18.44	SERVICIOS ADICIONALES - ÁREA NO PAGA
R-00-2	SERVICIOS ADICIONALES - CORREDOR OPERATIVO	30.76	SERVICIOS ADICIONALES - ÁREA NO PAGA
R-00-3	SERVICIOS ADICIONALES - CORREDOR OPERATIVO	13.32	SERVICIOS ADICIONALES - ÁREA NO PAGA
R-04	SERVICIOS ADICIONALES - CONTROL DE ACCESO BAÑOS PÚBLICOS	3.83	SERVICIOS ADICIONALES - ÁREA NO PAGA
R-106	SERVICIOS ADICIONALES - ÁREA DE SERVICIO	46.80	SERVICIOS ADICIONALES - ÁREA NO PAGA
T-20-L-2	MEDIDORES (LUZ)	8.79	ÁREA TÉCNICA
T-20-W-2	MEDIDORES (AGUA)	8.44	ÁREA TÉCNICA
T-21-2	ÁREA DE INSPECCIÓN	7.05	ÁREA TÉCNICA
T-21-3	ÁREA DE INSPECCIÓN	12.46	ÁREA TÉCNICA
T-21-5	ÁREA DE INSPECCIÓN	6.43	ÁREA TÉCNICA
T-21-6	ÁREA DE INSPECCIÓN	10.78	ÁREA TÉCNICA
T-25-2	NODO DE ACCESO DE TELECOMUNICACIONES	6.32	ÁREA TÉCNICA
T-25-3	NODO DE ACCESO DE TELECOMUNICACIONES	3.68	ÁREA TÉCNICA
		594.99	
ARQ_PL_00.6_ACCESO			
R-00-4	SERVICIOS ADICIONALES - CORREDOR OPERATIVO	28.16	SERVICIOS ADICIONALES - ÁREA NO PAGA
R-01	SERVICIOS ADICIONALES - CUARTO DE BASURAS PARA METRO	11.82	SERVICIOS ADICIONALES - ÁREA NO PAGA
R-02	SERVICIOS ADICIONALES - BAÑO PÚBLICO DE MUJERES	15.49	SERVICIOS ADICIONALES - ÁREA NO PAGA
R-03	SERVICIOS ADICIONALES - BAÑO PÚBLICO DE HOMBRES	15.37	SERVICIOS ADICIONALES - ÁREA NO PAGA
R-05	SERVICIOS ADICIONALES - CUARTO DE LIMPIEZA	4.05	SERVICIOS ADICIONALES - ÁREA NO PAGA
R-06	SERVICIOS ADICIONALES - BAÑOS EMPLEADOS MUJERES	15.53	SERVICIOS ADICIONALES - ÁREA NO PAGA
R-07	SERVICIOS ADICIONALES - VESTIDORES EMPLEADOS MUJERES	10.77	SERVICIOS ADICIONALES - ÁREA NO PAGA
R-08	SERVICIOS ADICIONALES - BAÑOS EMPLEADOS HOMBRES	15.97	SERVICIOS ADICIONALES - ÁREA NO PAGA
R-09	SERVICIOS ADICIONALES - VESTIDORES EMPLEADOS HOMBRES	10.21	SERVICIOS ADICIONALES - ÁREA NO PAGA
R-10	SERVICIOS ADICIONALES - SALA DE EMPLEADOS	10.28	SERVICIOS ADICIONALES - ÁREA NO PAGA
R-201	SERVICIOS ADICIONALES - ÁREA DE COMIDAS	53.21	SERVICIOS ADICIONALES - ÁREA NO PAGA
R-202	SERVICIOS ADICIONALES - ÁREA DE COMIDAS	59.57	SERVICIOS ADICIONALES - ÁREA NO PAGA
T-21-4	ÁREA DE INSPECCIÓN	3.91	ÁREA TÉCNICA
T-30	SISTEMA PROTECCIÓN CONTRA INCENDIO ENEL	5.26	ÁREA TÉCNICA
		259.59	
ARQ_PL_01_ACCESO			
R-102	SERVICIOS ADICIONALES - ÁREA DE SERVICIO	182.79	SERVICIOS ADICIONALES - ÁREA NO PAGA
T-20-G	MEDIDORES (GAS)	12.90	ÁREA TÉCNICA
		195.69	
TOTAL NIVEL ACCESO		3815.17	

TABLA ÁREAS ÚTILES POR DEPARTAMENTO (NIVEL ACCESO)

DEPARTAMENTO	ÁREA (m²)
EDIFICIO ASCENDENTE	
ARQ_PL_01_ACCESO	
SERVICIOS ADICIONALES - ÁREA NO PAGA	1136.74
ÁREA CULTURAL	8.00
ÁREA NO PAGA	400.42
ÁREA TÉCNICA	202.07
ARQ_PL_01.1_ACCESO	
SERVICIOS ADICIONALES - ÁREA NO PAGA	115.88
ÁREA TÉCNICA	56.14
EDIFICIO DESCENDENTE	
ARQ_PL_00.2_ACCESO	
ÁREA TÉCNICA	61.98
ARQ_PL_00.3_ACCESO	
SERVICIOS ADICIONALES - ÁREA NO PAGA	650.93
ARQ_PL_00.4_ACCESO	
SERVICIOS ADICIONALES - ÁREA NO PAGA	132.75
ARQ_PL_00.5_ACCESO	
SERVICIOS ADICIONALES - ÁREA NO PAGA	113.15
ÁREA NO PAGA	401.52
ÁREA OPERATIVA	16.38
ÁREA TÉCNICA	63.94
ARQ_PL_00.6_ACCESO	
SERVICIOS ADICIONALES - ÁREA NO PAGA	250.42
ÁREA TÉCNICA	9.17
ARQ_PL_01_ACCESO	
SERVICIOS ADICIONALES - ÁREA NO PAGA	182.79
ÁREA TÉCNICA	12.90
TOTAL NIVEL ACCESO	3815.17

LOCALIZACIÓN

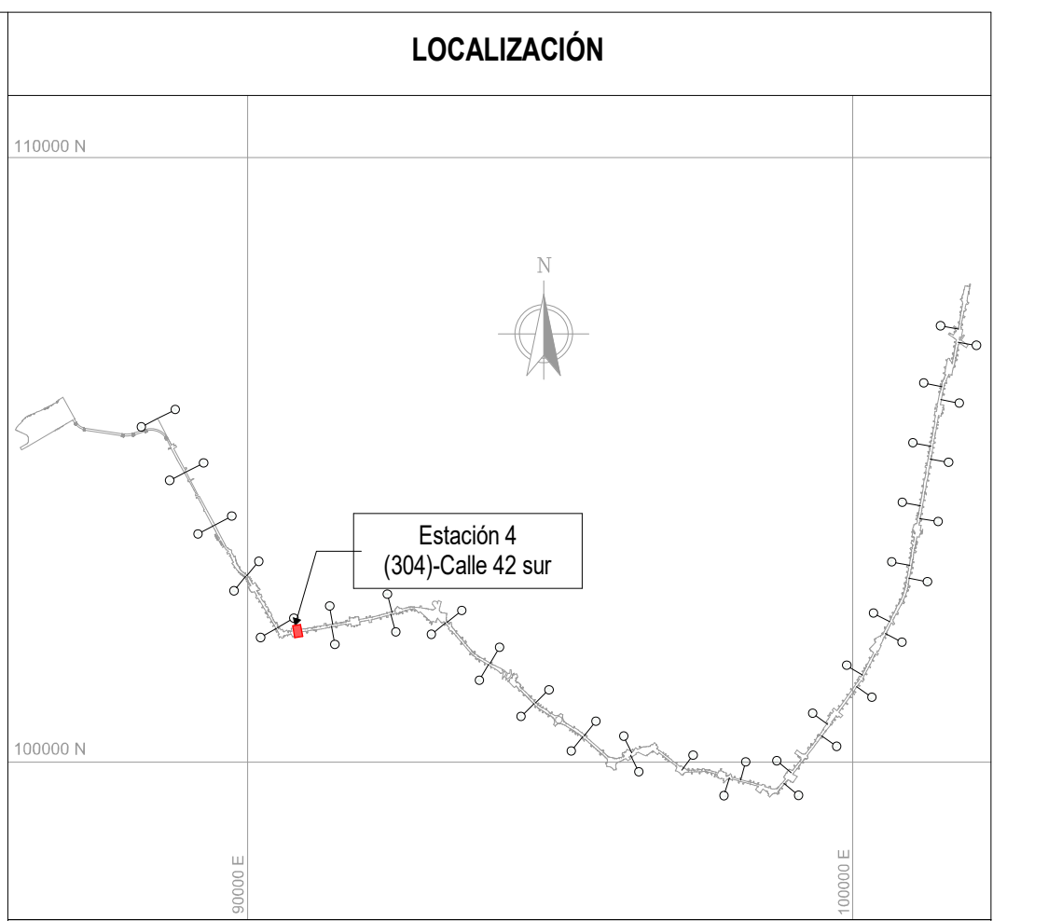

NOTAS

01 TODAS LAS DIMENSIONES ESTÁN CONFIGURADAS EN METROS A MENOS QUE SE INDIQUE UNA UNIDAD DE MEDIDA DIFERENTE.

02 TODAS LAS MEDIDAS, UBICACIÓN Y NIVELES DEBEN VERIFICARSE EN EL LUGAR DE CONSTRUCCIÓN.

03 EL NIVEL DE ACCESO AL EDIFICIO PL 01 CORRESPONDE AL +0,00 DE LA ESTACIÓN Y REFERENCIA AL NIVEL 2555.00 M.S.N.M

04 LOS NOMBRES ESPECÍFICOS DE LAS ÁREAS PUEDEN SER CONSULTADAS EN EL PLANO NO. 3 Ó EN LAS VISTAS EN PLANTA.

05 LOS COLORES QUE SE MUESTRAN EN LOS PLANOS COMO PROYECCIÓN DE ELEMENTOS ARQUITECTÓNICOS COMO CUBIERTAS, FACHADAS, MUROS, ETC. NO REPRESENTAN LA MATERIALIDAD Y REALIDAD DE ACABADOS DEL PROYECTO, SOLO SON INDICATIVOS PARA REALIZAR UNA CORRECTA LECTURA DE LA PLANIMETRÍA.

06 LAS ESCALERAS ELÉCTRICAS INDICAN SU SENTIDO CON LA SIGUIENTE NOMENCLATURA: “SUBE” Y “BAJA”.

07 SE DEBEN REVISAR LOS NIVELES ESTRUCTURALES PARA NIVEL DE ACCESO PL_01 Y SUBNIVELES, PL_02 (INTERMEDIO), PL_03 (PLATAFORMA) CON LA PLANIMETRÍA DE PLACAS ESTRUCTURALES EN LOS ENTREGABLES L1T1-1300-404-CON-ED-EST-PL-0038, 39, 88, 89, 92, 93, RESPECTIVAMENTE. EL NIVEL ESTRUCTURAL (NE) REFERENCIA LOS ESPACIOS DONDE SE DEBE ACONDICIONAR EL ACABADO DE PISO SEGÚN CORRESPONDA, CON LOS NIVELES DE PISO TERMINADO (NPT). LOS NIVELES PROYECTADOS DE EMPATE (NPE) EN LAS ÁREAS DE SERVICIOS ADICIONALES, REFERENCIAN LA ADECUACIÓN DE LOS DESNIVELES EN ESTAS ÁREAS; QUEDA COMO RESPONSABILIDAD DEL LOCATARIO DEFINIR Y ACONDICIONAR ESTE ACABADO DE PISO (NPE) EN LÍNEA CON EL NIVEL (NPT) DE ESPACIOS COLINDANTES. EL NIVEL ESTRUCTURAL (NE) SE ENCUENTRA A (- 0.10M) POR DEBAJO DE LOS NIVELES DE PISO TERMINADO (NPT) Y LOS NIVELES PROYECTADOS DE EMPATE (NPE) MARCADOS EN LA PLANIMETRÍA.

- ARQ_PL_00 = SÓTANO / NPT -6.90m
- ARQ_PL_00.1 = ACCESO / NPT -0.50m
- ARQ_PL_00.2 = ACCESO / NPT -0.45m
- ARQ_PL_00.3 = ACCESO / NPT -0.38m
- ARQ_PL_00.4 = ACCESO / NPT -0.30m
- ARQ_PL_00.5 = ACCESO / NPT -0.25m
- ARQ_PL_00.6 = ACCESO / NPT -0.20m
- ARQ_PL_01 = ACCESO / NPT 0.00m
- ARQ_PL_01.1 = ACCESO / NPT 0.14m
- ARQ_PL_01.2 = ACCESO / NPT 0.25m
- ARQ_PL_02 = INTERMEDIO / NPT 6.60m
- ARQ_PL_02.2 = TOPE DE RIEL (TOR) / NPT 14.20m
- ARQ_PL_03 = PLATAFORMA / NPT 15.34m
- ARQ_PL_04 = CUBIERTA EDIFICACIONES / NPT 21.94m
- ARQ_PL_05 = CUBIERTA NAVE CENTRAL / NPT 24.59m

CONVENCIONES

- - - -	LÍMITE DE INTERVENCIÓN
- - - -	HUELLA APÉNDICE TÉCNICO
▬	MURO DIVISORIO
— — —	PROYECCIÓN NIVEL SUPERIOR
🟩	SERVICIOS ADICIONALES - ÁREA NO PAGA
🟩	SERVICIOS ADICIONALES - ÁREA PAGA
🟩	SERVICIO PÚBLICO
🟦	ZONA DE REFUGIO
🟥	ÁREA CULTURAL
🟨	ÁREA NO PAGA
🟦	ÁREA OPERATIVA
🟧	ÁREA PAGA
🟦	ÁREA PÚBLICA
⬜	ÁREA TÉCNICA

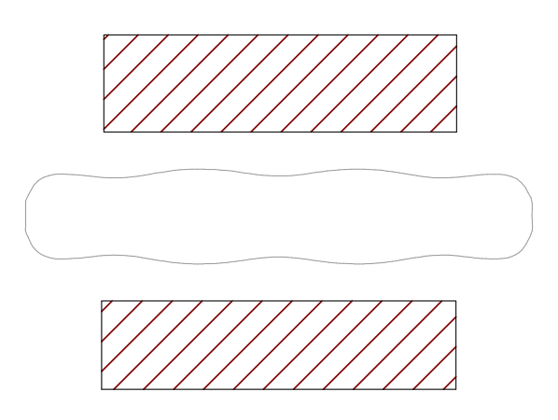

PLANO CLAVE ESTACIÓN 4

No.	PLANOS DE REFERENCIA	REV.

No.	MODELO BIM DE REFERENCIA	REV.
1	L1T1-1100-204-CON-ED-EST-MO-0001.rvt	V00
2	L1T1-1100-205-CON-ED-EST-MO-0001.rvt	V00
3	L1T1-1100-304-CON-ED-EST-MO-0001.rvt	V00
4	L1T1-1150-204-CON-ED-EST-MO-0001.rvt	V00
5	L1T1-1150-205-CON-ED-EST-MO-0001.rvt	V00
6	L1T1-1150-304-CON-ED-EST-MO-0001.rvt	V00
7	L1T1-1200-304-CON-ED-EST-MO-0001.rvt	V00
8	L1T1-1300-404-CON-ED-EST-MO-0001.rvt	V00
9	L1T1-1300-404-CON-ED-EST-MO-0002.rvt	V00
10	L1T1-1310-404-CON-ED-EST-MO-0001.rvt	V00
11	L1T1-1410-304-CON-ED-MEC-MO-0001.rvt	V00
12	L1T1-1420-404-CON-ED-MEC-MO-0001.rvt	V00
13	L1T1-5160-304-CON-ED-EST-MO-0001.rvt	V00
14	L1T1-5160-304-CON-ED-ARQ-MO-0001.rvt	V00
15	L1T1-5300-304-CON-ED-MEC-MO-0001.rvt	V00
16	L1T1-5600-304-CON-ED-INS-MO-0001.rvt	V00
17	L1T1-1330-404-CON-ED-ARQ-MO-0011.rvt	V00
18	L1T1-1330-404-CON-ED-ARQ-MO-0012.rvt	V00

No.	PAQUETE DE TRABAJO DE REFERENCIA	REV.
1	XREF-URBANISM_CONTEXT_ST04.rvt	
2	XREF-SECONDARY-STRUCTURE-ST04.rvt	

0 2 10m
1:200

VÁLIDO PARA CONSTRUCCIÓN
01-03-26

DISEÑÓ:
REN ZHENHUA
Licencia de Arq.nivel I (China): 1101735-614

APROBÓ:
DIEGO ERNESTO DUEÑAS
Mat.: 25202-53876 CND

REVISÓ:
CARLOS MAURICIO BARRETO BARBOSA
Mat.: A4012012-14139353

DIBUJÓ:
EQUIPO CHEC

REVISIÓN No.	FECHA	DESCRIPCIÓN	REVISÓ	APROBÓ	APROBACIÓN CLIENTE
V01	01/03/2026	EMITIDO PARA CONSTRUCCIÓN	C.M.B.B	D.E.D	
V00	20/12/2024	REVISIÓN NO OBJETADA - EMITIDO PARA CONSTRUCCIÓN	F.B.R	E.O.M	
VFF	28/06/2024	EMITIDO PARA REVISIÓN Y COMENTARIOS DEL CLIENTE E INTERVENTORÍA - INCLUYE COMENTARIOS /(AJUSTES V3)	F.B.R	E.O.M	
VEE	01/09/2023	EMITIDO PARA REVISIÓN Y COMENTARIOS DEL CLIENTE E INTERVENTORÍA - INCLUYE COMENTARIOS /(AJUSTES V2)	J.E.M	M.B.M	
VDD	18/12/2022	EMITIDO PARA REVISIÓN Y COMENTARIOS DEL CLIENTE E INTERVENTORÍA - INCLUYE COMENTARIOS /(AJUSTES)	J.E.M	M.B.M	
VCC	02/06/2022	EMITIDO PARA REVISIÓN Y COMENTARIOS DEL CLIENTE E INTERVENTORÍA - INCLUYE COMENTARIOS /(ENTREGA 90%)	J.E.M	M.B.M	
VBB	06/12/2021	EMITIDO PARA REVISIÓN Y COMENTARIOS DEL CLIENTE E INTERVENTORÍA	J.E.M	M.B.M	
VA0	30/06/2021	EMITIDO PARA COMENTARIOS INTERNOS - EMISIÓN PRELIMINAR PARA COMENTARIOS	J.E.M	M.B.M	

METRO LÍNEA 1
CONTRATO DE CONCESIÓN No. 163 DE 2019

PROYECTO PRIMERA LÍNEA DEL METRO DE BOGOTÁ - TRAMO 1

DIRECTOR DE INTERVENTORÍA:
JAVIER DESCARGA N.
Mat.:25202-68697 CND

ESPECIALISTA INTERVENTORÍA:
CARLOS ALBERTO HOYOS SOTO
Mat.:A25072000-14251682

FECHA: MARZO 2026

INFRAESTRUCTURA VIAL
ARQUITECTURA
ESTACIÓN METRO 4 (CALLE 42 SUR)
GENERAL
VISTA EN PLANTA Y 3D - NIVEL ACCESO

PLANCHA No: L1T1-0000-304-CON-ED-ARQ-PL-0001_05_V01
ARCHIVO: L1T1-0000-304-CON-ED-ARQ-MO-0001_V00.rvt
ESCALA: INDICADA
FECHA: JUNIO 2021
REVISIÓN No.: V01
PLANO No.: 05 DE 97