L1T1-CON-CAL-FR-0120 - B1 : 1000x707mm

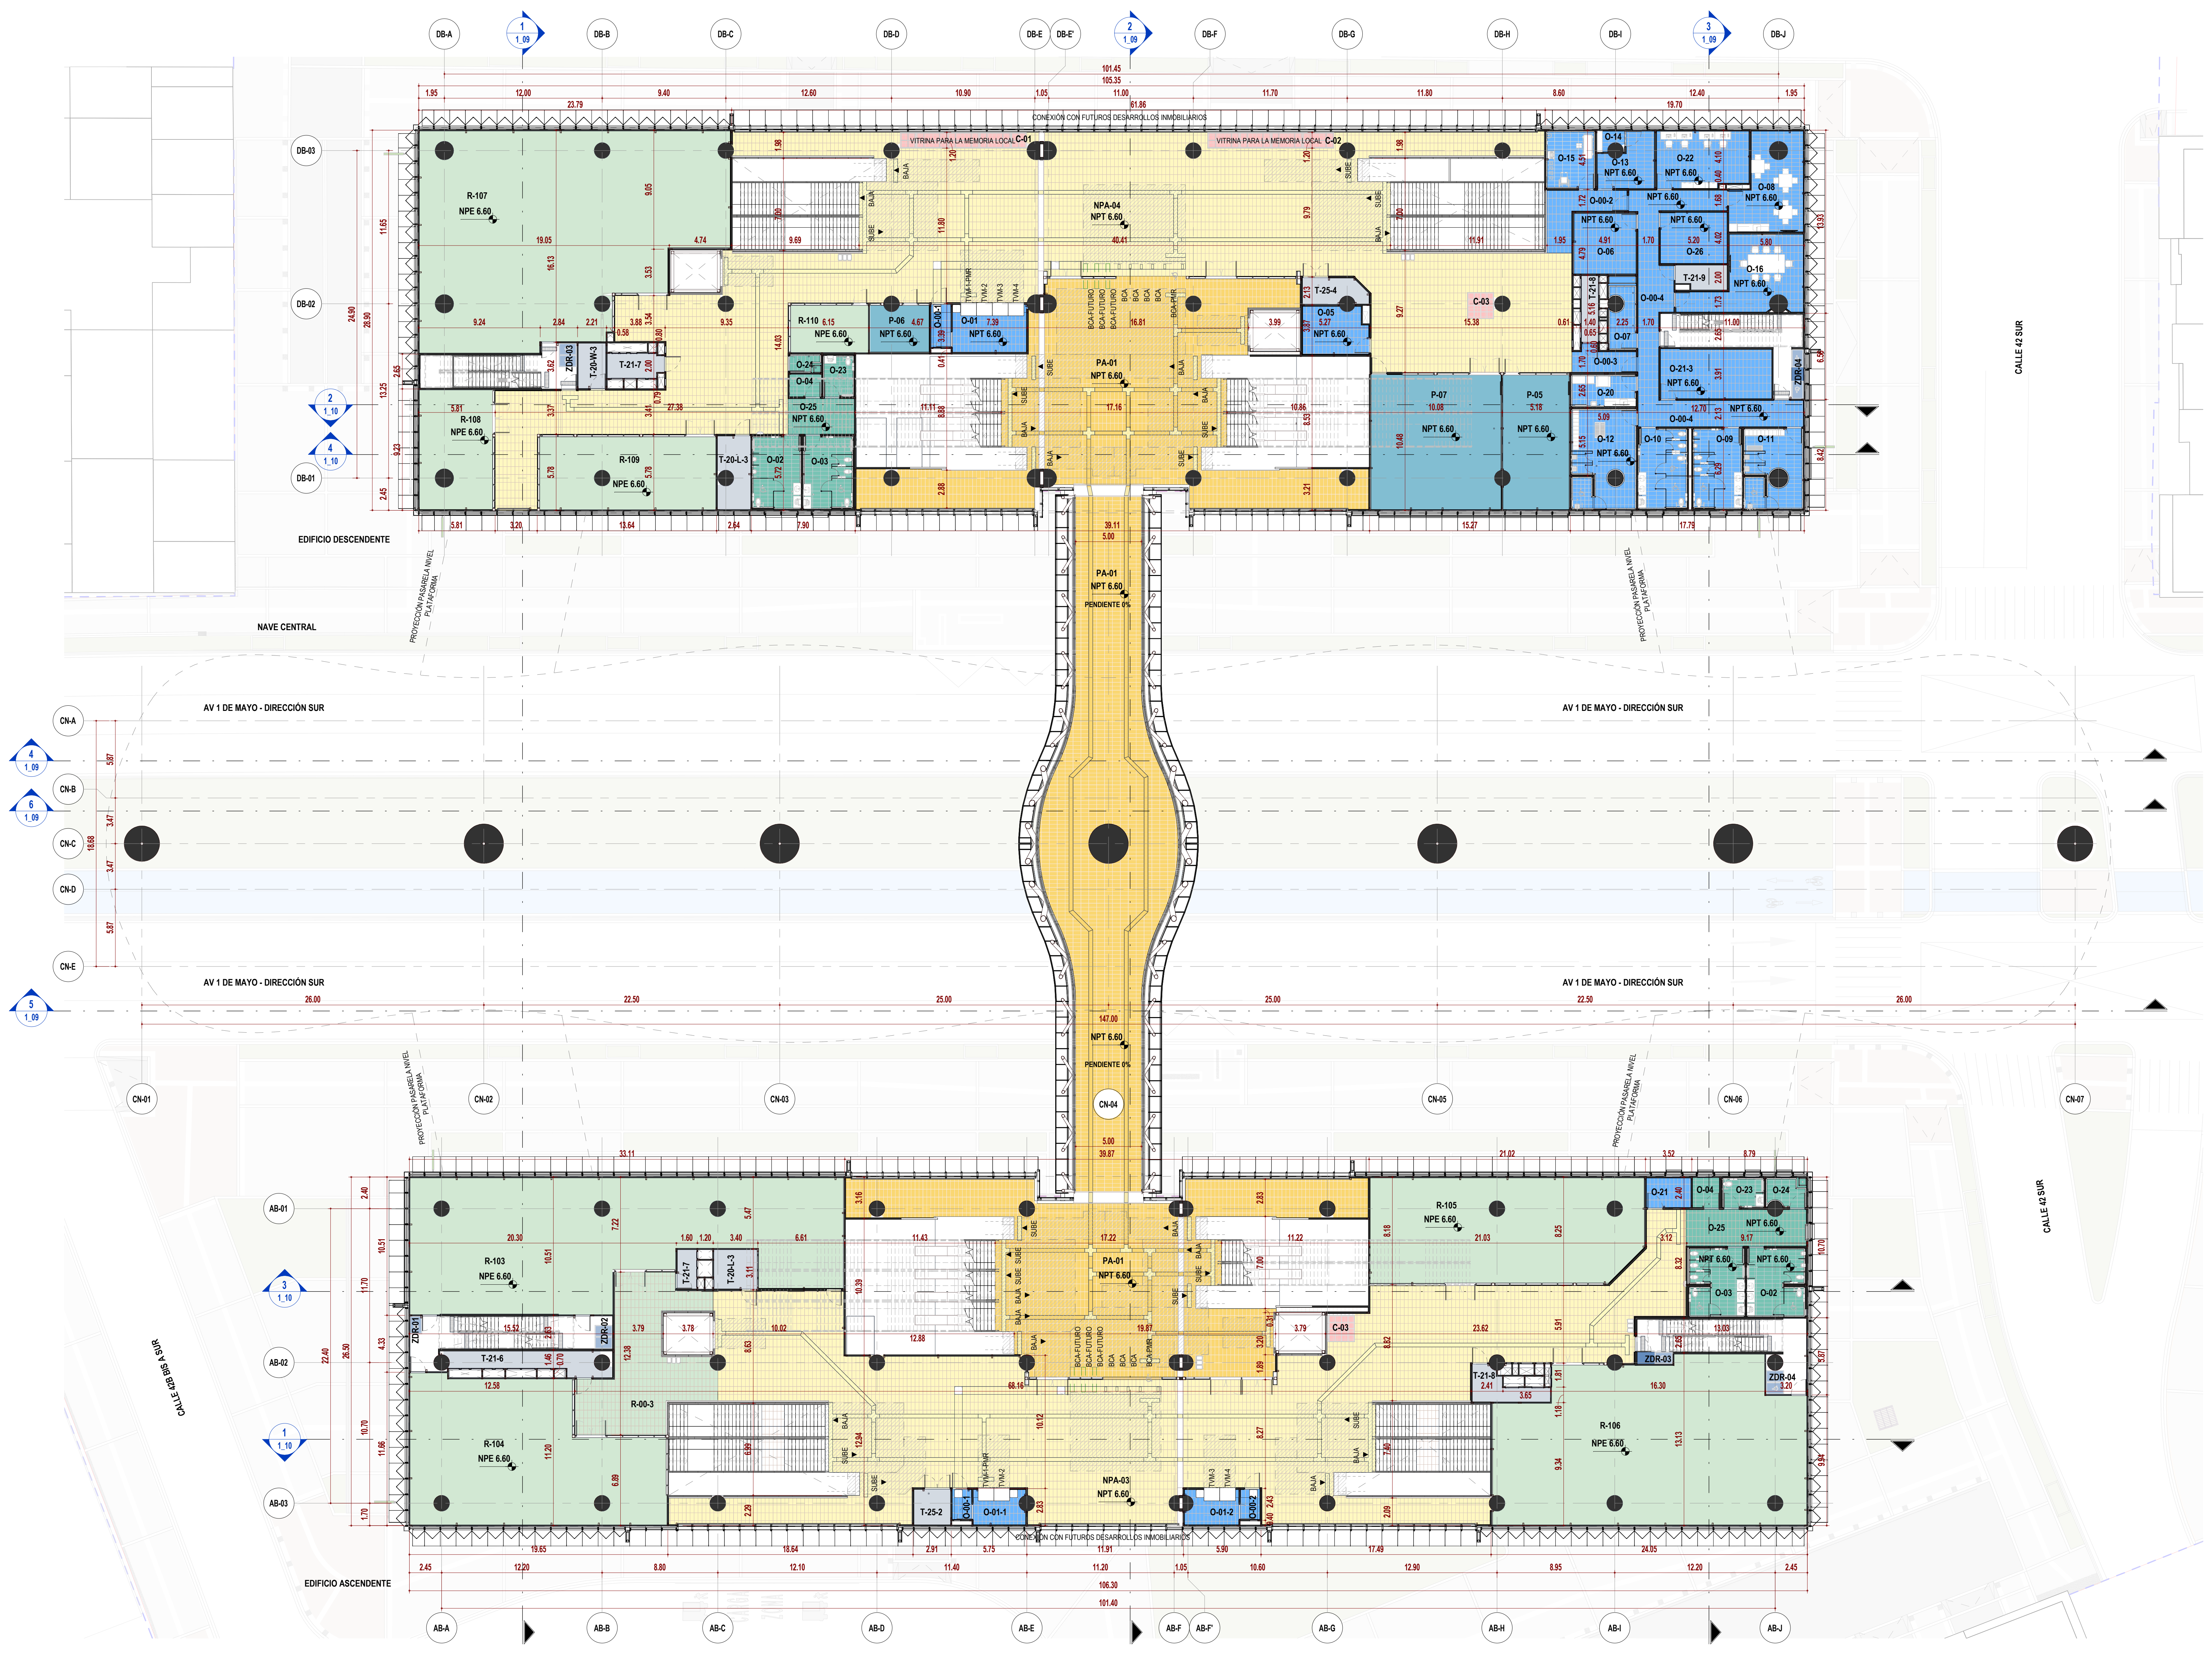

2 NIVEL INTERMEDIO_GENERAL
ESC : 1 : 200

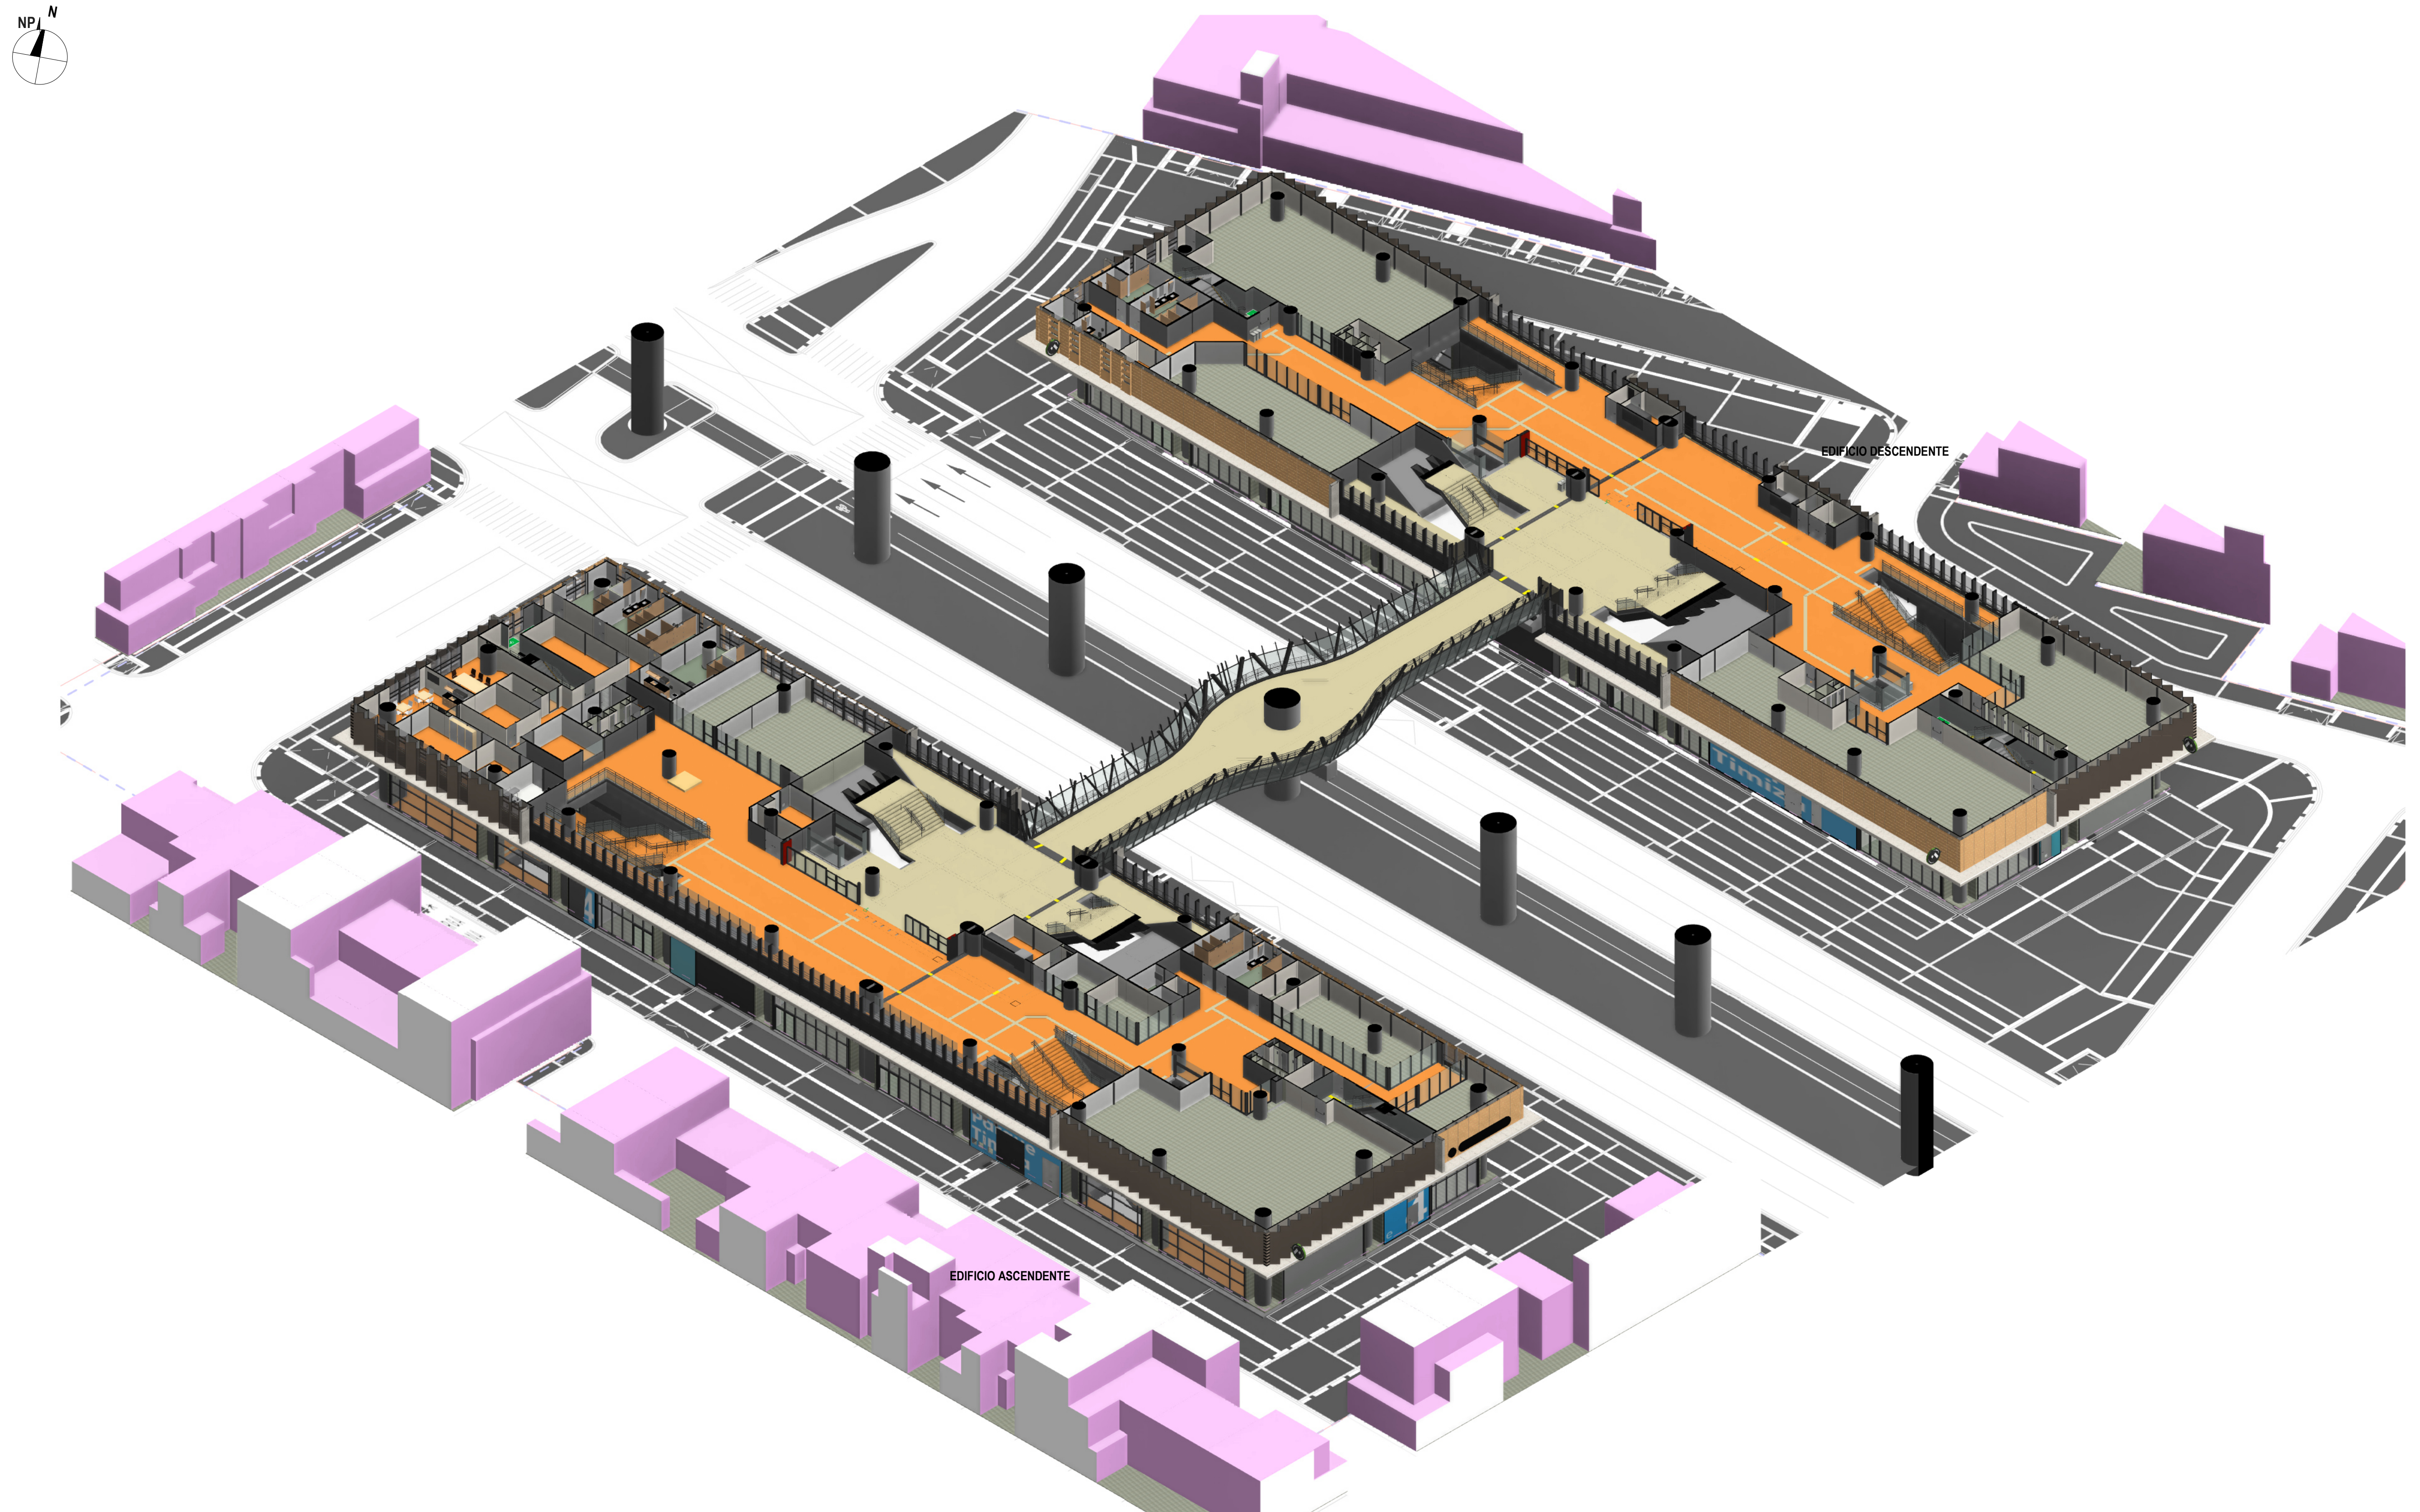

1 3D_NIVEL INTERMEDIO_GENERAL
ESC : N/A

TABLA DE ÁREAS ÚTILES (NIVEL INTERMEDIO)			
CÓDIGO	**NOMBRE**	**ÁREA (m²)**	**DEPARTAMENTO**
EDIFICIO ASCENDENTE			
ARQ_PL_02_INTERMEDIO			
C-03	ÁREAS DE USO CULTURAL	4.00	ÁREA CULTURAL
NPA-03	ÁREA NO PAGA	731.00	ÁREA NO PAGA
O-00-1	CIRCULACIÓN ÁREAS OPERATIVAS	3.45	ÁREA OPERATIVA
O-00-2	CIRCULACIÓN ÁREAS OPERATIVAS	3.45	ÁREA OPERATIVA
O-01-1	VENTA AUTOMÁTICA DE BOLETOS	10.35	ÁREA OPERATIVA
O-01-2	VENTA AUTOMÁTICA DE BOLETOS	10.53	ÁREA OPERATIVA
O-02	BAÑOS PÚBLICOS DE HOMBRES	22.64	SERVICIO PÚBLICO
O-03	BAÑOS PÚBLICOS DE MUJERES	21.63	SERVICIO PÚBLICO
O-04	CONTROL DE ACCESO BAÑOS PÚBLICOS	4.64	SERVICIO PÚBLICO
O-21	ALMACENAMIENTO DE LA ESTACIÓN	7.75	ÁREA OPERATIVA
O-23	BAÑO PÚBLICO - FAMILIAR	7.03	SERVICIO PÚBLICO
O-24	CUARTO DE LIMPIEZA DE BAÑOS PÚBLICOS	6.35	SERVICIO PÚBLICO
O-25	BAÑO PÚBLICO - CORREDOR OPERACIONAL	25.34	SERVICIO PÚBLICO
PA-01	ÁREA PAGA	308.79	ÁREA PAGA
R-00-3	SERVICIOS ADICIONALES - CORREDOR OPERATIVO	79.27	SERVICIOS ADICIONALES - ÁREA NO PAGA
R-103	SERVICIOS ADICIONALES - ÁREA DE SERVICIO	277.68	SERVICIOS ADICIONALES - ÁREA NO PAGA
R-104	SERVICIOS ADICIONALES - ÁREA DE SERVICIO	183.22	SERVICIOS ADICIONALES - ÁREA NO PAGA
R-105	SERVICIOS ADICIONALES - ÁREA DE SERVICIO	160.13	SERVICIOS ADICIONALES - ÁREA NO PAGA
R-106	SERVICIOS ADICIONALES - ÁREA DE SERVICIO	271.74	SERVICIOS ADICIONALES - ÁREA NO PAGA
T-20-L-3	MEDIDORES (LUZ)	9.80	ÁREA TÉCNICA
T-21-6	ÁREA DE INSPECCIÓN	17.34	ÁREA TÉCNICA
T-21-7	ÁREA DE INSPECCIÓN	4.39	ÁREA TÉCNICA
T-21-8	ÁREA DE INSPECCIÓN	9.82	ÁREA TÉCNICA
T-25-2	NODO DE ACCESO DE TELECOMUNICACIONES	7.50	ÁREA TÉCNICA
ZDR-01	ZONA DE REFUGIO (PMR)	1.22	ZONA DE REFUGIO
ZDR-02	ZONA DE REFUGIO (PMR)	2.43	ZONA DE REFUGIO
ZDR-03	ZONA DE REFUGIO (PMR)	2.42	ZONA DE REFUGIO
ZDR-04	ZONA DE REFUGIO (PMR)	2.43	ZONA DE REFUGIO
EDIFICIO ASCENDENTE		2196.35	
EDIFICIO DESCENDENTE			
ARQ_PL_02_INTERMEDIO			
C-01	ÁREAS DE USO CULTURAL	11.46	ÁREA CULTURAL
C-02	ÁREAS DE USO CULTURAL	11.52	ÁREA CULTURAL
C-03	ÁREAS DE USO CULTURAL	4.00	ÁREA CULTURAL
NPA-04	ÁREA NO PAGA	814.03	ÁREA NO PAGA
O-00-1	CIRCULACIÓN ÁREAS OPERATIVAS	4.90	ÁREA OPERATIVA
O-00-2	CIRCULACIÓN ÁREAS OPERATIVAS	16.52	ÁREA OPERATIVA
O-00-3	CIRCULACIÓN ÁREAS OPERATIVAS	8.70	ÁREA OPERATIVA
O-00-4	CIRCULACIÓN ÁREAS OPERATIVAS	64.29	ÁREA OPERATIVA
O-01	VENTA AUTOMÁTICA DE BOLETOS	20.66	ÁREA OPERATIVA
O-02	BAÑOS PÚBLICOS DE HOMBRES	20.46	SERVICIO PÚBLICO
O-03	BAÑOS PÚBLICOS DE MUJERES	20.77	SERVICIO PÚBLICO
O-04	CONTROL DE ACCESO BAÑOS PÚBLICOS	4.08	SERVICIO PÚBLICO
O-05	LOCAL DE INFORMACIÓN	17.29	ÁREA OPERATIVA
O-06	OFICINA DEL SUPERVISOR DE LA ESTACIÓN	21.57	ÁREA OPERATIVA
O-07	CUARTO DE LIMPIEZA	10.65	ÁREA OPERATIVA
O-08	SALA DE DESCANSO PARA EMPLEADOS	34.53	ÁREA OPERATIVA
O-09	BAÑOS EMPLEADOS HOMBRES	22.55	ÁREA OPERATIVA
O-10	BAÑOS EMPLEADOS MUJERES	22.55	ÁREA OPERATIVA
O-11	VESTIDORES EMPLEADOS HOMBRES	25.43	ÁREA OPERATIVA
O-12	VESTIDORES EMPLEADOS MUJERES	35.97	ÁREA OPERATIVA
O-13	LOCAL DE POLICÍA	15.02	ÁREA OPERATIVA
O-14	CALABOZO	2.59	ÁREA OPERATIVA
O-15	LOCAL PRIMEROS AUXILIOS	16.34	ÁREA OPERATIVA
O-16	SALA DE REUNIONES	38.23	ÁREA OPERATIVA
O-20	SALA DE LACTANCIA	11.98	ÁREA OPERATIVA
O-21-3	ALMACENAMIENTO DE LA ESTACIÓN	32.10	ÁREA OPERATIVA
O-22	OFICINA DE MANTENIMIENTO	30.01	ÁREA OPERATIVA
O-23	BAÑO PÚBLICO - FAMILIAR	7.32	SERVICIO PÚBLICO
O-24	CUARTO DE LIMPIEZA DE BAÑOS PÚBLICOS	3.29	SERVICIO PÚBLICO
O-25	BAÑO PÚBLICO - CORREDOR OPERACIONAL	13.72	SERVICIO PÚBLICO
O-26	ALMACENAMIENTO DE BASURAS METRO	19.90	ÁREA OPERATIVA
P-05	BIBLIOMETRO	50.82	ÁREA PÚBLICA
P-06	ESPACIO IPES (INSTITUTO PARA LA ECONOMÍA SOCIAL)	15.45	ÁREA PÚBLICA
P-07	SALÓN MÚLTIPLE EMB	104.54	ÁREA PÚBLICA
PA-01	ÁREA PAGA	327.81	ÁREA PAGA
R-107	SERVICIOS ADICIONALES - ÁREA DE SERVICIO	330.40	SERVICIOS ADICIONALES - ÁREA NO PAGA
R-108	SERVICIOS ADICIONALES - ÁREA DE SERVICIO	49.09	SERVICIOS ADICIONALES - ÁREA NO PAGA
R-109	SERVICIOS ADICIONALES - ÁREA DE SERVICIO	72.97	SERVICIOS ADICIONALES - ÁREA NO PAGA
R-110	SERVICIOS ADICIONALES - ÁREA DE SERVICIO	21.14	SERVICIOS ADICIONALES - ÁREA NO PAGA
T-20-L-3	MEDIDORES (LUZ)	12.88	ÁREA TÉCNICA
T-20-W-3	MEDIDORES (AGUA)	7.23	ÁREA TÉCNICA
T-21-7	ÁREA DE INSPECCIÓN	7.78	ÁREA TÉCNICA
T-21-8	ÁREA DE INSPECCIÓN	6.49	ÁREA TÉCNICA
T-21-9	ÁREA DE INSPECCIÓN	6.85	ÁREA TÉCNICA
T-25-4	NODO DE ACCESO DE TELECOMUNICACIONES	8.78	ÁREA TÉCNICA
ZDR-03	ZONA DE REFUGIO (PMR)	2.43	ZONA DE REFUGIO
ZDR-04	ZONA DE REFUGIO (PMR)	3.38	ZONA DE REFUGIO
EDIFICIO DESCENDENTE		2410.46	
NAVE CENTRAL			
ARQ_PL_02_INTERMEDIO			
PA-01	ÁREA PAGA	324.54	ÁREA PAGA
NAVE CENTRAL		324.54	
TOTAL NIVEL INTERMEDIO		4931.35	

TABLA ÁREAS POR DEPARTAMENTO (NIVEL INTERMEDIO)	
DEPARTAMENTO	**ÁREA (m²)**
EDIFICIO ASCENDENTE	
ARQ_PL_02_INTERMEDIO	
SERVICIO PÚBLICO	87.63
SERVICIOS ADICIONALES - ÁREA NO PAGA	972.06
ZONA DE REFUGIO	8.50
ÁREA CULTURAL	4.00
ÁREA NO PAGA	731.00
ÁREA OPERATIVA	35.53
ÁREA PAGA	308.79
ÁREA TÉCNICA	48.85
EDIFICIO DESCENDENTE	
ARQ_PL_02_INTERMEDIO	
SERVICIO PÚBLICO	69.63
SERVICIOS ADICIONALES - ÁREA NO PAGA	473.61
ZONA DE REFUGIO	5.81
ÁREA CULTURAL	26.98
ÁREA NO PAGA	814.03
ÁREA OPERATIVA	471.77
ÁREA PAGA	327.81
ÁREA PÚBLICA	170.80
ÁREA TÉCNICA	50.01
NAVE CENTRAL	
ARQ_PL_02_INTERMEDIO	
ÁREA PAGA	324.54
TOTAL NIVEL INTERMEDIO	4931.35

VÁLIDO PARA CONSTRUCCIÓN
01-03-26

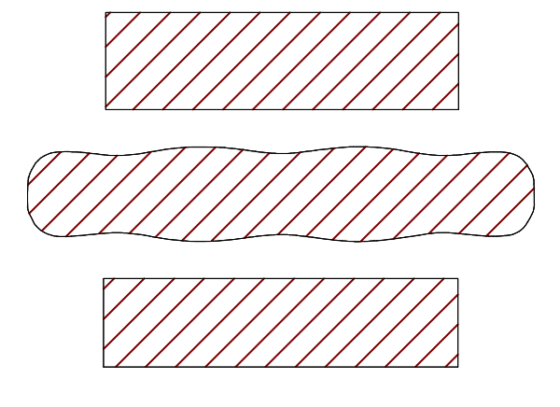

PLANO CLAVE ESTACIÓN 4

LOCALIZACIÓN

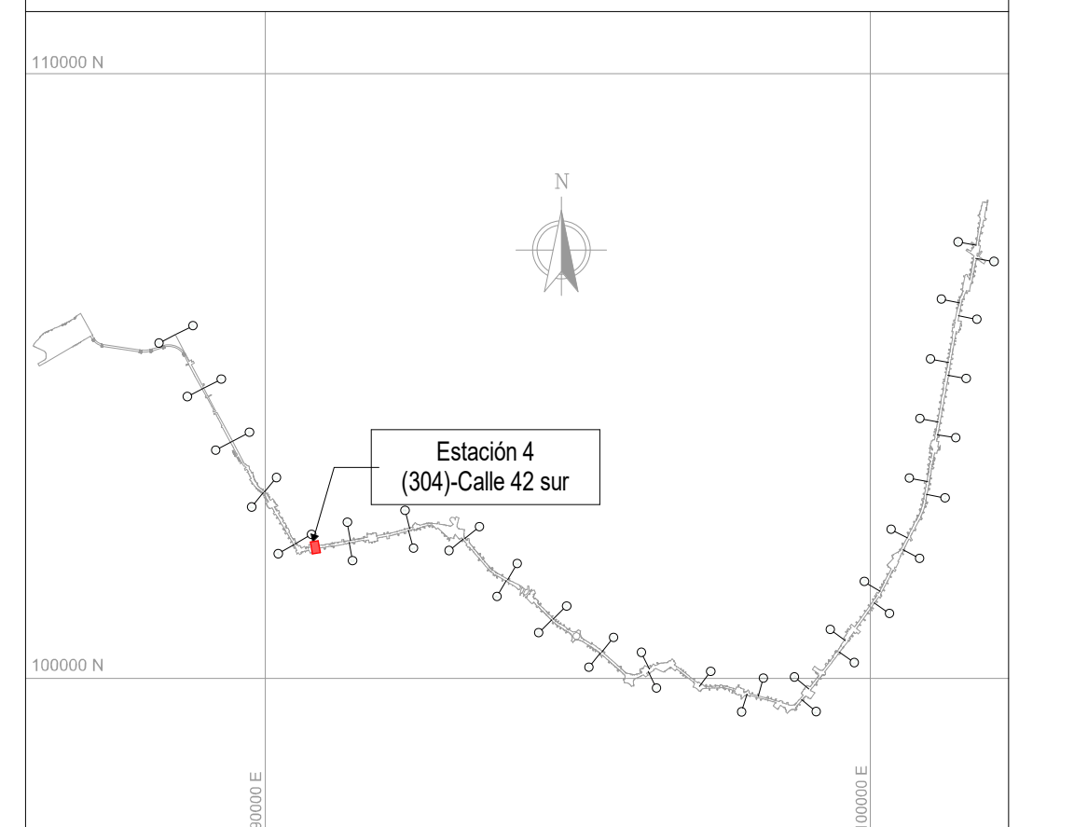

NOTAS

01 TODAS LAS DIMENSIONES ESTÁN CONFIGURADAS EN METROS A MENOS QUE SE INDIQUE UNA UNIDAD DE MEDIDA DIFERENTE.

02 TODAS LAS MEDIDAS, UBICACIÓN Y NIVELES DEBEN VERIFICARSE EN EL LUGAR DE CONSTRUCCIÓN.

03 EL NIVEL DE ACCESO AL EDIFICIO PL 01 CORRESPONDE AL +0,00 DE LA ESTACIÓN Y REFERENCIA AL NIVEL 2555.00 M.S.N.M

04 LOS NOMBRES ESPECÍFICOS DE LAS ÁREAS PUEDEN SER CONSULTADAS EN EL PLANO NO. 3 Ó EN LAS VISTAS EN PLANTA.

05 LOS COLORES QUE SE MUESTRAN EN LOS PLANOS COMO PROYECCIÓN DE ELEMENTOS ARQUITECTÓNICOS COMO CUBIERTAS, FACHADAS, MUROS, ETC. NO REPRESENTAN LA MATERIALIDAD Y REALIDAD DE ACABADOS DEL PROYECTO, SOLO SON INDICATIVOS PARA REALIZAR UNA CORRECTA LECTURA DE LA PLANIMETRÍA.

06 LAS ESCALERAS ELÉCTRICAS INDICAN SU SENTIDO CON LA SIGUIENTE NOMENCLATURA: "SUBE" Y "BAJA".

07 SE DEBEN REVISAR LOS NIVELES ESTRUCTURALES PARA NIVEL DE ACCESO PL_01 Y SUBNIVELES, PL_02 (INTERMEDIO), PL_03 (PLATAFORMA) CON LA PLANIMETRÍA DE PLACAS ESTRUCTURALES EN LOS ENTREGABLES L1T1-1300-404-CON-ED-EST-PL-0038, 39, 88, 89, 92, 93, RESPECTIVAMENTE. EL NIVEL ESTRUCTURAL (NE) REFERENCIA LOS ESPACIOS DONDE SE DEBE ACONDICIONAR EL ACABADO DE PISO SEGÚN CORRESPONDA, CON LOS NIVELES DE PISO TERMINADO (NPT). LOS NIVELES PROYECTADOS DE EMPATE (NPE) EN LAS ÁREAS DE SERVICIOS ADICIONALES, REFERENCIAN LA ADECUACIÓN DE LOS DESNIVELES EN ESTAS ÁREAS; QUEDA COMO RESPONSABILIDAD DEL LOCATARIO DEFINIR Y ACONDICIONAR ESTE ACABADO DE PISO (NPE) EN LÍNEA CON EL NIVEL (NPT) DE ESPACIOS COLINDANTES. EL NIVEL ESTRUCTURAL (NE) SE ENCUENTRA A (- 0.10M) POR DEBAJO DE LOS NIVELES DE PISO TERMINADO (NPT) Y LOS NIVELES PROYECTADOS DE EMPATE (NPE) MARCADOS EN LA PLANIMETRÍA.

- ARQ_PL_00 = SÓTANO / NPT -6.90m
- ARQ_PL_00.1 = ACCESO / NPT -0.50m
- ARQ_PL_00.2 = ACCESO / NPT -0.45m
- ARQ_PL_00.3 = ACCESO / NPT -0.38m
- ARQ_PL_00.4 = ACCESO / NPT -0.30m
- ARQ_PL_00.5 = ACCESO / NPT -0.25m
- ARQ_PL_00.6 = ACCESO / NPT -0.20m
- ARQ_PL_01 = ACCESO / NPT 0.00m
- ARQ_PL_01.1 = ACCESO / NPT 0.14m
- ARQ_PL_01.2 = ACCESO / NPT 0.25m
- ARQ_PL_02 = INTERMEDIO / NPT 6.60m
- ARQ_PL_02.2 = TOPE DE RIEL (TOR) / NPT 14.20m
- ARQ_PL_03 = PLATAFORMA / NPT 15.34m
- ARQ_PL_04 = CUBIERTA EDIFICACIONES / NPT 21.94m
- ARQ_PL_05 = CUBIERTA NAVE CENTRAL / NPT 24.59m

CONVENCIONES

▬ ▬ ▬	LÍMITE DE INTERVENCIÓN
▬ ▬ ▬	HUELLA APÉNDICE TÉCNICO
▬	MURO DIVISORIO
— — —	PROYECCIÓN NIVEL SUPERIOR
🟩	SERVICIOS ADICIONALES - ÁREA NO PAGA
🟩	SERVICIOS ADICIONALES - ÁREA PAGA
🟩	SERVICIO PÚBLICO
🟦	ZONA DE REFUGIO
🟥	ÁREA CULTURAL
🟨	ÁREA NO PAGA
🟦	ÁREA OPERATIVA
🟧	ÁREA PAGA
🟦	ÁREA PÚBLICA
⬜	ÁREA TÉCNICA

No.	PLANOS DE REFERENCIA	REV.
No.	**MODELO BIM DE REFERENCIA**	**REV.**
1	L1T1-1100-204-CON-ED-EST-MO-0001.rvt	V00
2	L1T1-1100-205-CON-ED-EST-MO-0001.rvt	V00
3	L1T1-1100-304-CON-ED-EST-MO-0001.rvt	V00
4	L1T1-1150-204-CON-ED-EST-MO-0001.rvt	V00
5	L1T1-1150-205-CON-ED-EST-MO-0001.rvt	V00
6	L1T1-1150-304-CON-ED-EST-MO-0001.rvt	V00
7	L1T1-1200-304-CON-ED-EST-MO-0001.rvt	V00
8	L1T1-1300-404-CON-ED-EST-MO-0001.rvt	V00
9	L1T1-1300-404-CON-ED-EST-MO-0002.rvt	V00
10	L1T1-1310-404-CON-ED-EST-MO-0001.rvt	V00
11	L1T1-1410-304-CON-ED-MEC-MO-0001.rvt	V00
12	L1T1-1420-404-CON-ED-MEC-MO-0001.rvt	V00
13	L1T1-5160-304-CON-ED-EST-MO-0001.rvt	V00
14	L1T1-5160-304-CON-ED-ARQ-MO-0001.rvt	V00
15	L1T1-5300-304-CON-ED-MEC-MO-0001.rvt	V00
16	L1T1-5600-304-CON-ED-INS-MO-0001.rvt	V00
17	L1T1-1330-404-CON-ED-ARQ-MO-0011.rvt	V00
18	L1T1-1330-404-CON-ED-ARQ-MO-0012.rvt	V00
No.	**PAQUETE DE TRABAJO DE REFERENCIA**	**REV.**
1	XREF-URBANISM_CONTEXT_ST04.rvt	
2	XREF-SECONDARY-STRUCTURE-ST04.rvt	

0 2 10m
1:200

METRO BOGOTÁ
GCS Consorcio Consultores PMO Bogotá
CONSORCIO SUPERVISOR PLMB
CHEC

DISEÑÓ:	REN ZHENHUA Licencia de Arq.nivel I (China): 1101735-614
APROBÓ:	DIEGO ERNESTO DUEÑAS Mat.: 25202-53876 CND
REVISÓ:	CARLOS MAURICIO BARRETO BARBOSA Mat.: A4012012-14139353
DIBUJÓ:	EQUIPO CHEC

REVISIÓN No.	FECHA	DESCRIPCIÓN	REVISÓ	APROBÓ	APROBACIÓN CLIENTE
V01	01/03/2026	EMITIDO PARA CONSTRUCCIÓN	C.M.B.B	D.E.D	
V00	20/12/2024	REVISIÓN NO OBJETADA - EMITIDO PARA CONSTRUCCIÓN	F.B.R	E.O.M	
VFF	28/06/2024	EMITIDO PARA REVISIÓN Y COMENTARIOS DEL CLIENTE E INTERVENTORÍA - INCLUYE COMENTARIOS /(AJUSTES V3)	F.B.R	E.O.M	
VEE	01/09/2023	EMITIDO PARA REVISIÓN Y COMENTARIOS DEL CLIENTE E INTERVENTORÍA - INCLUYE COMENTARIOS /(AJUSTES V2)	J.E.M	M.B.M	
VDD	18/12/2022	EMITIDO PARA REVISIÓN Y COMENTARIOS DEL CLIENTE E INTERVENTORÍA - INCLUYE COMENTARIOS /(AJUSTES)	J.E.M	M.B.M	
VCC	02/06/2022	EMITIDO PARA REVISIÓN Y COMENTARIOS DEL CLIENTE E INTERVENTORÍA - INCLUYE COMENTARIOS /(ENTREGA 90%)	J.E.M	M.B.M	
VBB	06/12/2021	EMITIDO PARA REVISIÓN Y COMENTARIOS DEL CLIENTE E INTERVENTORÍA	J.E.M	M.B.M	
VA0	30/06/2021	EMITIDO PARA COMENTARIOS INTERNOS - EMISIÓN PRELIMINAR PARA COMENTARIOS	J.E.M	M.B.M	

METRO LÍNEA 1

METRO LÍNEA 1
CONTRATO DE CONCESIÓN No. 163 DE 2019

PROYECTO PRIMERA LÍNEA DEL METRO DE BOGOTÁ - TRAMO 1

DIRECTOR DE INTERVENTORÍA: JAVIER DESCARGA N. Mat.:25202-68697 CND	ESPECIALISTA INTERVENTORÍA: CARLOS ALBERTO HOYOS SOTO Mat.:A25072000-14251682	FECHA: MARZO 2026

INFRAESTRUCTURA VIAL

ARQUITECTURA

ESTACIÓN METRO 4 (CALLE 42 SUR)
GENERAL
VISTA EN PLANTA Y 3D - NIVEL INTERMEDIO

PLANCHA No: L1T1-0000-304-CON-ED-ARQ-PL-0001_06_V01	ESCALA: INDICADA	REVISIÓN No. V01	PLANO No. 06 DE 97
ARCHIVO: L1T1-0000-304-CON-ED-ARQ-MO-0001_V00.rvt	FECHA: JUNIO 2021		