L1T1-CON-CAL-FR-0120 - B1 : 1000x707mm

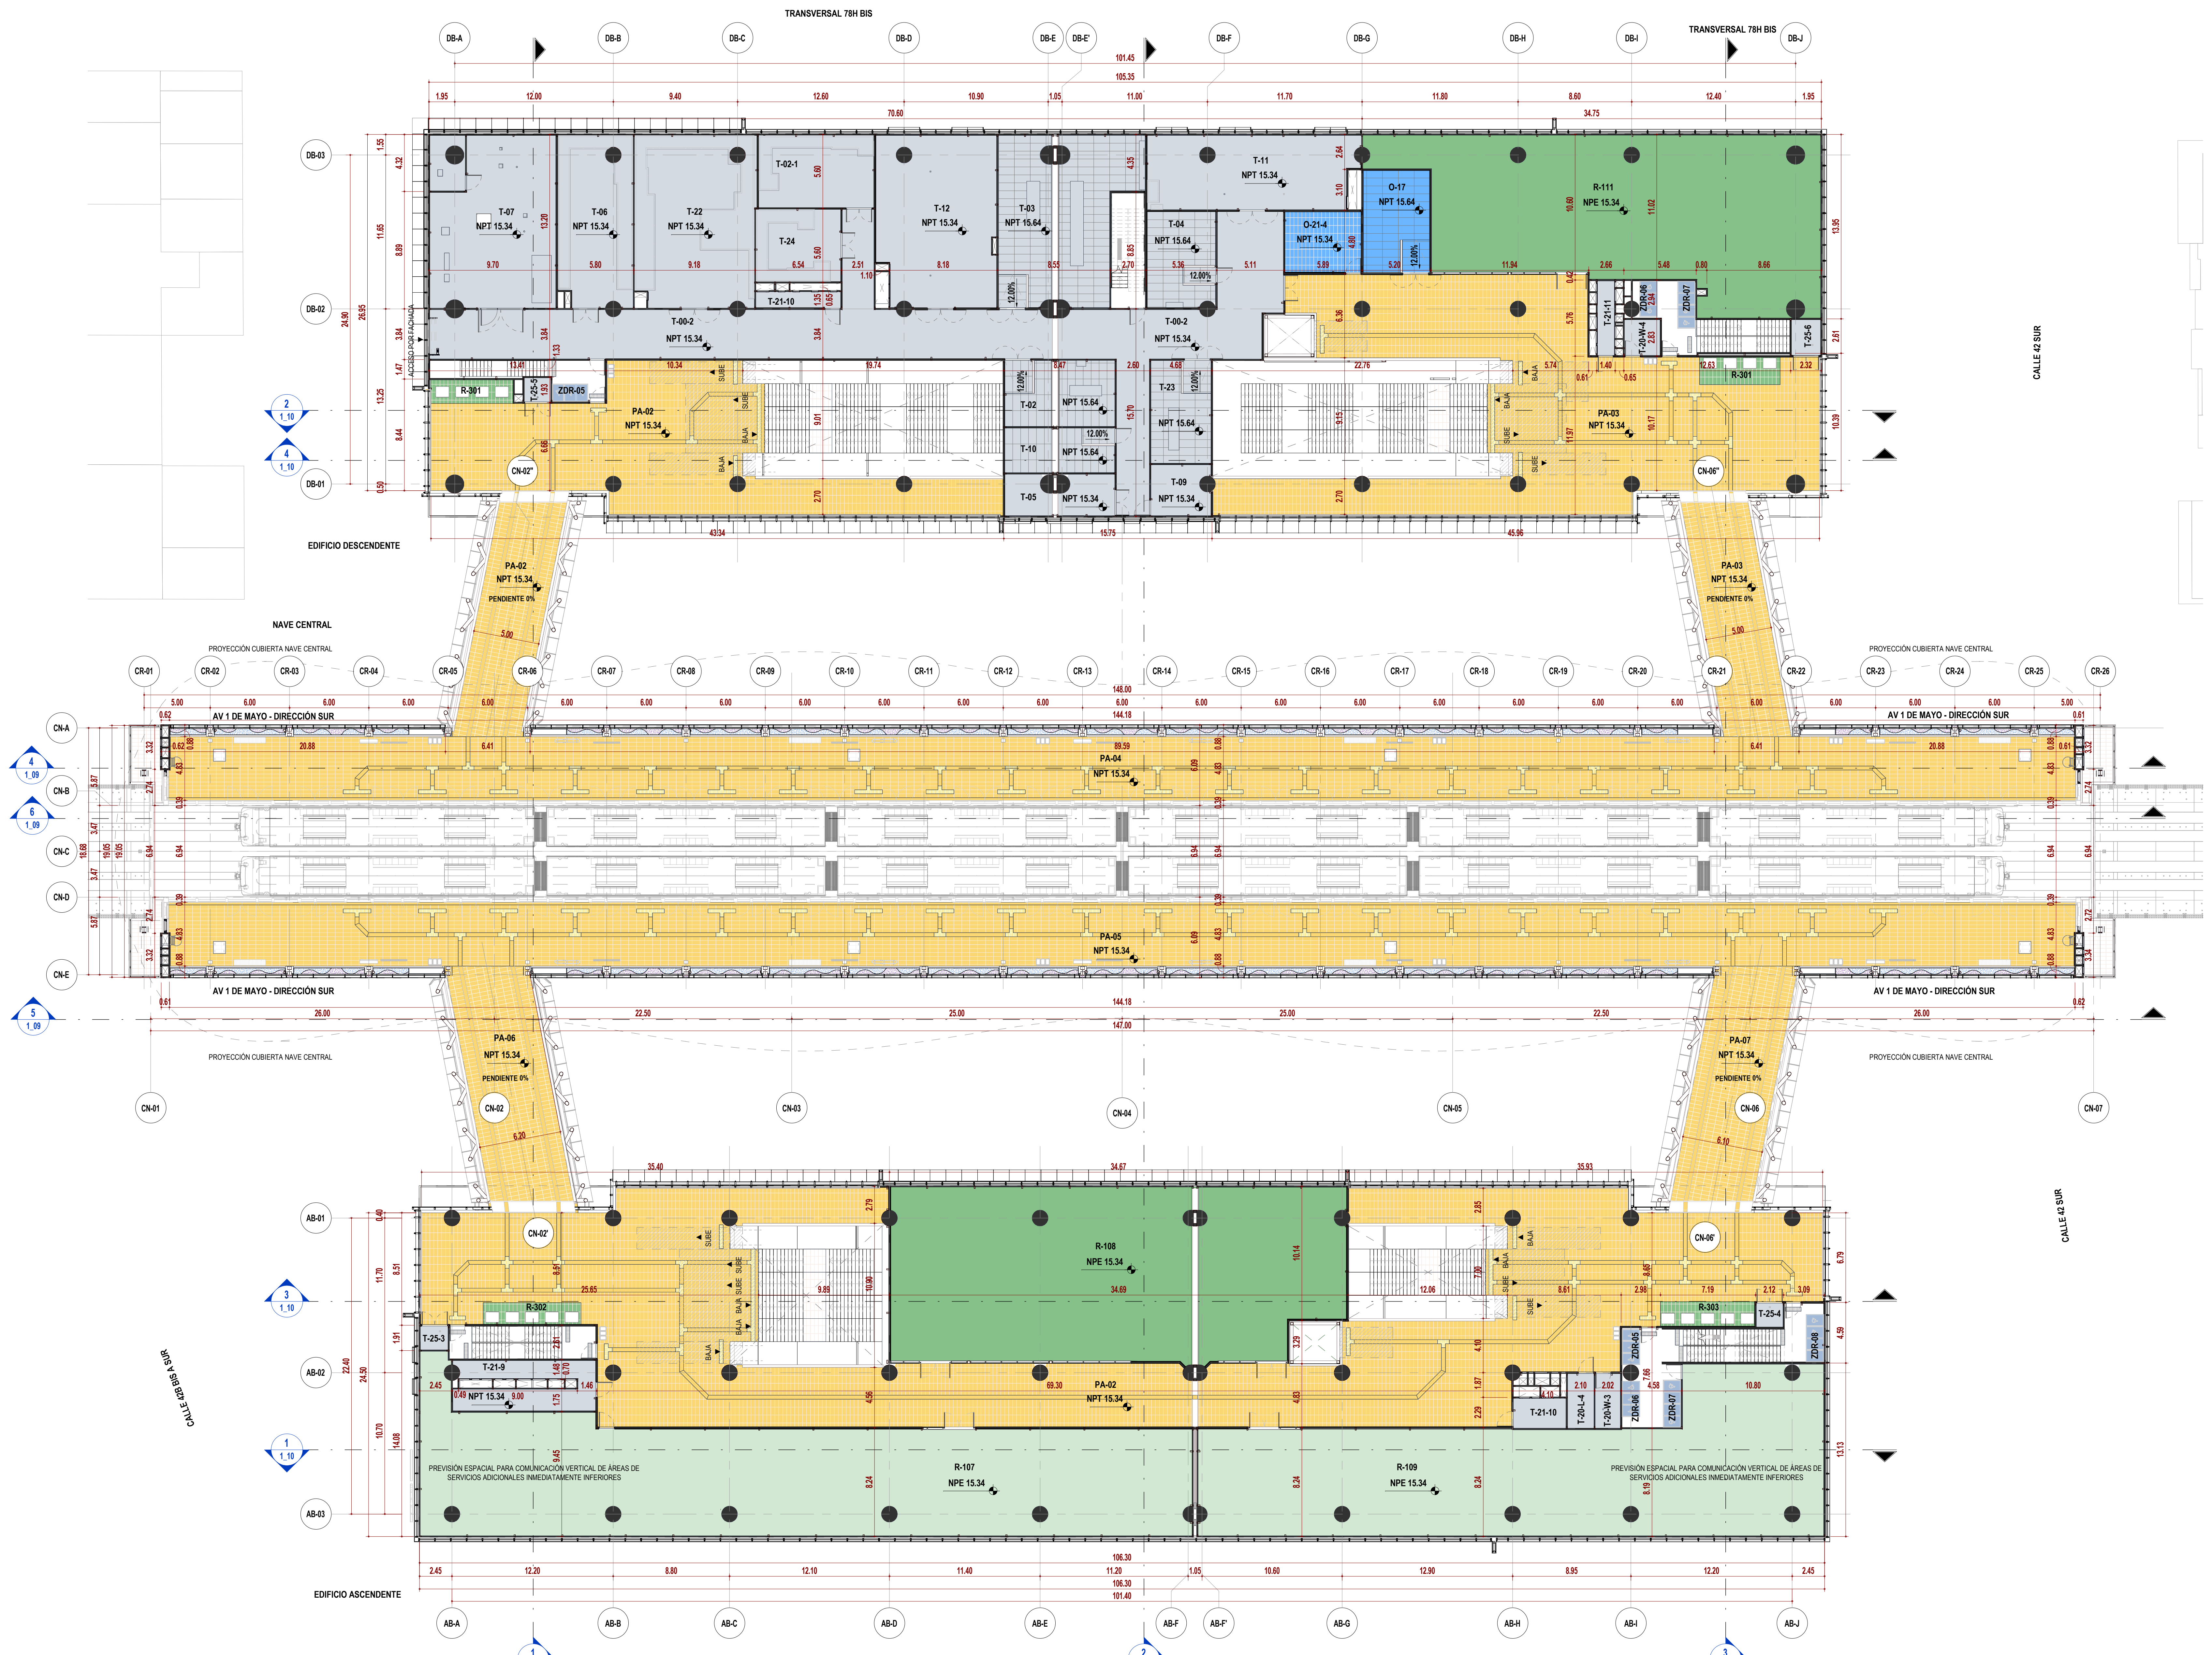
TRANSVERSAL 78H BIS
EDIFICIO DESCENDENTE
NAVE CENTRAL
PROYECCIÓN CUBIERTA NAVE CENTRAL
AV 1 DE MAYO - DIRECCIÓN SUR
PA-02
PA-03
PA-04
PA-05
PA-06
PA-07
NPT 15.34
PENDIENTE 8%
R-108
R-107
R-109
R-111
CALLE 42 SUR
EDIFICIO ASCENDENTE
PREVISIÓN ESPACIAL PARA COMUNICACIÓN VERTICAL DE ÁREAS DE SERVICIOS ADICIONALES INMEDIATAMENTE INFERIORES

2 NIVEL PLATAFORMA_GENERAL
ESC : 1 : 200

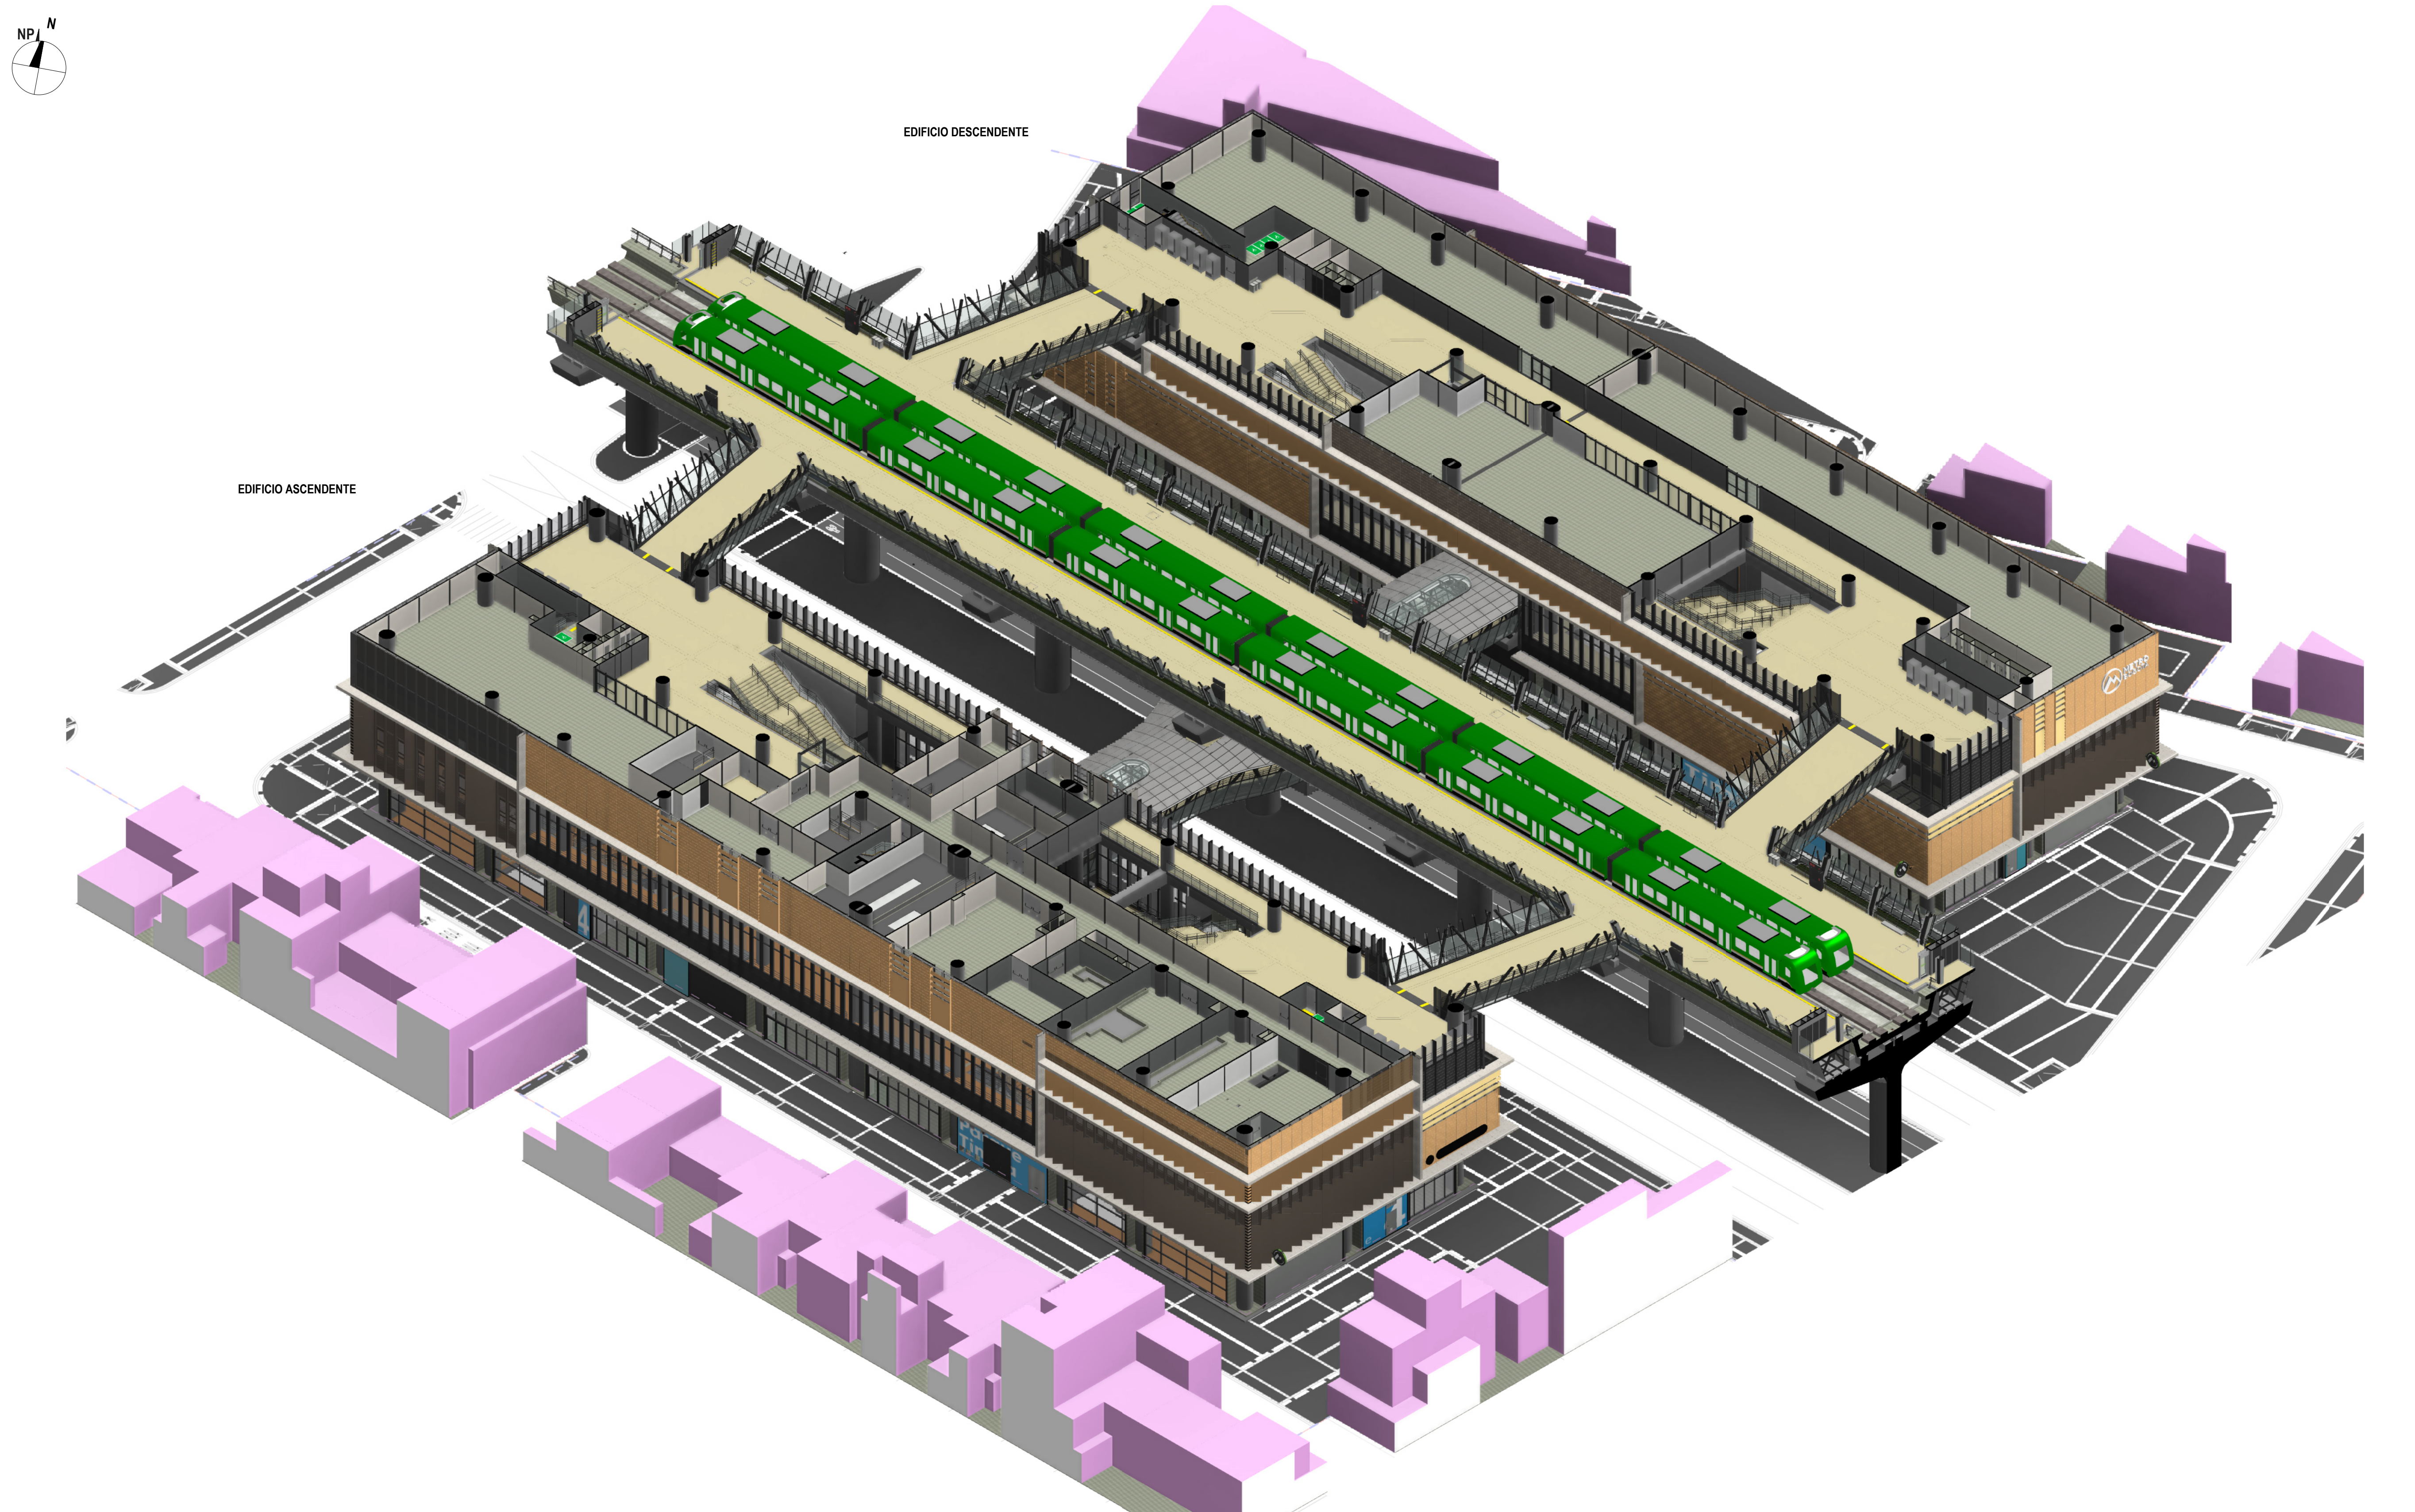

1 3D_NIVEL PLATAFORMA_GENERAL
ESC : N/A

CÓDIGO	NOMBRE	ÁREA (m²)	DEPARTAMENTO
EDIFICIO ASCENDENTE			
ARQ_PL_03_PLATAFORMA			
PA-02	ÁREA PAGA	913.28	ÁREA PAGA
R-107	SERVICIOS ADICIONALES - ÁREA DE SERVICIO	491.75	SERVICIOS ADICIONALES - ÁREA NO PAGA
R-108	SERVICIOS ADICIONALES - ÁREA DE SERVICIO	435.31	SERVICIOS ADICIONALES - ÁREA PAGA
R-109	SERVICIOS ADICIONALES - ÁREA DE SERVICIO	427.88	SERVICIOS ADICIONALES - ÁREA NO PAGA
R-302	SERVICIOS ADICIONALES - MÁQUINAS EXPENDEDORAS/CAJEROS AUTOMÁTICOS	12.12	SERVICIOS ADICIONALES - ÁREA PAGA
R-303	SERVICIOS ADICIONALES - MÁQUINAS EXPENDEDORAS/CAJEROS AUTOMÁTICOS	13.31	SERVICIOS ADICIONALES - ÁREA PAGA
T-20-L-4	MEDIDORES (LUZ)	8.24	ÁREA TÉCNICA
T-20-W-3	MEDIDORES (AGUA)	7.89	ÁREA TÉCNICA
T-21-9	ÁREA DE INSPECCIÓN	33.19	ÁREA TÉCNICA
T-21-10	ÁREA DE INSPECCIÓN	9.09	ÁREA TÉCNICA
T-25-3	NODO DE ACCESO DE TELECOMUNICACIONES	3.74	ÁREA TÉCNICA
T-25-4	NODO DE ACCESO DE TELECOMUNICACIONES	3.56	ÁREA TÉCNICA
ZDR-05	ZONA DE REFUGIO (PMR)	3.65	ZONA DE REFUGIO
ZDR-06	ZONA DE REFUGIO (PMR)	3.65	ZONA DE REFUGIO
ZDR-07	ZONA DE REFUGIO (PMR)	4.86	ZONA DE REFUGIO
ZDR-08	ZONA DE REFUGIO (PMR)	4.84	ZONA DE REFUGIO
EDIFICIO DESCENDENTE			
ARQ_PL_03_PLATAFORMA			
O-17	OPERADORES TELECOMUNICACIONES EXTERIORES	38.57	ÁREA OPERATIVA
O-21-4	ALMACENAMIENTO DE LA ESTACIÓN	26.65	ÁREA OPERATIVA
PA-02	ÁREA PAGA	282.20	ÁREA PAGA
PA-03	ÁREA PAGA	448.34	ÁREA PAGA
R-111	SERVICIOS ADICIONALES - ÁREA DE SERVICIO	348.63	SERVICIOS ADICIONALES - ÁREA PAGA
R-301	SERVICIOS ADICIONALES - MÁQUINAS EXPENDEDORAS/CAJEROS AUTOMÁTICOS	11.11	SERVICIOS ADICIONALES - ÁREA PAGA
R-301	SERVICIOS ADICIONALES - MÁQUINAS EXPENDEDORAS/CAJEROS AUTOMÁTICOS	12.76	SERVICIOS ADICIONALES - ÁREA PAGA
T-00-2	CIRCULACIÓN TÉCNICA	315.38	ÁREA TÉCNICA
T-02	LOCAL DE CONDUCCIÓN AUTOMÁTICA (CBTC)	41.80	ÁREA TÉCNICA
T-02-1	UPS DEDICADA (CBTC)	47.67	ÁREA TÉCNICA
T-03	TELECOMUNICACIONES ESTACIÓN - CORRIENTE DÉBIL	117.64	ÁREA TÉCNICA
T-04	EQUIPO BOLETERÍA	38.06	ÁREA TÉCNICA
T-05	ALMACÉN PARA MANTENIMIENTO	23.29	ÁREA TÉCNICA
T-06	SALA DE TABLEROS	71.06	ÁREA TÉCNICA
T-07	CENTRO DE TRANSFORMACIÓN (CT)	122.35	ÁREA TÉCNICA
T-09	ALMACÉN EQUIPO ELÉCTRICO	16.66	ÁREA TÉCNICA
T-10	CUARTO DE EQUIPO ELECTROMECÁNICO	28.22	ÁREA TÉCNICA
T-11	CUARTO DE VENTILACIÓN	85.95	ÁREA TÉCNICA
T-12	PLANTA DE REFRIGERACIÓN PARA LA CLIMATIZACIÓN	113.22	ÁREA TÉCNICA
T-20-W-4	MEDIDORES (AGUA)	7.26	ÁREA TÉCNICA
T-21-10	ÁREA DE INSPECCIÓN	7.72	ÁREA TÉCNICA
T-21-11	ÁREA DE INSPECCIÓN	7.27	ÁREA TÉCNICA
T-22	CUARTO DE UPS	116.41	ÁREA TÉCNICA
T-23	CUARTO PDAP	35.55	ÁREA TÉCNICA
T-24	TETRA UPS	35.06	ÁREA TÉCNICA
T-25-5	NODO DE ACCESO DE TELECOMUNICACIONES	3.60	ÁREA TÉCNICA
T-25-6	NODO DE ACCESO DE TELECOMUNICACIONES	5.97	ÁREA TÉCNICA
ZDR-05	ZONA DE REFUGIO (PMR)	3.65	ZONA DE REFUGIO
ZDR-06	ZONA DE REFUGIO (PMR)	3.65	ZONA DE REFUGIO
ZDR-07	ZONA DE REFUGIO (PMR)	4.86	ZONA DE REFUGIO
NAVE CENTRAL			
ARQ_PL_03_PLATAFORMA			
PA-02	ÁREA PAGA	97.77	ÁREA PAGA
PA-03	ÁREA PAGA	91.23	ÁREA PAGA
PA-04	ÁREA PAGA	696.88	ÁREA PAGA
PA-05	ÁREA PAGA	696.79	ÁREA PAGA
PA-06	ÁREA PAGA	123.98	ÁREA PAGA
PA-07	ÁREA PAGA	114.71	ÁREA PAGA
TOTAL NIVEL PLATAFORMA		6618.27	

TABLA DE ÁREAS ÚTILES (NIVEL PLATAFORMA)

TABLA ÁREAS ÚTILES POR DEPARTAMENTO (NIVEL PLATAFORMA)

DEPARTAMENTO	ÁREA (m²)
EDIFICIO ASCENDENTE	
ARQ_PL_03_PLATAFORMA	
SERVICIOS ADICIONALES - ÁREA NO PAGA	919.63
SERVICIOS ADICIONALES - ÁREA PAGA	460.74
ZONA DE REFUGIO	16.99
ÁREA PAGA	913.28
ÁREA TÉCNICA	65.71
EDIFICIO DESCENDENTE	
ARQ_PL_03_PLATAFORMA	
SERVICIOS ADICIONALES - ÁREA PAGA	372.50
ZONA DE REFUGIO	12.15
ÁREA OPERATIVA	65.22
ÁREA PAGA	730.53
ÁREA TÉCNICA	1240.15
NAVE CENTRAL	
ARQ_PL_03_PLATAFORMA	
ÁREA PAGA	1821.36
TOTAL NIVEL PLATAFORMA	6618.27

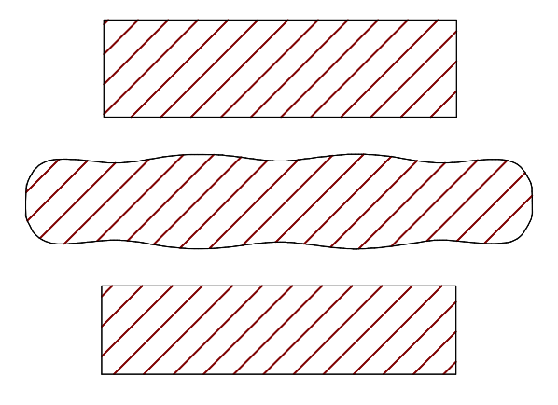

PLANO CLAVE ESTACIÓN 4

VÁLIDO PARA CONSTRUCCIÓN
01-03-26

LOCALIZACIÓN

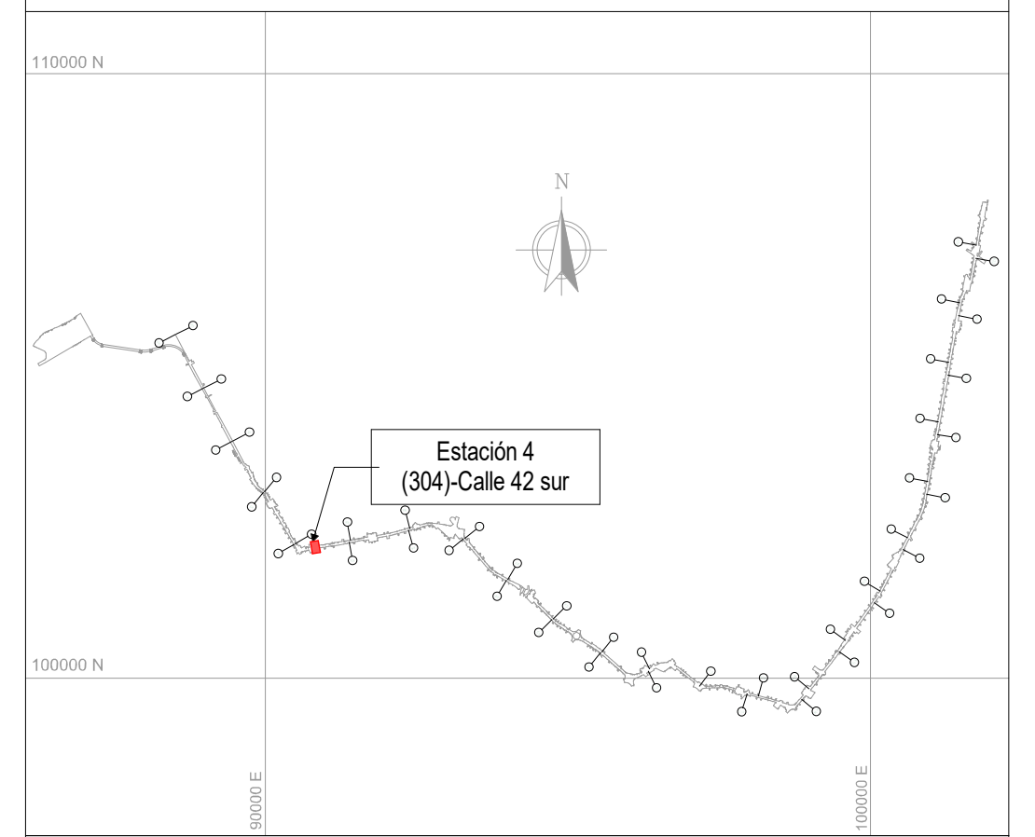

NOTAS

01 TODAS LAS DIMENSIONES ESTÁN CONFIGURADAS EN METROS A MENOS QUE SE INDIQUE UNA UNIDAD DE MEDIDA DIFERENTE.

02 TODAS LAS MEDIDAS, UBICACIÓN Y NIVELES DEBEN VERIFICARSE EN EL LUGAR DE CONSTRUCCIÓN.

03 EL NIVEL DE ACCESO AL EDIFICIO PL 01 CORRESPONDE AL +0,00 DE LA ESTACIÓN Y REFERENCIA AL NIVEL 2555.00 M.S.N.M

04 LOS NOMBRES ESPECÍFICOS DE LAS ÁREAS PUEDEN SER CONSULTADAS EN EL PLANO NO. 3 Ó EN LAS VISTAS EN PLANTA.

05 LOS COLORES QUE SE MUESTRAN EN LOS PLANOS COMO PROYECCIÓN DE ELEMENTOS ARQUITECTÓNICOS COMO CUBIERTAS, FACHADAS, MUROS, ETC. NO REPRESENTAN LA MATERIALIDAD Y REALIDAD DE ACABADOS DEL PROYECTO, SOLO SON INDICATIVOS PARA REALIZAR UNA CORRECTA LECTURA DE LA PLANIMETRÍA.

06 LAS ESCALERAS ELÉCTRICAS INDICAN SU SENTIDO CON LA SIGUIENTE NOMENCLATURA: "SUBE" Y "BAJA".

07 SE DEBEN REVISAR LOS NIVELES ESTRUCTURALES PARA NIVEL DE ACCESO PL_01 Y SUBNIVELES, PL_02 (INTERMEDIO), PL_03 (PLATAFORMA) CON LA PLANIMETRÍA DE PLACAS ESTRUCTURALES EN LOS ENTREGABLES L1T1-1300-404-CON-ED-EST-PL-0038, 39, 88, 89, 92, 93, RESPECTIVAMENTE. EL NIVEL ESTRUCTURAL (NE) REFERENCIA LOS ESPACIOS DONDE SE DEBE ACONDICIONAR EL ACABADO DE PISO SEGÚN CORRESPONDA, CON LOS NIVELES DE PISO TERMINADO (NPT). LOS NIVELES PROYECTADOS DE EMPATE (NPE) EN LAS ÁREAS DE SERVICIOS ADICIONALES, REFERENCIAN LA ADECUACIÓN DE LOS DESNIVELES EN ESTAS ÁREAS; QUEDA COMO RESPONSABILIDAD DEL LOCATARIO DEFINIR Y ACONDICIONAR ESTE ACABADO DE PISO (NPE) EN LÍNEA CON EL NIVEL (NPT) DE ESPACIOS COLINDANTES. EL NIVEL ESTRUCTURAL (NE) SE ENCUENTRA A (- 0.10M) POR DEBAJO DE LOS NIVELES DE PISO TERMINADO (NPT) Y LOS NIVELES PROYECTADOS DE EMPATE (NPE) MARCADOS EN LA PLANIMETRÍA.

- ARQ_PL_00 = SÓTANO / NPT -6.90m
- ARQ_PL_00.1 = ACCESO / NPT -0.50m
- ARQ_PL_00.2 = ACCESO / NPT -0.45m
- ARQ_PL_00.3 = ACCESO / NPT -0.38m
- ARQ_PL_00.4 = ACCESO / NPT -0.30m
- ARQ_PL_00.5 = ACCESO / NPT -0.25m
- ARQ_PL_00.6 = ACCESO / NPT -0.20m
- ARQ_PL_01 = ACCESO / NPT 0.00m
- ARQ_PL_01.1 = ACCESO / NPT 0.14m
- ARQ_PL_01.2 = ACCESO / NPT 0.25m
- ARQ_PL_02 = INTERMEDIO / NPT 6.60m
- ARQ_PL_02.2 = TOPE DE RIEL (TOR) / NPT 14.20m
- ARQ_PL_03 = PLATAFORMA / NPT 15.34m
- ARQ_PL_04 = CUBIERTA EDIFICACIONES / NPT 21.94m
- ARQ_PL_05 = CUBIERTA NAVE CENTRAL / NPT 24.59m

CONVENCIONES

▬ ▬ ▬	LÍMITE DE INTERVENCIÓN
▬ ▬ ▬	HUELLA APÉNDICE TÉCNICO
▬	MURO DIVISORIO
— — —	PROYECCIÓN NIVEL SUPERIOR
🟩	SERVICIOS ADICIONALES - ÁREA NO PAGA
🟩	SERVICIOS ADICIONALES - ÁREA PAGA
🟩	SERVICIO PÚBLICO
🟦	ZONA DE REFUGIO
🟥	ÁREA CULTURAL
🟨	ÁREA NO PAGA
🟦	ÁREA OPERATIVA
🟧	ÁREA PAGA
🟦	ÁREA PÚBLICA
⬜	ÁREA TÉCNICA

No.	PLANOS DE REFERENCIA	REV.

No.	MODELO BIM DE REFERENCIA	REV.
1	L1T1-1100-204-CON-ED-EST-MO-0001.rvt	V00
2	L1T1-1100-205-CON-ED-EST-MO-0001.rvt	V00
3	L1T1-1100-304-CON-ED-EST-MO-0001.rvt	V00
4	L1T1-1150-204-CON-ED-EST-MO-0001.rvt	V00
5	L1T1-1150-205-CON-ED-EST-MO-0001.rvt	V00
6	L1T1-1150-304-CON-ED-EST-MO-0001.rvt	V00
7	L1T1-1200-304-CON-ED-EST-MO-0001.rvt	V00
8	L1T1-1300-404-CON-ED-EST-MO-0001.rvt	V00
9	L1T1-1300-404-CON-ED-EST-MO-0002.rvt	V00
10	L1T1-1310-404-CON-ED-EST-MO-0001.rvt	V00
11	L1T1-1410-304-CON-ED-MEC-MO-0001.rvt	V00
12	L1T1-1420-404-CON-ED-MEC-MO-0001.rvt	V00
13	L1T1-5160-304-CON-ED-EST-MO-0001.rvt	V00
14	L1T1-5160-304-CON-ED-ARQ-MO-0001.rvt	V00
15	L1T1-5300-304-CON-ED-MEC-MO-0001.rvt	V00
16	L1T1-5600-304-CON-ED-INS-MO-0001.rvt	V00
17	L1T1-1330-404-CON-ED-ARQ-MO-0011.rvt	V00
18	L1T1-1330-404-CON-ED-ARQ-MO-0012.rvt	V00

No.	PAQUETE DE TRABAJO DE REFERENCIA	REV.
1	XREF-URBANISM_CONTEXT_ST04.rvt	
2	XREF-SECONDARY-STRUCTURE-ST04.rvt	

0 2 10m
1:200

METRO BOGOTÁ
GCS Consorcio Consultores PMO Bogotá
CONSORCIO SUPERVISOR PLMB
CHEC

DISEÑÓ:
REN ZHENHUA
Licencia de Arq.nivel I (China): 1101735-614

APROBÓ:
DIEGO ERNESTO DUEÑAS
Mat.: 25202-53876 CND

REVISÓ:
CARLOS MAURICIO BARRETO BARBOSA
Mat.: A4012012-14139353

DIBUJÓ:
EQUIPO CHEC

REVISIÓN No.	FECHA	DESCRIPCIÓN	REVISÓ	APROBÓ	APROBACIÓN CLIENTE
V01	01/03/2026	EMITIDO PARA CONSTRUCCIÓN	C.M.B.B	D.E.D	
V00	20/12/2024	REVISIÓN NO OBJETADA - EMITIDO PARA CONSTRUCCIÓN	F.B.R	E.O.M	
VFF	28/06/2024	EMITIDO PARA REVISIÓN Y COMENTARIOS DEL CLIENTE E INTERVENTORÍA - INCLUYE COMENTARIOS /(AJUSTES V3)	F.B.R	E.O.M	
VEE	01/09/2023	EMITIDO PARA REVISIÓN Y COMENTARIOS DEL CLIENTE E INTERVENTORÍA - INCLUYE COMENTARIOS /(AJUSTES V2)	J.E.M	M.B.M	
VDD	18/12/2022	EMITIDO PARA REVISIÓN Y COMENTARIOS DEL CLIENTE E INTERVENTORÍA - INCLUYE COMENTARIOS /(AJUSTES)	J.E.M	M.B.M	
VCC	02/06/2022	EMITIDO PARA REVISIÓN Y COMENTARIOS DEL CLIENTE E INTERVENTORÍA - INCLUYE COMENTARIOS /(ENTREGA 90%)	J.E.M	M.B.M	
VBB	06/12/2021	EMITIDO PARA REVISIÓN Y COMENTARIOS DEL CLIENTE E INTERVENTORÍA	J.E.M	M.B.M	
VA0	30/06/2021	EMITIDO PARA COMENTARIOS INTERNOS - EMISIÓN PRELIMINAR PARA COMENTARIOS	J.E.M	M.B.M	

METRO LÍNEA 1

METRO LÍNEA 1
CONTRATO DE CONCESIÓN No. 163 DE 2019

PROYECTO PRIMERA LÍNEA DEL METRO DE BOGOTÁ - TRAMO 1

DIRECTOR DE INTERVENTORÍA:
JAVIER DESCARGA N.
Mat.:25202-68697 CND

ESPECIALISTA INTERVENTORÍA:
CARLOS ALBERTO HOYOS SOTO
Mat.:A25072000-14251682

FECHA: MARZO 2026

INFRAESTRUCTURA VIAL
ARQUITECTURA
ESTACIÓN METRO 4 (CALLE 42 SUR)
GENERAL
VISTA EN PLANTA Y 3D - NIVEL PLATAFORMA

PLANCHA No: L1T1-0000-304-CON-ED-ARQ-PL-0001_07_V01
ARCHIVO: L1T1-0000-304-CON-ED-ARQ-MO-0001_V00.rvt
ESCALA: INDICADA
FECHA: JUNIO 2021
REVISIÓN No. V01
PLANO No. 07 DE 97