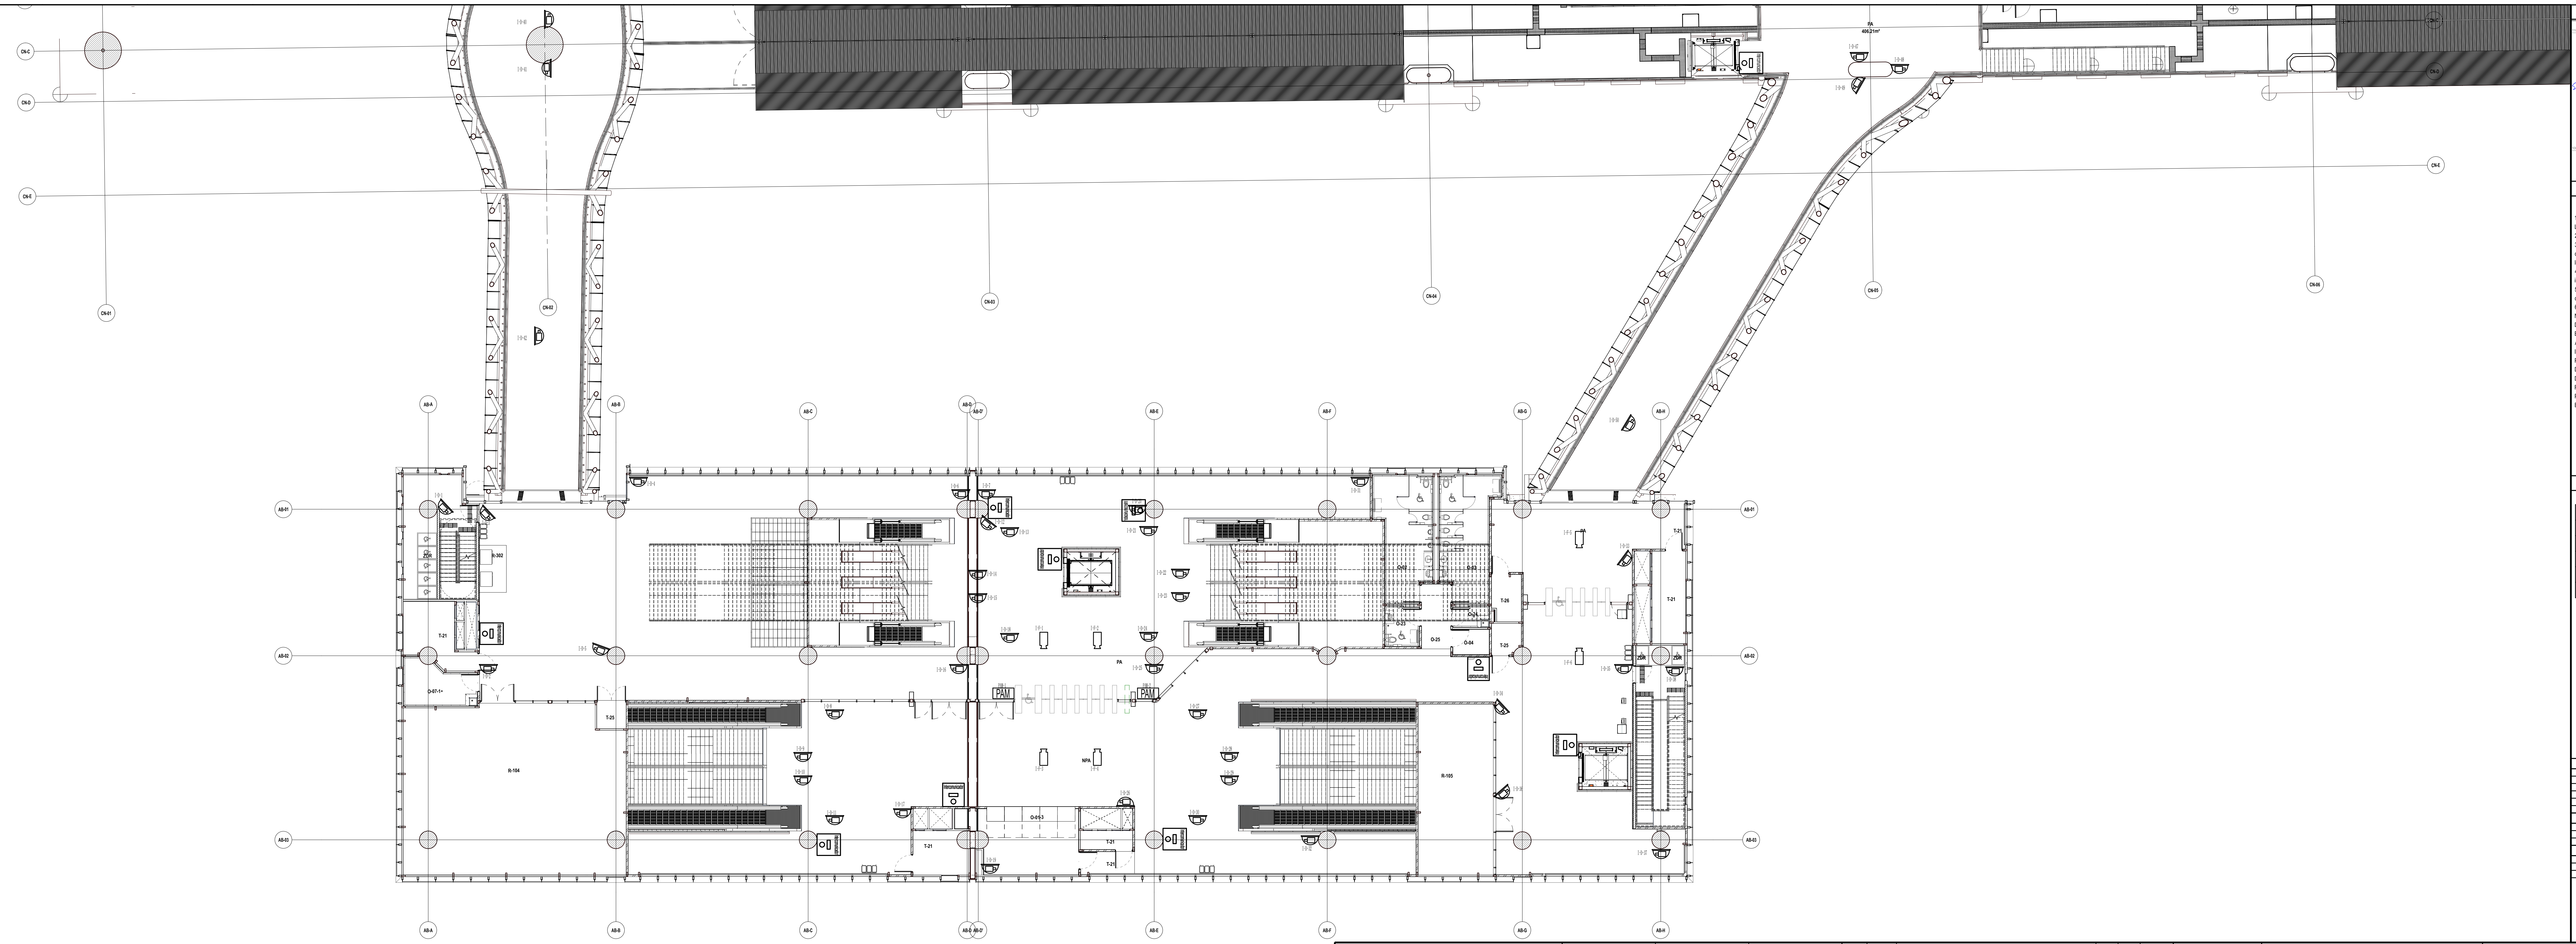

LOCALIZACIÓN GENERAL

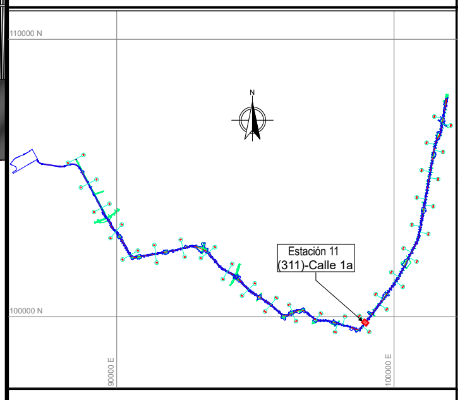

NOTAS

1.Este plano debe revisarse junto con el informe de diseño de L1T1-5445-000-CON-ED-INS-IN-0001 y L1T1-5420-311-CON-ED-INS-PL-0001.
2.Para el listado de equipo, consulte L1T1-5445-000-CON-ED-INS-CO-0001.
3.Para el listado del cable Ethernet (incluyendo el Ethernet para los puertos de contacto seco conectados a los intercomunicadores), se incluye en los planos de los enlaces de acceso de RMS.
4.Para el listado de cables conectados a la detección de intrusos, estos se incluyen en los planos del ACS.
5.Para la información de las bandejas portacables y tuberías consultar los planos de CNL.
6. Los criterios de denominación de las cámaras son los siguientes:
Nivel - tipo de cámara - código de la cámara.
Definición de nivel:
B: se refiere al sótano;
A: se refiere al nivel de acceso;
I: se refiere a la planta intermedia;
P: se refiere al nivel de plataforma;
Definición del tipo de cámara:
D: se refiere a la cámara de domo;
F: se refiere a la cámara fija;
P: se refiere a la cámara PTZ.
Ejemplo: B-F-1 es una cámara fija con código 1 en el nivel del sótano.

CONVENCIONES

◒	Cámara de domo
▭	Cámara fija (tipo inteligente)
⊖	Cámara PTZ
PAM	Monitor de vigilancia de pasajeros
DEC	Decodificador de vídeo
Intercomunicador	Intercomunicador

N.º	PLANOS DE REFERENCIA	REV.
1	L1T1-5420-311-CON-ED-INS-PL-0001	V00

N.º	MODELO BIM DE REFERENCIA	REV.
1	L1T1-0000-311-CON-ED-ARQ-MO-0001.RVT	V00

N.º	PAQUETE DE TRABAJO DE REFERENCIA	REV.

METRO BOGOTÁ
GCS Consorcio Consultores PMO Bogotá
CONSORCIO SUPERVISOR PLMB
wsp Líder de Diseño Interfaz y Gerencia de Integración

DISEÑÓ: WANG KEJIA	APROBÓ: ZHANG YUJIE	ARANI MUKHERJEE
REVISÓ: YANG BAODONG	MODELÓ/DIBUJÓ: WANG KEJIA	JAIME ZAMLUNG Mat.: I:E-3182 DE 2022

REVISIÓN N.º	FECHA	DESCRIPCIÓN	REVISÓ	APROBÓ	APROBACIÓN CLIENTE
V00	28/06/2024	Revisión no objetada - Emitido para implementación	Y.B.	Z.Y.	
VDD	05/06/2023	Emitido para revisión y comentarios del cliente e Interventoría - Incluye comentarios / modificado donde se indica en el control de cambios	Y.B.	Z.Y.	
VA1	30/05/2023	Emitido para comentarios internos - Emisión preliminar para comentarios	Y.B.	Z.Y.	
VCC	11/10/2022	Emitido para revisión y comentarios del cliente e Interventoría - Incluye comentarios / modificado donde se indica en el control de cambios	F.K.		
VBB	14/12/2021	Emitido para revisión y comentarios del cliente e Interventoría	J.Z.	F.M.	
VA0	13/12/2021	Emitido para comentarios internos - Emisión preliminar para comentarios	A.M.	P.B.	

METRO LÍNEA 1

METRO LÍNEA 1
CONTRATO DE CONCESIÓN N.º 163 DE 2019

PROYECTO PRIMERA LÍNEA DEL METRO DE BOGOTÁ - TRAMO 1

DIRECTOR INTERVENTORÍA: JAVIER DESCARGA N. Mat.: 25202-68697 CND	ESPECIALISTA INTERVENTORÍA: A.PAREDES Z. Mat.: VL206 36884	FECHA: JUNIO 2024

SISTEMAS Y EQUIPOS
TELECOMUNICACIONES
ESTACIÓN CALLE 1A - DISEÑO DETALLADO DEL NIVEL INTERMEDIO (PARTE-2)
SISTEMA CCTV
DISPOSICIÓN GENERAL

PLANCHA N.º L1T1-5445-311-CON-ED-INS-PL-0009_09_V00	ESCALA: 1:100	REVISIÓN N.º V00	HOJA N.º 9 DE 16
ARCHIVO: L1T1-5445-311-CON-ED-INS-PL-0009.DWG	FECHA: DICIEMBRE 2021		