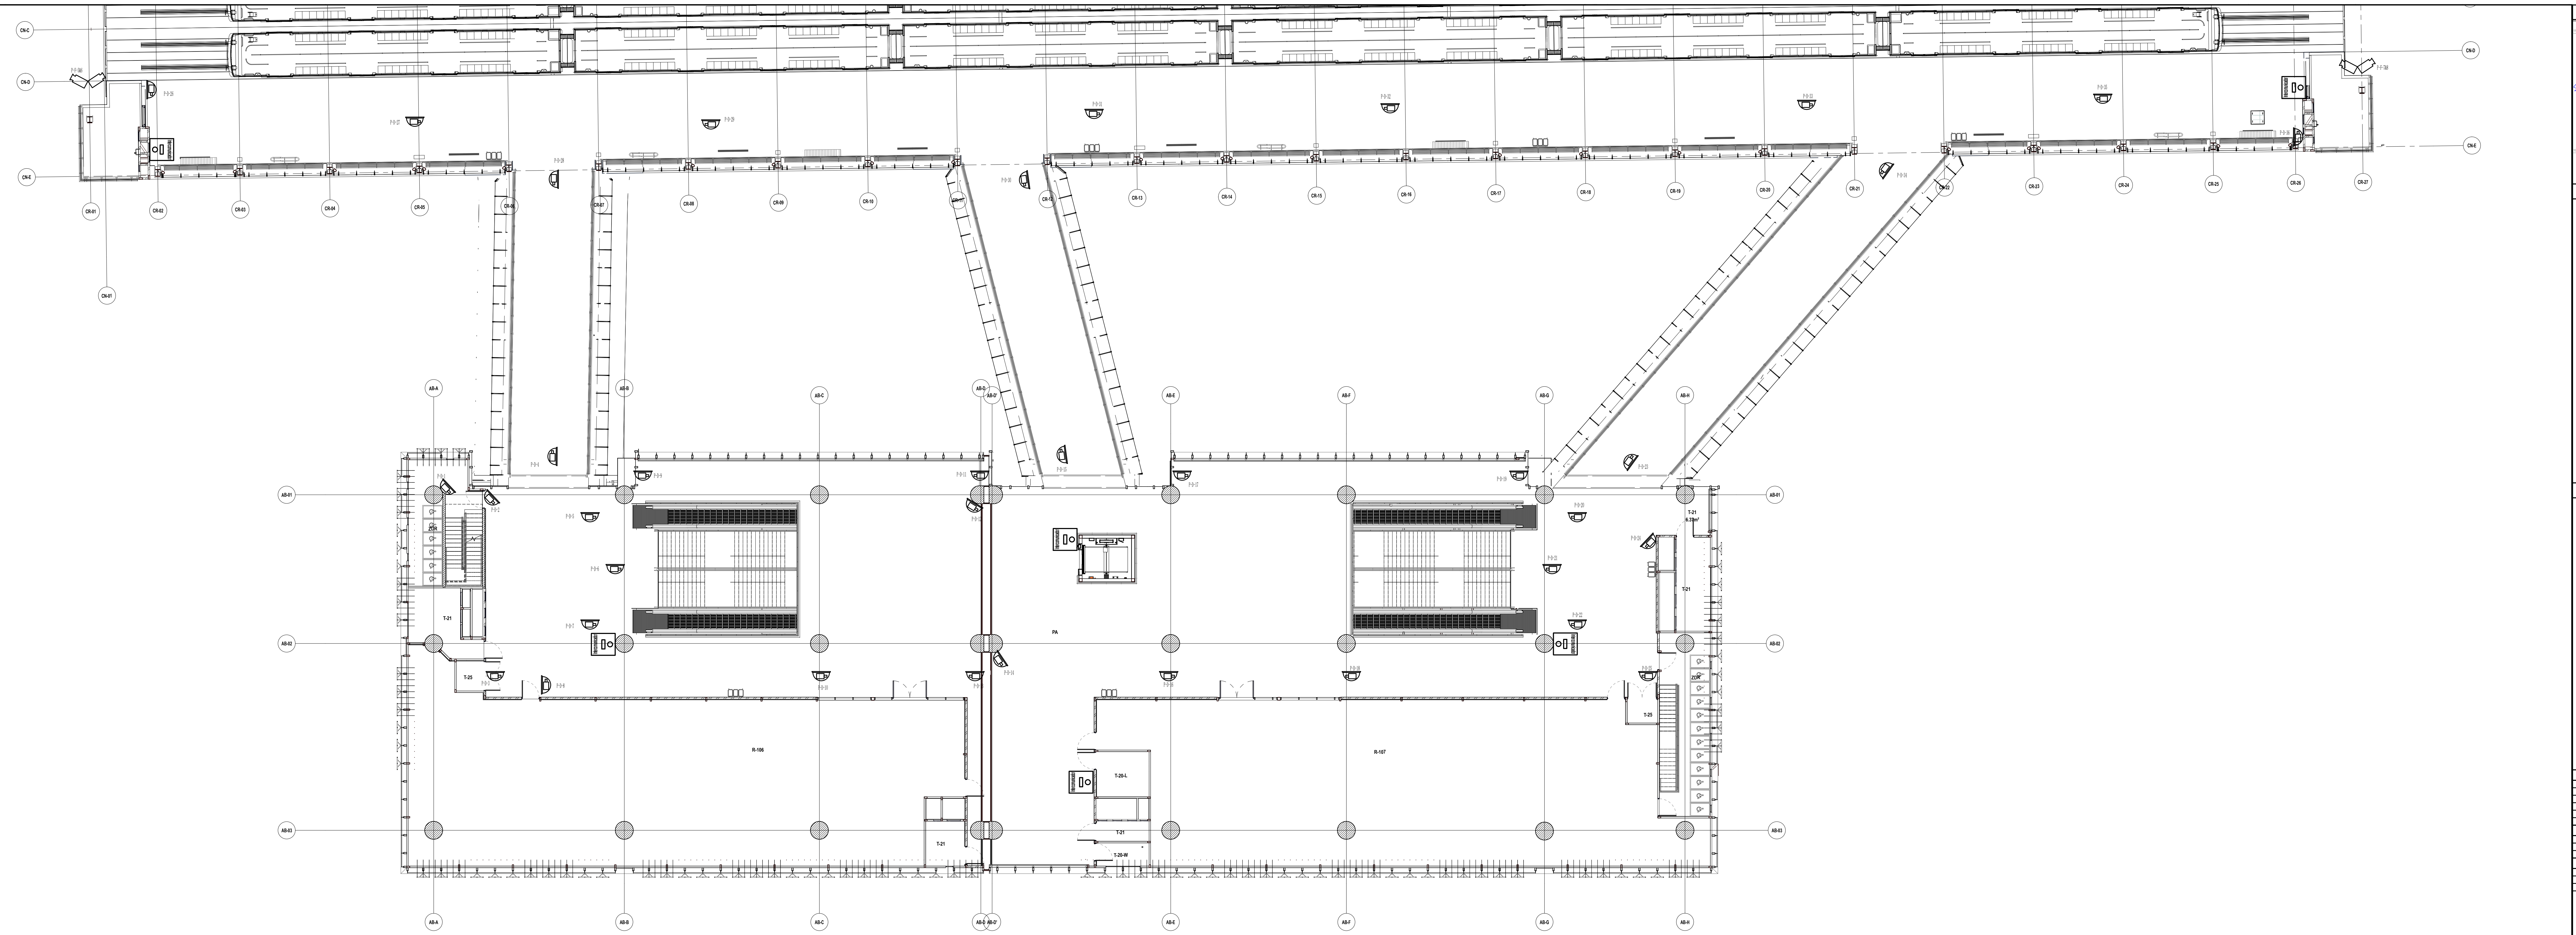
CN-C
CN-D
CN-E
CN-01
P-F-5&6
P-F-7&8
P-D-26
P-D-27
P-D-28
P-D-29
P-D-30
P-D-31
P-D-32
P-D-33
P-D-34
P-D-35
P-D-36
CR-01
CR-02
CR-03
CR-04
CR-05
CR-06
CR-07
CR-08
CR-09
CR-10
CR-11
CR-12
CR-13
CR-14
CR-15
CR-16
CR-17
CR-18
CR-19
CR-20
CR-21
CR-22
CR-23
CR-24
CR-25
CR-26
CR-27
Intercomunicador
AB-A
AB-B
AB-C
AB-D
AB-D'
AB-E
AB-F
AB-G
AB-H
AB-01
AB-02
AB-03
P-D-1
P-D-2
P-D-3
P-D-4
P-D-5
P-D-6
P-D-7
P-D-8
P-D-9
P-D-10
P-D-11
P-D-12
P-D-13
P-D-14
P-D-15
P-D-16
P-D-17
P-D-18
P-D-19
P-D-20
P-D-21
P-D-22
P-D-23
P-D-24
P-D-25
ZDR
T-21
T-25
R-106
PA
T-20-L
T-20-W
R-107
T-21 6.37m²

LOCALIZACIÓN GENERAL


Estación 11
(311)-Calle 1a
100000 N
90000 E
100000 E

NOTAS

1.Este plano debe revisarse junto con el informe de diseño de L1T1-5445-000-CON-ED-INS-IN-0001 y L1T1-5420-311-CON-ED-INS-PL-0001.
2.Para el listado de equipo, consulte L1T1-5445-000-CON-ED-INS-CO-0001.
3.Para el listado del cable Ethernet (incluyendo el Ethernet para los puertos de contacto seco conectados a los intercomunicadores), se incluye en los planos de los enlaces de acceso de RMS.
4.Para el listado de cables conectados a la detección de intrusos, estos se incluyen en los planos del ACS.
5.Para la información de las bandejas portacables y tuberías consultar los planos de CNL.
6. Los criterios de denominación de las cámaras son los siguientes:
Nivel - tipo de cámara - código de la cámara.
Definición de nivel:
B: se refiere al sótano;
A: se refiere al nivel de acceso;
I: se refiere a la planta intermedia;
P: se refiere al nivel de plataforma;
Definición del tipo de cámara:
D: se refiere a la cámara de domo;
F: se refiere a la cámara fija;
P: se refiere a la cámara PTZ.
Ejemplo: B-F-1 es una cámara fija con código 1 en el nivel del sótano.

CONVENCIONES

	Cámara de domo
	Cámara fija (tipo inteligente)
	Cámara PTZ
PAM	Monitor de vigilancia de pasajeros
DEC	Decodificador de vídeo
Intercomunicador	Intercomunicador

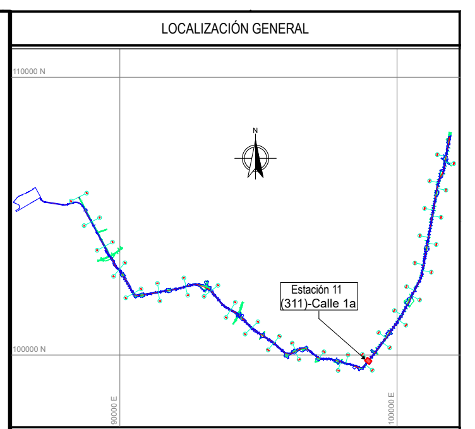N.º	PLANOS DE REFERENCIA	REV.
1	L1T1-5420-311-CON-ED-INS-PL-0001	V00

N.º	MODELO BIM DE REFERENCIA	REV.
1	L1T1-0000-311-CON-ED-ARQ-MO-0001.RVT	V00

N.º	PAQUETE DE TRABAJO DE REFERENCIA	REV.

METRO BOGOTÁ
Consorcio Consultores PMO Bogotá
CONSORCIO SUPERVISOR PLMB
Líder de Diseño Interfaz y Gerencia de Integración

DISEÑÓ: WANG KEJIA
APROBÓ: ZHANG YUJIE
ARANI MUKHERJEE
REVISÓ: YANG BAODONG
MODELÓ/DIBUJÓ: WANG KEJIA
JAIME ZAMLUNG
Mat.: I:E-3182 DE 2022

REVISIÓN N.º	FECHA	DESCRIPCIÓN	REVISÓ	APROBÓ	APROBACIÓN CLIENTE
V00	28/06/2024	Revisión no objetada - Emitido para implementación	Y.B.	Z.Y.	
VDD	05/06/2023	Emitido para revisión y comentarios del cliente e Interventoría - Incluye comentarios / modificado donde se indica en el control de cambios	Y.B.	Z.Y.	
VA1	30/05/2023	Emitido para comentarios internos - Emisión preliminar para comentarios	Y.B.	Z.Y.	
VCC	11/10/2022	Emitido para revisión y comentarios del cliente e Interventoría - Incluye comentarios / modificado donde se indica en el control de cambios	F.K.		
VBB	14/12/2021	Emitido para revisión y comentarios del cliente e Interventoría	J.Z.	F.M.	
VA0	13/12/2021	Emitido para comentarios internos - Emisión preliminar para comentarios	A.M.	P.B.	

METRO LÍNEA 1

METRO LÍNEA 1
CONTRATO DE CONCESIÓN N.º 163 DE 2019

PROYECTO PRIMERA LÍNEA DEL METRO DE BOGOTÁ - TRAMO 1

DIRECTOR INTERVENTORÍA:
JAVIER DESCARGA N.
Mat.: 25202-68697 CND

ESPECIALISTA INTERVENTORÍA:
A.PAREDES Z.
Mat.: VL206 36884

FECHA: JUNIO 2024

SISTEMAS Y EQUIPOS

TELECOMUNICACIONES

ESTACIÓN CALLE 1A - DISEÑO DETALLADO DEL NIVEL DE PLATAFORMA (PARTE-2)
SISTEMA CCTV
DISPOSICIÓN GENERAL

PLANCHA N.º L1T1-5445-311-CON-ED-INS-PL-0009_13_V00
ARCHIVO: L1T1-5445-311-CON-ED-INS-PL-0009.DWG
ESCALA: 1:100
FECHA: DICIEMBRE 2021
REVISIÓN N.º V00
HOJA N.º 13 DE 16