L1T1-CON-CAL-FR-0122 - A3-EXT1 : 1681x707mm

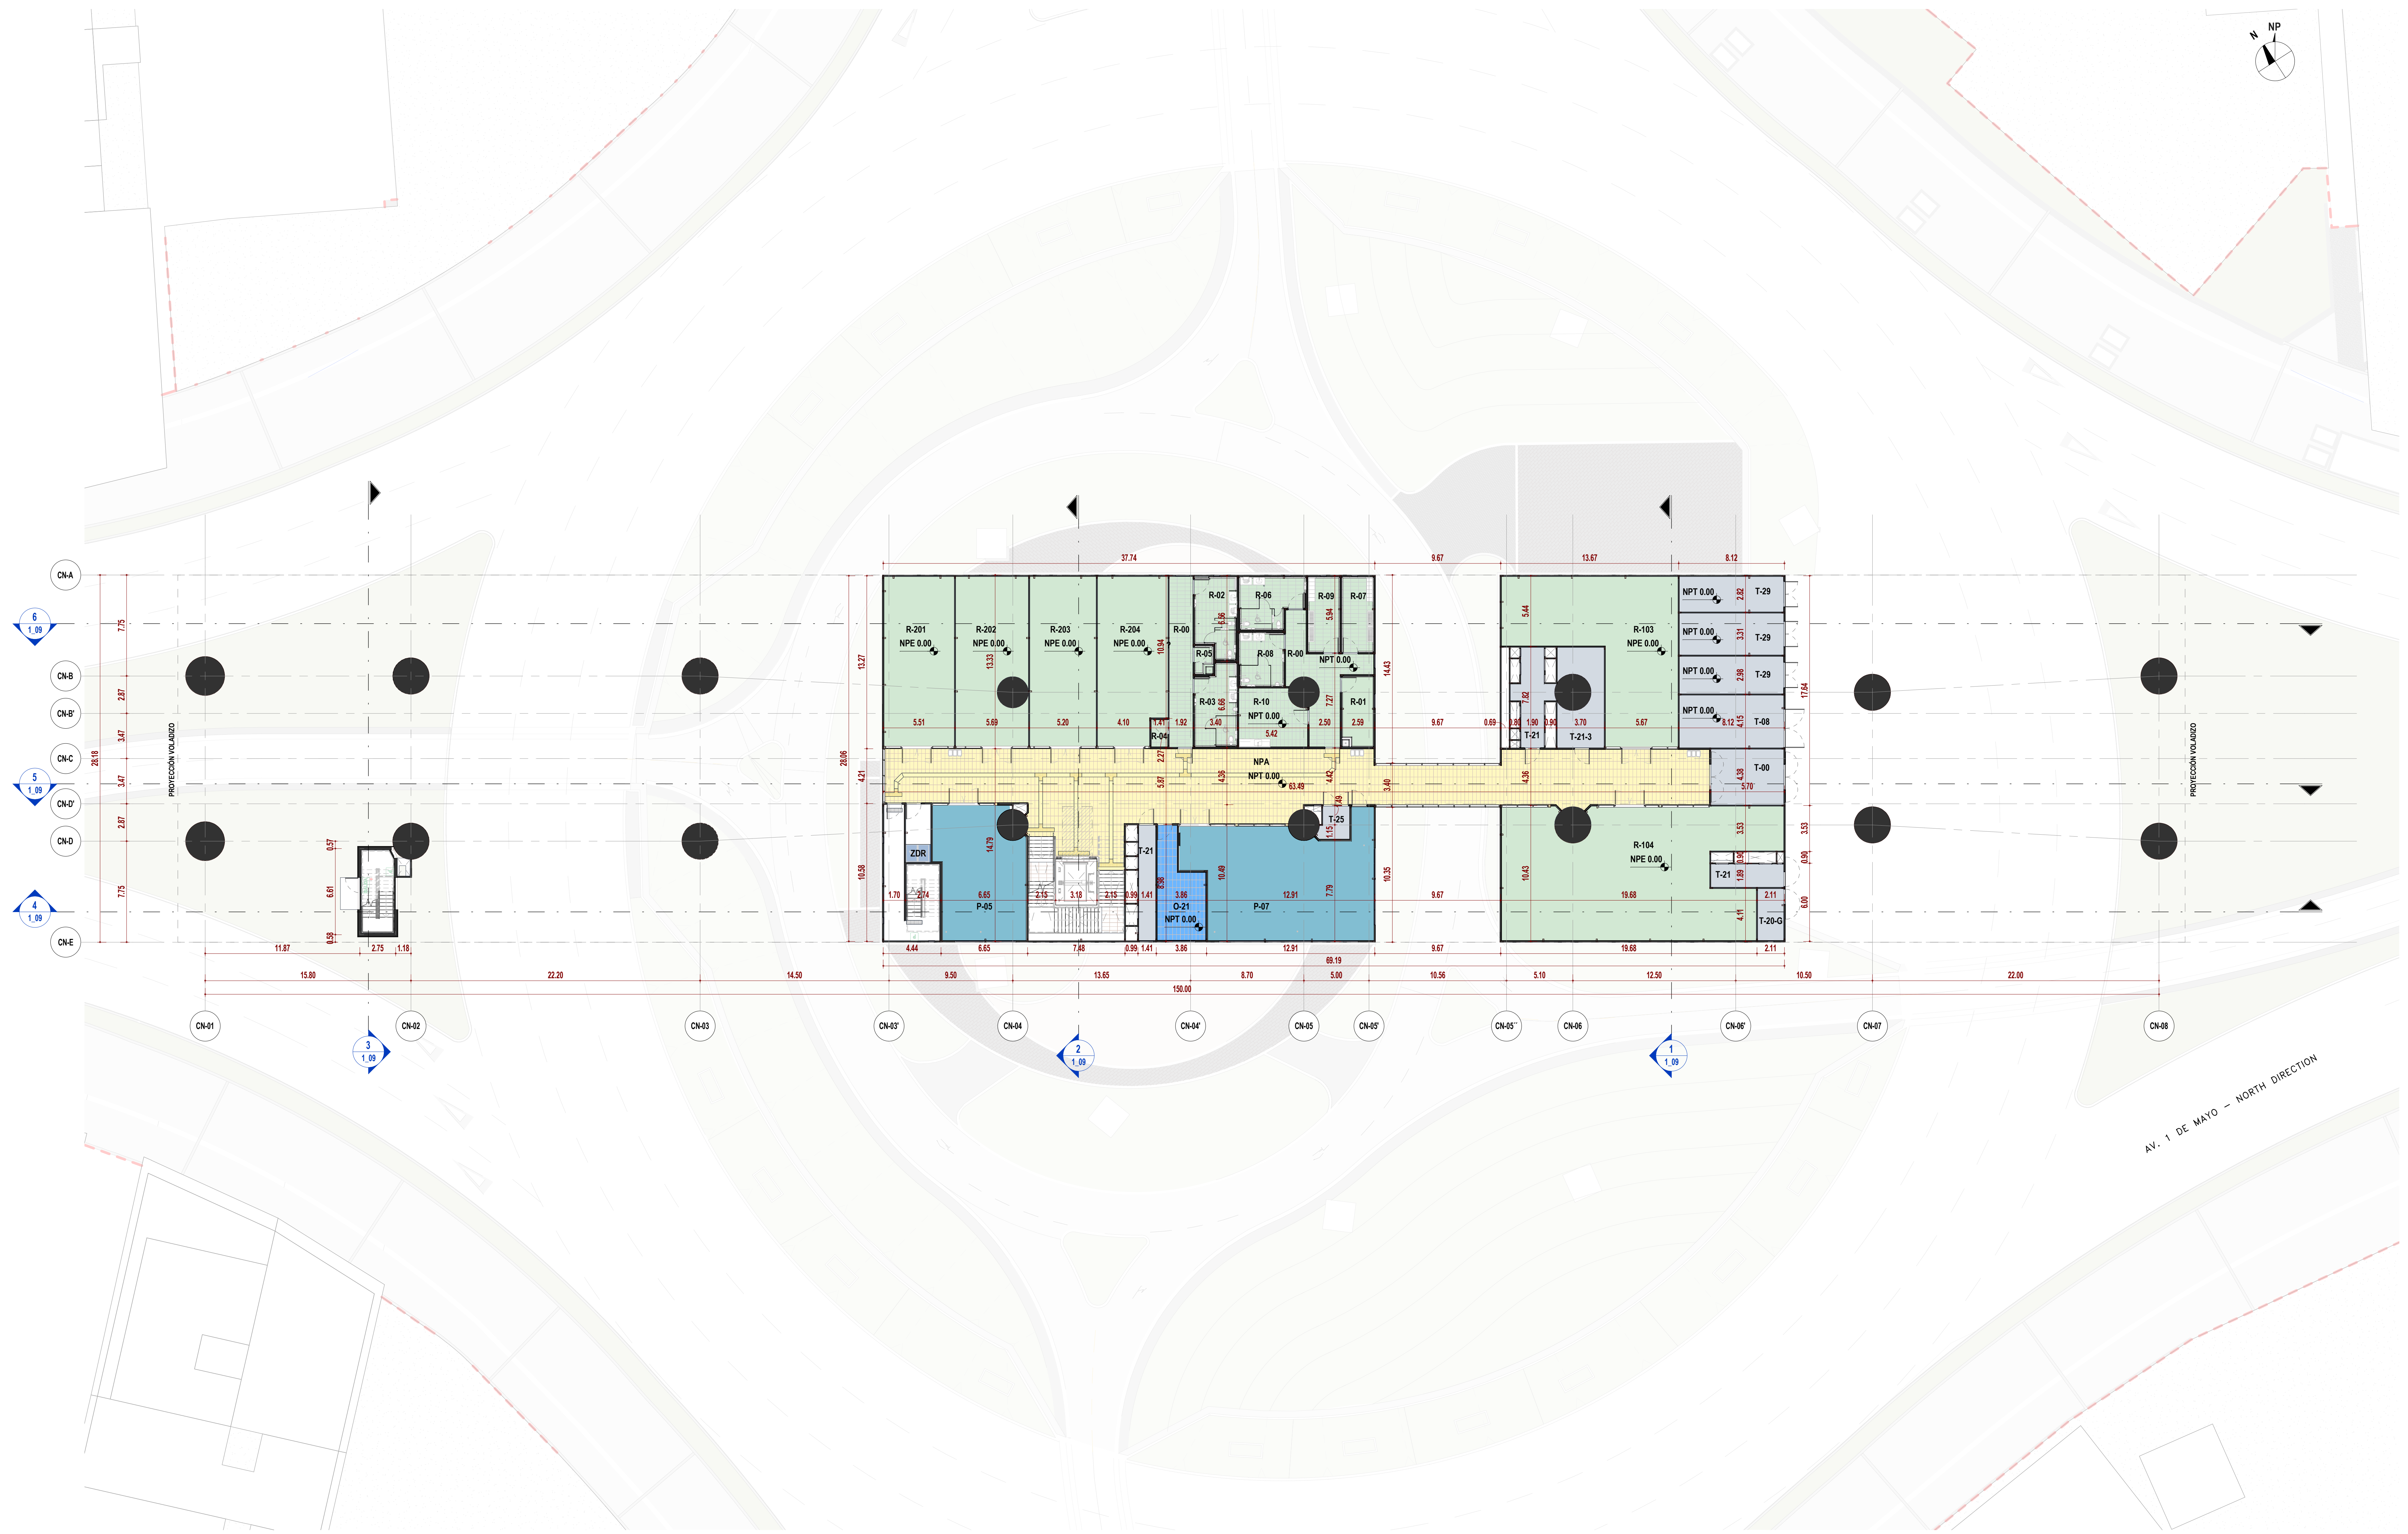

2 NIVEL ACCESO_NAVE CENTRAL
ESC: 1 : 200

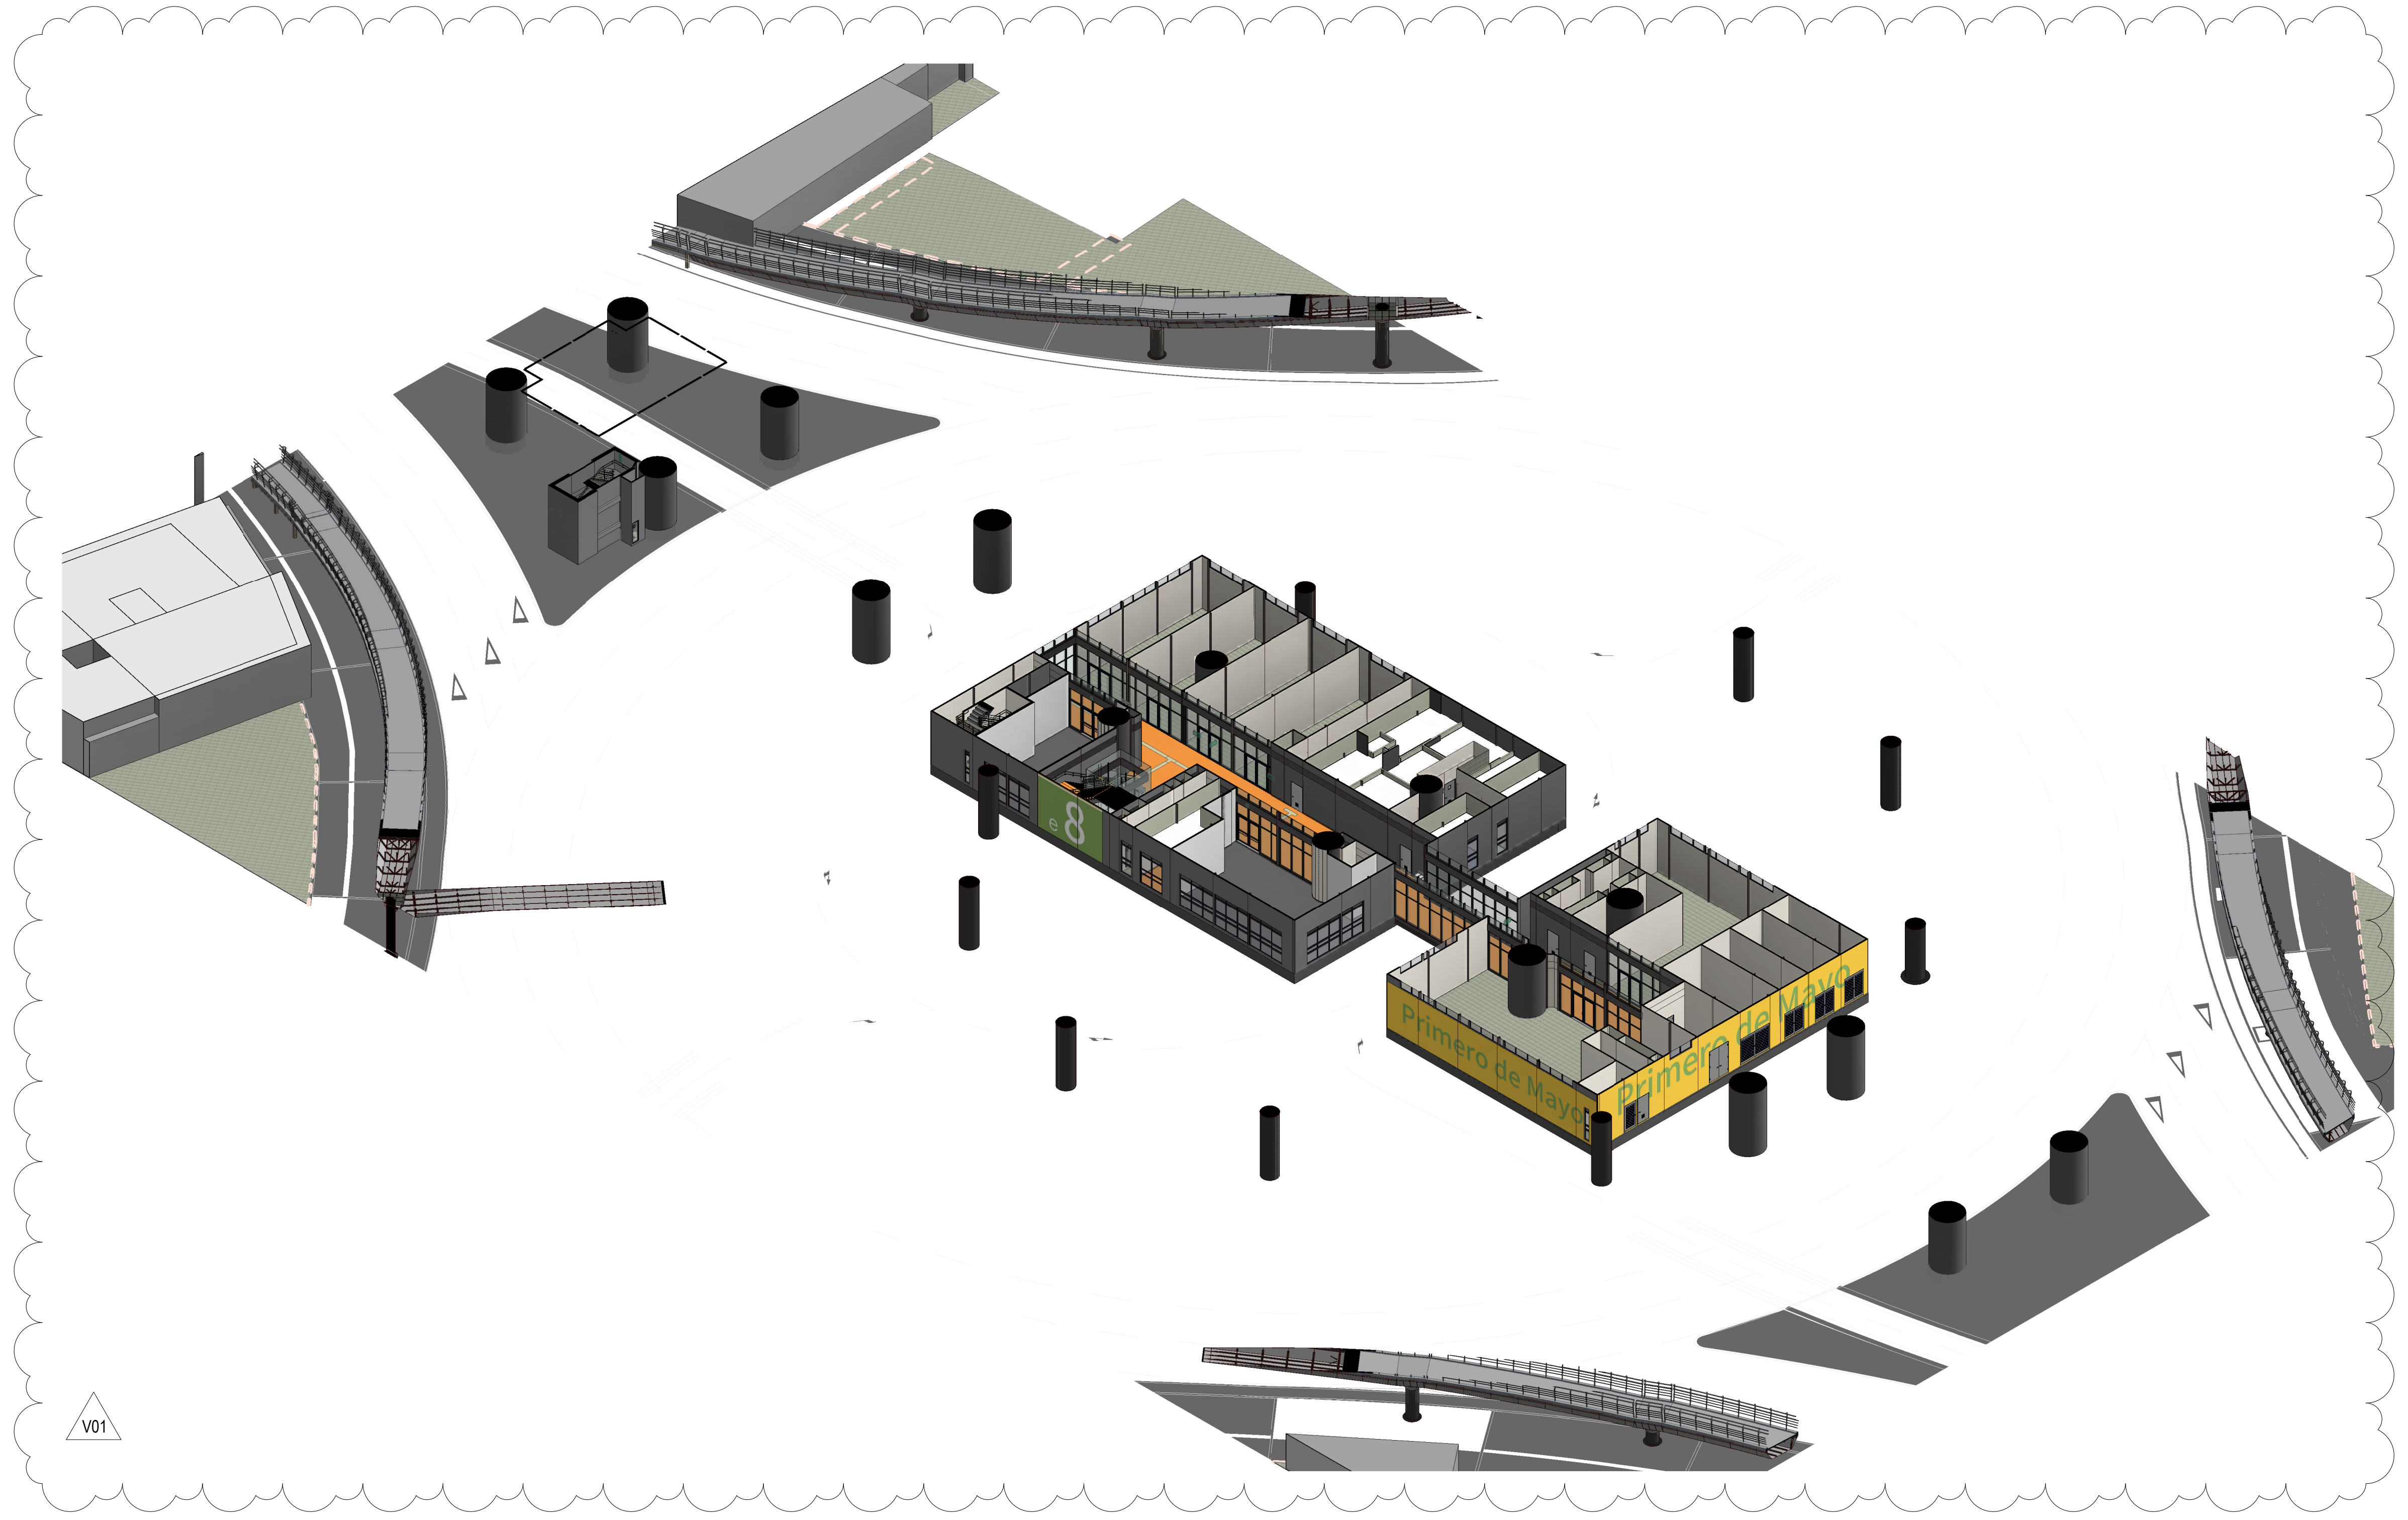

1 3D_NIVEL ACCESO_NAVE CENTRAL
ESC: N/A

LOCALIZACIÓN

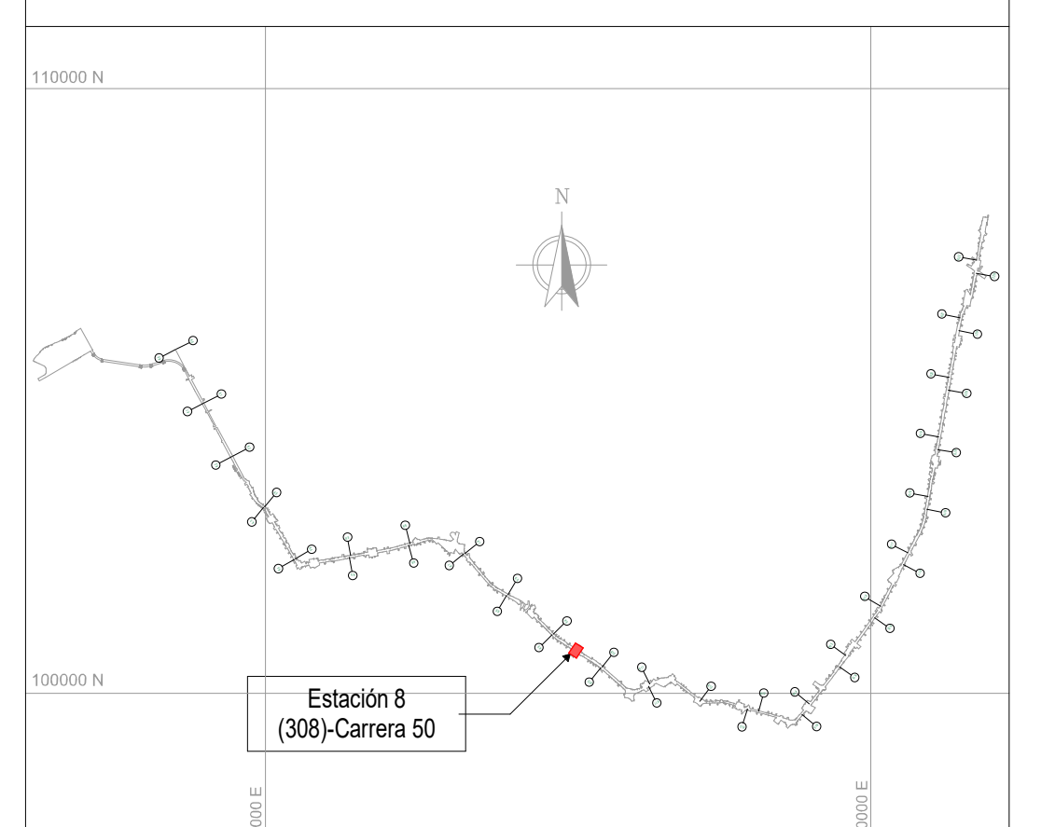

NOTAS

01 TODAS LAS DIMENSIONES ESTÁN CONFIGURADAS EN METROS A MENOS QUE SE INDIQUE UNA UNIDAD DE MEDIDA DIFERENTE.

02 TODAS LAS MEDIDAS, UBICACIÓN Y NIVELES DEBEN VERIFICARSE EN EL LUGAR DE CONSTRUCCIÓN.

03 EL NIVEL DE ACCESO AL EDIFICIO PL 01 CORRESPONDE AL +0,00 DE LA ESTACIÓN Y REFERENCIA AL NIVEL 2555.65 M.S.N.M

04 REVISAR LOS NIVELES ESTRUCTURALES PARA NIVEL DE ACCESO PL_01 Y SUBNIVELES, PL_02 (INTERMEDIO), PL_03 (PLATAFORMA) CON LA PLANIMETRÍA DE PLACAS ESTRUCTURALES EN LOS ENTREGABLES L1T1-1200-308-CON-ED-EST-PL-0068, 69, RESPECTIVAMENTE. EL NIVEL ESTRUCTURAL (NE) REFERENCIA LOS ESPACIOS DONDE SE DEBE ACONDICIONAR EL ACABADO DE PISO SEGÚN CORRESPONDA, CON LOS NIVELES DE PISO TERMINADO (NPT). LOS NIVELES PROYECTADOS DE EMPATE (NPE) EN LAS ÁREAS DE SERVICIOS ADICIONALES, REFERENCIAN LA ADECUACIÓN DE LOS DESNIVELES EN ESTAS ÁREAS; QUEDA COMO RESPONSABILIDAD DEL LOCATARIO DEFINIR Y ACONDICIONAR ESTE ACABADO DE PISO (NPE) EN LÍNEA CON EL NIVEL (NPT) DE ESPACIOS COLINDANTES

05 LAS ESCALERAS ELÉCTRICAS INDICAN SU SENTIDO CON LA SIGUIENTE NOMENCLATURA: "SUBE" Y "BAJA".

06 SE HA DEJADO EL ESPACIO "CALABOZO 2M²" DE ACUERDO CON LO SOLICITADO POR EL APÉNDICE TÉCNICO 6 S 1.1 NUMERAL 2.11.3 DEL CONTRATO DE CONCESIÓN. SIN EMBARGO, ES NUESTRA RECOMENDACIÓN COMO DISEÑADORES QUE ESTE ESPACIO NO SEA DESTINADO PARA ESTE FIN PUES VA EN CONTRA DEL ORDENAMIENTO JURÍDICO COLOMBIANO, EN VIRTUD DEL CUAL LOS LUGARES DE RECLUSIÓN DEBEN SER DEFINIDOS ÚNICAMENTE POR LA LEY. LOS CALABOZOS EN LAS ESTACIONES DE METRO NO ESTÁN ESTABLECIDOS DE MANERA EXPRESA EN NINGUNA NORMA VIGENTE. SERÁ FINALMENTE RESPONSABILIDAD DEL OPERADOR DE ESTE ESPACIO SU USO Y ADMINISTRACIÓN SIN NINGUNA REPERCUSIÓN AL DISEÑADOR.

- ARC_PL_00 = SÓTANO	/ NPT -6.25
- ARC_PL_01 = ACCESO	/ NPT 0.00
- ARC_PL_02 = INTERMEDIO	/ NPT 7.60
- ARC_PL_02.1 = PLACA INFERIOR VIGA CAJÓN	/ NPT 13.82
- ARC_PL_02.2 = TOPE DE RIEL (TOR)	/ NPT 15.95
- ARC_PL_03 = PLATAFORMA	/ NPT 17.09
- ARC_PL_05 = CUBIERTA NAVE CENTRAL	/ NPT 26.42

CONVENCIONES

■	SERVICIOS ADICIONALES - ÁREA NO PAGA	■	ÁREA NO PAGA
■	SERVICIOS ADICIONALES - ÁREA PAGA	■	ÁREA OPERATIVA
■	SERVICIO PÚBLICO	■	ÁREA PAGA
■	ZONA DE REFUGIO	■	ÁREA PÚBLICA
■	ÁREA CULTURAL	■	ÁREA TÉCNICA
■	ÁREA DE TAQUILLAS BRT		

TABLA DE AREAS ÚTILES (NIVEL ACCESO NAVE CENTRAL)

CÓDIGO	NOMBRE	ÁREA (m²)	DEPARTAMENTO
NAVE CENTRAL			
ARQ_PL_01_ACCESO			
NPA	ÁREA NO PAGA	310.44	ÁREA NO PAGA
O-21	ALMACENAMIENTO DE LA ESTACIÓN	25.29	ÁREA OPERATIVA
P-05	BIBLIOMETRO	64.90	ÁREA PÚBLICA
P-07	SALÓN MÚLTIPLE EMB	114.55	ÁREA PÚBLICA
R-00	SERVICIOS ADICIONALES - CORREDOR OPERATIVO	23.69	SERVICIOS ADICIONALES - ÁREA NO PAGA
R-00	SERVICIOS ADICIONALES - CORREDOR OPERATIVO	28.87	SERVICIOS ADICIONALES - ÁREA NO PAGA
R-01	SERVICIOS ADICIONALES - CUARTO DE BASURAS PARA METRO	12.62	SERVICIOS ADICIONALES - ÁREA NO PAGA
R-02	SERVICIOS ADICIONALES - BAÑO PÚBLICO DE MUJERES	18.67	SERVICIOS ADICIONALES - ÁREA NO PAGA
R-03	SERVICIOS ADICIONALES - BAÑO PÚBLICO DE HOMBRES	19.45	SERVICIOS ADICIONALES - ÁREA NO PAGA
R-04	SERVICIOS ADICIONALES - CONTROL DE ACCESO BAÑOS PÚBLICOS	2.78	SERVICIOS ADICIONALES - ÁREA NO PAGA
R-05	SERVICIOS ADICIONALES - CUARTO DE LIMPIEZA	3.20	SERVICIOS ADICIONALES - ÁREA NO PAGA
R-06	SERVICIOS ADICIONALES - BAÑOS EMPLEADOS MUJERES	18.19	SERVICIOS ADICIONALES - ÁREA NO PAGA
R-07	SERVICIOS ADICIONALES - VESTIDORES EMPLEADOS MUJERES	14.14	SERVICIOS ADICIONALES - ÁREA NO PAGA
R-08	SERVICIOS ADICIONALES - BAÑOS EMPLEADOS HOMBRES	14.25	SERVICIOS ADICIONALES - ÁREA NO PAGA
R-09	SERVICIOS ADICIONALES - VESTIDORES EMPLEADOS HOMBRES	14.14	SERVICIOS ADICIONALES - ÁREA NO PAGA
R-10	SERVICIOS ADICIONALES - SALA DE EMPLEADOS	22.02	SERVICIOS ADICIONALES - ÁREA NO PAGA
R-103	SERVICIOS ADICIONALES - ÁREA DE SERVICIO	115.71	SERVICIOS ADICIONALES - ÁREA NO PAGA
R-104	SERVICIOS ADICIONALES - ÁREA DE SERVICIO	192.23	SERVICIOS ADICIONALES - ÁREA NO PAGA
R-201	SERVICIOS ADICIONALES - ÁREA DE COMIDAS	71.02	SERVICIOS ADICIONALES - ÁREA NO PAGA
R-202	SERVICIOS ADICIONALES - ÁREA DE COMIDAS	69.13	SERVICIOS ADICIONALES - ÁREA NO PAGA
R-203	SERVICIOS ADICIONALES - ÁREA DE COMIDAS	67.19	SERVICIOS ADICIONALES - ÁREA NO PAGA
R-204	SERVICIOS ADICIONALES - ÁREA DE COMIDAS	67.89	SERVICIOS ADICIONALES - ÁREA NO PAGA
T-00	CIRCULACIÓN TÉCNICA	23.72	ÁREA TÉCNICA
T-01	ÁREA DE INSPECCIÓN	21.67	ÁREA TÉCNICA
T-08	CENTRO DE TRANSFORMACIÓN ENEL-CODENSA (CT)	32.30	ÁREA TÉCNICA
T-20-G	MEDIDORES (GAS)	7.88	ÁREA TÉCNICA
T-21	ÁREA DE INSPECCIÓN	11.49	ÁREA TÉCNICA
T-21	ÁREA DE INSPECCIÓN	9.91	ÁREA TÉCNICA
T-21	ÁREA DE INSPECCIÓN	15.92	ÁREA TÉCNICA
T-25	NODO DE ACCESO DE TELECOMUNICACIONES	5.55	ÁREA TÉCNICA
T-29	SUBESTACIÓN ELÉCTRICA ESTACIÓN DE BOMBEO	72.09	ÁREA TÉCNICA
TOTAL NIVEL ACCESO		1490.91	

TABLA DE ÁREAS ÚTILES POR DEPARTAMENTO (NIVEL ACCESO)

DEPARTAMENTO	ÁREA (m²)
SERVICIOS ADICIONALES - ÁREA NO PAGA	775.21
ÁREA NO PAGA	310.44
ÁREA OPERATIVA	25.29
ÁREA PÚBLICA	179.45
ÁREA TÉCNICA	200.52
TOTAL NIVEL ACCESO	1490.91

V01 CAMBIOS EFECTUADOS:
1.ACTUALIZACIÓN DEL PROYECTO DE FACHADA

No.	PLANOS DE REFERENCIA	REV.

No.	MODELO BIM DE REFERENCIA	REV.
1	L1T1-1100-208-CON-ED-EST-MO-0001.rvt	V00
2	L1T1-1100-209-CON-ED-EST-MO-0001.rvt	V00
3	L1T1-1100-308-CON-ED-EST-MO-0001.rvt	V00
4	L1T1-1150-208-CON-ED-EST-MO-0001.rvt	V00
5	L1T1-1150-209-CON-ED-EST-MO-0001.rvt	V00
6	L1T1-1150-308-CON-ED-EST-MO-0001.rvt	V00
7	L1T1-1200-308-CON-ED-EST-MO-0001.rvt	V00
8	L1T1-1410-308-CON-ED-MEC-MO-0001.rvt	V00
9	L1T1-1420-308-CON-ED-MEC-MO-0001.rvt	V00
10	L1T1-2420-561-CON-ED-MEC-MO-0001.rvt	V00
11	L1T1-5160-308-CON-ED-EST-MO-0001.rvt	V00
12	L1T1-5160-308-CON-ED-ARQ-MO-0001.rvt	V00
13	L1T1-5300-308-CON-ED-MEC-MO-0001.rvt	V00
14	L1T1-1270-308-CON-ED-ARQ-MO-0011.rvt	V00

No.	PAQUETE DE TRABAJO DE REFERENCIA	REV.
1	XREF-URBANISM_CONTEXT_ST08.rvt	
2	XREF-SECONDARY-STRUCTURE-ST08.rvt	

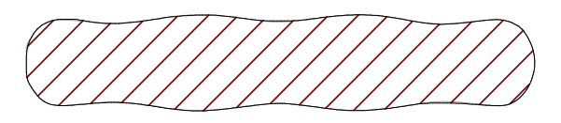

PLANO CLAVE ESTACIÓN 08

0 2 10m
1:200

VÁLIDO PARA CONSTRUCCIÓN
31-03-26

METRO BOGOTÁ
Consorcio Consultores PMO Bogotá
CONSORCIO SUPERVISOR PLMB

DISEÑÓ:
REN ZHENHUA
Licencia de Arq.nivel I (China): 1101735-614

APROBÓ:
DIEGO ERNESTO DUEÑAS
Mat.: 25202-53876 CND

REVISÓ:
CARLOS MAURICIO BARRETO BARBOSA
Mat.: A4012012-14139353

DIBUJÓ:
EQUIPO CHEC

REVISIÓN No.	FECHA	DESCRIPCIÓN	REVISÓ	APROBÓ	APROBACIÓN CLIENTE
V01	31/03/2026	EMITIDO PARA CONSTRUCCIÓN	C.M.B.B	D.E.D	
V00	12/12/2025	REVISIÓN NO OBJETADA - EMITIDO PARA CONSTRUCCIÓN	F.B.R	M.M.R	
VCC	01/10/2025	EMITIDO PARA REVISIÓN Y COMENTARIOS DEL CLIENTE E INTERVENTORÍA - INCLUYE COMENTARIOS /(AJUSTE)	F.B.R	M.M.R	
VBB	15/07/2025	EMITIDO PARA REVISIÓN Y COMENTARIOS DEL CLIENTE E INTERVENTORÍA	F.B.R	M.M.R	
VA0	04/07/2025	EMITIDO PARA COMENTARIOS INTERNOS - EMISIÓN PRELIMINAR PARA COMENTARIOS	F.B.R	M.M.R	

METRO LÍNEA 1

METRO LÍNEA 1
CONTRATO DE CONCESIÓN No. 163 DE 2019

PROYECTO PRIMERA LÍNEA DEL METRO DE BOGOTÁ - TRAMO 1

DIRECTOR DE INTERVENTORÍA:
JAVIER DESCARGA N.
Mat.:25202-68697 CND

ESPECIALISTA INTERVENTORÍA:
CARLOS ALBERTO HOYOS SOTO
Mat.:A25072000-14251682

FECHA:
MARZO 2026

INFRAESTRUCTURA VIAL

ARQUITECTURA

ESTACIÓN METRO 8 (CARRERA 50)
NAVE CENTRAL
VISTA EN PLANTA Y 3D - NIVEL ACCESO

PLANCHA No: L1T1-0000-308-CON-ED-ARQ-PL-0022_05_V01
ARCHIVO: L1T1-0000-308-CON-ED-ARQ-MO-0002_V00.rvt
ESCALA: INDICADA
FECHA: JULIO 2025
REVISIÓN No. V01
PLANO No. 05 DE 45