L1T1-CON-CAL-FR-0122 - A3-EXT1 : 1891x707mm

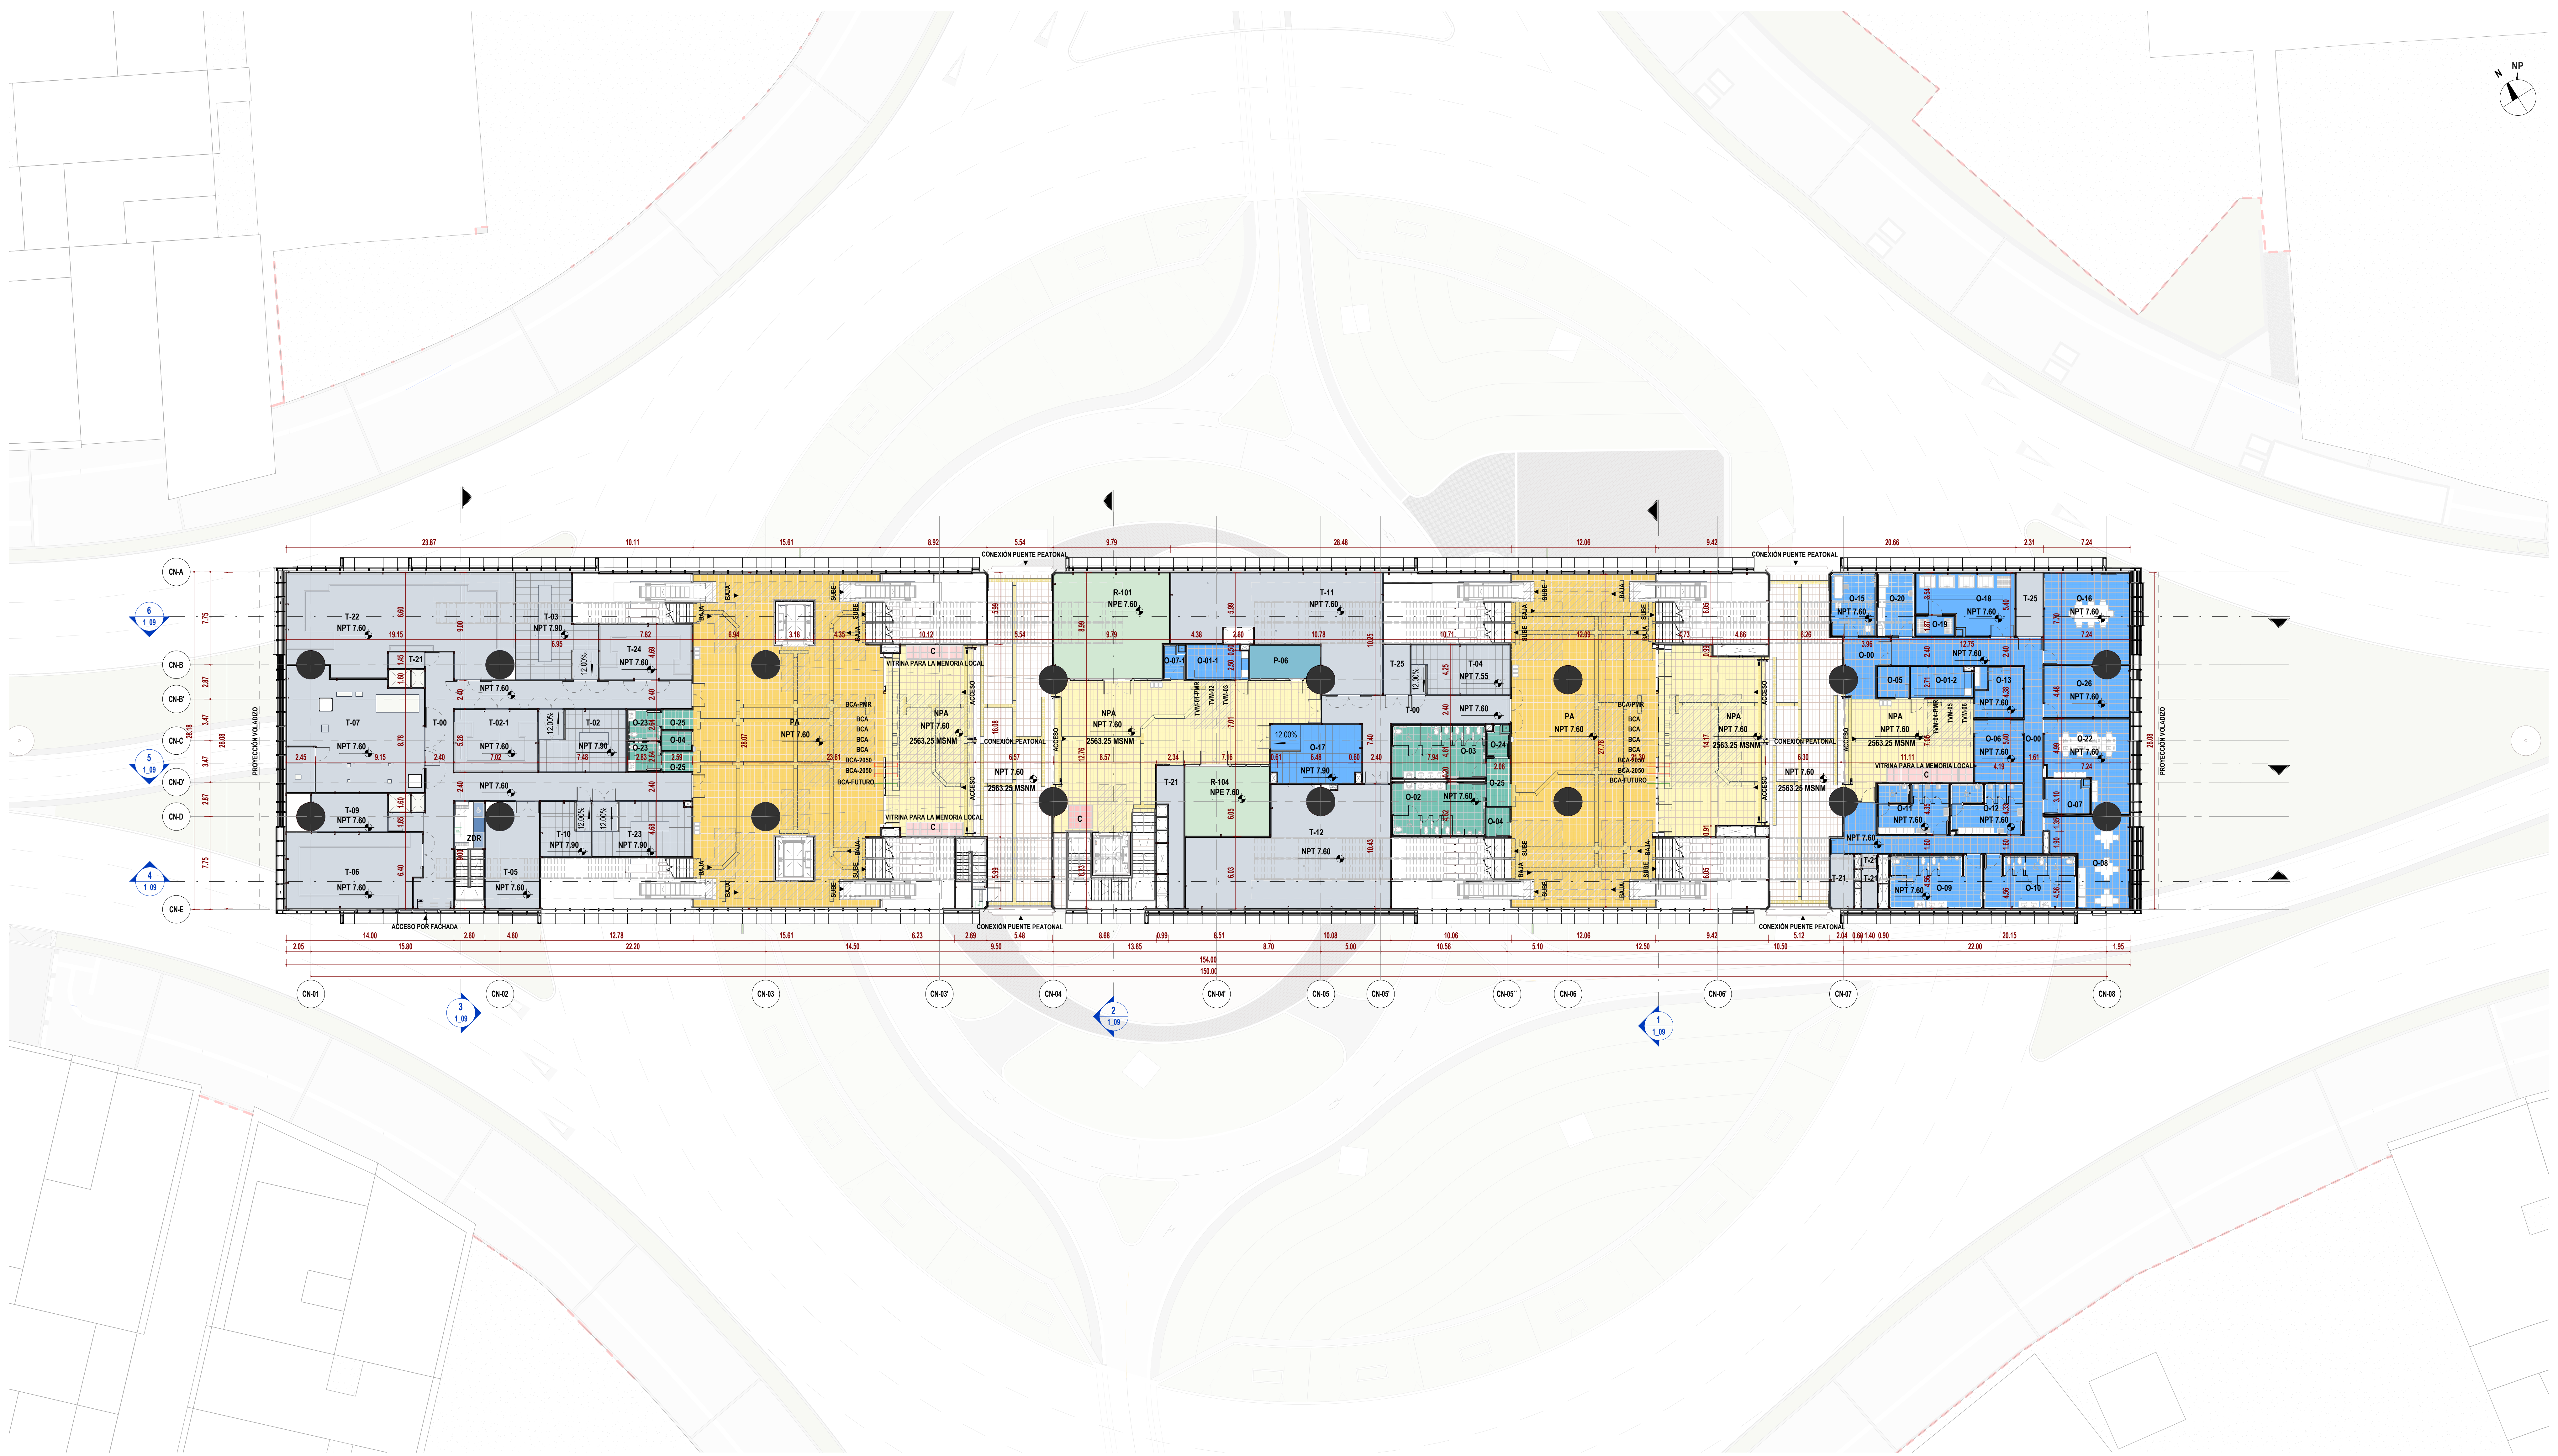

2 NIVEL INTERMEDIO_NAVE CENTRAL
ESC: 1:200

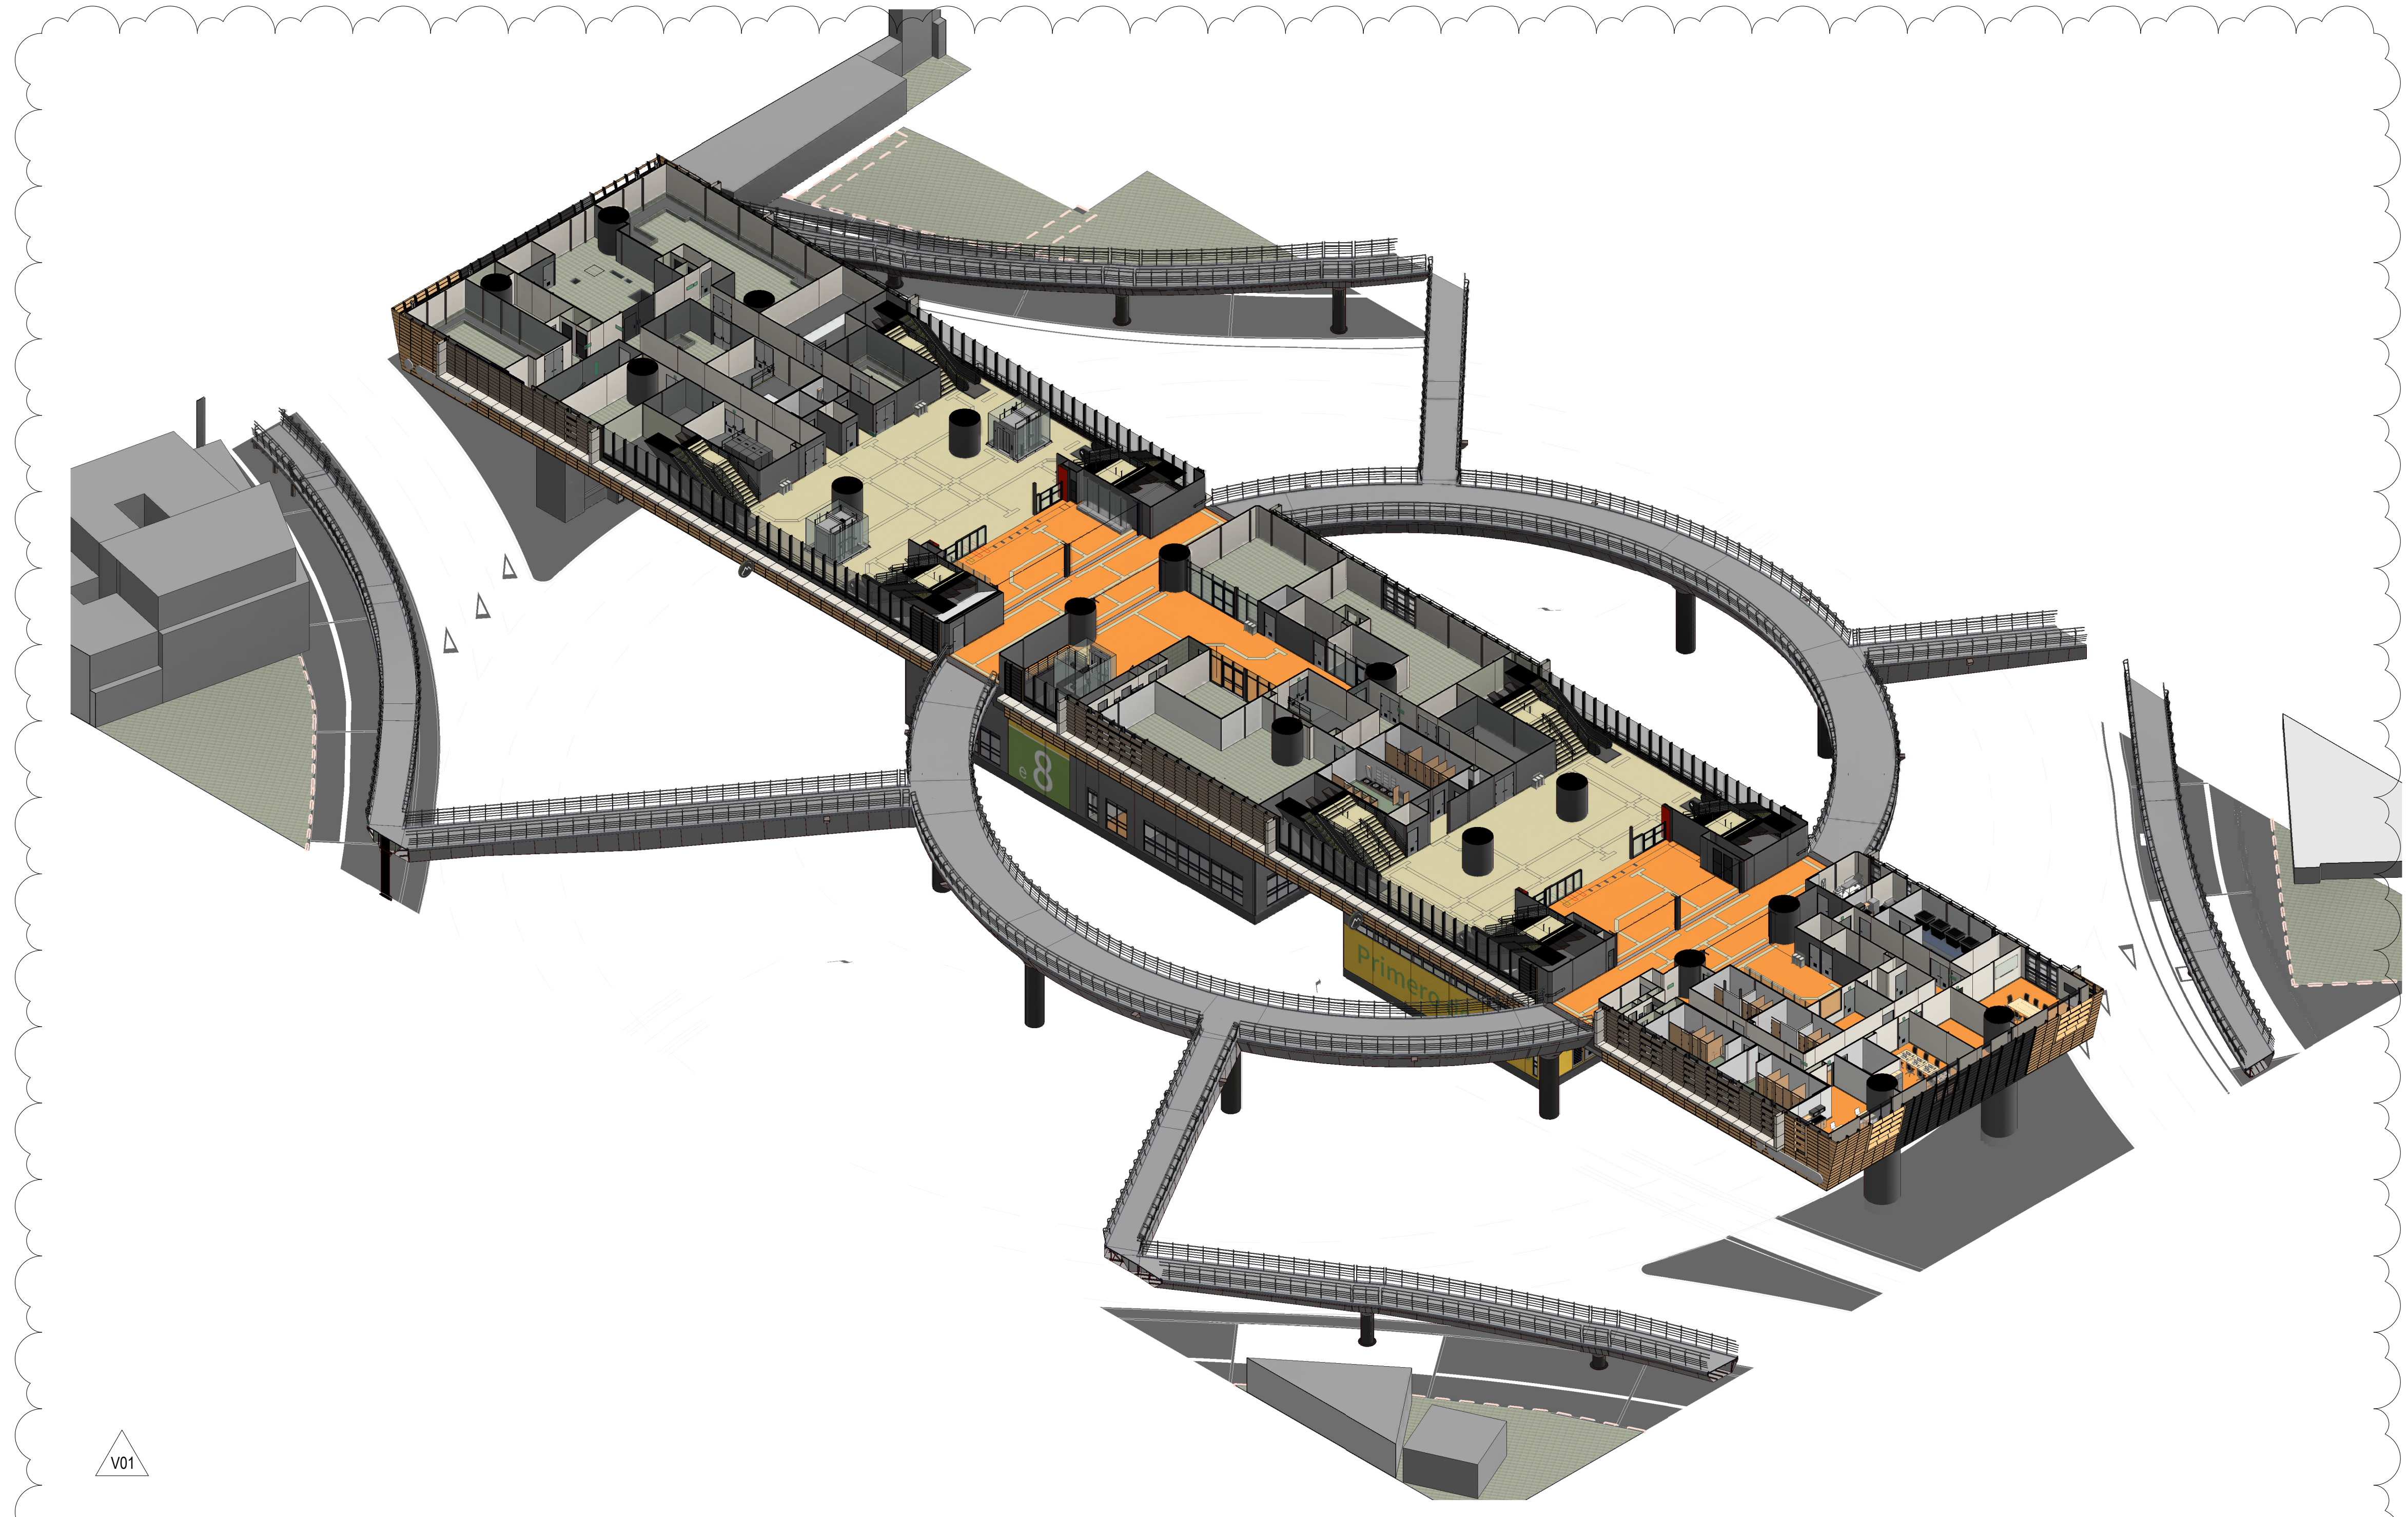

1 3D_NIVEL INTERMEDIO_NAVE CENTRAL
ESC: N/A

V01

TABLA DE AREAS ÚTILES (NIVEL INTERMEDIO NAVE CENTRAL)			
CÓDIGO	**NOMBRE**	**AREA (m²)**	**DEPARTAMENTO**
NAVE CENTRAL			
ARQ_PL_01_ACCESO			
ZDR	ZONA DE REFUGIO (PMR)	2.55	ZONA DE REFUGIO
ARQ_PL_02_INTERMEDIO			
C	ÁREAS DE USO CULTURAL	5.76	ÁREA CULTURAL
C	ÁREAS DE USO CULTURAL	8.96	ÁREA CULTURAL
C	ÁREAS DE USO CULTURAL	5.76	ÁREA CULTURAL
C	ÁREAS DE USO CULTURAL	3.99	ÁREA CULTURAL
NPA	ÁREA NO PAGA	107.66	ÁREA NO PAGA
NPA	ÁREA NO PAGA	138.61	ÁREA NO PAGA
NPA	ÁREA NO PAGA	179.26	ÁREA NO PAGA
NPA	ÁREA NO PAGA	71.20	ÁREA NO PAGA
O-00	CIRCULACIÓN ÁREAS OPERATIVAS	82.84	ÁREA OPERATIVA
O-00	CIRCULACIÓN ÁREAS OPERATIVAS	14.04	ÁREA OPERATIVA
O-01-1	VENTA AUTOMÁTICA DE BOLETOS	14.50	ÁREA OPERATIVA
O-01-2	VENTA AUTOMÁTICA DE BOLETOS	13.24	ÁREA OPERATIVA
O-02	BAÑOS PÚBLICOS DE HOMBRES	34.34	SERVICIO PÚBLICO
O-03	BAÑOS PÚBLICOS DE MUJERES	34.34	SERVICIO PÚBLICO
O-04	CONTROL DE ACCESO BAÑOS PÚBLICOS	4.58	SERVICIO PÚBLICO
O-04	CONTROL DE ACCESO BAÑOS PÚBLICOS	4.02	SERVICIO PÚBLICO
O-05	LOCAL DE INFORMACIÓN	6.86	ÁREA OPERATIVA
O-06	OFICINA DEL SUPERVISOR DE LA ESTACIÓN	21.36	ÁREA OPERATIVA
O-07	CUARTO DE LIMPIEZA	11.56	ÁREA OPERATIVA
O-07-1	CUARTO DE LIMPIEZA	5.26	ÁREA OPERATIVA
O-08	SALA DE DESCANSO PARA EMPLEADOS	38.31	ÁREA OPERATIVA
O-09	BAÑOS EMPLEADOS HOMBRES	33.55	ÁREA OPERATIVA
O-10	BAÑOS EMPLEADOS MUJERES	33.58	ÁREA OPERATIVA
O-11	VESTIDORES EMPLEADOS HOMBRES	25.41	ÁREA OPERATIVA
O-12	VESTIDORES EMPLEADOS MUJERES	25.46	ÁREA OPERATIVA
O-13	LOCAL DE POLICÍA	15.02	ÁREA OPERATIVA
O-14	CALABOZO	2.02	ÁREA OPERATIVA
O-15	LOCAL PRIMEROS AUXILIOS	19.77	ÁREA OPERATIVA
O-16	SALA DE REUNIONES	51.99	ÁREA OPERATIVA
O-17	OPERADORES TELECOMUNICACIONES EXTERIORES	35.61	ÁREA OPERATIVA
O-18	CUARTO DE ALMACENAMIENTO DE RESIDUOS SÓLIDOS	37.20	ÁREA OPERATIVA
O-19	CUARTO DE ALMACENAMIENTO DE RESIDUOS PELIGROSOS	5.55	ÁREA OPERATIVA
O-20	SALA DE LACTANCIA	16.12	ÁREA OPERATIVA
O-22	OFICINA DE MANTENIMIENTO	42.29	ÁREA OPERATIVA

TABLA DE AREAS ÚTILES (NIVEL INTERMEDIO NAVE CENTRAL)			
CÓDIGO	**NOMBRE**	**AREA (m²)**	**DEPARTAMENTO**
O-23	BAÑO PÚBLICO - FAMILIAR	6.75	SERVICIO PÚBLICO
O-23	BAÑO PÚBLICO - FAMILIAR	6.75	SERVICIO PÚBLICO
O-24	CUARTO DE LIMPIEZA DE BAÑOS PÚBLICOS	4.87	SERVICIO PÚBLICO
O-25	BAÑO PÚBLICO - CORREDOR OPERACIONAL	8.04	SERVICIO PÚBLICO
O-25	BAÑO PÚBLICO - CORREDOR OPERACIONAL	4.21	SERVICIO PÚBLICO
O-25	BAÑO PÚBLICO - CORREDOR OPERACIONAL	4.21	SERVICIO PÚBLICO
O-26	ALMACENAMIENTO DE BASURAS METRO	29.03	ÁREA OPERATIVA
P-06	ESPACIO IPES (INSTITUTO PARA LA ECONOMÍA SOCIAL)	15.21	ÁREA PÚBLICA
PA	ÁREA PAGA	414.75	ÁREA PAGA
PA	ÁREA PAGA	334.09	ÁREA PAGA
R-101	SERVICIOS ADICIONALES - ÁREA DE SERVICIO	83.44	SERVICIOS ADICIONALES - ÁREA NO PAGA
R-104	SERVICIOS ADICIONALES - ÁREA DE SERVICIO	42.25	SERVICIOS ADICIONALES - ÁREA NO PAGA
T-00	CIRCULACIÓN TÉCNICA	143.77	ÁREA TÉCNICA
T-00	CIRCULACIÓN TÉCNICA	47.41	ÁREA TÉCNICA
T-02	LOCAL DE CONDUCCIÓN AUTOMÁTICA (CBTC)	37.68	ÁREA TÉCNICA
T-02-1	UPS DEDICADA (CBTC)	35.48	ÁREA TÉCNICA
T-03	TELECOMUNICACIONES ESTACIÓN - CORRIENTE DÉBIL	51.21	ÁREA TÉCNICA
T-04	EQUIPO BOLETERÍA	33.74	ÁREA TÉCNICA
T-05	ALMACÉN PARA MANTENIMIENTO	35.00	ÁREA TÉCNICA
T-06	SALA DE TABLEROS	68.70	ÁREA TÉCNICA
T-07	CENTRO DE TRANSFORMACIÓN (CT)	108.37	ÁREA TÉCNICA
T-09	ALMACÉN EQUIPO ELÉCTRICO	17.73	ÁREA TÉCNICA
T-10	CUARTO DE EQUIPO ELECTROMECÁNICO	18.84	ÁREA TÉCNICA
T-11	CUARTO DE VENTILACIÓN	119.46	ÁREA TÉCNICA
T-12	PLANTA DE REFRIGERACIÓN PARA LA CLIMATIZACIÓN	139.06	ÁREA TÉCNICA
T-21	ÁREA DE INSPECCIÓN	4.01	ÁREA TÉCNICA
T-21	ÁREA DE INSPECCIÓN	17.85	ÁREA TÉCNICA
T-21	ÁREA DE INSPECCIÓN	8.47	ÁREA TÉCNICA
T-21	ÁREA DE INSPECCIÓN	4.15	ÁREA TÉCNICA
T-21	ÁREA DE INSPECCIÓN	1.62	ÁREA TÉCNICA
T-21	ÁREA DE INSPECCIÓN	4.42	ÁREA TÉCNICA
T-22	CUARTO DE UPS	143.15	ÁREA TÉCNICA
T-23	CUARTO PDAP	37.31	ÁREA TÉCNICA
T-24	TETRA UPS	35.24	ÁREA TÉCNICA
T-25	NODO DE ACCESO DE TELECOMUNICACIONES	11.64	ÁREA TÉCNICA
T-25	NODO DE ACCESO DE TELECOMUNICACIONES	9.09	ÁREA TÉCNICA
ZDR	ZONA DE REFUGIO (PMR)	3.50	ZONA DE REFUGIO
TOTAL NIVEL INTERMEDIO		3243.07	

TABLA DE ÁREAS ÚTILES POR DEPARTAMENTO (NIVEL INTERMEDIO)	
DEPARTAMENTO	**ÁREA (m²)**
SERVICIO PÚBLICO	112.11
SERVICIOS ADICIONALES - ÁREA NO PAGA	125.69
ZONA DE REFUGIO	6.05
ÁREA CULTURAL	24.47
ÁREA NO PAGA	496.74
ÁREA OPERATIVA	580.57
ÁREA PAGA	748.84
ÁREA PÚBLICA	15.21
ÁREA TÉCNICA	1133.39
TOTAL NIVEL INTERMEDIO	3243.07

VÁLIDO PARA CONSTRUCCIÓN
31-03-26

LOCALIZACIÓN

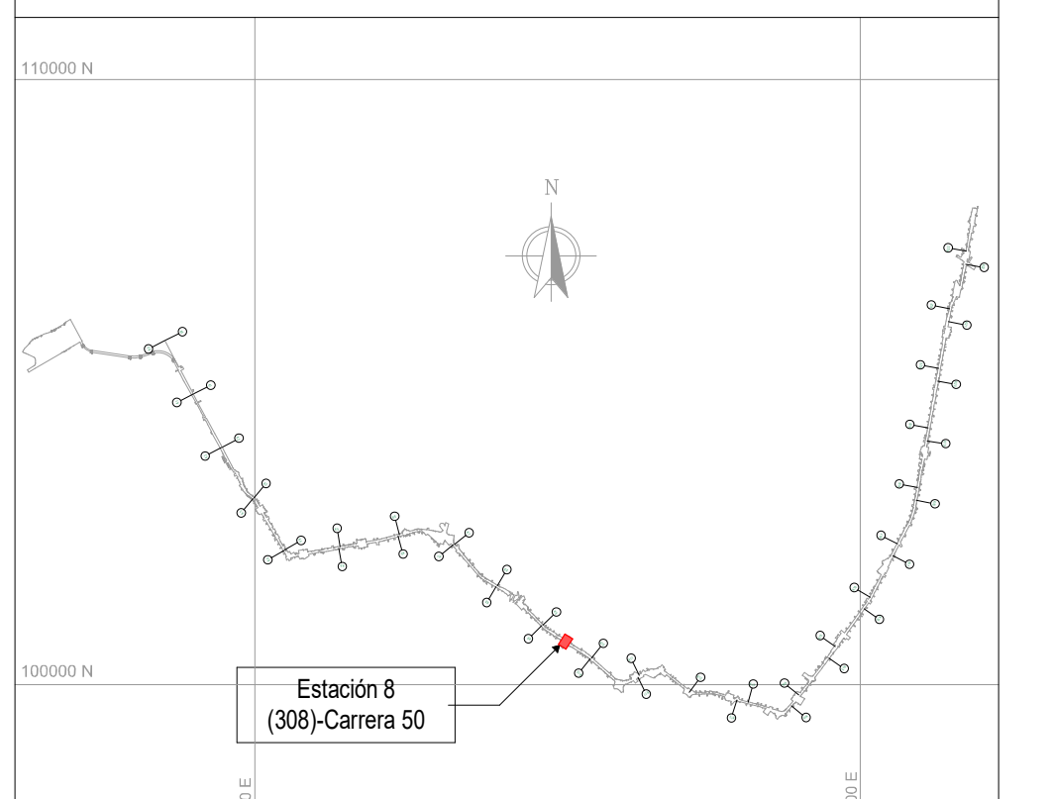

NOTAS

01 TODAS LAS DIMENSIONES ESTÁN CONFIGURADAS EN METROS A MENOS QUE SE INDIQUE UNA UNIDAD DE MEDIDA DIFERENTE.

02 TODAS LAS MEDIDAS, UBICACIÓN Y NIVELES DEBEN VERIFICARSE EN EL LUGAR DE CONSTRUCCIÓN.

03 EL NIVEL DE ACCESO AL EDIFICIO PL 01 CORRESPONDE AL +0,00 DE LA ESTACIÓN Y REFERENCIA AL NIVEL 2555.65 M.S.N.M

04 REVISAR LOS NIVELES ESTRUCTURALES PARA NIVEL DE ACCESO PL_01 Y SUBNIVELES, PL_02 (INTERMEDIO), PL_03 (PLATAFORMA) CON LA PLANIMETRÍA DE PLACAS ESTRUCTURALES EN LOS ENTREGABLES L1T1-1200-308-CON-ED-EST-PL-0068, 69, RESPECTIVAMENTE. EL NIVEL ESTRUCTURAL (NE) REFERENCIA LOS ESPACIOS DONDE SE DEBE ACONDICIONAR EL ACABADO DE PISO SEGÚN CORRESPONDA, CON LOS NIVELES DE PISO TERMINADO (NPT). LOS NIVELES PROYECTADOS DE EMPATE (NPE) EN LAS ÁREAS DE SERVICIOS ADICIONALES, REFERENCIAN LA ADECUACIÓN DE LOS DESNIVELES EN ESTAS ÁREAS; QUEDA COMO RESPONSABILIDAD DEL LOCATARIO DEFINIR Y ACONDICIONAR ESTE ACABADO DE PISO (NPE) EN LÍNEA CON EL NIVEL (NPT) DE ESPACIOS COLINDANTES

05 LAS ESCALERAS ELÉCTRICAS INDICAN SU SENTIDO CON LA SIGUIENTE NOMENCLATURA: "SUBE" Y "BAJA".

06 SE HA DEJADO EL ESPACIO "CALABOZO 2M²" DE ACUERDO CON LO SOLICITADO POR EL APÉNDICE TÉCNICO 6 S 1.1 NUMERAL 2.11.3 DEL CONTRATO DE CONCESIÓN. SIN EMBARGO, ES NUESTRA RECOMENDACIÓN COMO DISEÑADORES QUE ESTE ESPACIO NO SEA DESTINADO PARA ESTE FIN PUES VA EN CONTRA DEL ORDENAMIENTO JURÍDICO COLOMBIANO, EN VIRTUD DEL CUAL LOS LUGARES DE RECLUSIÓN DEBEN SER DEFINIDOS ÚNICAMENTE POR LA LEY. LOS CALABOZOS EN LAS ESTACIONES DE METRO NO ESTÁN ESTABLECIDOS DE MANERA EXPRESA EN NINGUNA NORMA VIGENTE. SERÁ FINALMENTE RESPONSABILIDAD DEL OPERADOR DE ESTE ESPACIO SU USO Y ADMINISTRACIÓN SIN NINGUNA REPERCUSIÓN AL DISEÑADOR.

- ARC_PL_00 = SÓTANO	/ NPT -6.25
- ARC_PL_01 = ACCESO	/ NPT 0.00
- ARC_PL_02 = INTERMEDIO	/ NPT 7.60
- ARC_PL_02.1 = PLACA INFERIOR VIGA CAJÓN	/ NPT 13.82
- ARC_PL_02.2 = TOPE DE RIEL (TOR)	/ NPT 15.95
- ARC_PL_03 = PLATAFORMA	/ NPT 17.09
- ARC_PL_05 = CUBIERTA NAVE CENTRAL	/ NPT 26.42

CONVENCIONES

🟩	SERVICIOS ADICIONALES - ÁREA NO PAGA	🟨	ÁREA NO PAGA
🟩	SERVICIOS ADICIONALES - ÁREA PAGA	🟦	ÁREA OPERATIVA
🟩	SERVICIO PÚBLICO	🟧	ÁREA PAGA
🟦	ZONA DE REFUGIO	🟦	ÁREA PÚBLICA
🟥	ÁREA CULTURAL	⬜	ÁREA TÉCNICA
🟪	ÁREA DE TAQUILLAS BRT		

V01 CAMBIOS EFECTUADOS:
1.ACTUALIZACIÓN DEL PROYECTO DE FACHADA

No.	PLANOS DE REFERENCIA	REV.

No.	MODELO BIM DE REFERENCIA	REV.
1	L1T1-1100-208-CON-ED-EST-MO-0001.rvt	V00
2	L1T1-1100-209-CON-ED-EST-MO-0001.rvt	V00
3	L1T1-1100-308-CON-ED-EST-MO-0001.rvt	V00
4	L1T1-1150-208-CON-ED-EST-MO-0001.rvt	V00
5	L1T1-1150-209-CON-ED-EST-MO-0001.rvt	V00
6	L1T1-1150-308-CON-ED-EST-MO-0001.rvt	V00
7	L1T1-1200-308-CON-ED-EST-MO-0001.rvt	V00
8	L1T1-1410-308-CON-ED-MEC-MO-0001.rvt	V00
9	L1T1-1420-308-CON-ED-MEC-MO-0001.rvt	V00
10	L1T1-2420-561-CON-ED-MEC-MO-0001.rvt	V00
11	L1T1-5160-308-CON-ED-EST-MO-0001.rvt	V00
12	L1T1-5160-308-CON-ED-ARQ-MO-0001.rvt	V00
13	L1T1-5300-308-CON-ED-MEC-MO-0001.rvt	V00
14	L1T1-1270-308-CON-ED-ARQ-MO-0011.rvt	V00

No.	PAQUETE DE TRABAJO DE REFERENCIA	REV.
1	XREF-URBANISM_CONTEXT_ST08.rvt	
2	XREF-SECONDARY-STRUCTURE-ST08.rvt	

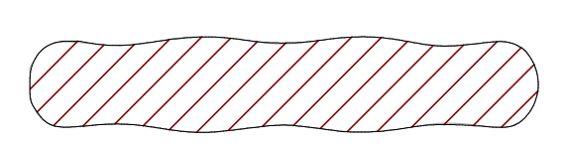

PLANO CLAVE ESTACIÓN 08

0 2 10m
1:200

METRO BOGOTÁ
GCS Consorcio Consultores PMO Bogotá
CONSORCIO SUPERVISOR PLMB
CHEC

DISEÑÓ:
REN ZHENHUA
Licencia de Arq.nivel I (China): 1101735-614

APROBÓ:
DIEGO ERNESTO DUEÑAS
Mat.: 25202-53876 CND

REVISÓ:
CARLOS MAURICIO BARRETO BARBOSA
Mat.: A4012012-14139353

DIBUJÓ:
EQUIPO CHEC

REVISIÓN No.	FECHA	DESCRIPCIÓN	REVISÓ	APROBÓ	APROBACIÓN CLIENTE
V01	31/03/2026	EMITIDO PARA CONSTRUCCIÓN	C.M.B.B	D.E.D	
V00	12/12/2025	REVISIÓN NO OBJETADA - EMITIDO PARA CONSTRUCCIÓN	F.B.R	M.M.R	
VCC	01/10/2025	EMITIDO PARA REVISIÓN Y COMENTARIOS DEL CLIENTE E INTERVENTORÍA - INCLUYE COMENTARIOS /(AJUSTE)	F.B.R	M.M.R	
VBB	15/07/2025	EMITIDO PARA REVISIÓN Y COMENTARIOS DEL CLIENTE E INTERVENTORÍA	F.B.R	M.M.R	
VA0	04/07/2025	EMITIDO PARA COMENTARIOS INTERNOS - EMISIÓN PRELIMINAR PARA COMENTARIOS	F.B.R	M.M.R	

METRO LÍNEA 1

METRO LÍNEA 1
CONTRATO DE CONCESIÓN No. 163 DE 2019

PROYECTO PRIMERA LÍNEA DEL METRO DE BOGOTÁ - TRAMO 1

DIRECTOR DE INTERVENTORÍA:
JAVIER DESCARGA N.
Mat.:25202-68697 CND

ESPECIALISTA INTERVENTORÍA:
CARLOS ALBERTO HOYOS SOTO
Mat.:A25072000-14251682

FECHA:
MARZO 2026

INFRAESTRUCTURA VIAL

ARQUITECTURA

ESTACIÓN METRO 8 (CARRERA 50)
NAVE CENTRAL
VISTA EN PLANTA Y 3D - NIVEL INTERMEDIO

PLANCHA No: L1T1-0000-308-CON-ED-ARQ-PL-0022_06_V01
ARCHIVO: L1T1-0000-308-CON-ED-ARQ-MO-0002_V00.rvt
ESCALA: INDICADA
FECHA: JULIO 2025
REVISIÓN No. V01
PLANO No. 06 DE 45