L1T1-CON-CAL-FR-0122 - A3-EXT1 : 1681x707mm

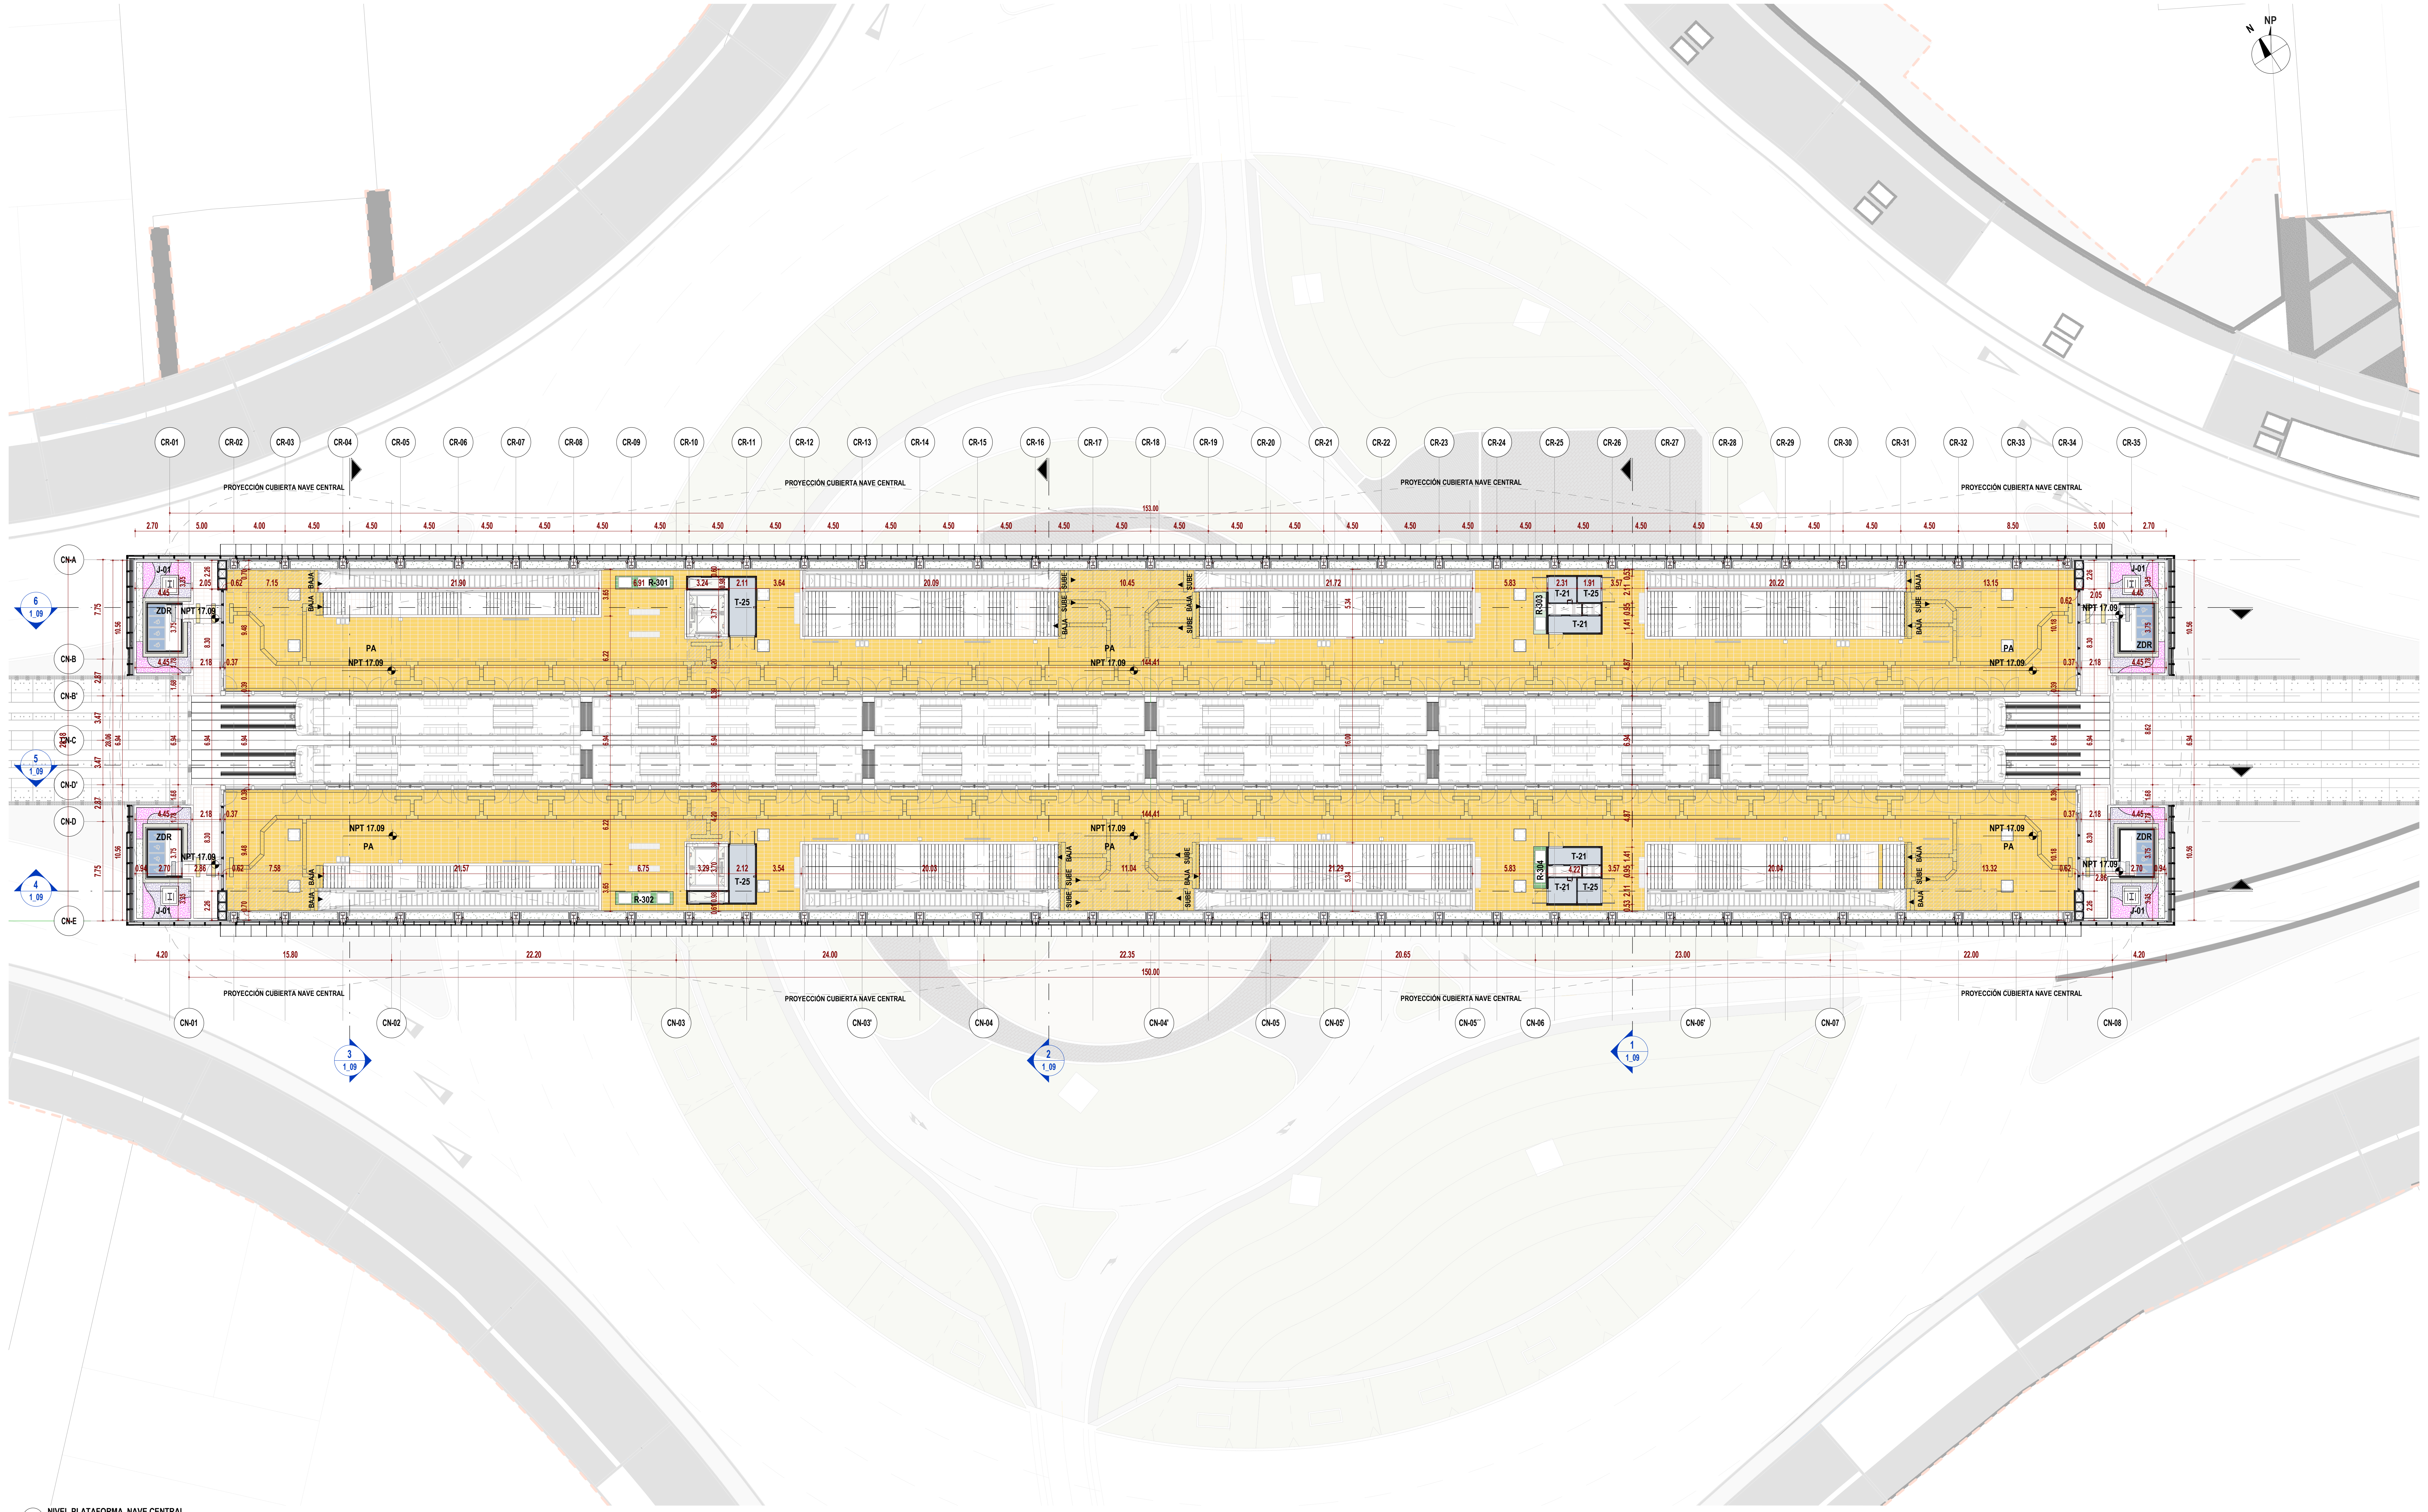

2 NIVEL PLATAFORMA_NAVE CENTRAL
ESC: 1 : 200

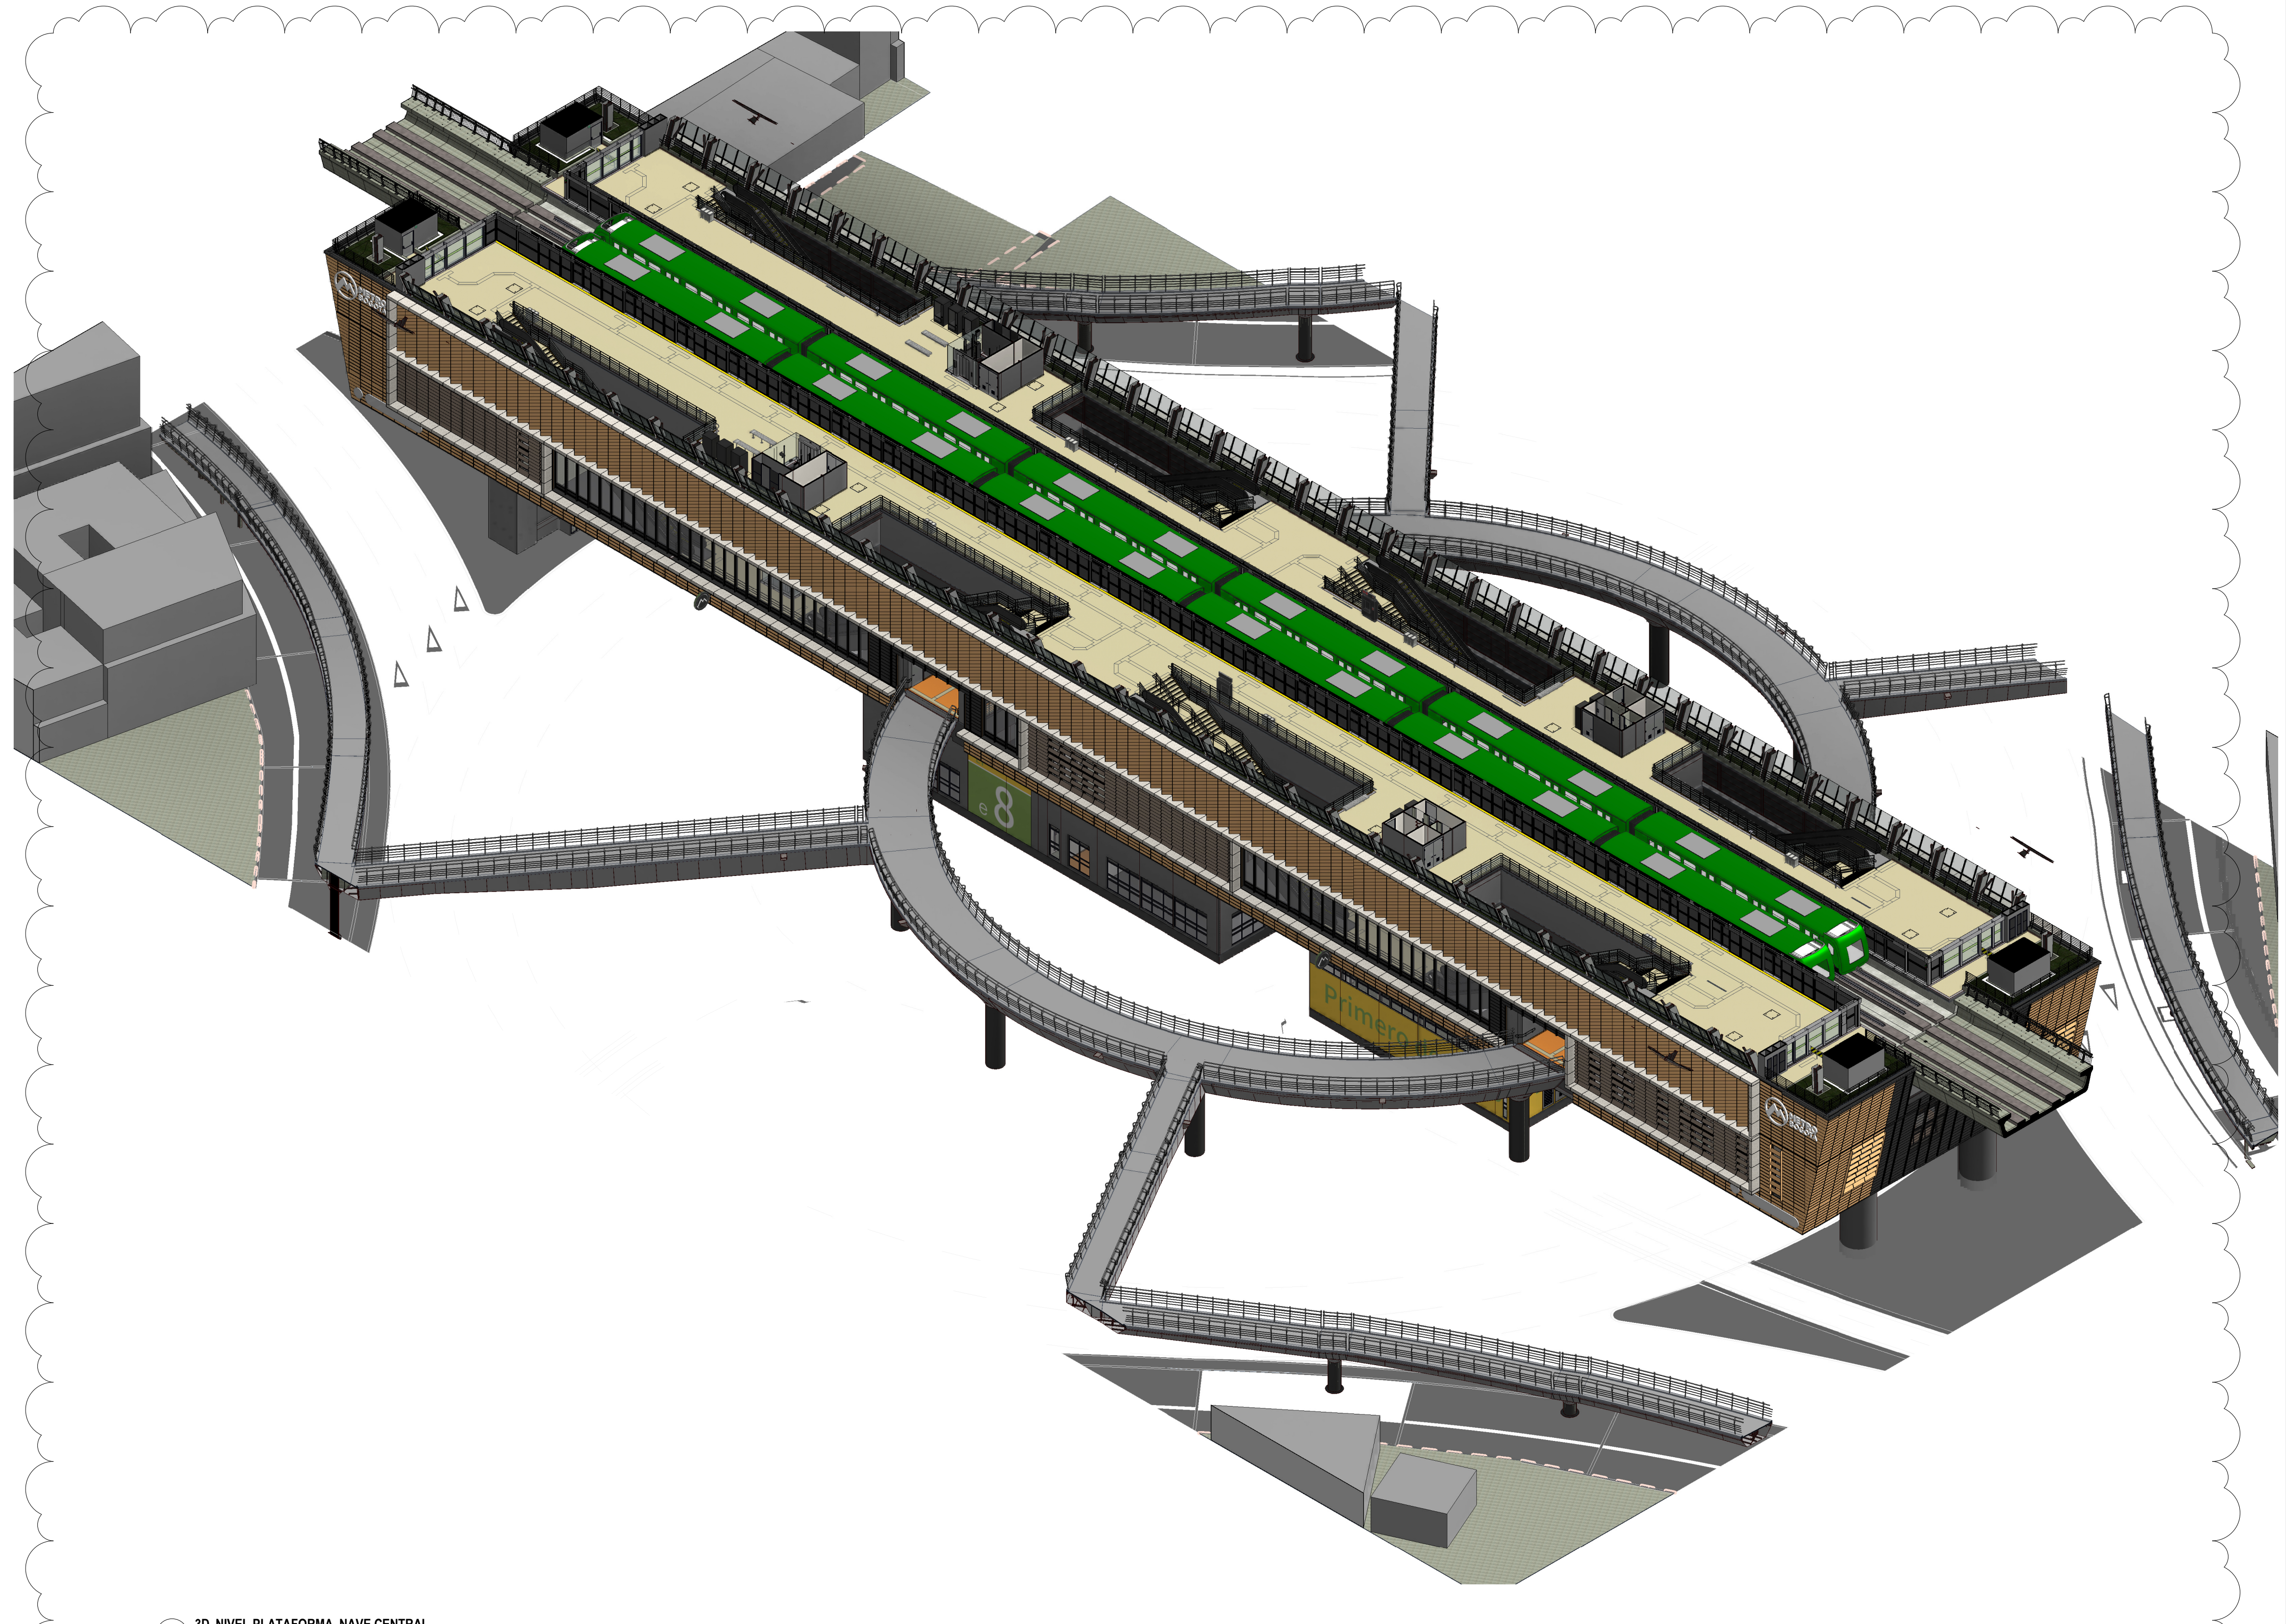

V01

1 3D_NIVEL PLATAFORMA_NAVE CENTRAL
ESC: N/A

TABLA DE ÁREAS ÚTILES (NIVEL PLATAFORMA_NAVE CENTRAL)			
CÓDIGO	**NOMBRE**	**ÁREA (m²)**	**DEPARTAMENTO**
NAVE CENTRAL			
ARQ_PL_03_PLATAFORMA			
J-01	JARDÍN	17.97	ÁREA JARDIN
J-01	JARDÍN	17.97	ÁREA JARDIN
J-01	JARDÍN	17.97	ÁREA JARDIN
J-01	JARDÍN	17.97	ÁREA JARDIN
PA	ÁREA PAGA	914.36	ÁREA PAGA
PA	ÁREA PAGA	921.22	ÁREA PAGA
R-301	SERVICIOS ADICIONALES - MÁQUINAS EXPENDEDORAS/CAJEROS AUTOMÁTICOS	4.59	SERVICIOS ADICIONALES - ÁREA PAGA
R-302	SERVICIOS ADICIONALES - MÁQUINAS EXPENDEDORAS/CAJEROS AUTOMÁTICOS	4.59	SERVICIOS ADICIONALES - ÁREA PAGA
R-303	SERVICIOS ADICIONALES - MÁQUINAS EXPENDEDORAS/CAJEROS AUTOMÁTICOS	3.17	SERVICIOS ADICIONALES - ÁREA NO PAGA
R-304	SERVICIOS ADICIONALES - MÁQUINAS EXPENDEDORAS/CAJEROS AUTOMÁTICOS	3.17	SERVICIOS ADICIONALES - ÁREA PAGA
T-21	ÁREA DE INSPECCIÓN	5.21	ÁREA TÉCNICA
T-21	ÁREA DE INSPECCIÓN	5.21	ÁREA TÉCNICA
T-21	ÁREA DE INSPECCIÓN	4.32	ÁREA TÉCNICA
T-21	ÁREA DE INSPECCIÓN	4.32	ÁREA TÉCNICA
T-25	NODO DE ACCESO DE TELECOMUNICACIONES	8.84	ÁREA TÉCNICA
T-25	NODO DE ACCESO DE TELECOMUNICACIONES	8.85	ÁREA TÉCNICA
T-25	NODO DE ACCESO DE TELECOMUNICACIONES	3.52	ÁREA TÉCNICA
T-25	NODO DE ACCESO DE TELECOMUNICACIONES	3.52	ÁREA TÉCNICA
ZDR	ZONA DE REFUGIO (PMR)	4.86	ZONA DE REFUGIO
ZDR	ZONA DE REFUGIO (PMR)	4.81	ZONA DE REFUGIO
ZDR	ZONA DE REFUGIO (PMR)	4.81	ZONA DE REFUGIO
ZDR	ZONA DE REFUGIO (PMR)	4.81	ZONA DE REFUGIO
TOTAL NIVEL PLATAFORMA		1986.06	

TABLA DE ÁREAS ÚTILES POR DEPARTAMENTO (NIVELPLATAFORMA)	
DEPARTAMENTO	**ÁREA (m²)**
SERVICIOS ADICIONALES - ÁREA NO PAGA	3.17
SERVICIOS ADICIONALES - ÁREA PAGA	12.34
ZONA DE REFUGIO	19.28
ÁREA JARDIN	71.90
ÁREA PAGA	1835.58
ÁREA TÉCNICA	43.80
TOTAL NIVEL PLATAFORMA	1986.06

LOCALIZACIÓN

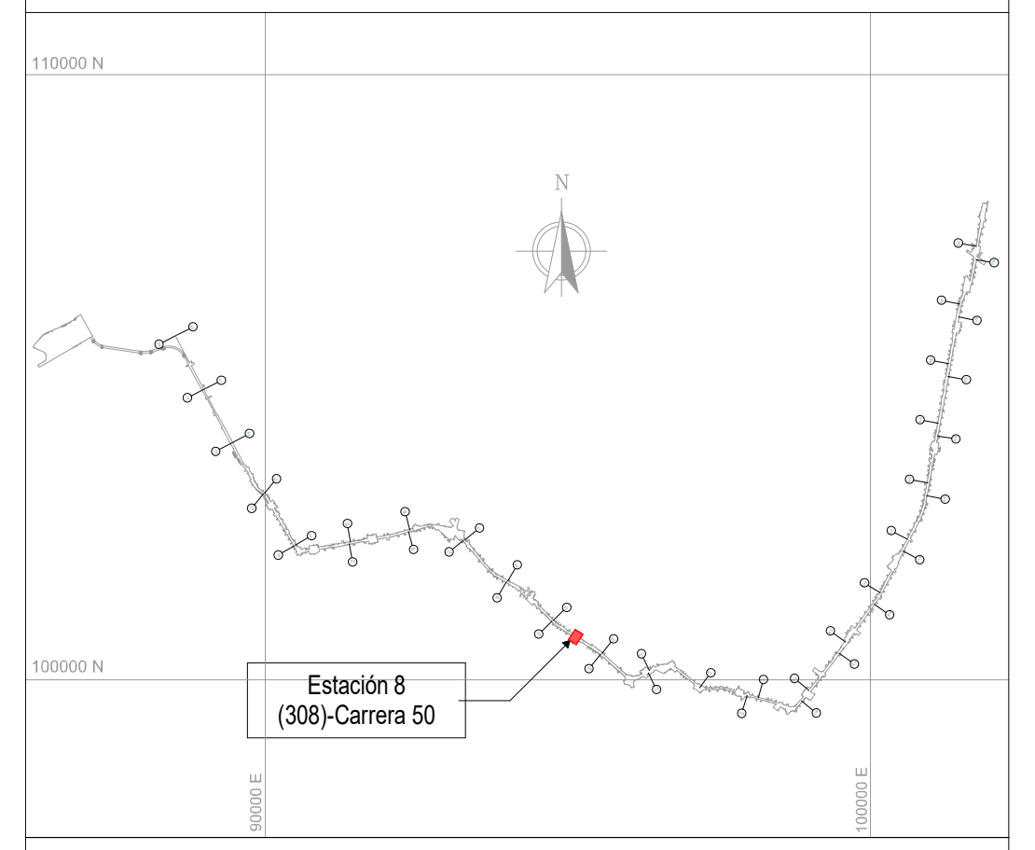

NOTAS

01 TODAS LAS DIMENSIONES ESTÁN CONFIGURADAS EN METROS A MENOS QUE SE INDIQUE UNA UNIDAD DE MEDIDA DIFERENTE.

02 TODAS LAS MEDIDAS, UBICACIÓN Y NIVELES DEBEN VERIFICARSE EN EL LUGAR DE CONSTRUCCIÓN.

03 EL NIVEL DE ACCESO AL EDIFICIO PL 01 CORRESPONDE AL +0,00 DE LA ESTACIÓN Y REFERENCIA AL NIVEL 2555.65 M.S.N.M

04 LOS NOMBRES ESPECÍFICOS DE LAS ÁREAS PUEDEN SER CONSULTADAS EN EL PLANO NO. 3 Ó EN LAS VISTAS EN PLANTA.

05 LOS COLORES QUE SE MUESTRAN EN LOS PLANOS COMO PROYECCIÓN DE ELEMENTOS ARQUITECTÓNICOS COMO CUBIERTAS FACHADAS MUROS ETC. NO REPRESENTAN LA MATERIALIDAD Y REALIDAD DE ACABADOS DEL PROYECTO, SOLO SON INDICATIVOS PARA REALIZAR UNA CORRECTA LECTURA DE LA PLANIMETRÍA.

06 LAS ESCALERAS ELÉCTRICAS INDICAN SU SENTIDO CON LA SIGUIENTE NOMENCLATURA: “SUBE” Y “BAJA”.

07 REVISAR LOS NIVELES ESTRUCTURALES PARA NIVEL DE ACCESO PL_01 Y SUBNIVELES, PL_02 (INTERMEDIO), PL_03 (PLATAFORMA) CON LA PLANIMETRÍA DE PLACAS ESTRUCTURALES EN LOS ENTREGABLES L1T1-1200-308-CON-ED-EST-PL-0068, 69, RESPECTIVAMENTE. EL NIVEL ESTRUCTURAL (NE) REFERENCIA LOS ESPACIOS DONDE SE DEBE ACONDICIONAR EL ACABADO DE PISO SEGÚN CORRESPONDA, CON LOS NIVELES DE PISO TERMINADO (NPT). LOS NIVELES PROYECTADOS DE EMPATE (NPE) EN LAS ÁREAS DE SERVICIOS ADICIONALES, REFERENCIAN LA ADECUACIÓN DE LOS DESNIVELES EN ESTAS ÁREAS; QUEDA COMO RESPONSABILIDAD DEL LOCATARIO DEFINIR Y ACONDICIONAR ESTE ACABADO DE PISO (NPE) EN LÍNEA CON EL NIVEL (NPT) DE ESPACIOS COLINDANTES

- ARC_PL_00 = SÓTANO	/ NPT -6.25
- ARC_PL_01 = ACCESO	/ NPT 0.00
- ARC_PL_02 = INTERMEDIO	/ NPT 7.60
- ARC_PL_02.1 = PLACA INFERIOR VIGA CAJÓN	/ NPT 13.82
- ARC_PL_02.2 = TOPE DE RIEL (TOR)	/ NPT 15.95
- ARC_PL_03 = PLATAFORMA	/ NPT 17.09
- ARC_PL_05 = CUBIERTA NAVE CENTRAL	/ NPT 26.42

CONVENCIONES

▨	SERVICIOS ADICIONALES - ÁREA NO PAGA	▨	ÁREA NO PAGA
🟩	SERVICIOS ADICIONALES - ÁREA PAGA	🟦	ÁREA OPERATIVA
🟩	SERVICIO PÚBLICO	🟨	ÁREA PAGA
🟦	ZONA DE REFUGIO	🟦	ÁREA PÚBLICA
🟥	ÁREA CULTURAL	▨	ÁREA TÉCNICA
🟪	ÁREA DE TAQUILLAS BRT		

V01 CAMBIOS EFECTUADOS:
1.ACTUALIZACIÓN DEL PROYECTO DE FACHADA

No.	PLANOS DE REFERENCIA	REV.

No.	MODELO BIM DE REFERENCIA	REV.
1	L1T1-1100-208-CON-ED-EST-MO-0001.rvt	V00
2	L1T1-1100-209-CON-ED-EST-MO-0001.rvt	V00
3	L1T1-1100-308-CON-ED-EST-MO-0001.rvt	V00
4	L1T1-1150-208-CON-ED-EST-MO-0001.rvt	V00
5	L1T1-1150-209-CON-ED-EST-MO-0001.rvt	V00
6	L1T1-1150-308-CON-ED-EST-MO-0001.rvt	V00
7	L1T1-1200-308-CON-ED-EST-MO-0001.rvt	V00
8	L1T1-1410-308-CON-ED-MEC-MO-0001.rvt	V00
9	L1T1-1420-308-CON-ED-MEC-MO-0001.rvt	V00
10	L1T1-2420-561-CON-ED-MEC-MO-0001.rvt	V00
11	L1T1-5160-308-CON-ED-EST-MO-0001.rvt	V00
12	L1T1-5160-308-CON-ED-ARQ-MO-0001.rvt	V00
13	L1T1-5300-308-CON-ED-MEC-MO-0001.rvt	V00
14	L1T1-1270-308-CON-ED-ARQ-MO-0011.rvt	V00

No.	PAQUETE DE TRABAJO DE REFERENCIA	REV.
1	XREF-URBANISM_CONTEXT_ST08.rvt	
2	XREF-SECONDARY-STRUCTURE-ST08.rvt	

0 2 10m
1:200

PLANO CLAVE ESTACIÓN 08

VÁLIDO PARA CONSTRUCCIÓN
31-03-26

METRO BOGOTÁ
Consorcio Consultores PMO Bogotá
CONSORCIO SUPERVISOR PLMB
HEC

DISEÑÓ:
REN ZHENHUA
Licencia de Arq.nivel I (China): 1101735-614

REVISÓ:
CARLOS MAURICIO BARRETO BARBOSA
Mat.: A4012012-14139353

APROBÓ:
DIEGO ERNESTO DUEÑAS
Mat.: 25202-53876 CND

DIBUJÓ:
EQUIPO CHEC

REVISIÓN No.	FECHA	DESCRIPCIÓN	REVISÓ	APROBÓ	APROBACIÓN CLIENTE
V01	31/03/2026	EMITIDO PARA CONSTRUCCIÓN	C.M.B.B	D.E.D	
V00	12/12/2025	REVISIÓN NO OBJETADA - EMITIDO PARA CONSTRUCCIÓN	F.B.R	M.M.R	
VCC	01/10/2025	EMITIDO PARA REVISIÓN Y COMENTARIOS DEL CLIENTE E INTERVENTORÍA - INCLUYE COMENTARIOS /(AJUSTE)	F.B.R	M.M.R	
VBB	15/07/2025	EMITIDO PARA REVISIÓN Y COMENTARIOS DEL CLIENTE E INTERVENTORÍA	F.B.R	M.M.R	
VA0	04/07/2025	EMITIDO PARA COMENTARIOS INTERNOS - EMISIÓN PRELIMINAR PARA COMENTARIOS	F.B.R	M.M.R	

METRO LÍNEA 1

DIRECTOR DE INTERVENTORÍA:
JAVIER DESCARGA N.
Mat.:25202-68697 CND

METRO LÍNEA 1
CONTRATO DE CONCESIÓN No. 163 DE 2019

PROYECTO PRIMERA LÍNEA DEL METRO DE BOGOTÁ - TRAMO 1

ESPECIALISTA INTERVENTORÍA:
CARLOS ALBERTO HOYOS SOTO
Mat.:A25072000-14251682

FECHA:
MARZO 2026

INFRAESTRUCTURA VIAL

ARQUITECTURA

ESTACIÓN METRO 8 (CARRERA 50)
NAVE CENTRAL
VISTA EN PLANTA Y 3D - NIVEL PLATAFORMA

PLANCHA No: L1T1-0000-308-CON-ED-ARQ-PL-0022_07_V01
ARCHIVO: L1T1-0000-308-CON-ED-ARQ-MO-0002_V00.rvt
ESCALA: INDICADA
FECHA: JULIO 2025
REVISIÓN No. V01
PLANO No. 07 DE 45